


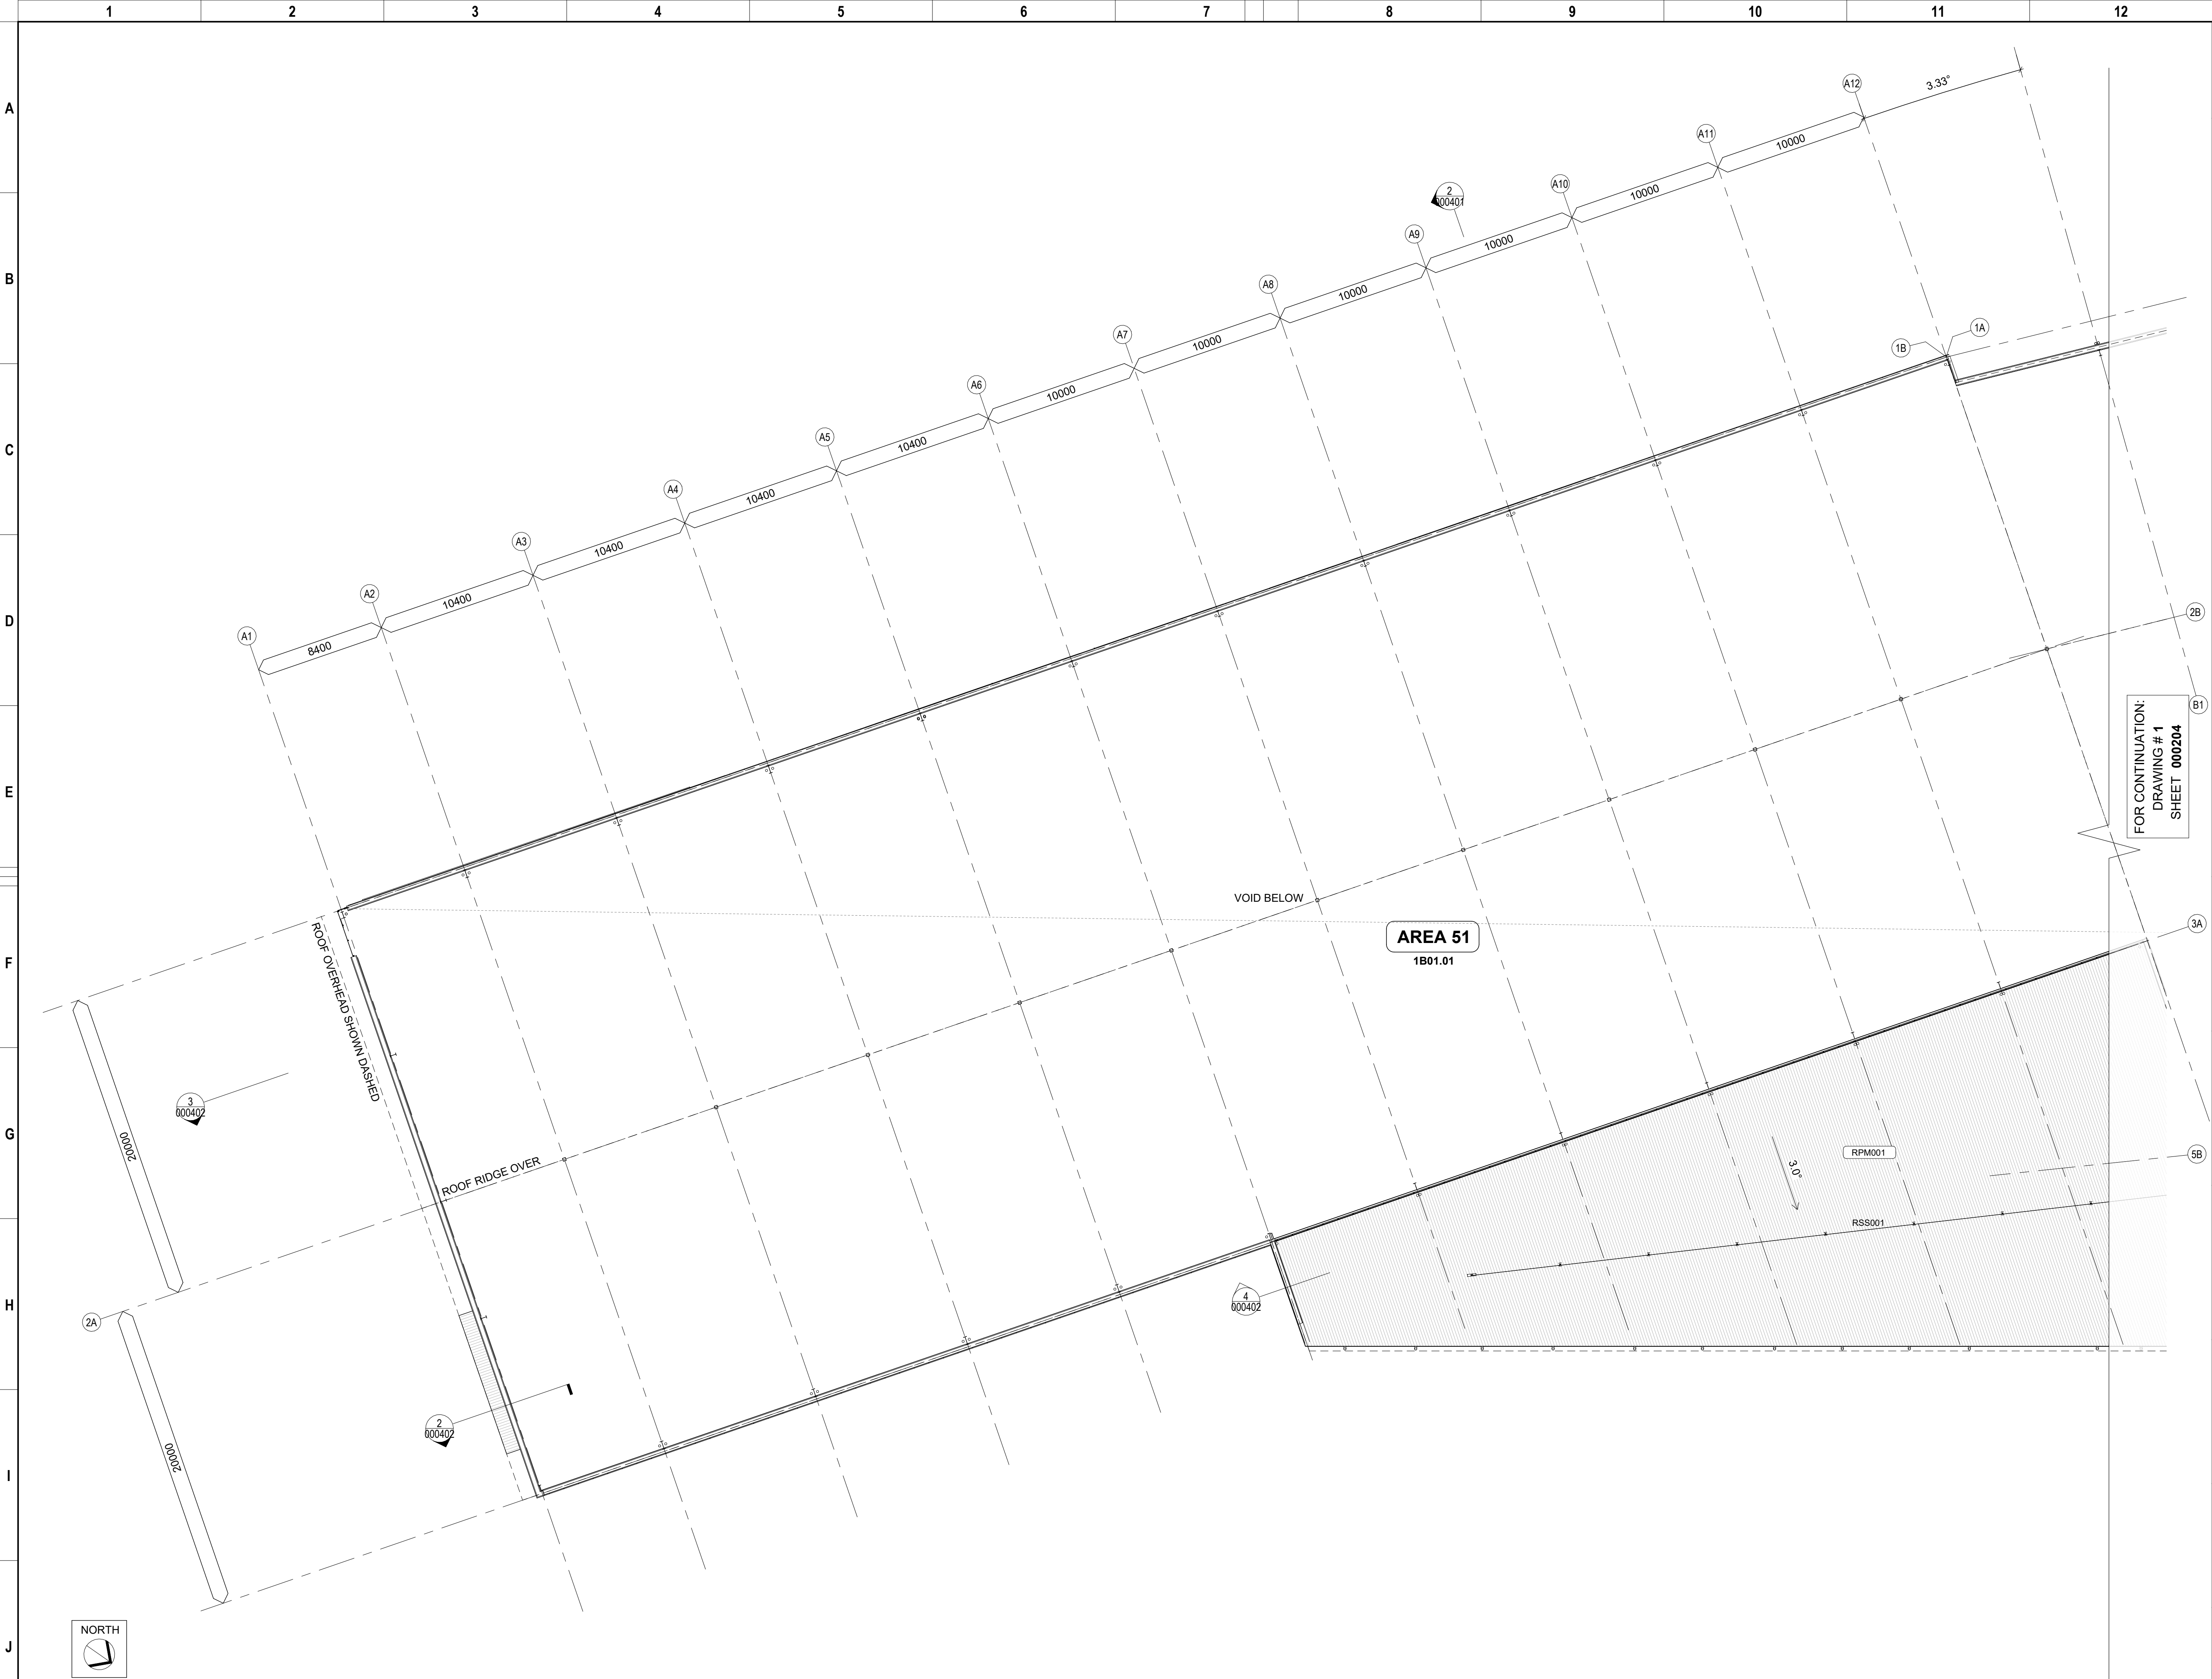

COPYRIGHT: REPRODUCTION OF WHOLE OR PART OF THIS DOCUMENT CONSTITUTES AN INFRINGEMENT OF COPYRIGHT. THE INFORMATION, IDEAS AND CONCEPTS CONTAINED IN THIS DOCUMENT ARE CONFIDENTIAL. THE RECIPIENT(S) OF THIS DOCUMENT IS PROHIBITED FROM DISCLOSING SUCH INFORMATION IDEAS AND CONCEPTS TO ANY PERSON WITHOUT THE PRIOR WRITTEN CONSENT OF THE BRISBANE AIRPORT CORPORATION PTY. LTD.

DRN	AMENDMENTS	DATE	REV
JB	FOR COORDINATION	04.12.2025	1
DC	FOR COORDINATION	21.01.2026	2
JB	60% DD ISSUE 2	05.02.2026	3
JB	FOR COORDINATION	12.06.2026	A

TAG LEGEND	
CLD002	PREFINISHED FC SHEET CLADDING - REFER TO SECTION J REPORT
CLD003	METAL SHEET CLADDING - REFER TO SECTION J REPORT
CLD004	KILP LOK PROFILED METAL SHEET CLADDING - REFER TO SECTION J REPORT
CLD005	DANPALON SINGLE GLAZED TRANSLUCENT CLADDING
COL	STRUCTURAL COLUMN - REFER STRUCTURAL ENGINEER
CT1	CURTAIN TRACK
DP	DOWNPIPE
GT01	COLORBAND FOLDED STEEL GUTTER
MLV001	MECHANICAL EXHAUST LOUVRE
RPM001	KILP LOK PROFILED METAL SHEET ROOFING - REFER TO SECTION J REPORT
RSS001	ROOF SAFETY SYSTEM
STR001	STRUCTURAL COLUMN - REFER STRUCTURAL ENGINEER

Archipelago

Archipelago
Level 3, 189 George Street, Brisbane QLD 4000
T +617 3236 4806 www.archipelago.com.au
© ARCHIPELAGO ARCHITECTS PTY. LTD. All Rights Reserved
This work is copyright and cannot be reproduced or copied by any means without written permission of Archipelago Architects Pty Ltd. Any license, express or implied, to use this document for any purpose whatsoever is restricted to the terms of the agreement between Archipelago Architects Pty Ltd and the instructing party.

SKYGATE PLAY	
GENERAL ARRANGEMENT - PART A - HIGH LEVEL	
Drawn JB	Checked DC
Design Coordinated	Compliance Checked
Authorised For Issue	Construction Checked

	Brisbane Airport Corporation Pty Ltd 11 The Circuit Brisbane Airport QLD 4008 PO Box 61 Hamilton QLD 4007 Australia		Scale 1 : 200
	Telephone : 61 7 3406 3000 Facsimile : 61 7 3406 3111 Email : info@bne.com.au www.brisbaneairport.com.au		Size A1
	ABN 54 076 870 650		Revision A
	Project No.	Originator	Volume

Drawing No.	25021	- ARC - XX - 01 - DR - AR - 000203
-------------	-------	------------------------------------