




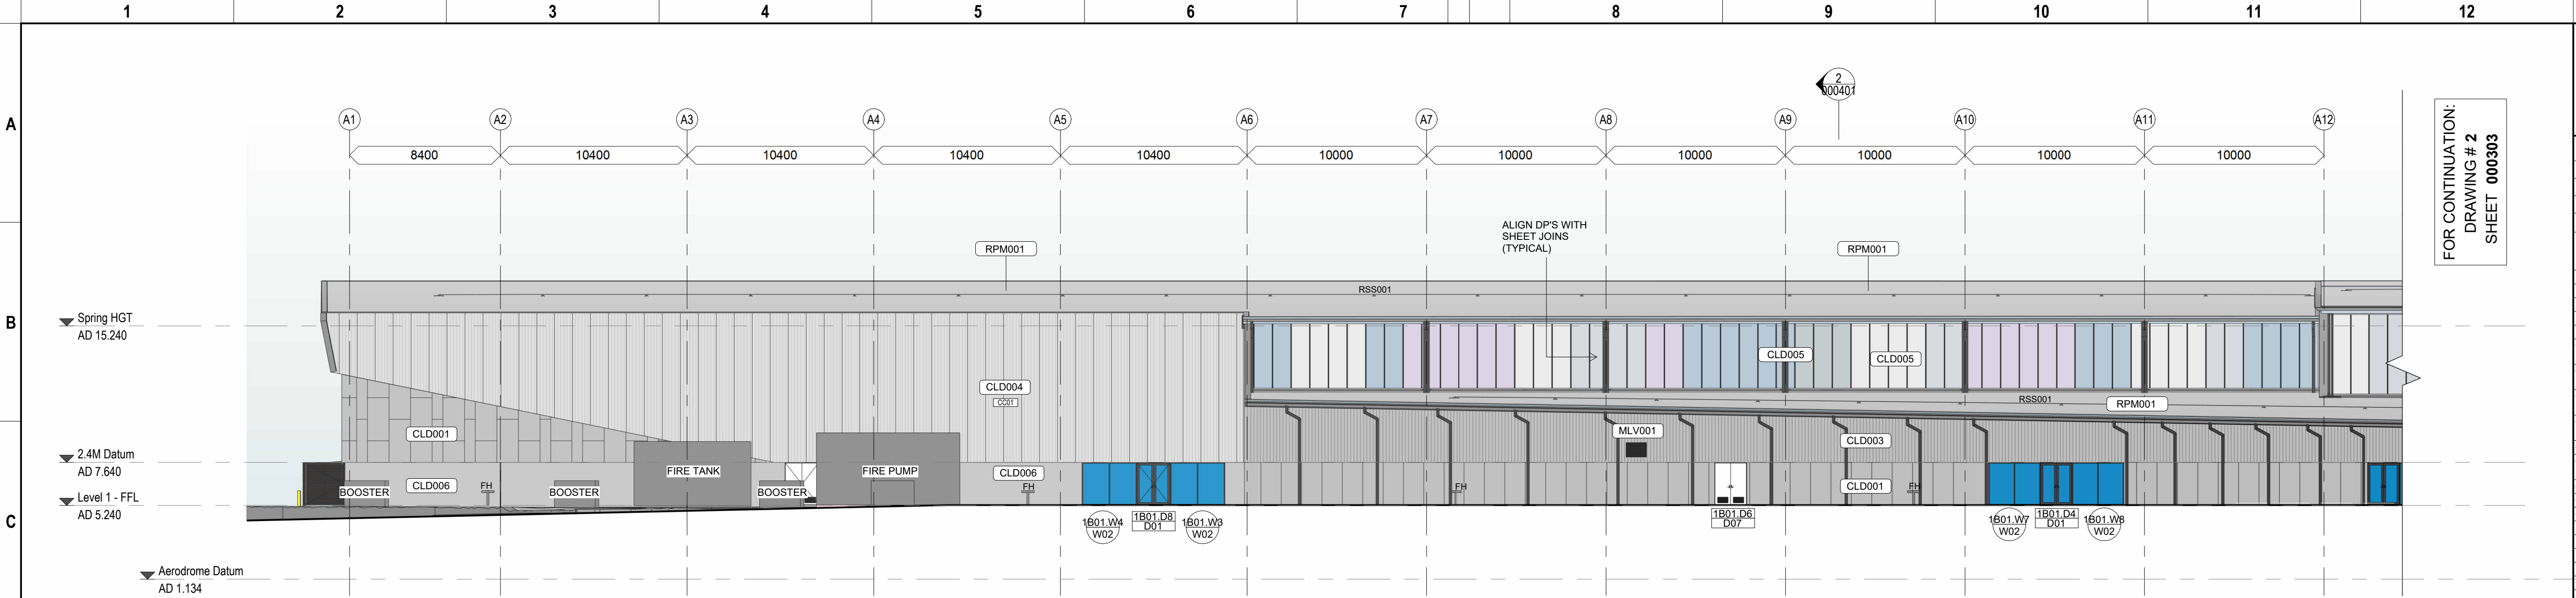

1 SOUTH EAST - PART A
1 : 200

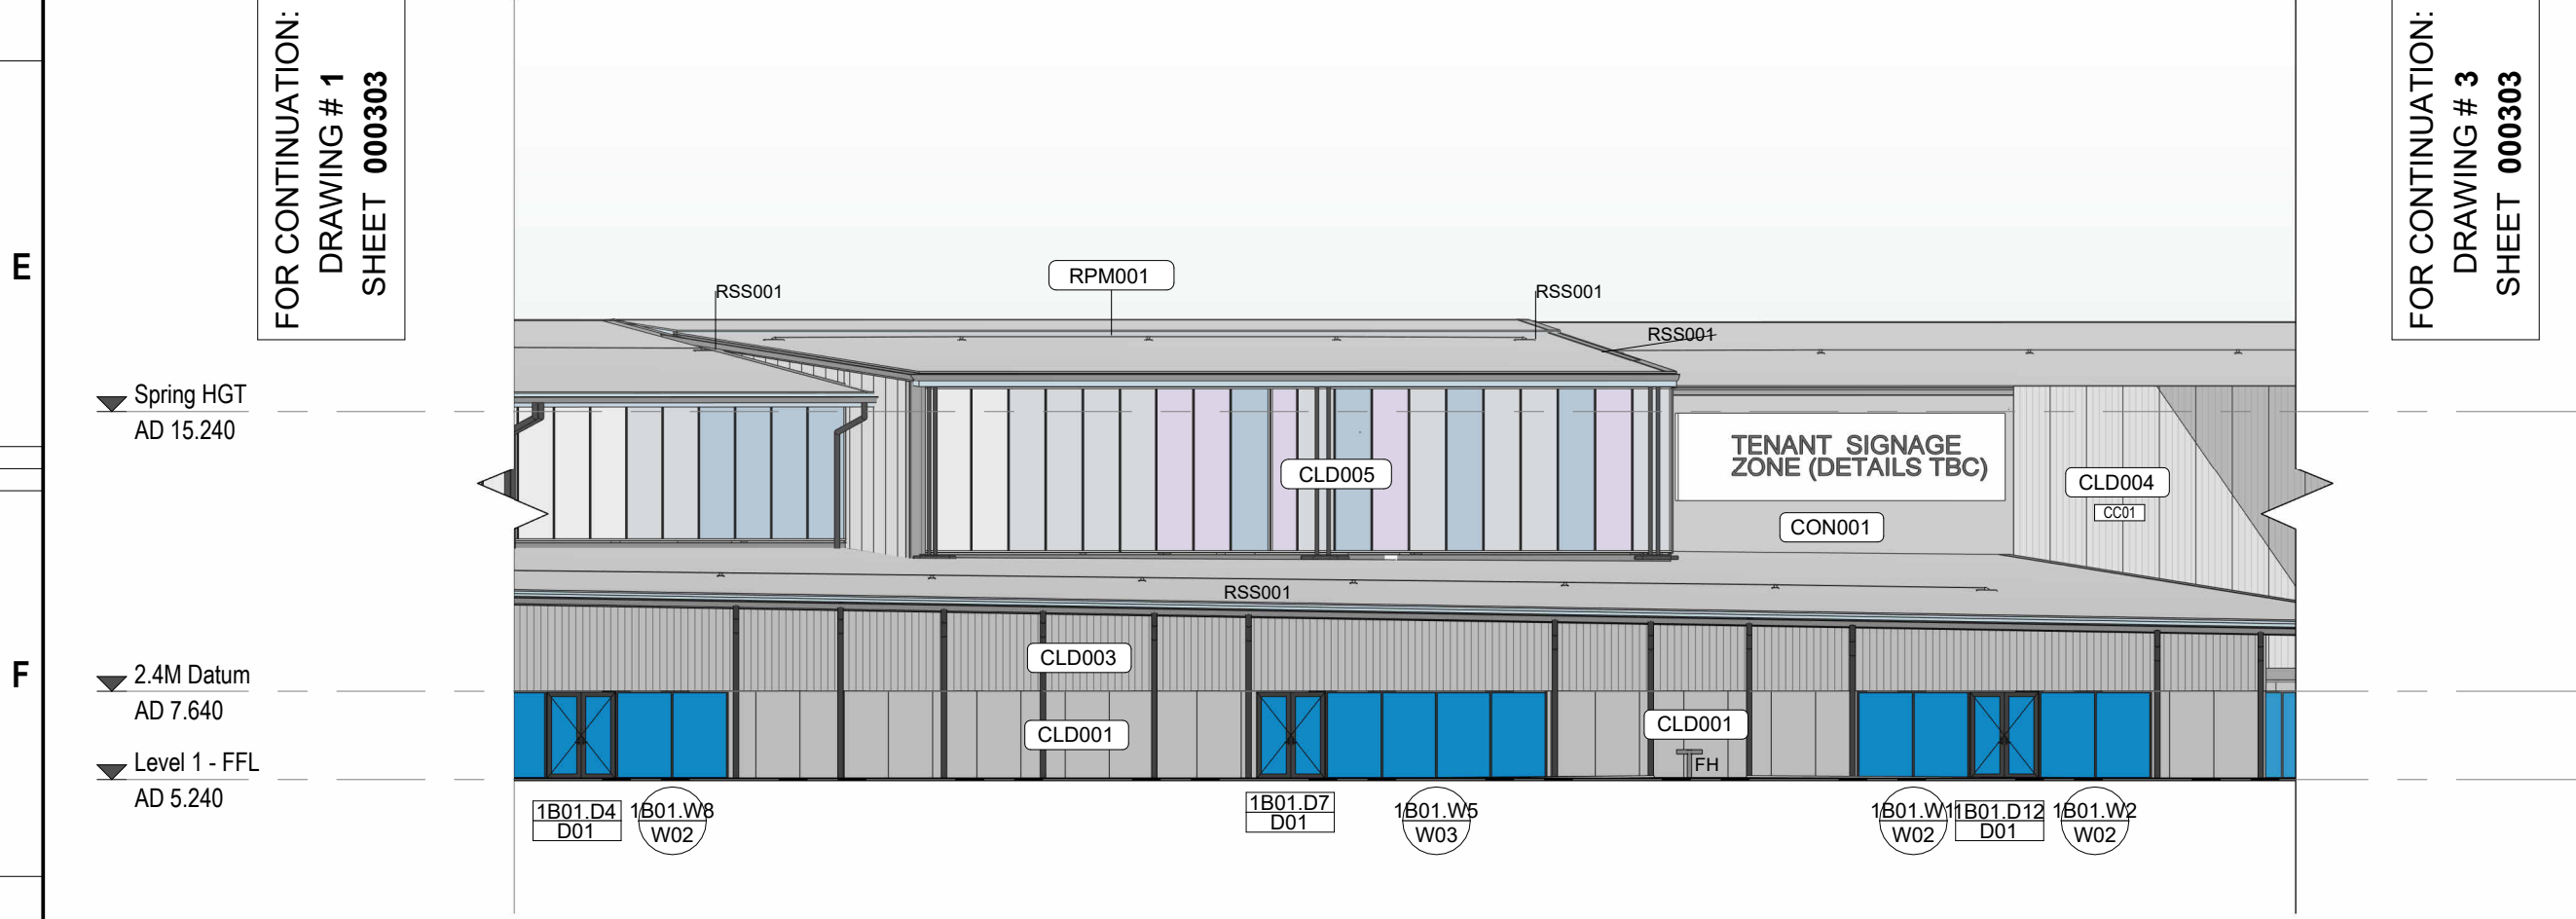

2 SOUTH EAST - PART B
1 : 200

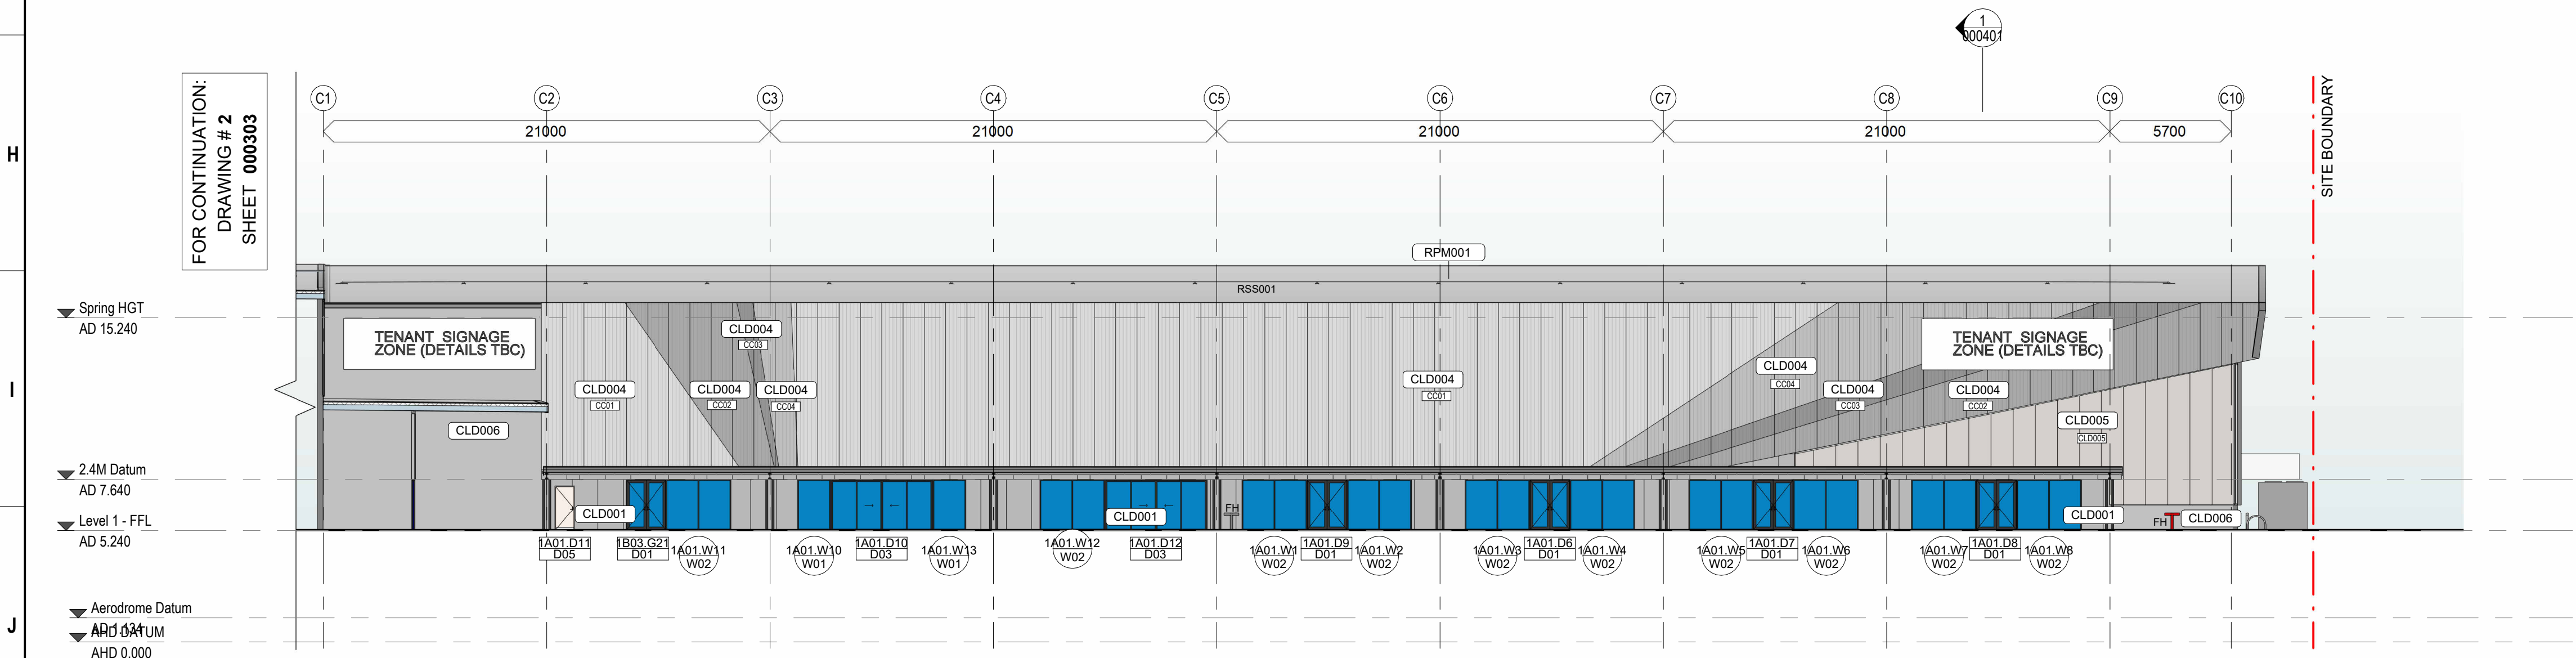

3 SOUTH EAST - PART C
1 : 200

COPYRIGHT : REPRODUCTION OF WHOLE OR PART OF THIS DOCUMENT CONSTITUTES AN INFRINGEMENT OF COPYRIGHT. THE INFORMATION, IDEAS AND CONCEPTS CONTAINED IN THIS DOCUMENT ARE CONFIDENTIAL. THE RECIPIENT(S) OF THIS DOCUMENT IS PROHIBITED FROM DISCLOSING SUCH INFORMATION IDEAS AND CONCEPTS TO ANY PERSON WITHOUT THE PRIOR WRITTEN CONSENT OF THE BRISBANE AIRPORT CORPORATION PTY. LTD.			
DRN	AMENDMENTS	DATE	REV
JB	FOR COORDINATION	15.05.2026	A
JB	FOR COORDINATION	05.06.2026	B
JB	FOR COORDINATION	12.06.2026	C

TAG LEGEND	
BCT1	Baby Change Tables
BIN1	WASTE BIN - RECESSED
BIN2	NAPPY BIN - IN CUPBOARD
BOL001	BOLLARD - FIXED
BOL002	BOLLARD - REMOVABLE
CLD002	PREFINISHED FC SHEET CLADDING - REFER TO SECTION J REPORT
CLD003	METAL SHEET CLADDING - REFER TO SECTION J REPORT
CLD004	KILP LOK PROFILED METAL SHEET CLADDING - REFER TO SECTION J REPORT
CLD005	DANPALON SINGLE GLAZED TRANSLUCENT CLADDING
CLD006	PRECAST CONCRETE
COL	STRUCTURAL COLUMN - REFER STRUCTURAL ENGINEER
CON001	CONCRETE SLAB
CON002	CONCRETE SLAB - EXTERNAL HARDSTAND
CT1	CURTAIN TRACK
DP	DOWNPIPE
FH	DOUBLE PILLAR FIRE HYDRANT REFER HYD. ENG.
FHR	FIRE HOSE REEL REFER HYD. ENG.
FLW003	FLOOR DRAIN
GPO1	GPO SINGLE
GPOC	GPO SINGLE - CLEANERS
GT01	COLORBOND FOLDED STEEL GUTTER
GT02	<varies>
M-FTL1	WET AREA TILES - FLOOR
M-FTL2	WET AREA TILES - FLOOR
M-STL1	WET AREA TILES - SKIRTING
M-TL2	WET AREA - WALL TILE
M-VNL1	SHEET VINYL - FLOOR
MCT1	PRIVACY CURTAIN
MEC001	MECHANICAL DUCT - REFER MECHANICAL ENGINEER
MLV001	MECHANICAL EXHAUST LOUVRE
MR2	MIRROR 2
MR3	MIRROR 3
RPM001	KILP LOK PROFILED METAL SHEET ROOFING - REFER TO SECTION J REPORT
RPM002	RIDGE CAPPING
RSS001	ROOF SAFETY SYSTEM
SCR001	ALUMINIUM LOUVRE SCREEN TYPE 1
SD3	SOAP DISPENSER
SNK2	SINK - CLEANERS
STR001	STRUCTURAL COLUMN - REFER STRUCTURAL ENGINEER
T1	WC STANDARD
T2	WC - AMBULANT
T4	WC - UNIVERSAL
THR1	TOILET ROLL HOLDER
TMV	THERMOSTATIC MIXING VALVE
TP1	TAP - WALL MOUNTED SENSOR
TRH2	TOILET ROLL HOLDER
URY1	URNAL - WALL HUNG
URY2	URNAL - THROUGH

MATERIAL TAG LEGEND		
MATERIAL	COLOUR CODE	DESCRIPTION
CLD004	CC01	Cladding Colour 1
CLD004	CC02	Cladding Colour 2
CLD004	CC03	Cladding Colour 3
CLD004	CC04	Cladding Colour 4

Archipelago

Archipelago
Level 3, 189 George Street, Brisbane QLD 4000
T +61 7 3236 4805 www.archipelago.com.au
© ARCHIPELAGO ARCHITECTS PTY. LTD. All Rights Reserved
This work is copyright and cannot be reproduced or copied by any means without written
permission of Archipelago Architects Pty Ltd. Any
license, express or implied, to use this document for any purpose
whatsoever is restricted to the terms of the agreement between Archipelago Architects P
ty Ltd and the instructing party.

SKYGATE PLAY

ELEVATIONS 03

Drawn JB	Checked DC
Design Coordinated	Compliance Checked
Authorised For Issue DC	Construction Checked

Brisbane Airport		Scale 1 : 200	
Project No. 25021 - ARC - XX - XX - DR - AR - 000303		Size A1	
Revision C		Number	