


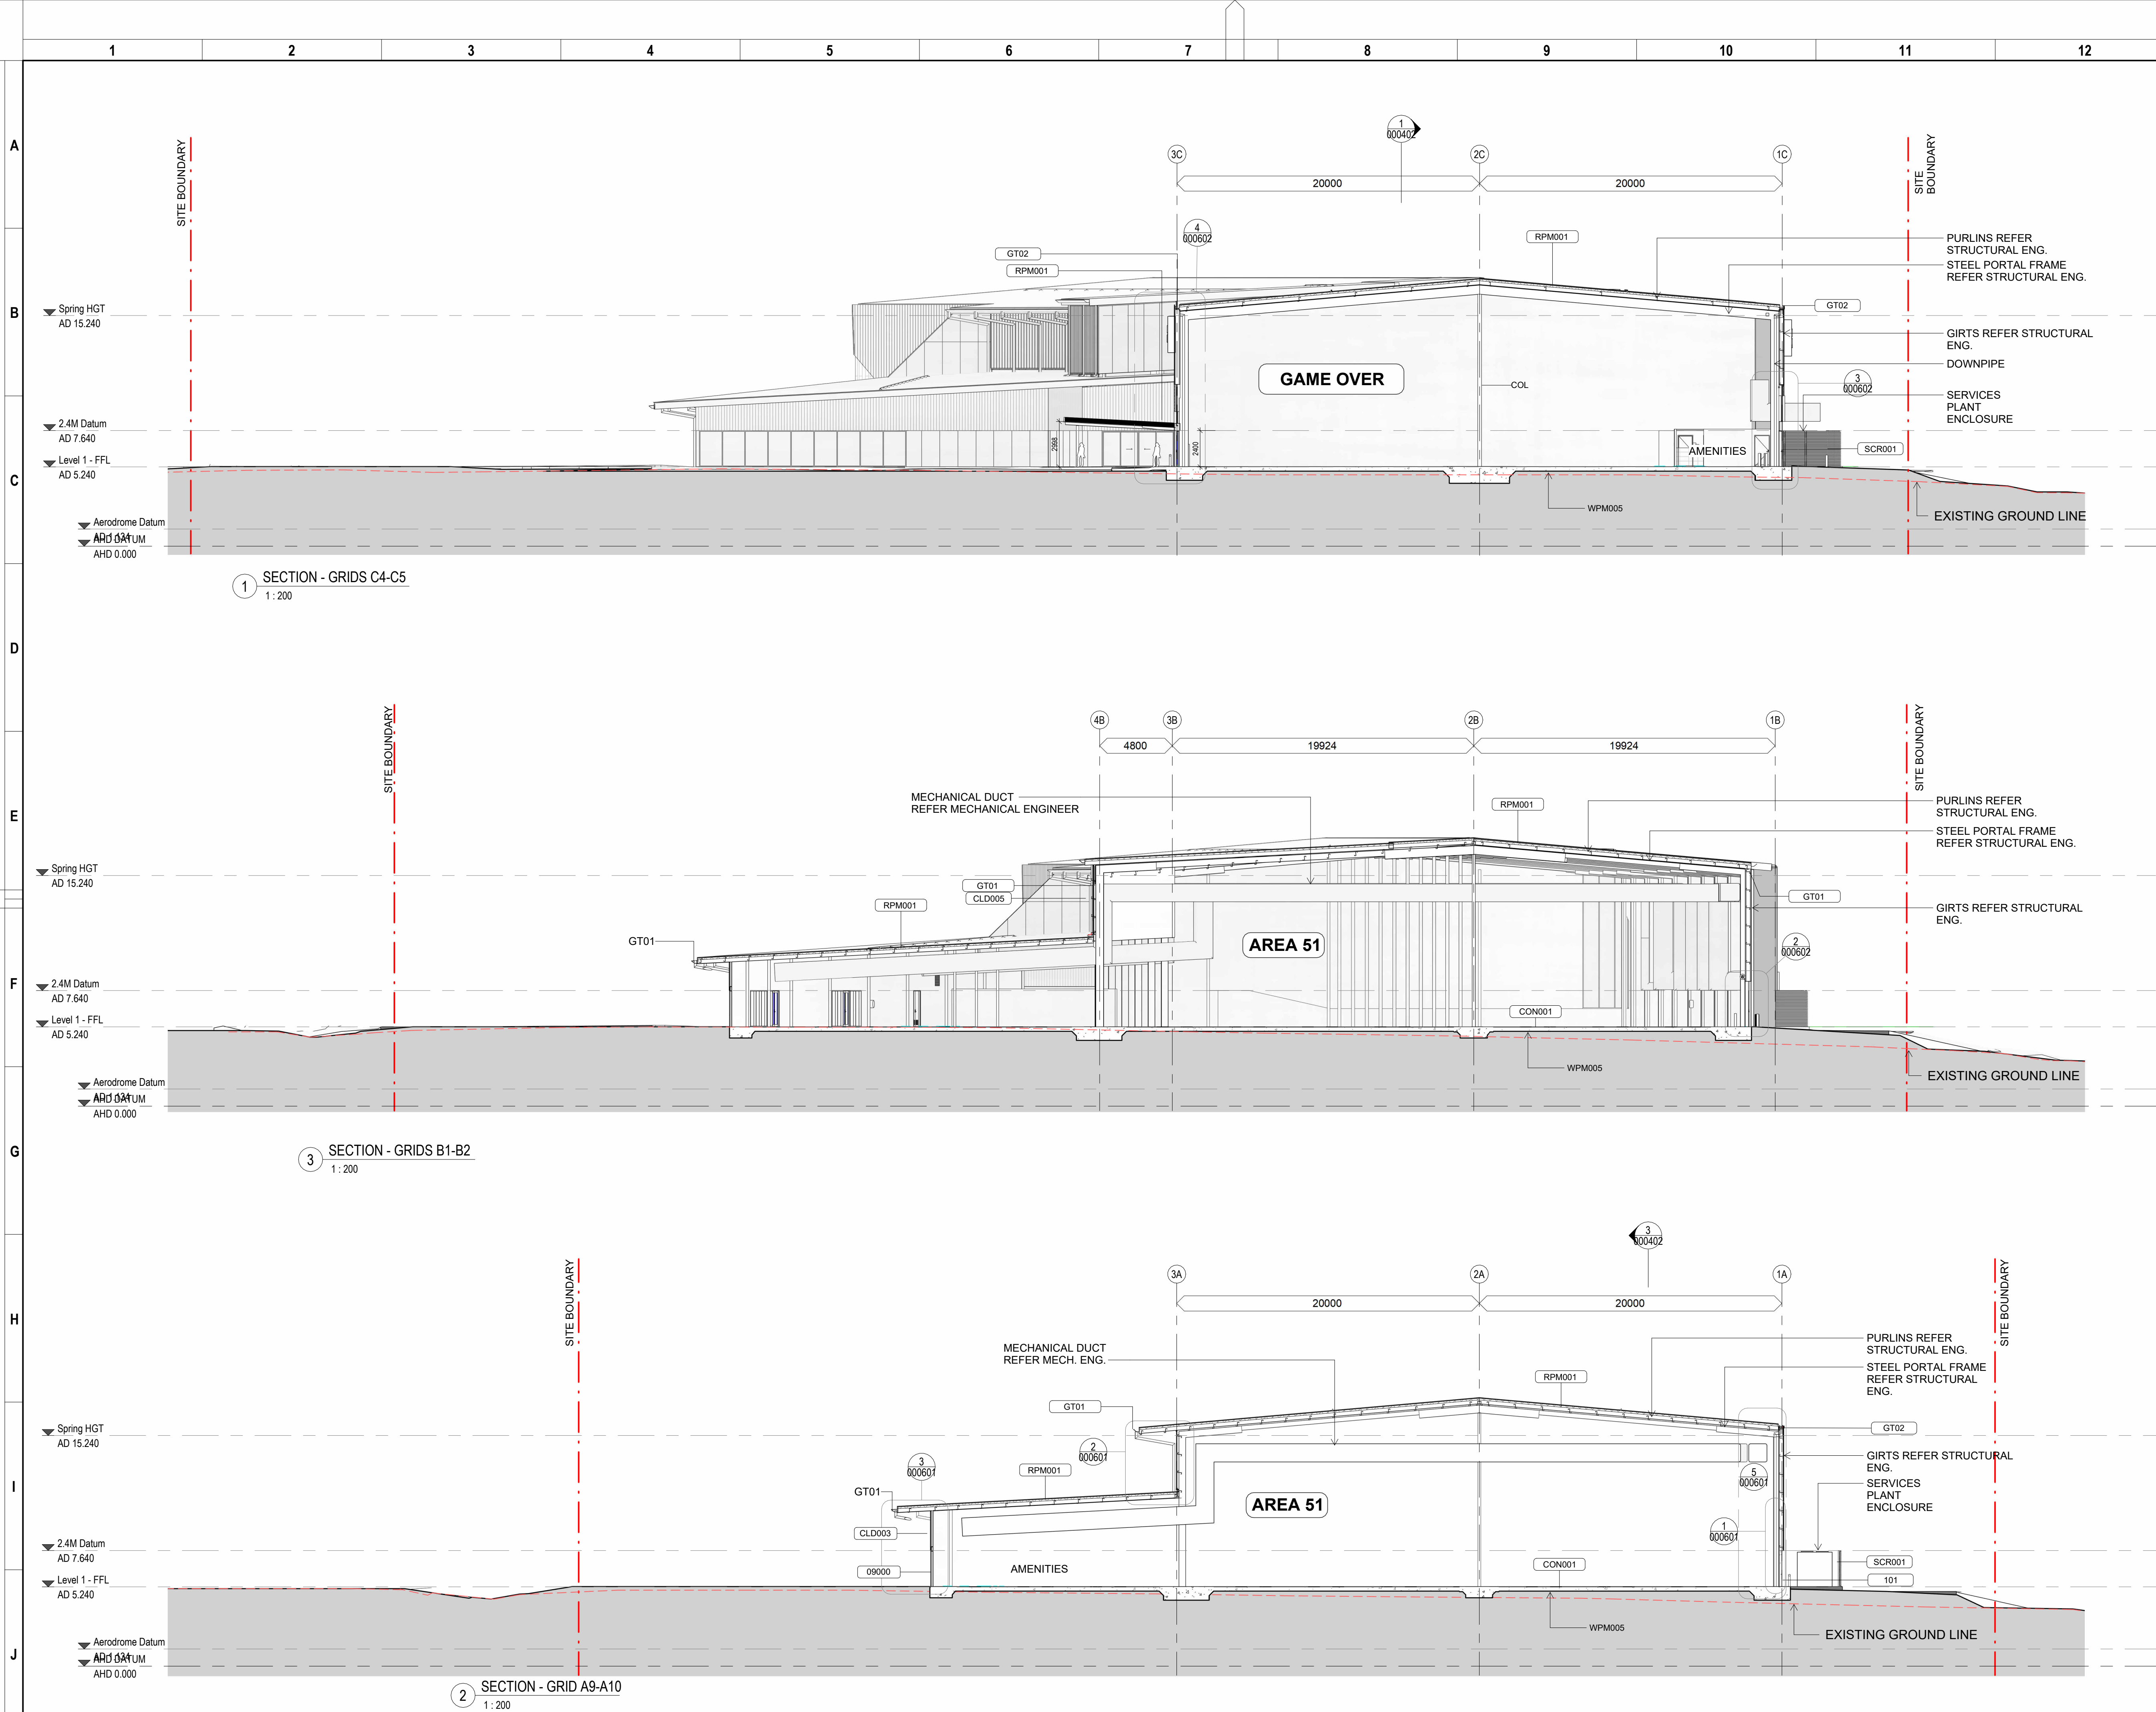

COPYRIGHT :
REPRODUCTION OF WHOLE OR PART OF THIS DOCUMENT
CONSTITUTES AN INFRINGEMENT OF COPYRIGHT. THE
INFORMATION, IDEAS AND CONCEPTS CONTAINED IN THIS
DOCUMENT ARE CONFIDENTIAL. THE RECIPIENT(S) OF THIS
DOCUMENT IS PROHIBITED FROM DISCLOSING SUCH
INFORMATION IDEAS AND CONCEPTS TO ANY PERSON
WITHOUT THE PRIOR WRITTEN CONSENT OF THE
BRISBANE AIRPORT CORPORATION PTY. LTD.

DRN	AMENDMENTS	DATE	REV
JB	FOR COORDINATION	15.05.2026	A
JB	FOR COORDINATION	05.06.2026	B
JB	FOR COORDINATION	12.06.2026	C

TAG LEGEND	
BC11	Baby Change Tables
BIN1	WASTE BIN - RECESSED
BIN2	NAPPY BIN - IN CUPBOARD
BOLO01	BOLLARD - FIXED
BOLO02	BOLLARD - REMOVABLE
CLD002	PREFINISHED PC SHEET CLADDING - REFER TO SECTION J REPORT
CLD003	METAL SHEET CLADDING - REFER TO SECTION J REPORT
CLD004	KILP LOK PROFILED METAL SHEET CLADDING - REFER TO SECTION J REPORT
CLD005	DANPALON SINGLE GLAZED TRANSLUCENT CLADDING
CLD006	PRECAST CONCRETE
COL	STRUCTURAL COLUMN - REFER STRUCTURAL ENGINEER
CON001	CONCRETE SLAB
CON002	CONCRETE SLAB - EXTERNAL HARDSTAND
CT1	CURTAIN TRACK
DP	DOWNPIPE
FH	DOUBLE PILLAR FIRE HYDRANT REFER HYD. ENG
FHR	FIRE HOSE REEL REFER HYD. ENG
FLW003	FLOOR DRAIN
GPO1	GPO SINGLE
GPO2	GPO SINGLE - CLEANERS
GT01	COLOROND FOLDEN STEEL GUTTER
GT02	<varies>
M-FTL1	WET AREA TILES - FLOOR
M-FTL2	WET AREA TILES - FLOOR
M-STL1	WET AREA TILES - SKIRTING
M-TL2	WET AREA - WALL TILE
M-VNL1	SHEET VINYL FLOOR
MCT1	PRIVACY CURTAIN
MEC001	MECHANICAL DUCT - REFER MECHANICAL ENGINEER
MLV001	MECHANICAL EXHAUST LOUVER
MR2	MIRROR 2
MR3	MIRROR 3
RP001	KILP LOK PROFILED METAL SHEET ROOFING - REFER TO SECTION J REPORT
RP002	RIDGE CAPPING
RS001	ROOF SAFETY SYSTEM
SCR001	ALUMINIUM LOUVER SCREEN TYPE 1
SD3	SOAP DISPENSER
SNK2	SINK - CLEANERS
STR001	STRUCTURAL COLUMN - REFER STRUCTURAL ENGINEER
T1	WC - STANDARD
T2	WC - AMBULANT
T4	WC - UNIVERSAL
THR1	TOILET ROLL HOLDER
TMV	THERMOSTATIC MIXING VALVE
TP1	TAP - WALL MOUNTED SENSOR
TRH2	TOILET ROLL HOLDER
UR1	URINAL - WALL HUNG
UR4	URINAL - TROUGH

Archipelago

Archipelago
Level 3, 150 George Street, Brisbane QLD 4000
T +617 3236 4606 www.archipelago.com.au

© ARCHPELAGO ARCHITECTS PTY. LTD. All Rights Reserved
This work is copyright and cannot be reproduced or copied by any means without written permission of Archipelago Architects Pty Ltd. Any
license, express or implied, to use this document for any purpose
whatsoever is restricted to the terms of the agreement between Archipelago Architects PT
Y Ltd and the instructing party.

SKYGATE PLAY

SECTIONS 01

Drawn JB	Checked DC
Design Coordinated	Compliance Checked
Authorised For Issue DC	Construction Checked

 Brisbane Airport	Brisbane Airport Corporation Pty Ltd 11 The Circuit Brisbane Airport QLD 4008 PO Box 61 Hamilton QLD 4007 Australia	Scale 1 : 200
	Telephone : 61 7 3406 3000 Facsimile : 61 7 3406 3111 Email : info@bne.com.au	Size A1
	www.brisbaneairport.com.au ABN 54 076 870 650	Revision C

	Project No.	Originator	Volume	Level	Type	Discipline	Number
Drawing No.	25021 - ARC - XX - XX - DR - AR - 000401						