



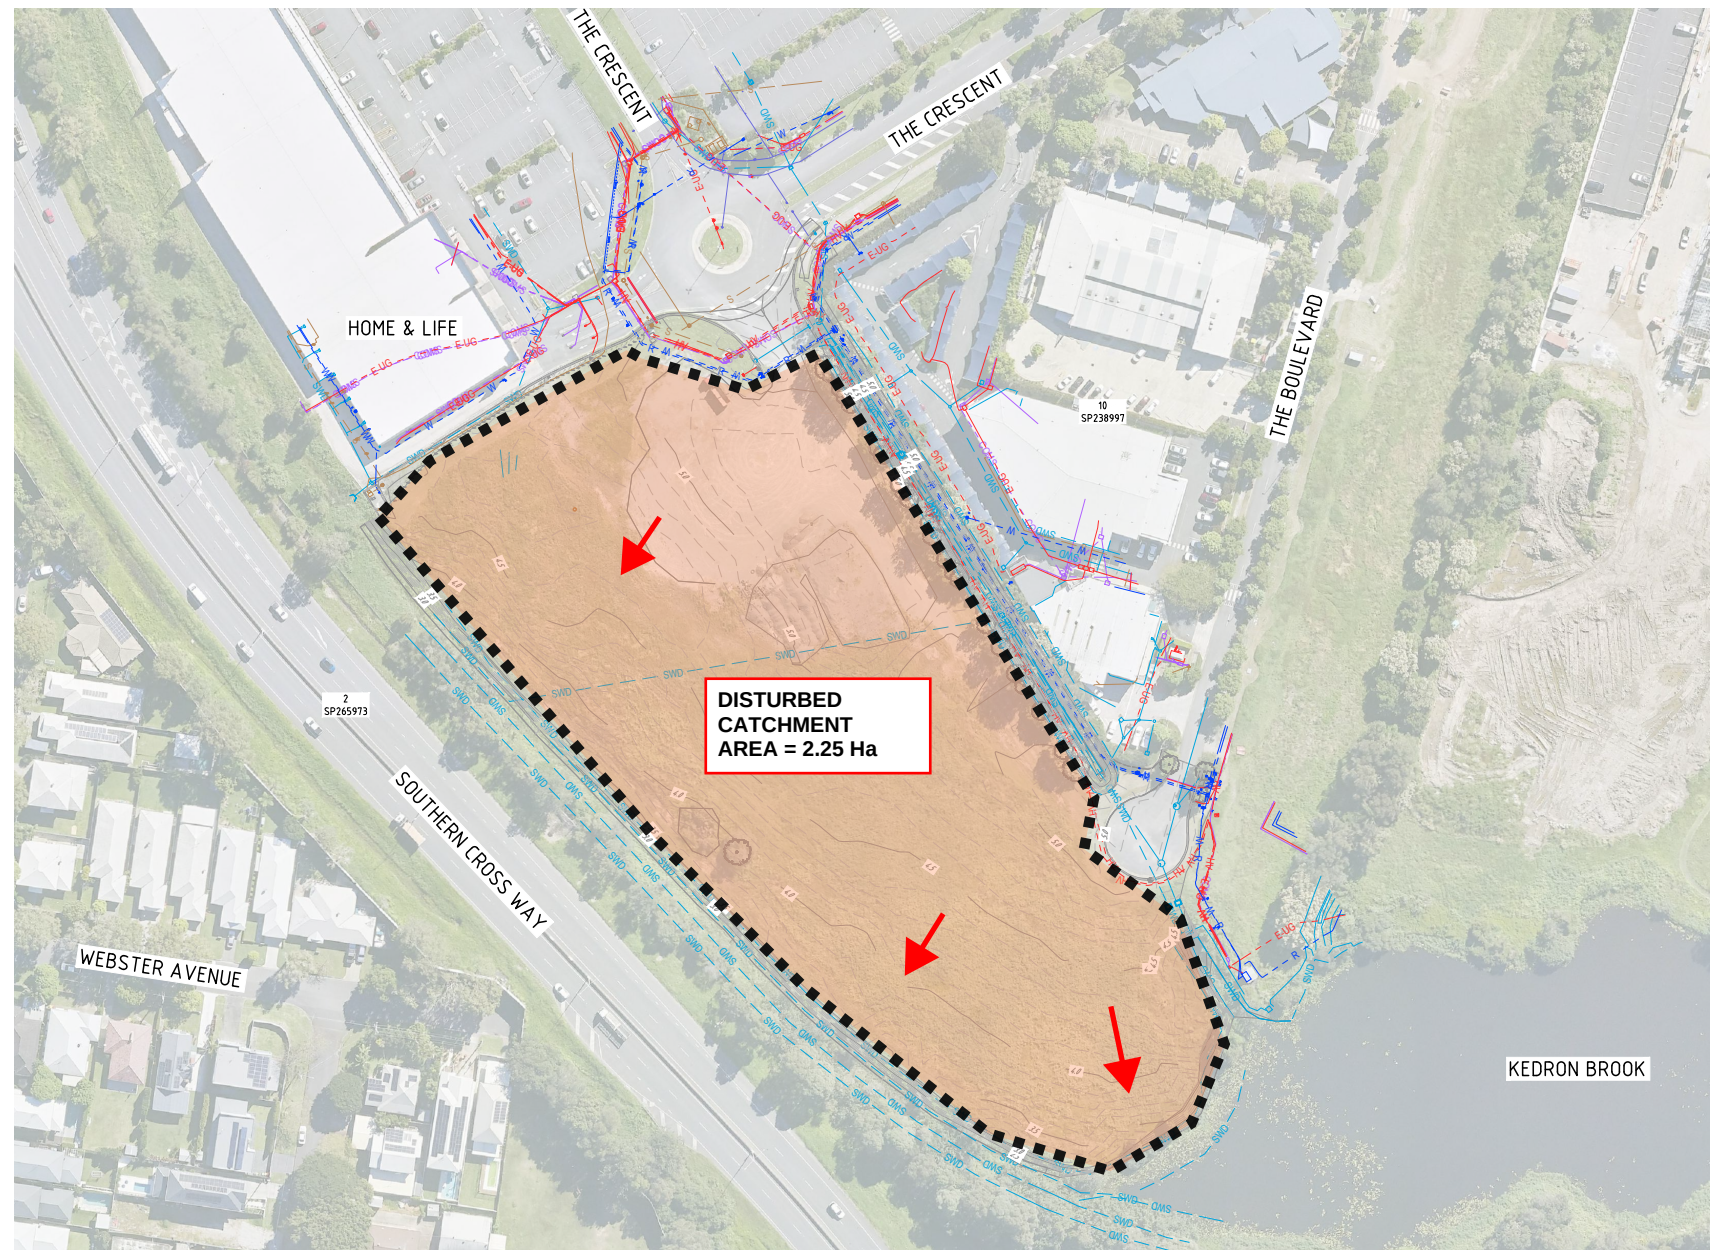

DISTURBED CATCHMENT LAYOUT PLAN

SCALE 1:800@A1
0 10 20 30 40m

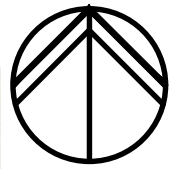


LOCALITY PLAN
NTS

ESC LEGEND:

- DISTURBED CATCHMENT
- RUNOFF FLOW DIRECTION

ORIGINAL DRAWINGS PROVIDED BY NORTHROP CONSULTING ENGINEERS

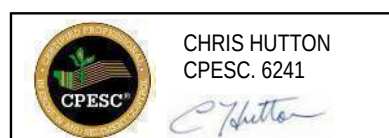

89 CASLICK LANE,
BROADWATER, QLD.
PH: (MOB) 0400 643 883

APPROVED
DATE
26-05-2026

CHRIS HUTTON - CPESC No. 6241

CLIENT	NORTHROP CONSULTING ENGINEERS		JOB No.	ESC-0606
PROJECT	SKYGATE PLAY		DRAWING No. / REVISION	DR-01 / b
LOCATION	LOT SKG26, THE CIRCUIT, BRISBANE AIRPORT			
DRAWING TITLE	EROSION AND SEDIMENT CONTROL - LOCALITY AND CATCHMENT PLAN			