


NOTE:
DIVERSION BUNDS SHOWN INDICATIVELY (TYP.).
INSTALL BUNDS WHERE THERE IS A LIKELYHOOD OF
RUNOFF FLOWING OFF SITE DURING THE
EARTHWORKS PHASE

DIVERSION BUNDS ARE TO BE
REINSTATED PROGRESSIVELY AT
THE TOP OF BATTER AS
EARTHWORKS LEVELS CHANGE

- ESC LEGEND:**
- ROCK PAD CONSTRUCTION ENTRANCE TO IECA STD. DRG. EXIT-01
 - SEDIMENT FENCE TO IECA STD. DRGS. SF-1 AND SF-02
 - DIVERSION BUND REFER DETAIL ON DR-05
 - ROCK FILTER DAM WITH ENERGY DISSIPATION APRON REFER DR-05 FOR DETAILS
 - COIR LOGS / SANDBAGS INSTALLED ACROSS SITE ENTRANCES PRIOR TO FORECAST RAIN EVENTS

- LEGEND**
- XX.XX--- PROPOSED SURFACE CONTOURS
 - XX.XX--- EXISTING SURFACE CONTOURS
 - EXISTING PROPERTY BOUNDARY
 - W --- EXISTING WATER MAIN
 - R --- EXISTING RECYCLED WATER
 - S --- EXISTING SEWER PIPE
 - RM --- EXISTING SEWER PIPE RISING MAIN
 - E-UG --- EXISTING ELECTRICITY (UNDERGROUND)
 - SWD --- EXISTING STORMWATER DRAINAGE PIPE CL
 - EXISTING STORMWATER STRUCTURES
 - WORKS BOUNDARY
 - SPOT LEVEL (EXISTING)
 - SPOT LEVEL (DESIGN)
 - PROPOSED RETAINING WALL

CUT/FILL DEPTH		
DEPTH COLOUR	LOWER DEPTH	UPPER DEPTH
	-999m	-2.0m
	-2.0m	-1.5m
	-1.5m	-1.25m
	-1.25m	-1.0m
	-1.0m	-0.75m
	-0.75m	-0.5m
	-0.5m	-0.25m
	-0.25m	0.0m
	0.0m	0.25m
	0.25m	0.5m
	0.5m	0.75m
	0.75m	1.0m
	1.0m	1.25m
	1.25m	1.5m
	1.5m	2.0m
	2.0m	999m

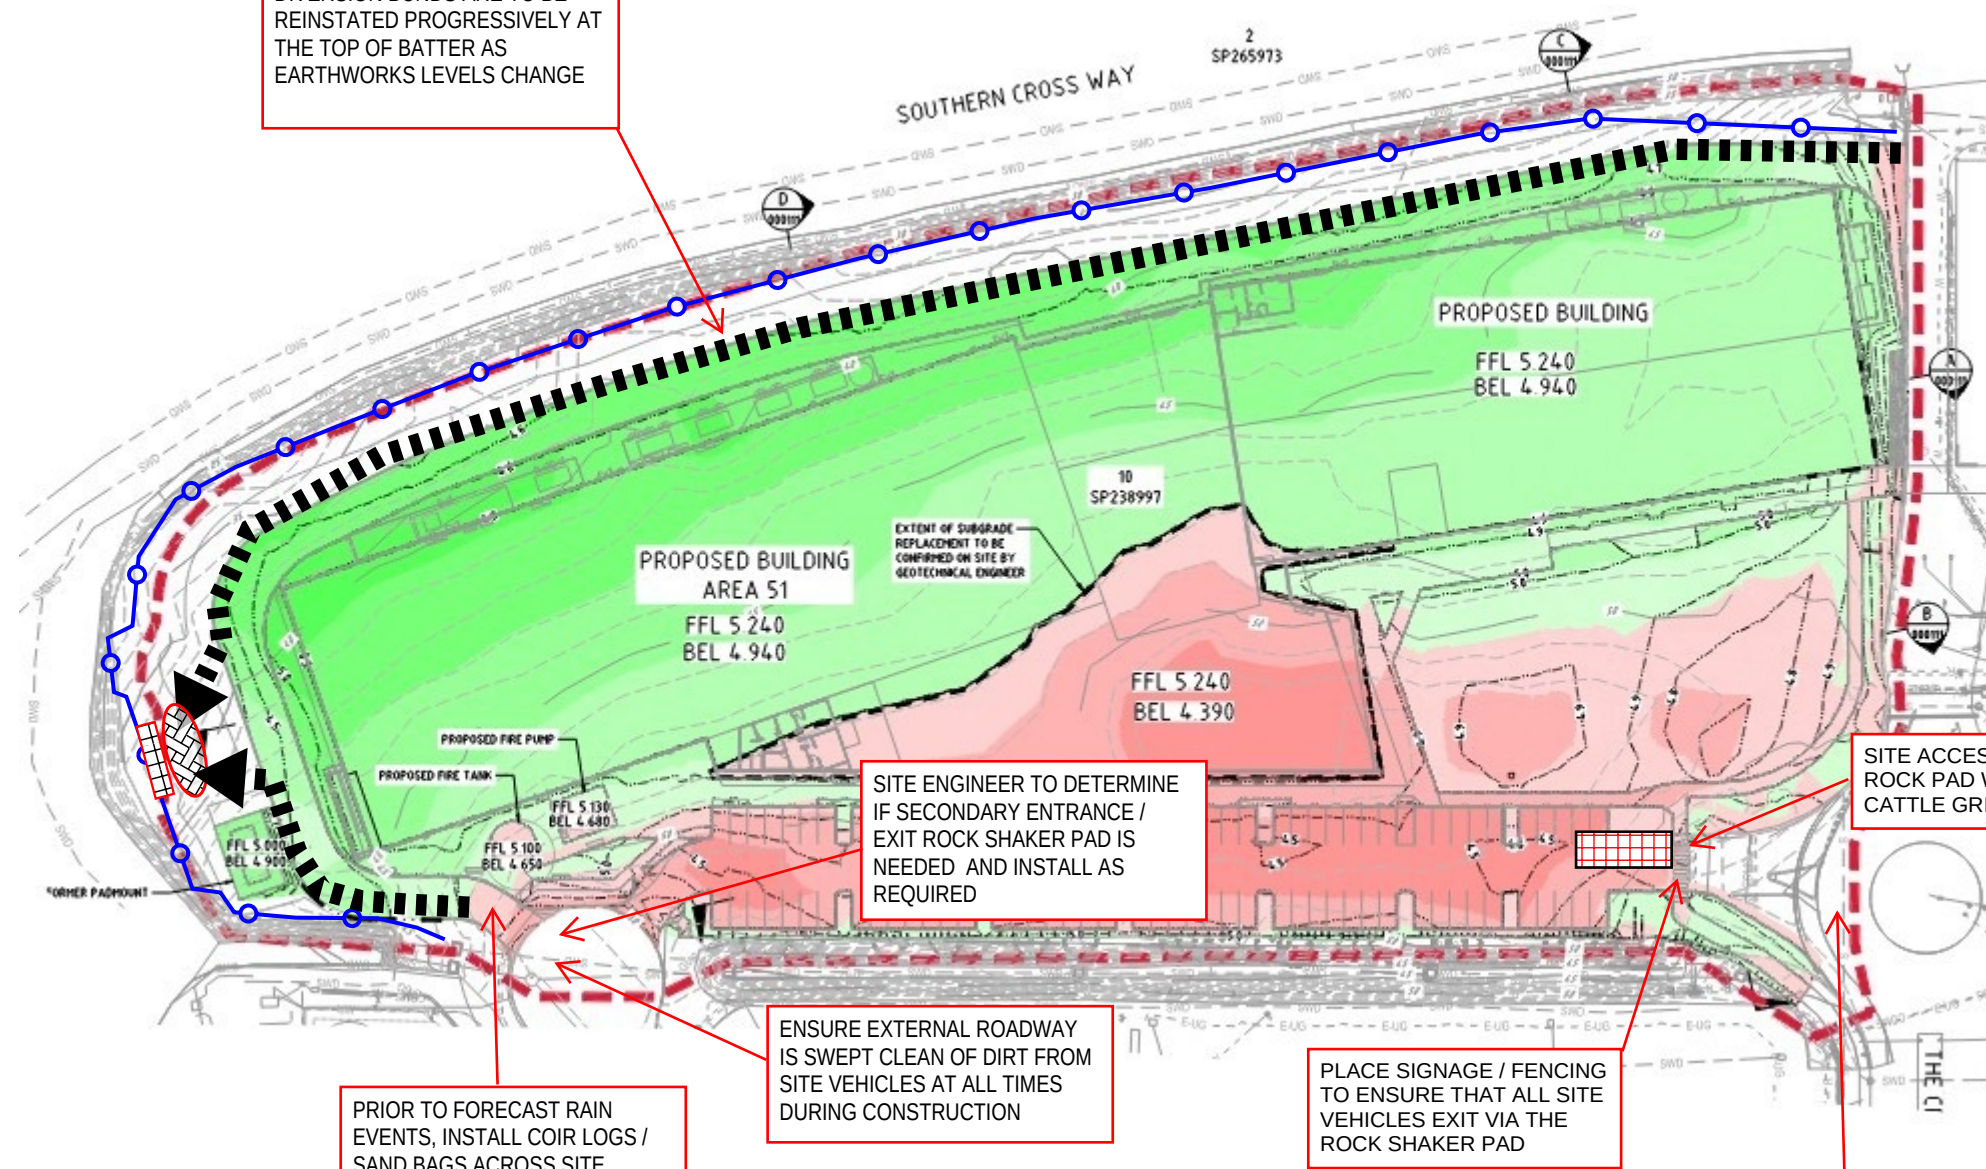

SITE ENGINEER TO DETERMINE
IF SECONDARY ENTRANCE /
EXIT ROCK SHAKER PAD IS
NEEDED AND INSTALL AS
REQUIRED

ENSURE EXTERNAL ROADWAY
IS SWEEPED CLEAN OF DIRT FROM
SITE VEHICLES AT ALL TIMES
DURING CONSTRUCTION


PLACE SIGNAGE / FENCING
TO ENSURE THAT ALL SITE
VEHICLES EXIT VIA THE
ROCK SHAKER PAD

ENSURE EXTERNAL ROADWAY
IS SWEEPED CLEAN OF DIRT FROM
SITE VEHICLES AT ALL TIMES
DURING CONSTRUCTION

PRIOR TO FORECAST RAIN
EVENTS, INSTALL COIR LOGS /
SAND BAGS ACROSS SITE
ENTRANCES WHERE INTERNAL
DISTURBED AREAS GRADE OFF
SITE (TYP.)

NOTE: SITE ACCESS ROCK SHAKER PADS
SHOULD BE TURNED OVER AT REGULAR
INTERVALS TO DESILT AND REMAIN EFFECTIVE

LAYOUT PLAN

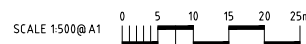

ORIGINAL DRAWINGS PROVIDED BY NORTHROP CONSULTING ENGINEERS



CHRIS HUTTON

CPESC. 6241



89 CASLICK LANE,
BROADWATER, QLD.
PH: (MOB) 0400 643 883

APPROVED

DATE

26-05-2026



CHRIS HUTTON - CPESC No. 6241

CLIENT

NORTHROP CONSULTING ENGINEERS

JOB No.

ESC-0606

PROJECT

SKYGATE PLAY

LOCATION

LOT SKG26, THE CIRCUIT, BRISBANE AIRPORT

DRAWING TITLE

EROSION AND SEDIMENT CONTROL - EARTHWORKS PHASE

DRAWING No. / REVISION

DR-04 / b