


ESC LEGEND:

ROCK PAD CONSTRUCTION ENTRANCE TO IECA STD. DRG. EXIT-01

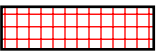

SEDIMENT FENCE TO IECA STD. DRGS. SF-1 AND SF-02




GULLY INLET PROTECTION
SEDIMENT TRAP REFER DR-07 FOR DETAILS



LEGEND

- EXISTING PROPERTY BOUNDARY
- EXISTING CONTOUR MAJOR
- PROPOSED CONTOUR MINOR
- EXISTING ELECTRICITY
- EXISTING ELECTRICITY (UNDERGROUND)
- EXISTING ELECTRICITY (HIGH VOLTAGE)
- EXISTING WATER
- EXISTING RECYCLE WATER
- EXISTING IRRIGATION
- EXISTING STORMWATER
- EXISTING SEWER MAIN
- EXISTING SEWER MAIN (RAISING MAIN)
- EXISTING COMMUNICATION
- PROPOSED RETAINING WALL
- WORKS BOUNDARY
- PROPOSED CONCRETE HARDSTAND PAVEMENT IN ACCORDANCE WITH STRUCTURAL ENGINEERS SPECIFICATION
- PROPOSED BUILDING. REFER TO ARCHITECTURAL DRAWINGS FOR DETAILS.
- PROPOSED LANDSCAPE AREA. REFER TO LANDSCAPE DRAWINGS FOR DETAILS
- PROPOSED 600mm AC REINSTATEMENT STRIP REFER TO DWG C-220 FOR DETAILS
- PROPOSED CONCRETE FOOTPATH IN ACCORDANCE WITH IPWEA STD DRG PSD-302
- PROPOSED PRECAST CONCRETE ISLAND REFER TO CIVILMART DWG 0913R FOR DETAILS
- PROPOSED WATER MAIN
- PROPOSED SEWER MAIN
- PROPOSED INTEGRAL KERB REFER TO DRAWING C-220
- PROPOSED ROOF EXTEND REFER TO ARCHITECTURAL DWG FOR DETAILS
- PROPOSED STORMWATER DRAINAGE
- PROPOSED STORMWATER HEADWALL
- PROPOSED STORMWATER MANHOLE
- PROPOSED STORMWATER PIT
- PROPOSED STORMWATER STRUCTURE NUMBER
- PROPOSED SEWER STRUCTURE NUMBER

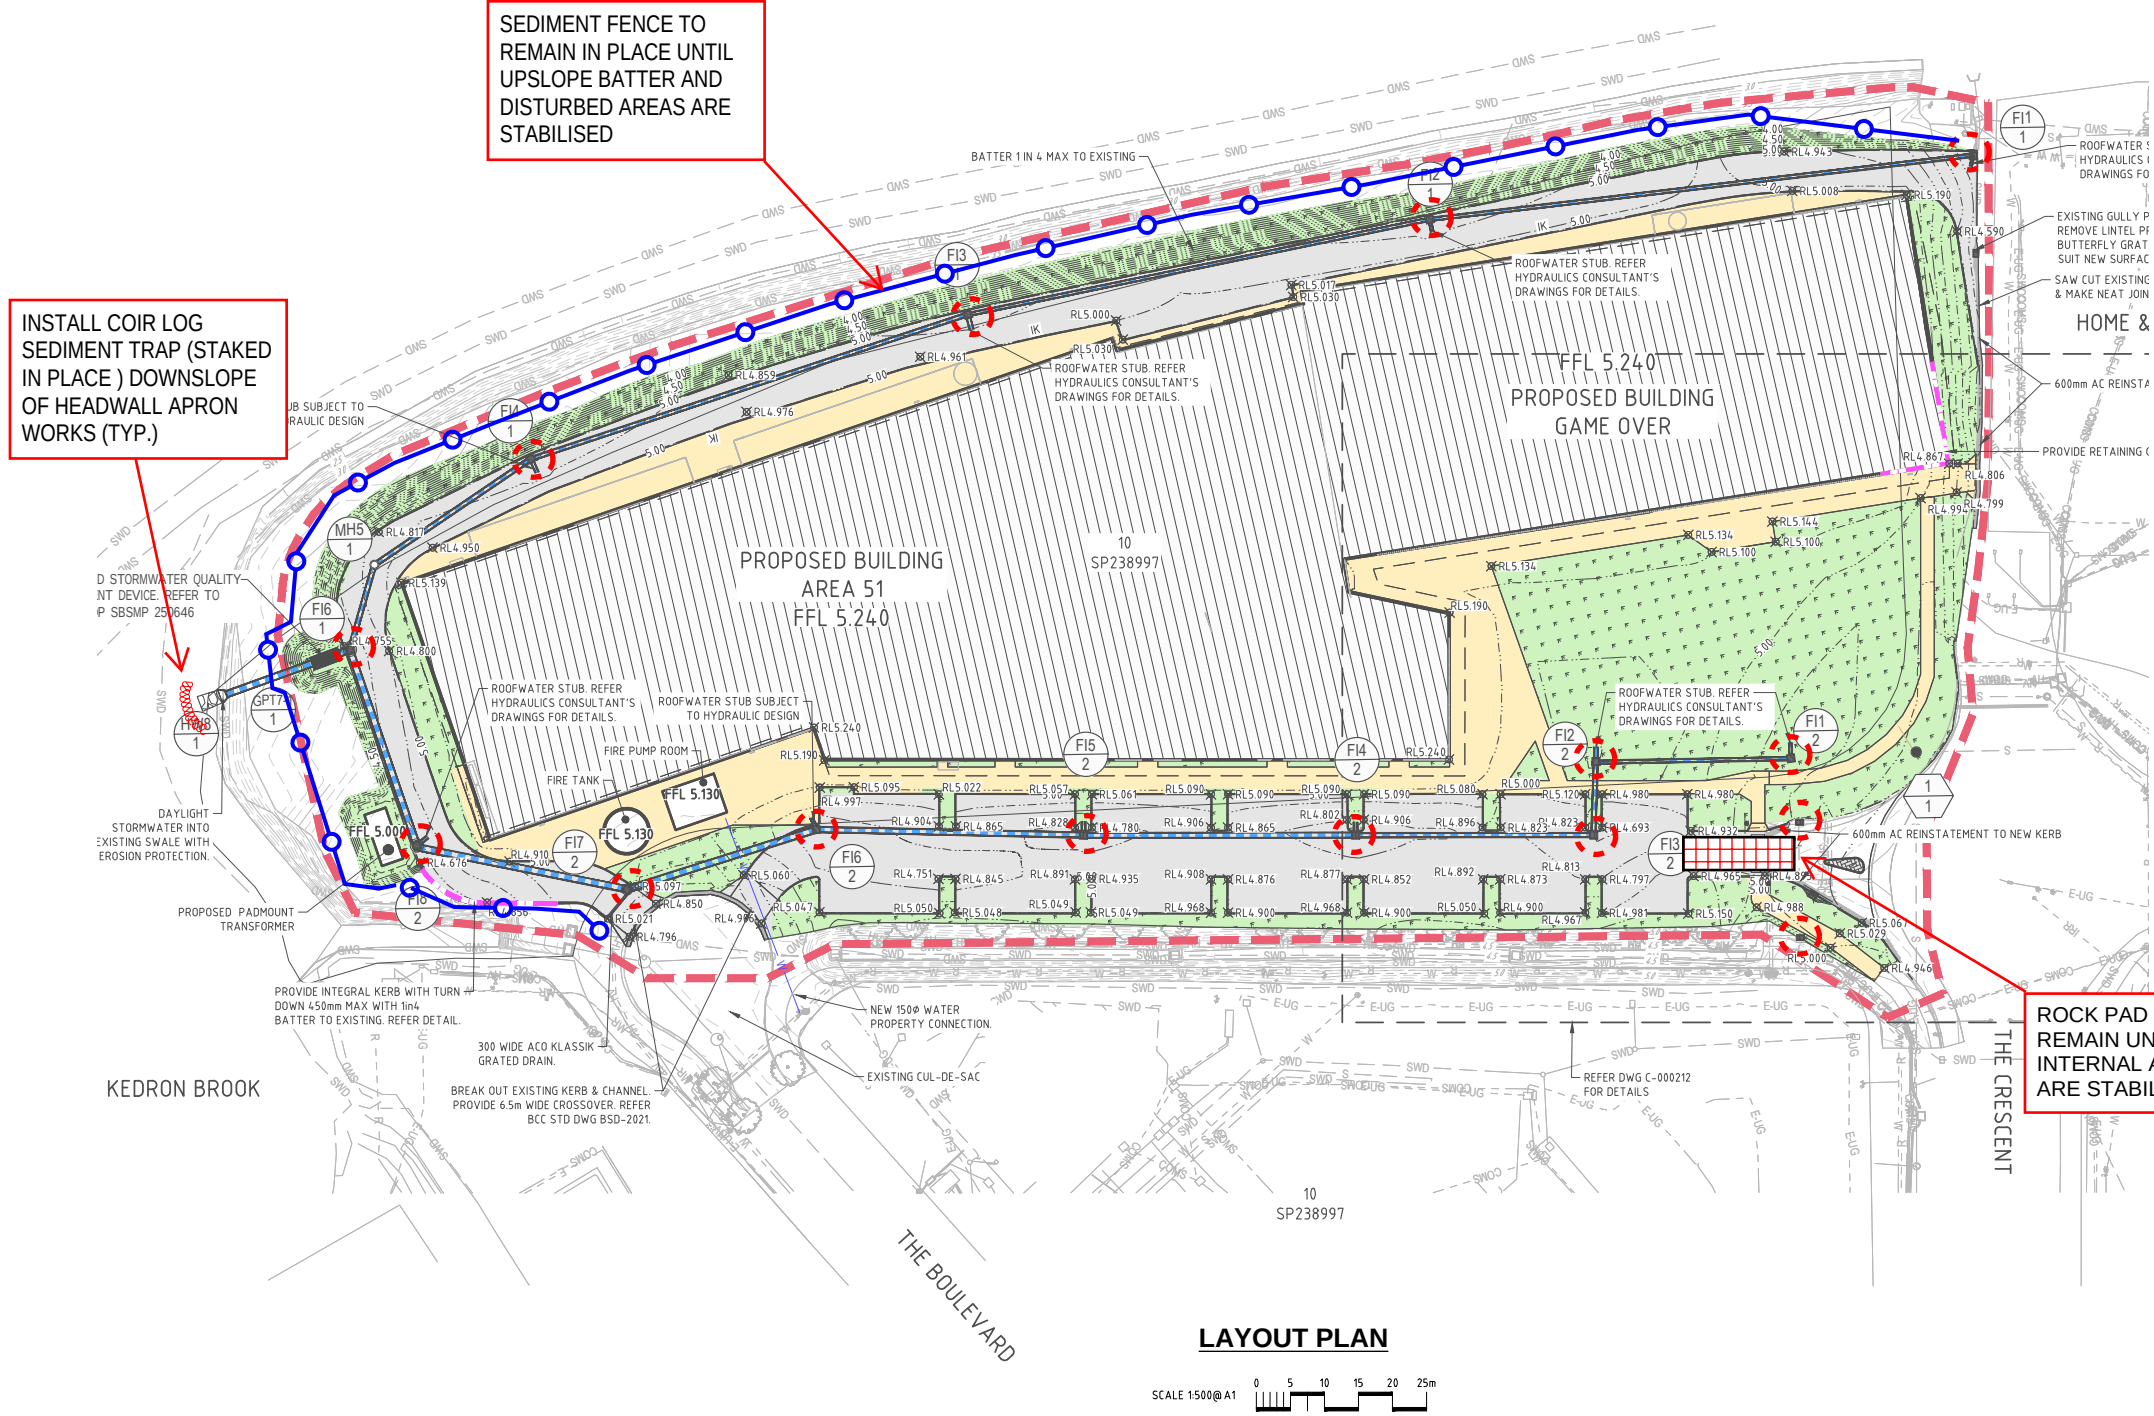

LAYOUT PLAN

SCALE 1500@A1

ORIGINAL DRAWINGS PROVIDED BY NORTHPROP CONSULTING ENGINEERS

CHRIS HUTTON
CPESC. 6241



89 CASLICK LANE,
BROADWATER, QLD.
PH: (MOB) 0400 643 883

APPROVED
DATE
26-05-2026
CHRIS HUTTON - CPESC No. 6241

CLIENT
NORTHPROP CONSULTING ENGINEERS
PROJECT
SKYGATE PLAY
LOCATION
LOT SKG26, THE CIRCUIT, BRISBANE AIRPORT
DRAWING TITLE
EROSION AND SEDIMENT CONTROL - CIVIL WORKS AND STABILISATION PHASE

JOB No.
ESC-0606
DRAWING No. / REVISION
DR-06 / b