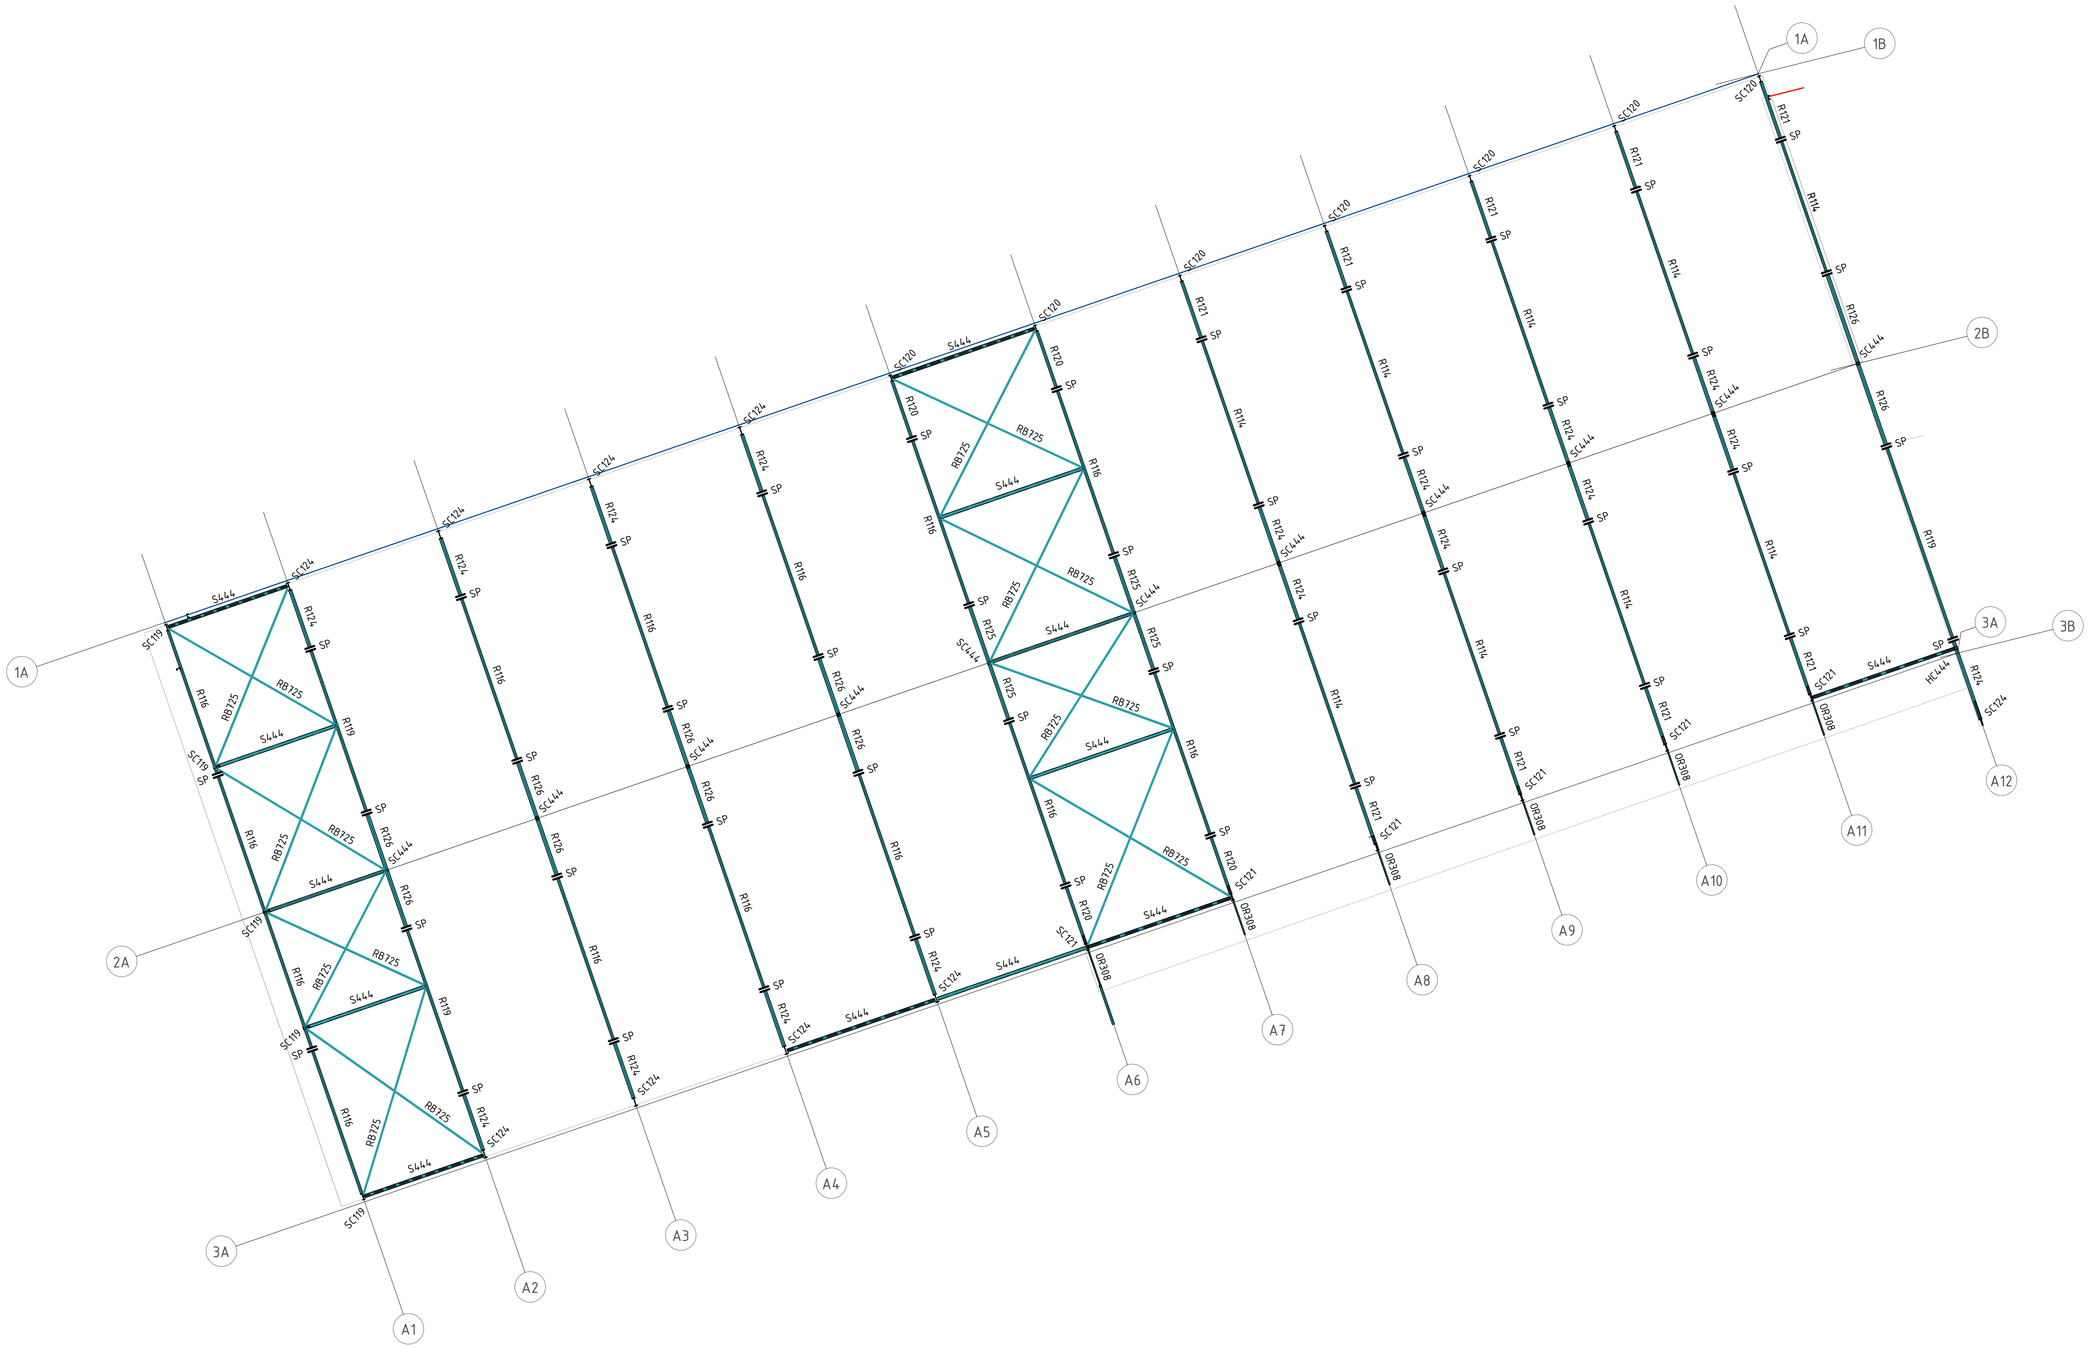

STEELWORK PLAN NOTES

1. REFER S0.001-S0.003 FOR CONSTRUCTION NOTES
2. UNLESS NOTED OTHERWISE ON PLAN LOADS AS FOLLOWS:

ROOF LIVE LOADS	
GENERAL	25 kg/m²
SUPERIMPOSED DEAD LOAD	
ROOF SHEETING	6 kg/m²
CEILING AND INSULATION	15 kg/m²
SERVICES	15 kg/m²
SOLAR	10 kg/m²

3. ALL EXTERNAL STEELWORK TO BE HOT DIPPED GALVANISED

STEELWORK LEGEND

SP — DENOTES STEEL SPLICE LOCATION

TF — TOP FLANGE CONNECTION

BF — BOTTOM FLANGE CONNECTION

MEMBER SCHEDULE

MARK	SIZE
COLUMN	
SC119	410 UB 53.7
SC120	410 UB 59.7
SC121	460 UB 67.1
SC122	460 UB 74.6
SC124	530 UB 82.0
SC433	100 x 100 x 5.0 SHS
SC440	150 x 150 x 5.0 SHS
SC444	200 x 200 x 6.0 SHS
SC446	250 x 250 x 6.0 SHS
HANGING COLUMN	
HC444	200 x 200 x 6.0 SHS
MULLION	
M308	250 PFC
M433	100 x 100 x 5.0 SHS
BEAM	
B306	200 PFC
B308	250 PFC
B309	300 PFC
OUTRIGGER	
OR308	250 PFC
RAFTER	
R108	200 UB 25.4
R114	310 UB 40.4
R116	360 UB 44.7
R117	360 UB 50.7
R119	410 UB 53.7
R120	410 UB 59.7
R121	460 UB 67.1
R122	460 UB 74.6
R124	530 UB 82.0
R125	530 UB 92.4
R126	610 UB 101
R308	250 PFC
R309	300 PFC
RAKING ANGLE	
RA728	90 x 90 x 8 EA
ROOF BRACING	
RB249	89x89x5.0SHS
RB725	75 x 75 x 8 EA
STRUT	
S433	100x100x5.0SHS
S440	150x150x5.0SHS
S444	200x200x6.0SHS
TRANSFER BEAM	
TB136	800 WB 146
WALL BRACING	
WB430	89x89x6.0SHS
WB725	75 x 75 x 8 EA
WALL HEAD	
WH433	100x100x5.0SHS
WH437	125x125x5.0SHS

UPPER FRAMING ROOF PLAN - PART 1

SCALE 1 : 200

COPYRIGHT :
REPRODUCTION OF WHOLE OR PART OF THIS DOCUMENT CONSTITUTES AN INFRINGEMENT OF COPYRIGHT. THE INFORMATION, IDEAS, AND CONCEPTS CONTAINED IN THIS DOCUMENT ARE CONFIDENTIAL. THE RECIPIENT(S) OF THIS DOCUMENT IS PROHIBITED FROM DISCLOSING SUCH INFORMATION IDEAS AND CONCEPTS TO ANY PERSON WITHOUT THE PRIOR WRITTEN CONSENT OF THE BRISBANE AIRPORT CORPORATION PTY. LTD.

DRN	AMENDMENTS	DATE	REV
NS	BAC APPROVAL	11.06.26	C
NS	STEEL DETAILS ISSUE	04.06.26	B
NS	PRELIM STEEL ISSUE	29.05.26	A

NORTHROP
PROJECT NUMBER: 250946

Drawn: HP	Checked:
Design Coordinated: HP	Compliance Checked: --
Authorised For Issue: NS	Construction Checked: --

SKYGATE PLAY

ROOF FRAMING PLAN - PART 1

Brisbane Airport
BRISBANE AIRPORT CORPORATION PTY LTD
11 THE CIRCUIT, BRISBANE AIRPORT, QLD, 4008, AUSTRALIA
PO BOX 61, HAMILTON CENTRAL, QLD, 4007, AUSTRALIA
T: +61 7 3406 3000
E: INFO@BNE.COM.AU
W: BNE.COM.AU

Scale: As indicated
Size: A1
Revision: C

Drawing Number	Project No.	Originator	Volume	Level	Type	Discipline	Number
	25021	NOR	XX	01	DR	ST	006001

File Path: Autodesk Docs://250946 - BNE Play/25021-NOR-ZZ-ZZ-M3-ST-000001.rvt

Plot Date & Time: 11/06/2026 10:03:32 AM