


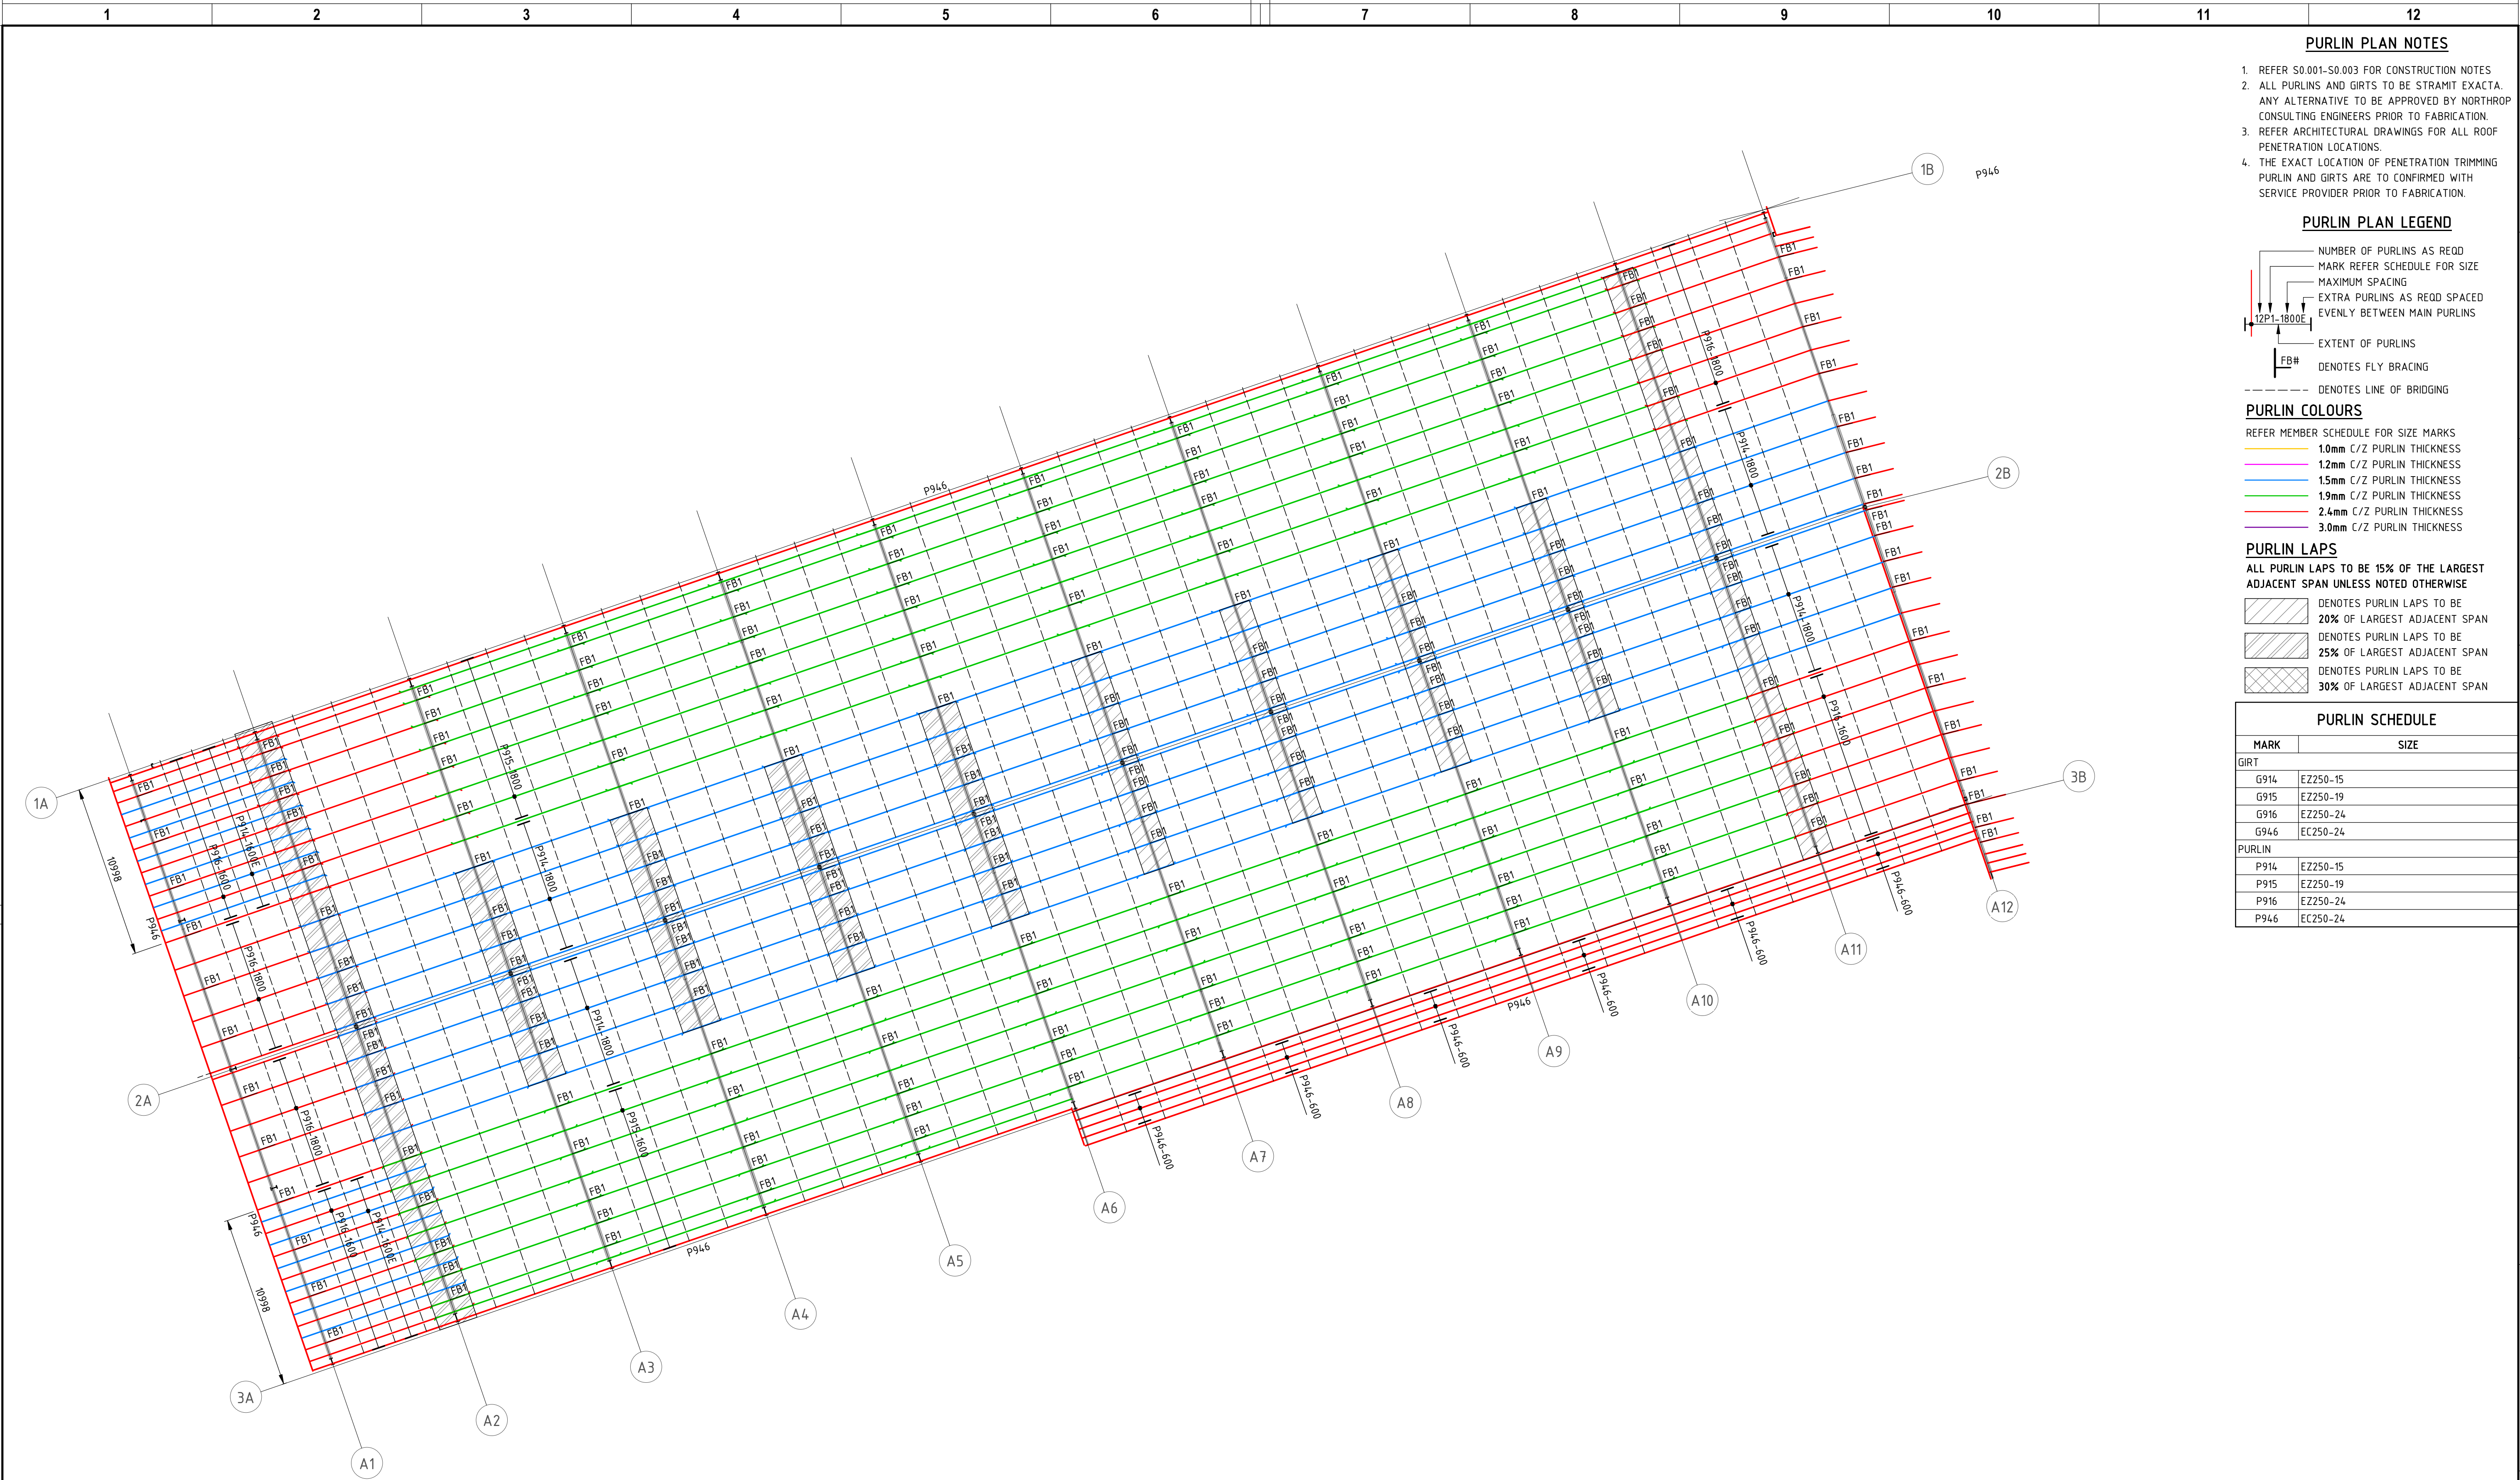


UPPER PURLIN PLAN - PART 1
SCALE 1 : 200

PURLIN PLAN NOTES

- REFER S0.001-S0.003 FOR CONSTRUCTION NOTES
- ALL PURLINS AND GIRTS TO BE STRAMIT EXACTA.
ANY ALTERNATIVE TO BE APPROVED BY NORTHROP CONSULTING ENGINEERS PRIOR TO FABRICATION.
- REFER ARCHITECTURAL DRAWINGS FOR ALL ROOF PENETRATION LOCATIONS.
- THE EXACT LOCATION OF PENETRATION TRIMMING PURLIN AND GIRTS ARE TO BE CONFIRMED WITH SERVICE PROVIDER PRIOR TO FABRICATION.

PURLIN PLAN LEGEND

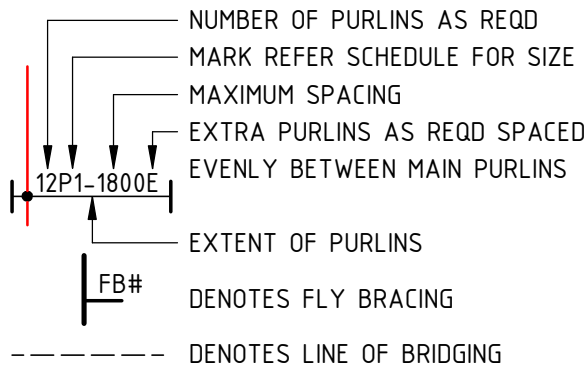

PURLIN COLOURS

- REFER MEMBER SCHEDULE FOR SIZE MARKS
- 1.0mm C/Z PURLIN THICKNESS
 - 1.2mm C/Z PURLIN THICKNESS
 - 1.5mm C/Z PURLIN THICKNESS
 - 1.9mm C/Z PURLIN THICKNESS
 - 2.4mm C/Z PURLIN THICKNESS
 - 3.0mm C/Z PURLIN THICKNESS

PURLIN LAPS

ALL PURLIN LAPS TO BE 15% OF THE LARGEST ADJACENT SPAN UNLESS NOTED OTHERWISE

- 20% OF LARGEST ADJACENT SPAN
- 25% OF LARGEST ADJACENT SPAN
- 30% OF LARGEST ADJACENT SPAN

PURLIN SCHEDULE

MARK	SIZE
GIRT	
G914	EZ250-15
G915	EZ250-19
G916	EZ250-24
G946	EC250-24
PURLIN	
P914	EZ250-15
P915	EZ250-19
P916	EZ250-24
P946	EC250-24

COPYRIGHT : REPRODUCTION OF WHOLE OR PART OF THIS DOCUMENT CONSTITUTES AN INFRINGEMENT OF COPYRIGHT. THE INFORMATION, IDEAS, AND CONCEPTS CONTAINED IN THIS DOCUMENT ARE CONFIDENTIAL. THE RECIPIENT(S) OF THIS DOCUMENT IS PROHIBITED FROM DISCLOSING SUCH INFORMATION IDEAS AND CONCEPTS TO ANY PERSON WITHOUT THE PRIOR WRITTEN CONSENT OF THE BRISBANE AIRPORT CORPORATION PTY. LTD.	NS	BAC APPROVAL	11.06.26	C
	NS	STEEL DETAILS ISSUE	04.06.26	B
	NS	PRELIM STEEL ISSUE	29.05.26	A
	DRN	AMENDMENTS	DATE	REV

NORTHROP
PROJECT NUMBER: 250946

Drawn: HP	Checked:
Design Coordinated: HP	Compliance Checked: --
Authorised For Issue: NS	Construction Checked: --

SKYGATE PLAY

ROOF PURLIN PLAN - PART 1

	BRISBANE AIRPORT CORPORATION PTY LTD 11 THE CIRCUIT, BRISBANE AIRPORT, QLD 4008, AUSTRALIA PO BOX 61, HAMILTON CENTRAL, QLD 4007, AUSTRALIA T: +61 7 3406 3000 E: INFO@BNE.COM.AU W: BNE.COM.AU							Scale: As indicated
								Size: A1
								Revision: C
Project No.	Originator	Volume	Level	Type	Discipline	Number		
25021	NOR	XX	01	DR	ST	006011		