

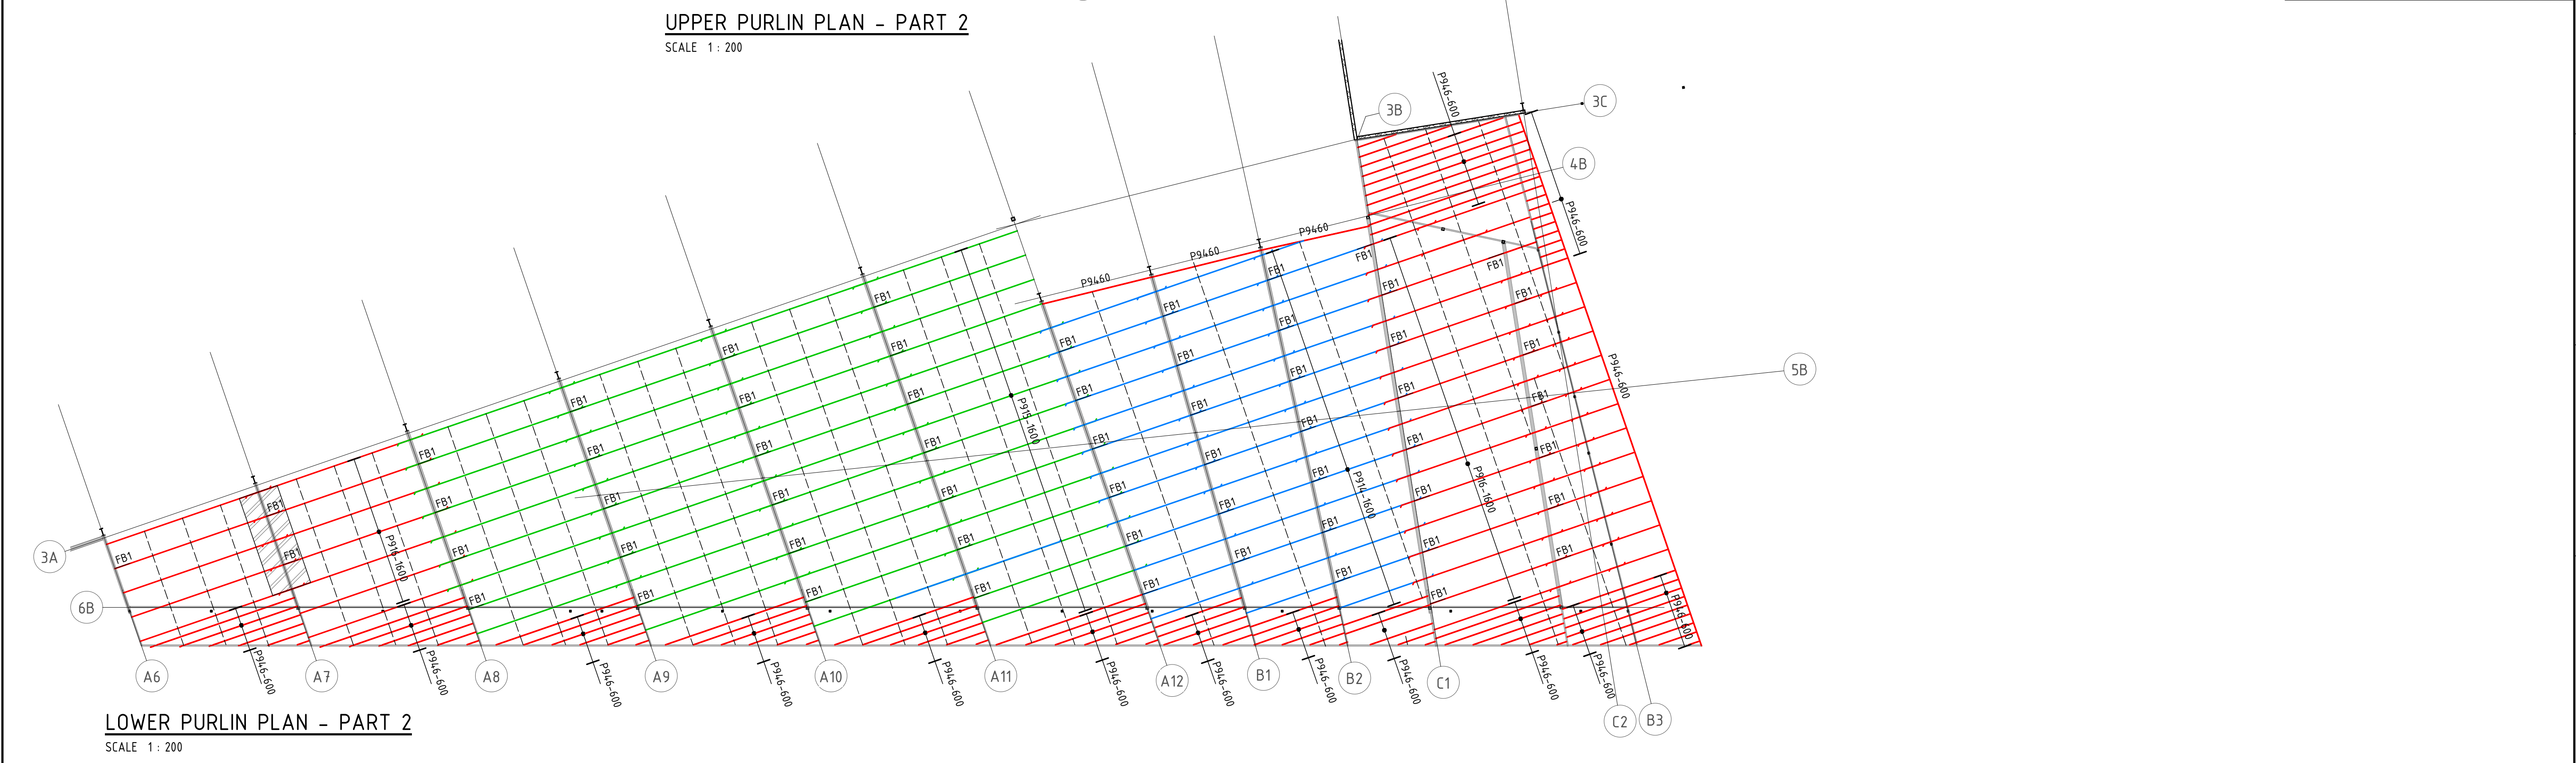


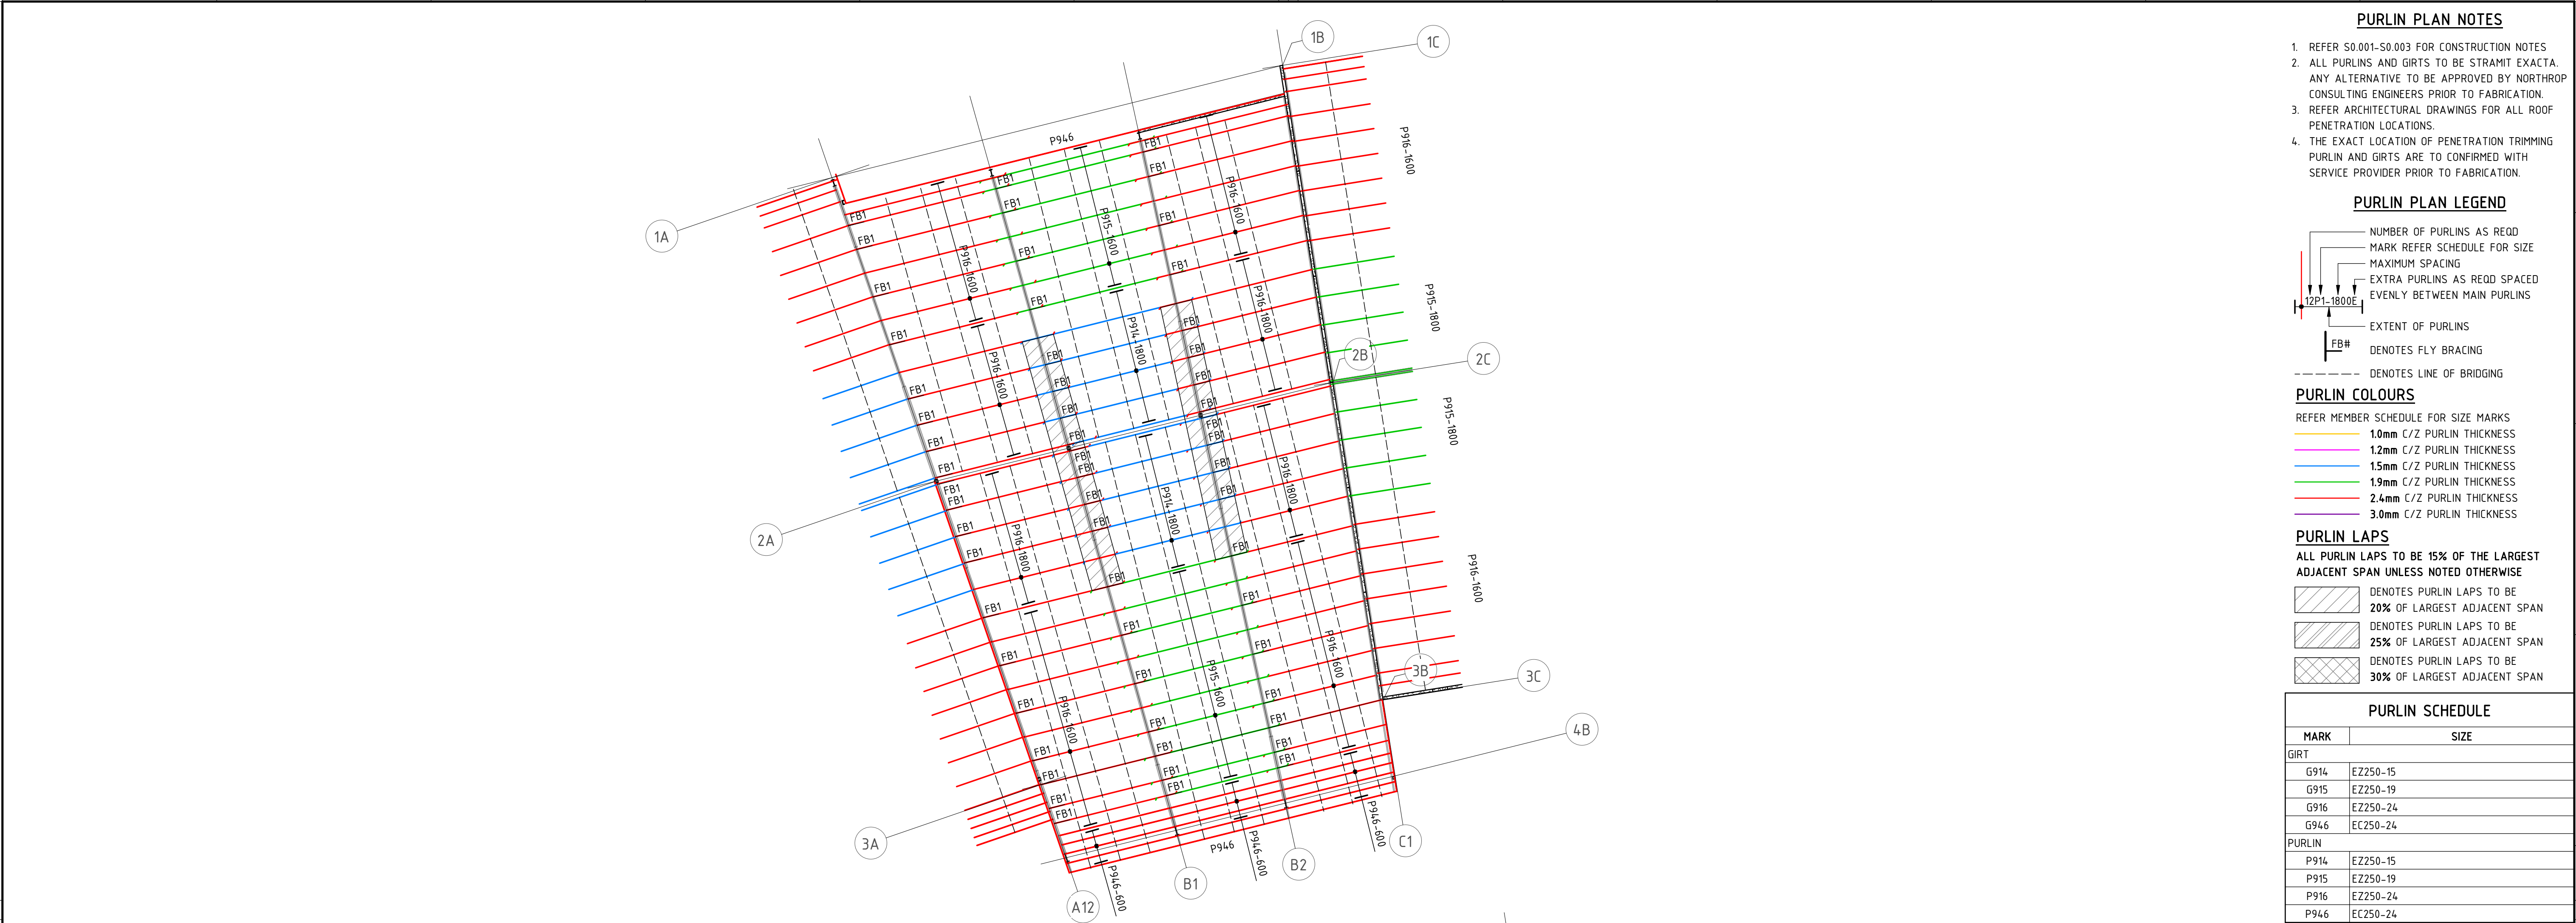

PURLIN PLAN NOTES

- REFER S0.001-S0.003 FOR CONSTRUCTION NOTES
- ALL PURLINS AND GIRTS TO BE STRAMIT EXACTA.
ANY ALTERNATIVE TO BE APPROVED BY NORTHROP CONSULTING ENGINEERS PRIOR TO FABRICATION.
- REFER ARCHITECTURAL DRAWINGS FOR ALL ROOF PENETRATION LOCATIONS.
- THE EXACT LOCATION OF PENETRATION TRIMMING PURLIN AND GIRTS ARE TO CONFIRMED WITH SERVICE PROVIDER PRIOR TO FABRICATION.

PURLIN PLAN LEGEND

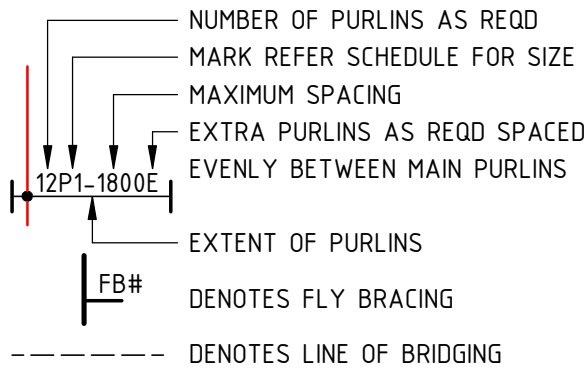

PURLIN COLOURS

- REFER MEMBER SCHEDULE FOR SIZE MARKS
- 1.0mm C/Z PURLIN THICKNESS
 - 1.2mm C/Z PURLIN THICKNESS
 - 1.5mm C/Z PURLIN THICKNESS
 - 1.9mm C/Z PURLIN THICKNESS
 - 2.4mm C/Z PURLIN THICKNESS
 - 3.0mm C/Z PURLIN THICKNESS

PURLIN LAPS

ALL PURLIN LAPS TO BE 15% OF THE LARGEST ADJACENT SPAN UNLESS NOTED OTHERWISE

- DENOTES PURLIN LAPS TO BE 20% OF LARGEST ADJACENT SPAN
- DENOTES PURLIN LAPS TO BE 25% OF LARGEST ADJACENT SPAN
- DENOTES PURLIN LAPS TO BE 30% OF LARGEST ADJACENT SPAN

PURLIN SCHEDULE

MARK	SIZE
GIRT	
G914	EZ250-15
G915	EZ250-19
G916	EZ250-24
G946	EC250-24
PURLIN	
P914	EZ250-15
P915	EZ250-19
P916	EZ250-24
P946	EC250-24