




SECTION 1A
SCALE 1 : 200

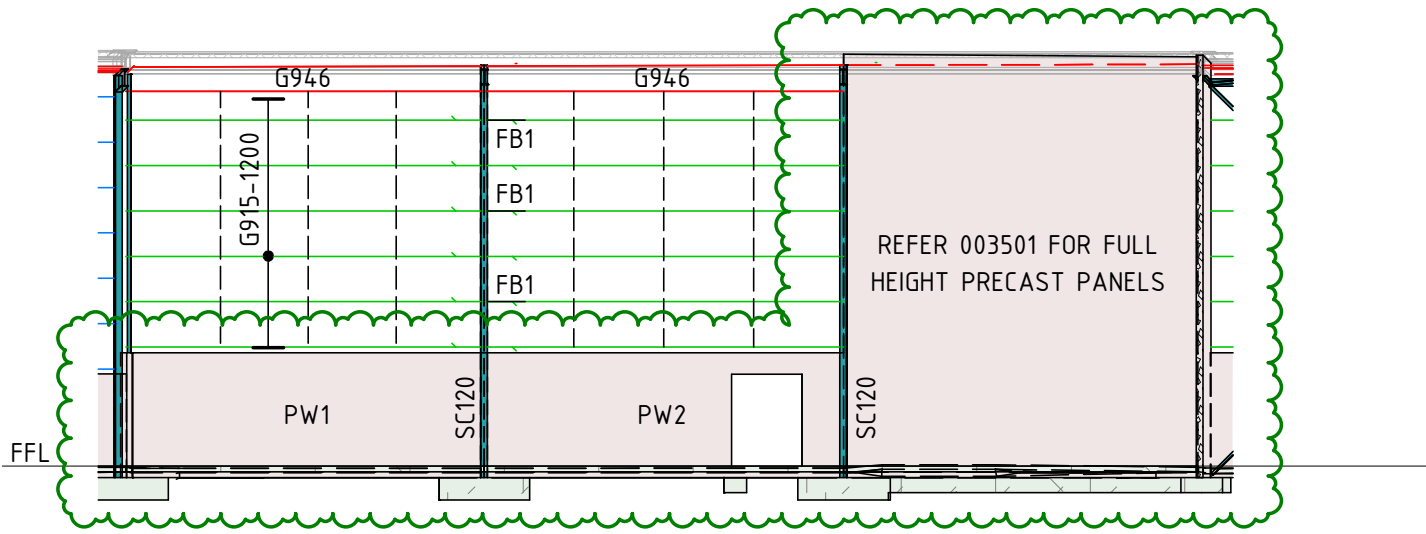

SECTION 1B
SCALE 1 : 200

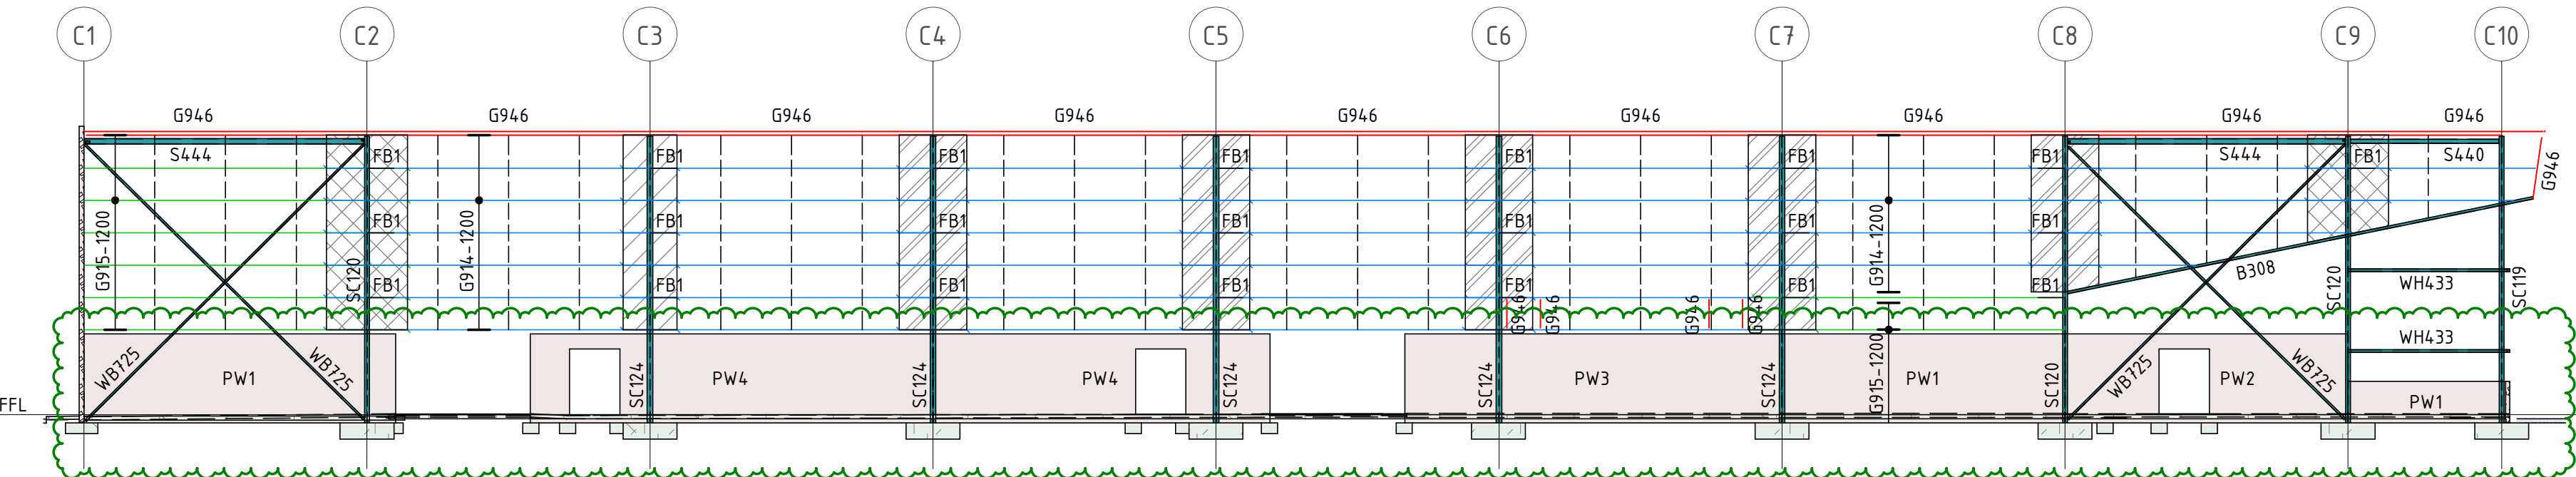

SECTION 1C
SCALE 1 : 200

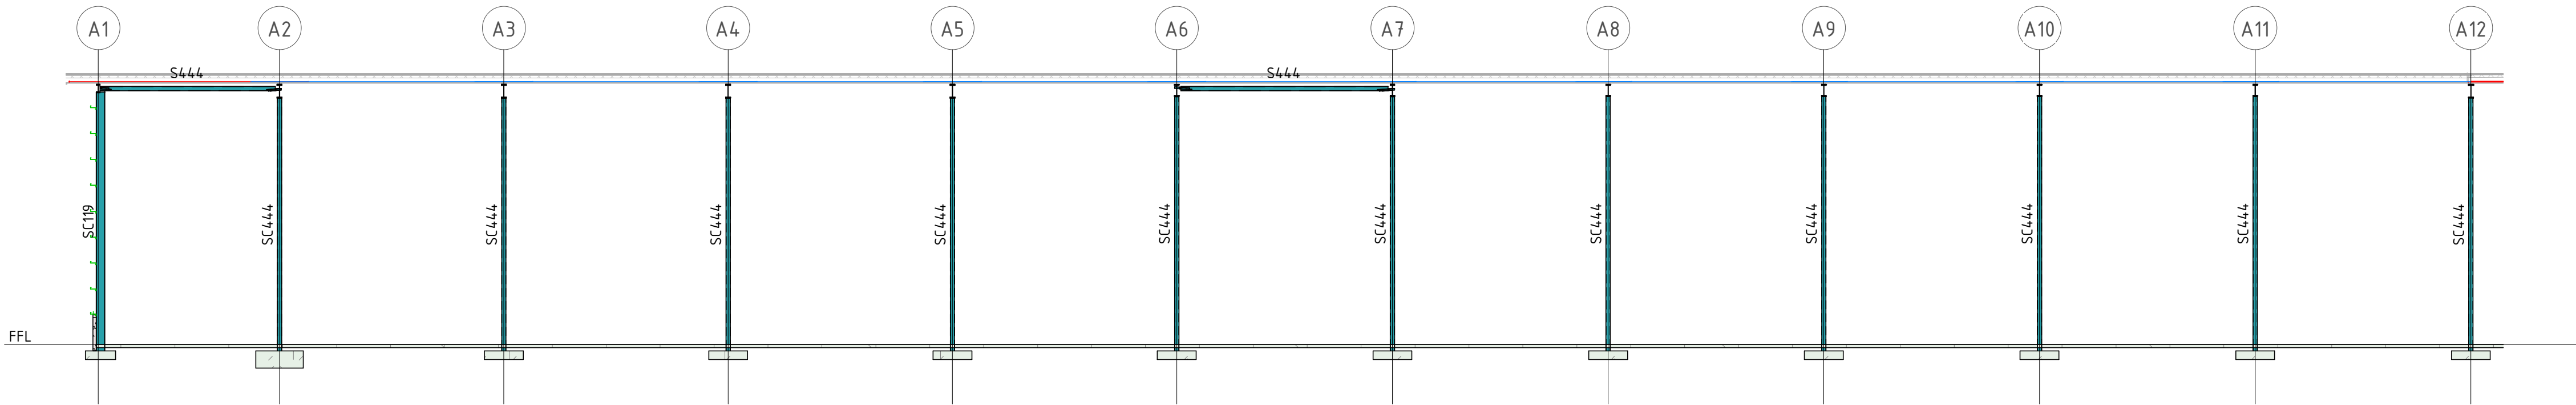


SECTION 2A
SCALE 1 : 200

ELEVATIONS AND SECTIONS NOTES

- REFER S0.001-S0.003 FOR CONSTRUCTION NOTES
- ALL PURLINS AND GIRTS TO BE STRAMIT EXACTA. ANY ALTERNATIVE TO BE APPROVED BY NORTHROP CONSULTING ENGINEERS PRIOR TO FABRICATION.
- REFER ARCHITECTURAL DRAWINGS FOR ALL ROOF PENETRATION LOCATIONS.
- THE EXACT LOCATION OF PENETRATION TRIMMING PURLIN AND GIRTS ARE TO CONFIRMED WITH SERVICE PROVIDER PRIOR TO FABRICATION.

ELEVATIONS AND SECTIONS LEGEND

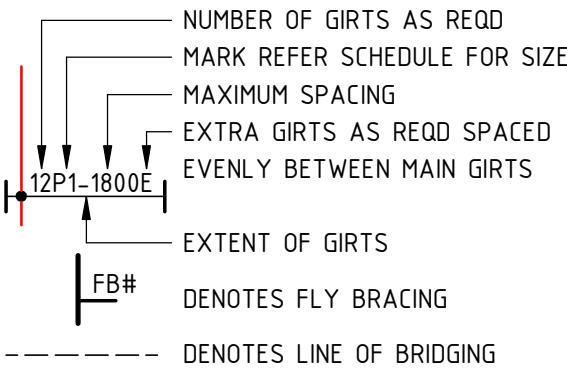

GIRT COLOURS

- REFER MEMBER SCHEDULE FOR SIZE MARKS
- 1.0mm C/Z GIRT THICKNESS
 - 1.2mm C/Z GIRT THICKNESS
 - 1.5mm C/Z GIRT THICKNESS
 - 1.9mm C/Z GIRT THICKNESS
 - 2.4mm C/Z GIRT THICKNESS
 - 3.0mm C/Z GIRT THICKNESS

GIRT LAPS

ALL GIRT LAPS TO BE 15% OF THE LARGEST ADJACENT SPAN UNLESS NOTED OTHERWISE

- 20% OF LARGEST ADJACENT SPAN
- 25% OF LARGEST ADJACENT SPAN
- 30% OF LARGEST ADJACENT SPAN
- 35% OF LARGEST ADJACENT SPAN

MEMBER SCHEDULE

MARK	SIZE
COLUMN	
SC119	410 UB 53.7
SC120	410 UB 59.7
SC124	530 UB 82.0
SC444	200 x 200 x 6.0 SHS
MULLION	
M308	250 PFC
BEAM	
B308	250 PFC
RAFTER	
R116	360 UB 44.7
R120	410 UB 59.7
R121	460 UB 67.1
R124	530 UB 82.0
R125	530 UB 92.4
R126	610 UB 101
RAKING ANGLE	
RA728	90 x 90 x 8 EA
ROOF BRACING	
RB725	75 x 75 x 8 EA
STRUT	
S440	150x150x5.0SHS
S444	200x200x6.0SHS
WALL BRACING	
WB725	75 x 75 x 8 EA
WALL HEAD	
WH433	100x100x5.0SHS
GIRT	
G914	EZ250-15
G915	EZ250-19
G946	EC250-24
PURLIN	
P914	EZ250-15
P915	EZ250-19
P916	EZ250-24
P946	EC250-24

NS	BAC APPROVAL	11.06.26	C
NS	STEEL DETAILS ISSUE	04.06.26	B
NS	PRELIM STEEL ISSUE	29.05.26	A
DRN	AMENDMENTS	DATE	REV

NORTHROP
PROJECT NUMBER: 250946

Drawn: HP	Checked:
Design Coordinated: HP	Compliance Checked: --
Authorised For Issue: NS	Construction Checked: --

SKYGATE PLAY
BUILDING SECTIONS - SHEET 1

 Brisbane Airport	BRISBANE AIRPORT CORPORATION PTY LTD 11 THE CIRCUIT, BRISBANE AIRPORT, QLD 4008, AUSTRALIA PO BOX 61, HAMILTON CENTRAL, QLD 4007, AUSTRALIA T: +61 7 3406 3000 E: INFO@BNE.COM.AU W: BNE.COM.AU							Scale: As indicated
								Size: A1
								Revision: C
Drawing Number	Project No	Originator	Volume	Level	Type	Discipline	Number	
	25021	- NOR	- XX	- 01	- DR	- ST	- 006501	
Plot Date & Time:								11/06/2025 09:50 AM