




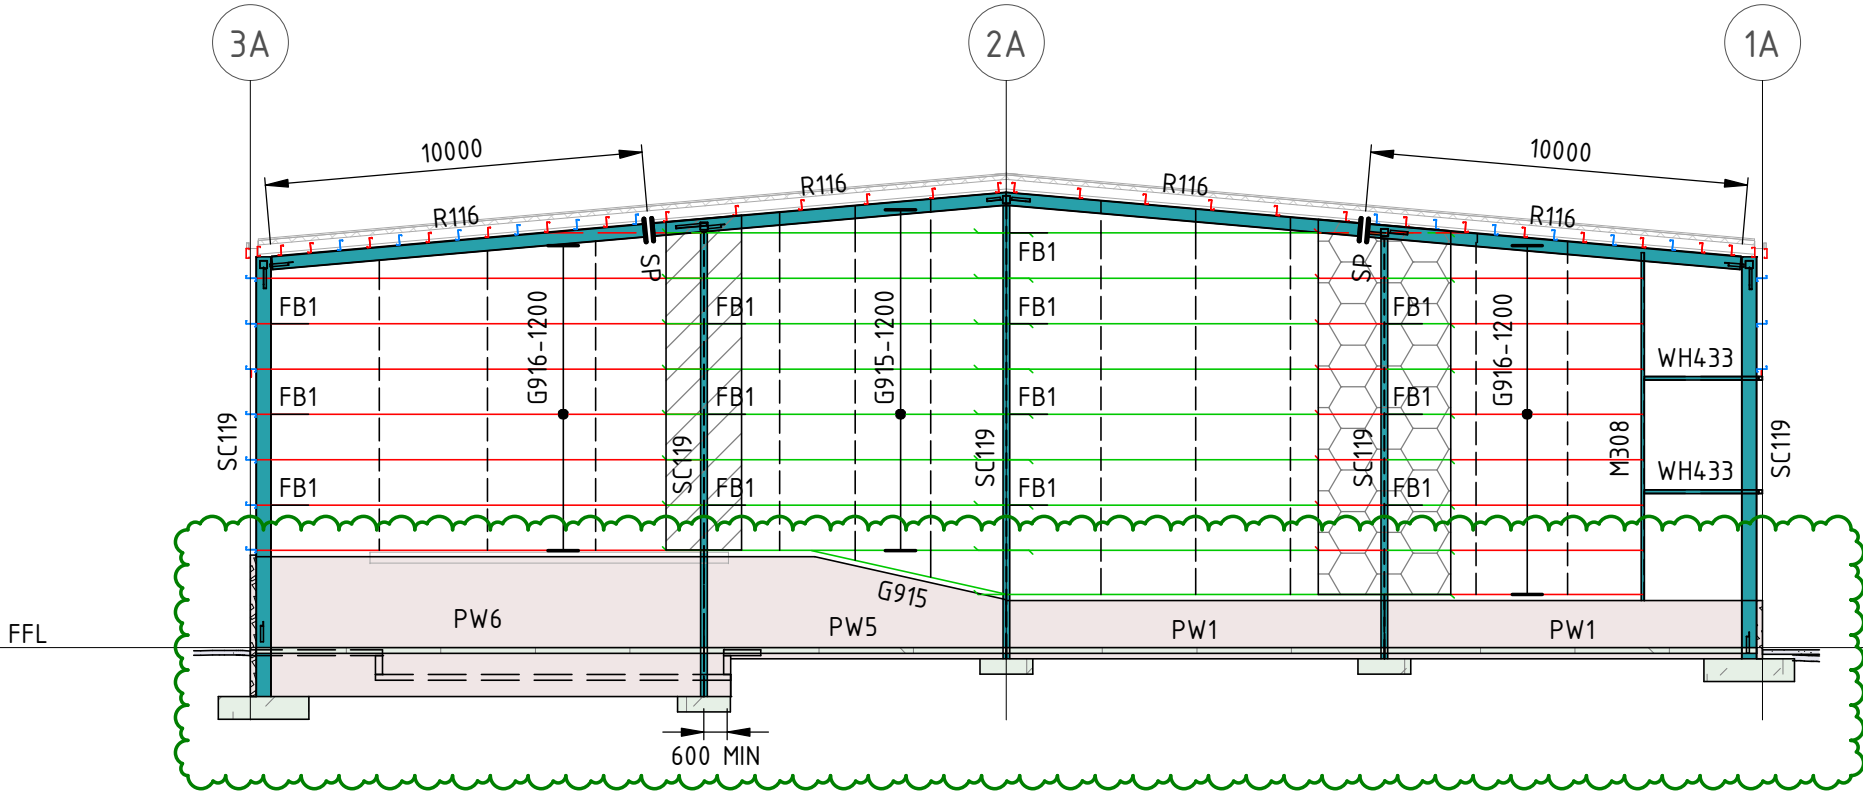


SECTION A1
SCALE 1 : 200

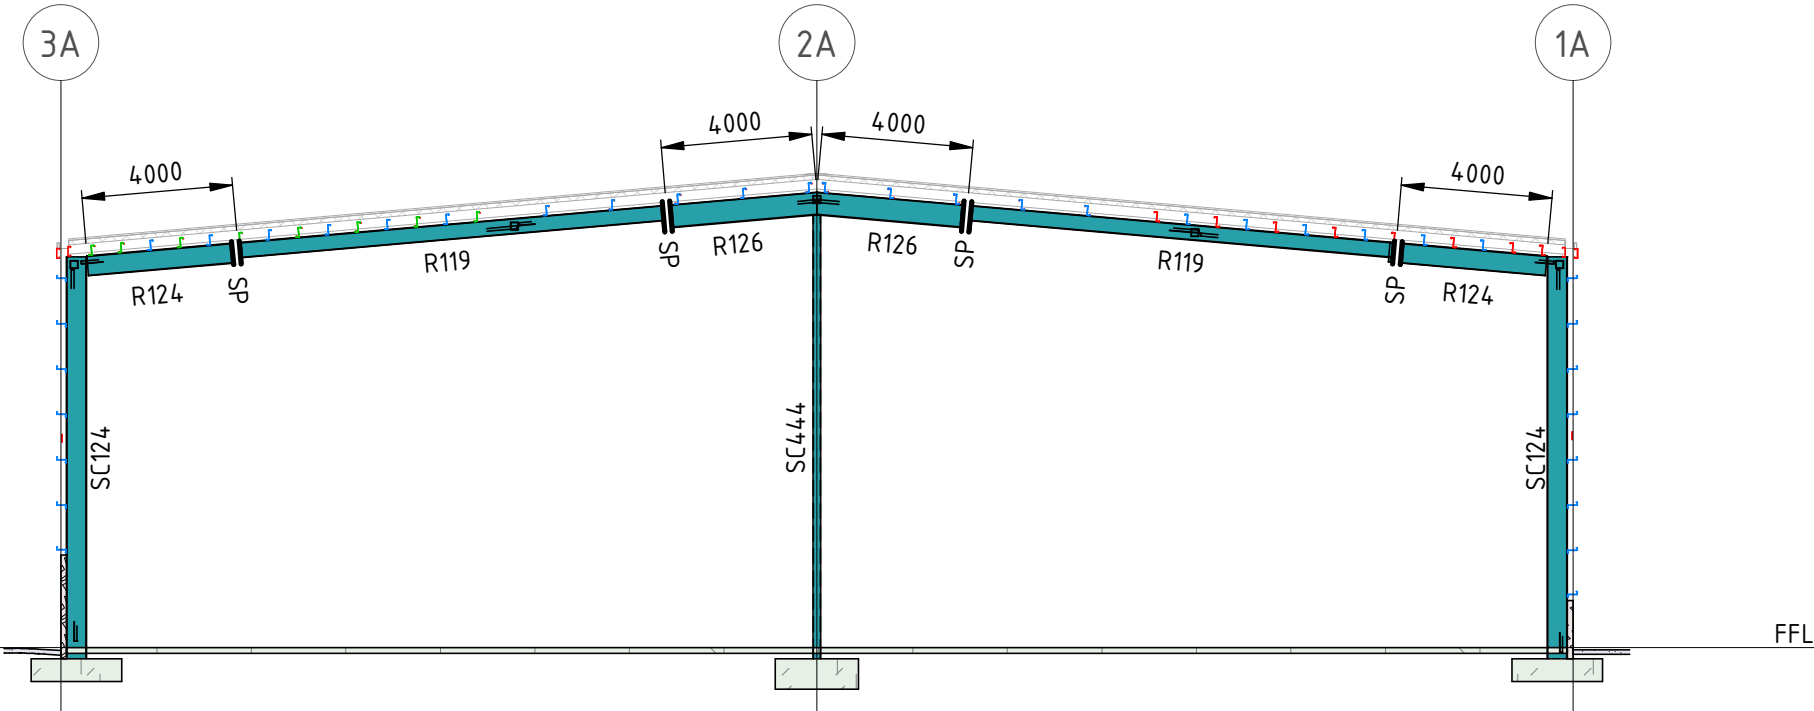


SECTION A2
SCALE 1 : 200

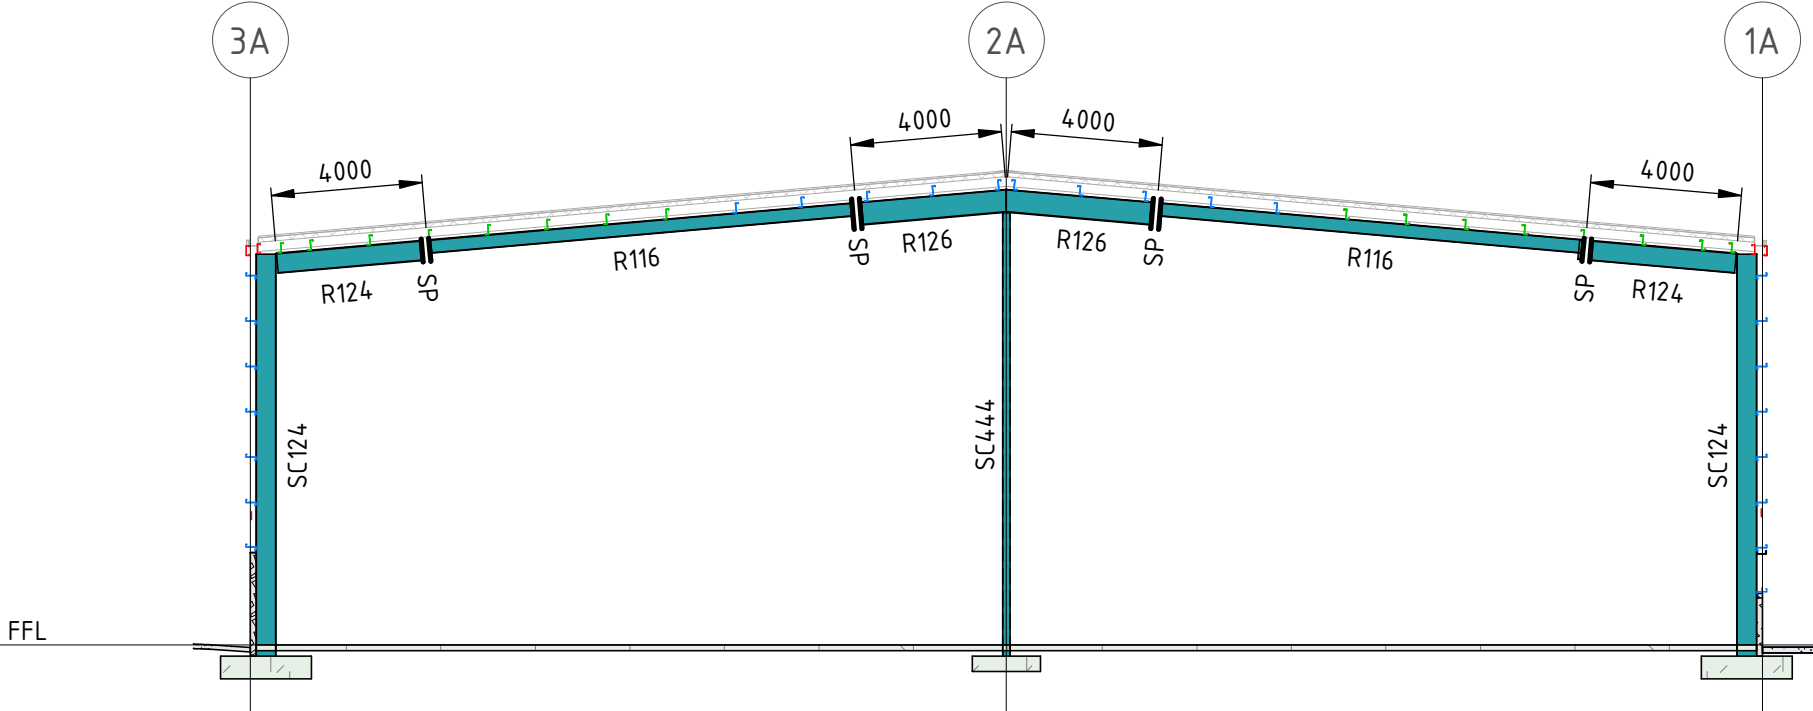


SECTION A3
SCALE 1 : 200

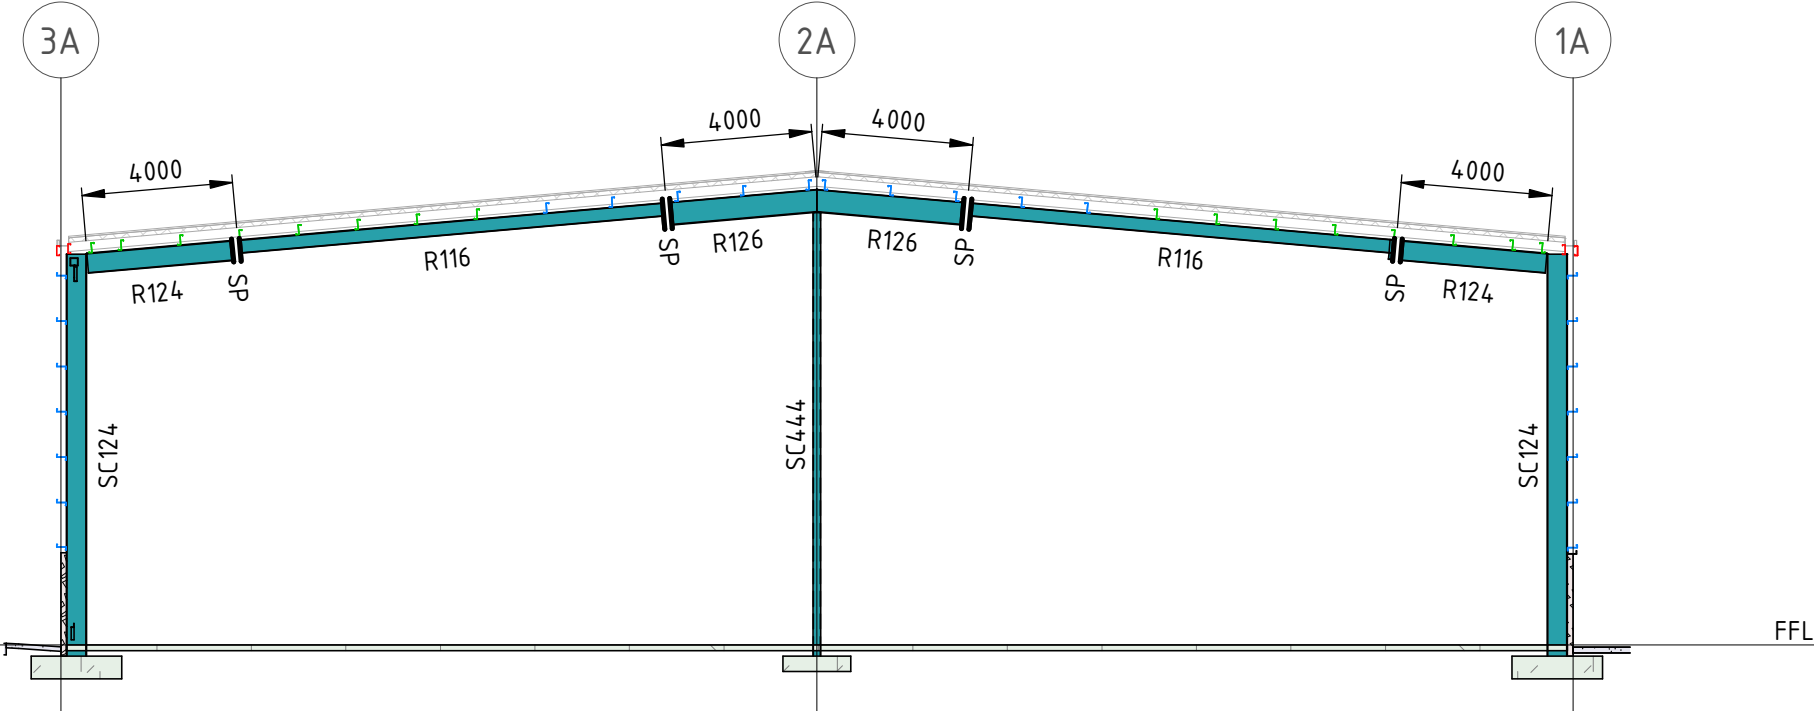


SECTION A4
SCALE 1 : 200

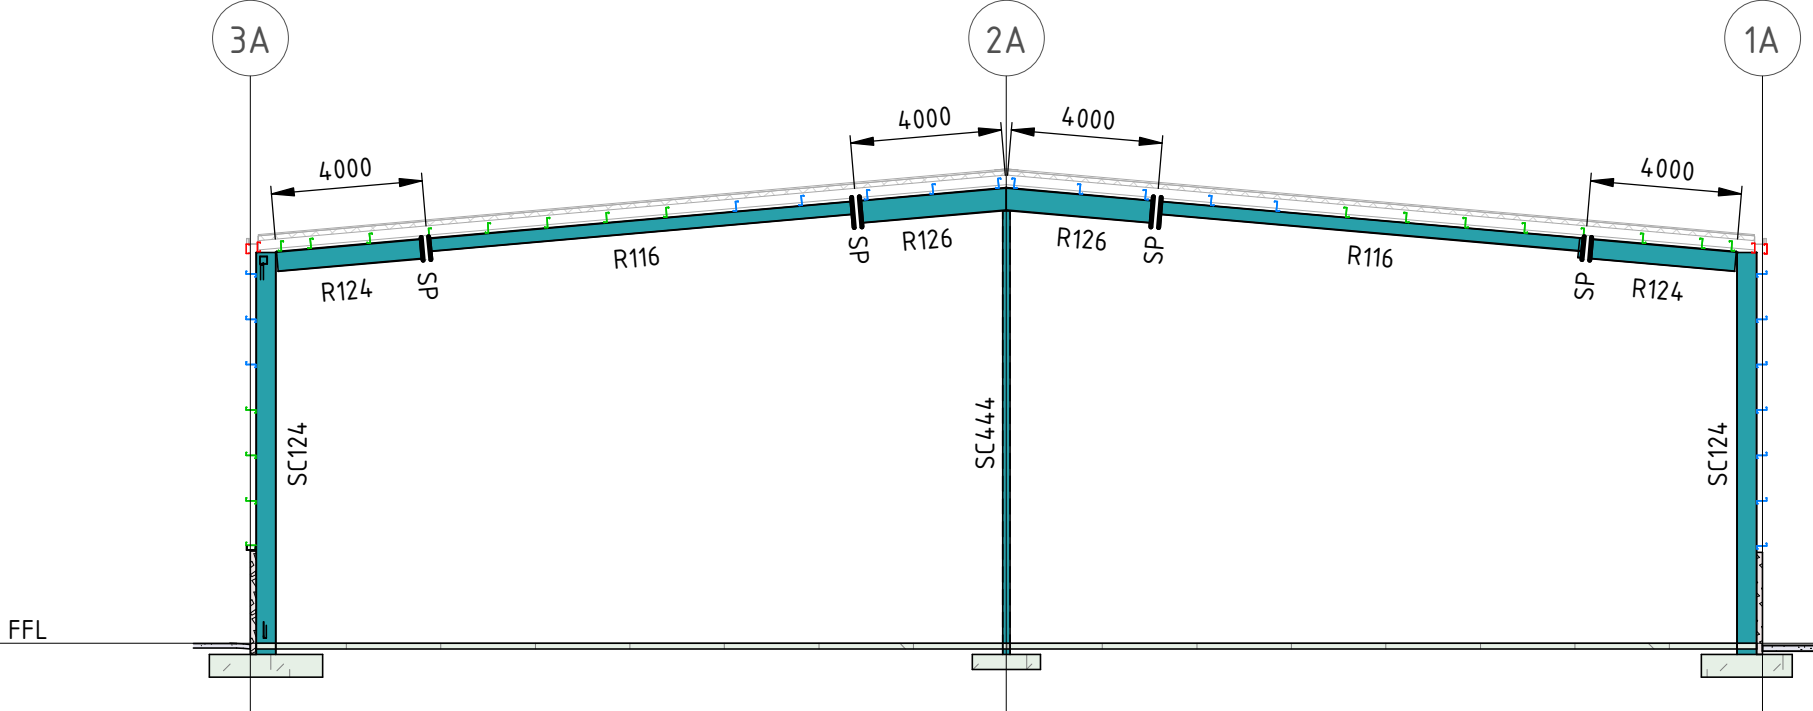


SECTION A5
SCALE 1 : 200

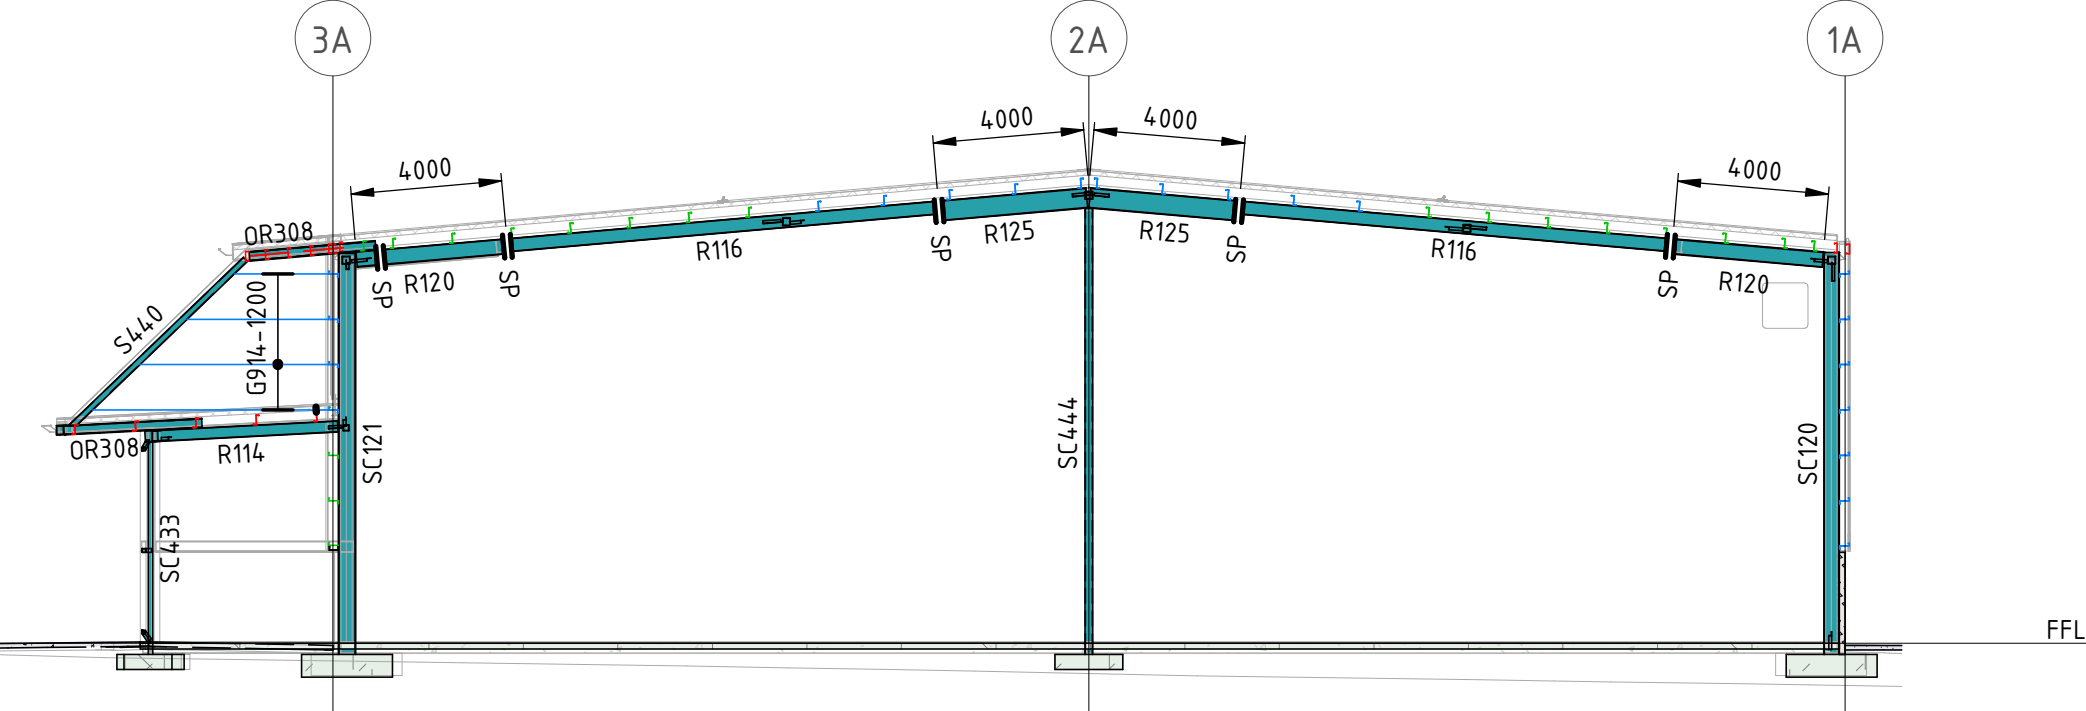

SECTION A6
SCALE 1 : 200

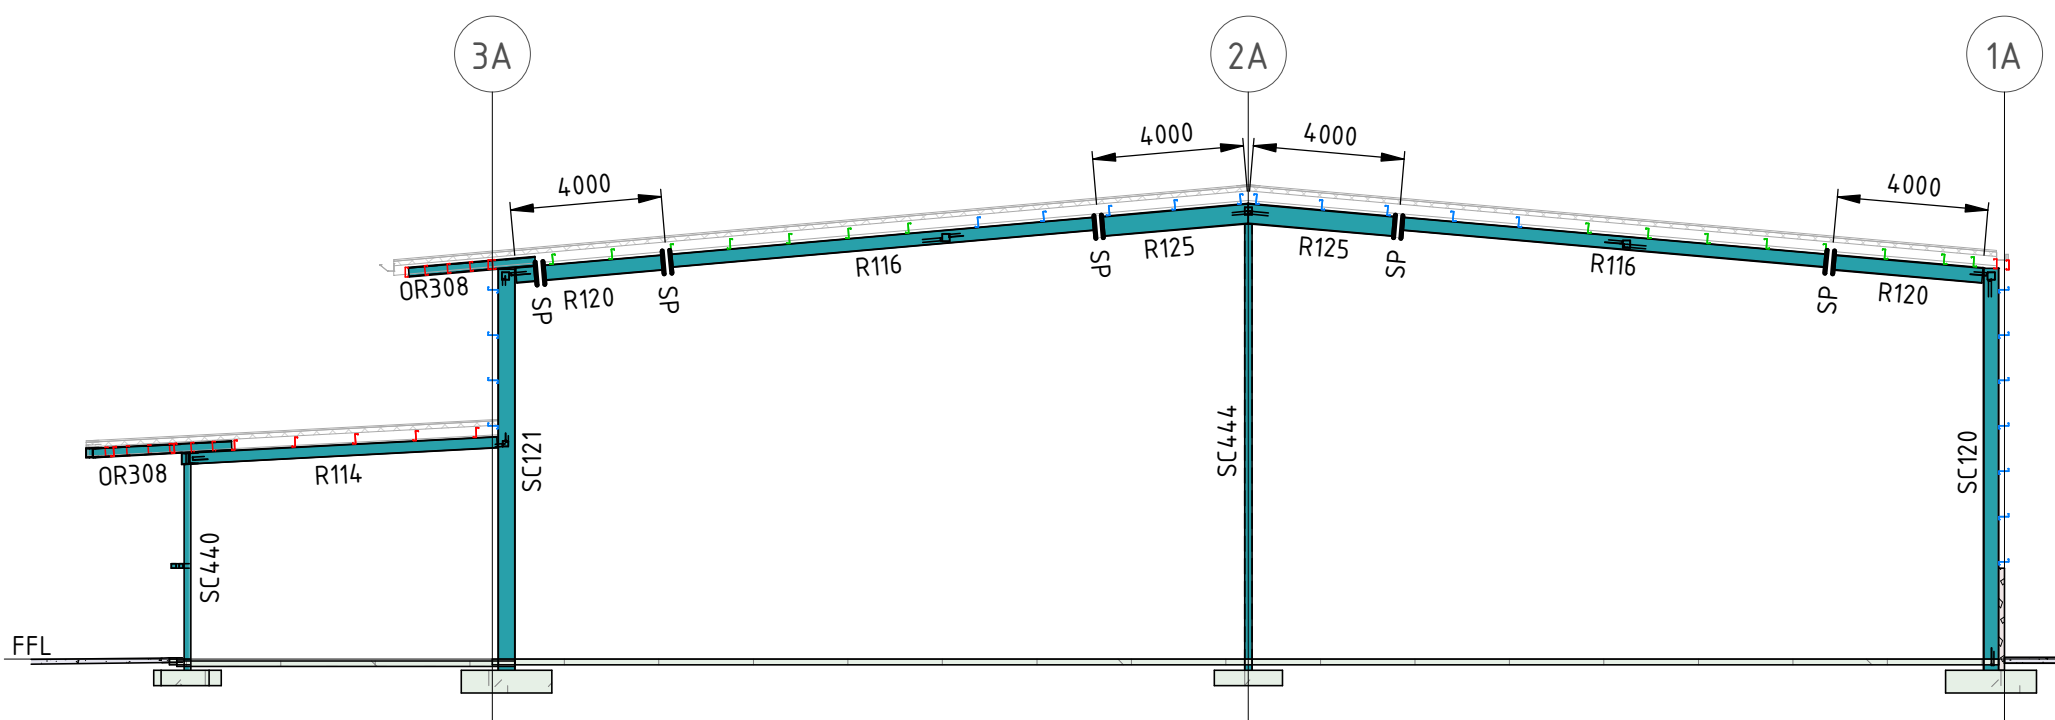

SECTION A7
SCALE 1 : 200

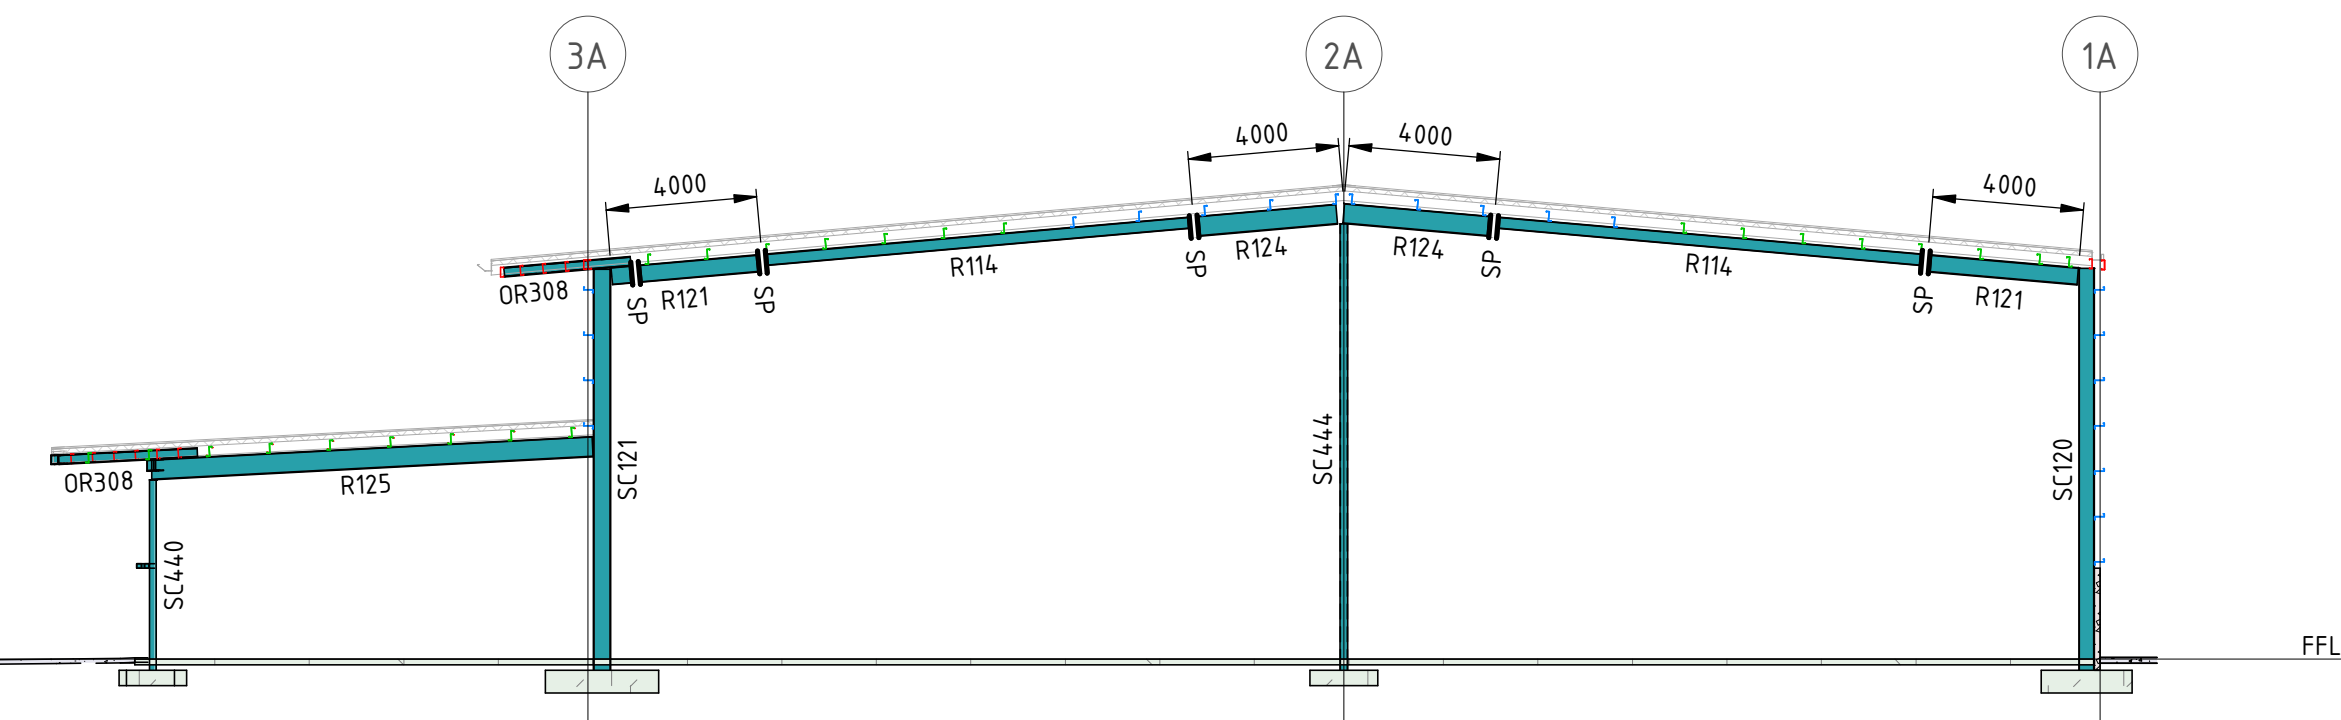


SECTION A8
SCALE 1 : 200

ELEVATIONS AND SECTIONS NOTES

- REFER S0.001-S0.003 FOR CONSTRUCTION NOTES
- ALL PURLINS AND GIRTS TO BE STRAIT EXACTA. ANY ALTERNATIVE TO BE APPROVED BY NORTHROP CONSULTING ENGINEERS PRIOR TO FABRICATION.
- REFER ARCHITECTURAL DRAWINGS FOR ALL ROOF PENETRATION LOCATIONS.
- THE EXACT LOCATION OF PENETRATION TRIMMING PURLIN AND GIRTS ARE TO BE CONFIRMED WITH SERVICE PROVIDER PRIOR TO FABRICATION.

ELEVATIONS AND SECTIONS LEGEND

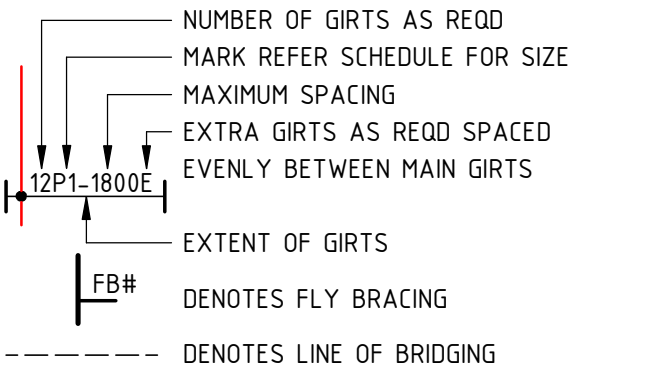

GIRT COLOURS

- REFER MEMBER SCHEDULE FOR SIZE MARKS
- 1.0mm C/Z GIRT THICKNESS
 - 1.2mm C/Z GIRT THICKNESS
 - 1.5mm C/Z GIRT THICKNESS
 - 1.9mm C/Z GIRT THICKNESS
 - 2.4mm C/Z GIRT THICKNESS
 - 3.0mm C/Z GIRT THICKNESS

GIRT LAPS

ALL GIRT LAPS TO BE 15% OF THE LARGEST ADJACENT SPAN UNLESS NOTED OTHERWISE

- DENOTES GIRT LAPS TO BE 20% OF LARGEST ADJACENT SPAN
- DENOTES GIRT LAPS TO BE 25% OF LARGEST ADJACENT SPAN
- DENOTES GIRT LAPS TO BE 30% OF LARGEST ADJACENT SPAN
- DENOTES GIRT LAPS TO BE 35% OF LARGEST ADJACENT SPAN

MEMBER SCHEDULE

MARK	SIZE
COLUMN	
SC119	410 UB 53.7
SC120	410 UB 59.7
SC121	460 UB 67.1
SC124	530 UB 82.0
SC433	100 x 100 x 5.0 SHS
SC440	150 x 150 x 5.0 SHS
SC444	200 x 200 x 6.0 SHS
MULLION	
M308	250 PFC
BEAM	
B308	250 PFC
B309	300 PFC
OUTRIGGER	
OR308	250 PFC
RAFTER	
R114	310 UB 40.4
R116	360 UB 44.7
R119	410 UB 53.7
R120	410 UB 59.7
R121	460 UB 67.1
R124	530 UB 82.0
R125	530 UB 92.4
R126	610 UB 101
ROOF BRACING	
RB725	75 x 75 x 8 EA
STRUT	
S440	150x150x5.0SHS
S444	200x200x6.0SHS
WALL BRACING	
WB430	89x89x6.0SHS
WB725	75 x 75 x 8 EA
WALL HEAD	
WH433	100x100x5.0SHS
WH437	125x125x5.0SHS
GIRT	
G914	EZ250-15
G915	EZ250-19
G916	EZ250-24
G946	EC250-24
PURLIN	
P914	EZ250-15
P915	EZ250-19
P916	EZ250-24
P946	EC250-24