


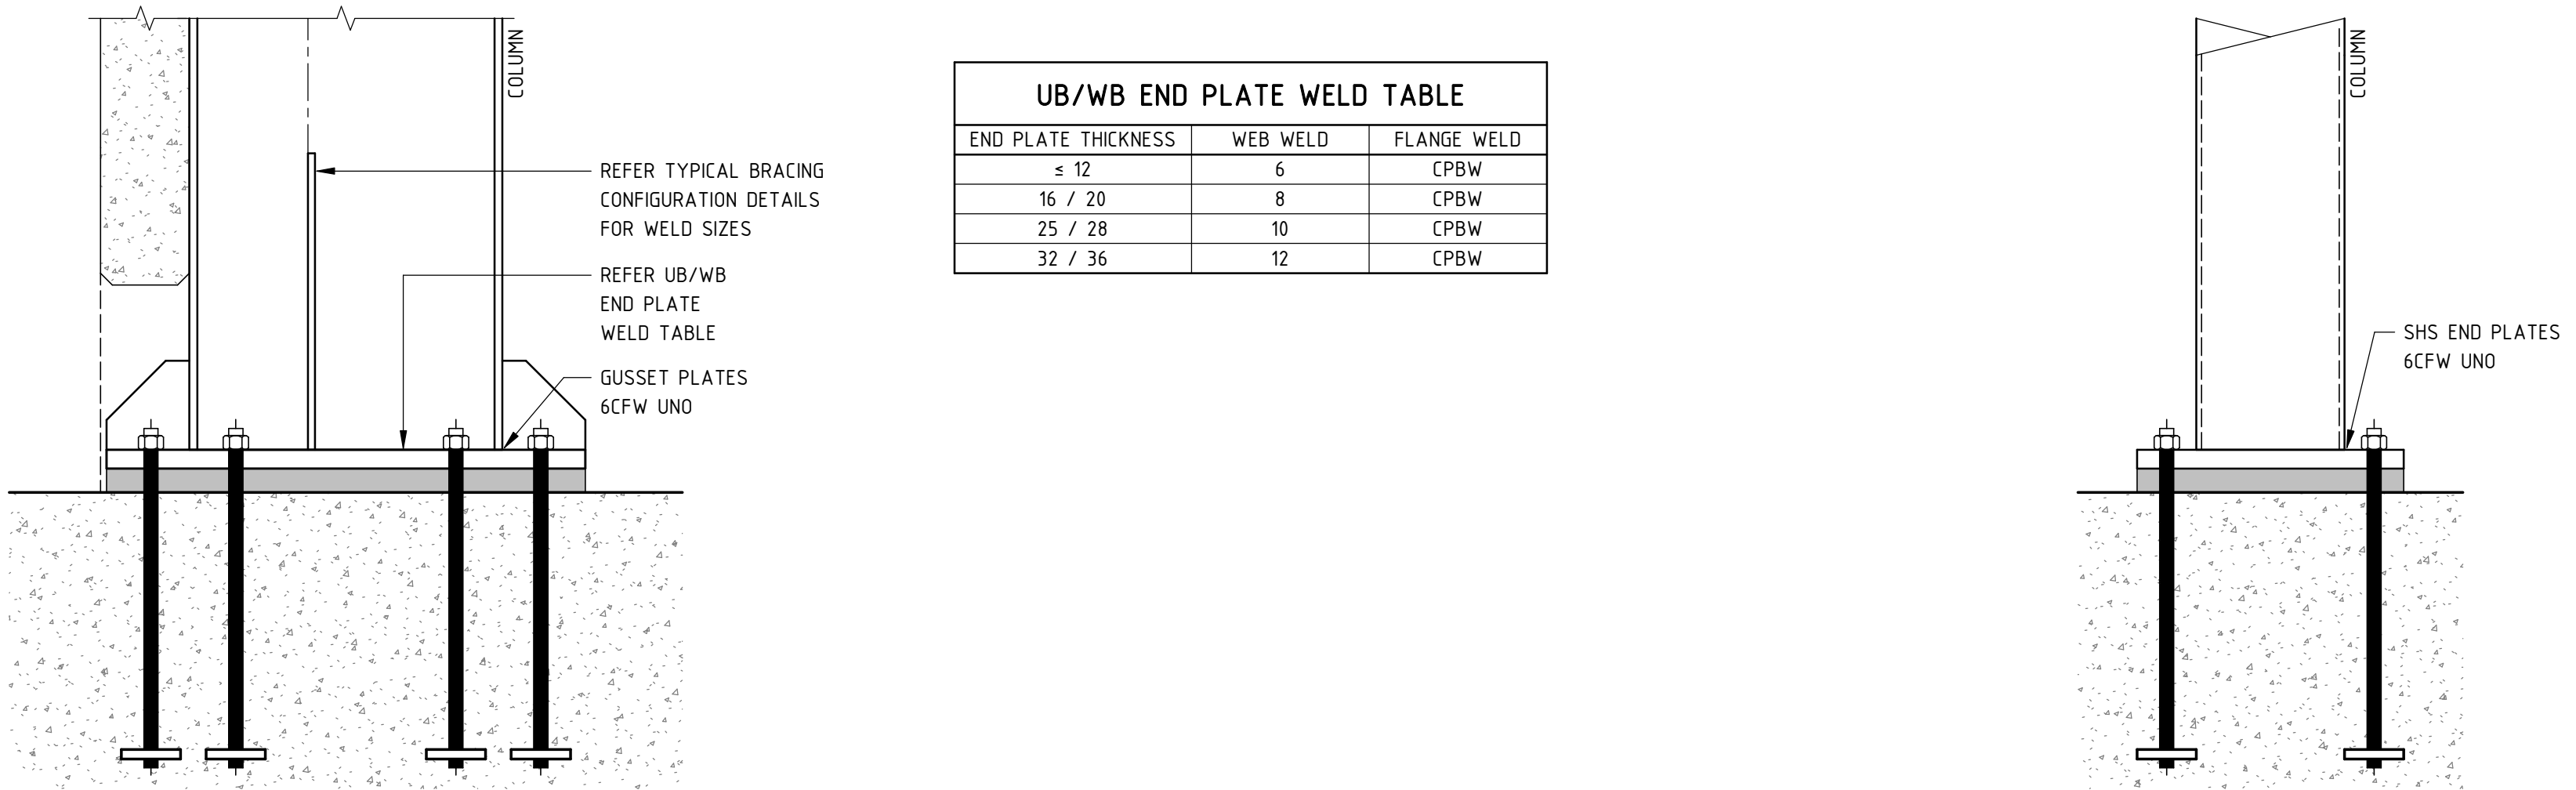

NOTE:
ALL WELD SIZES TO BE EQUAL TO THICKNESS OF STEEL SECTION UNLESS NOTED OTHERWISE.
WELD MAP TO BE USED FOR STEEL FRAMING CONNECTION DETAILING.
REFER TO TYPICAL BRACING DETAILS FOR WELDS OF BRACING MEMBER CONNECTIONS.