



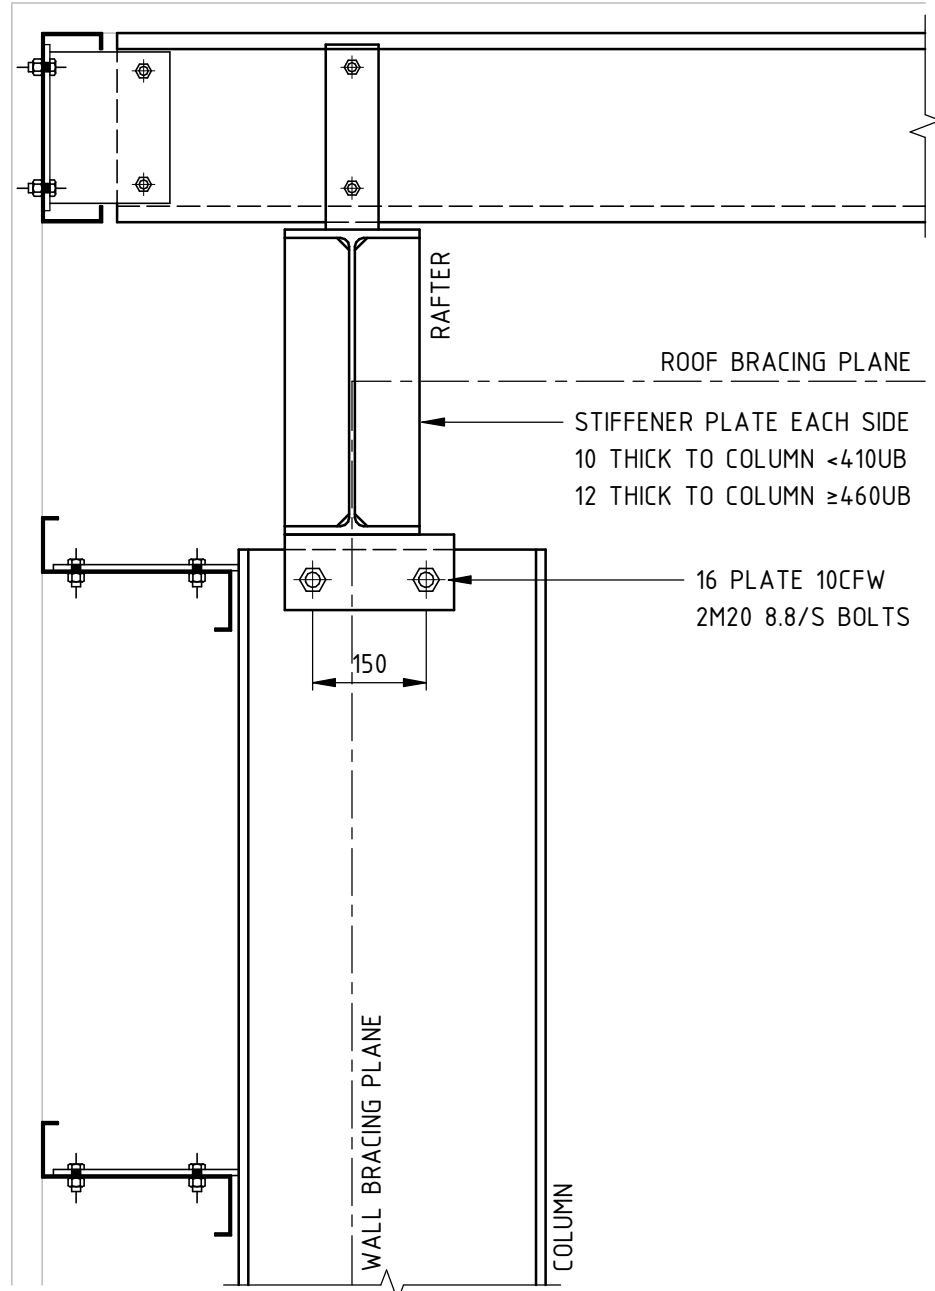


TYPICAL END WALL COLUMN TO RAFTER DETAIL

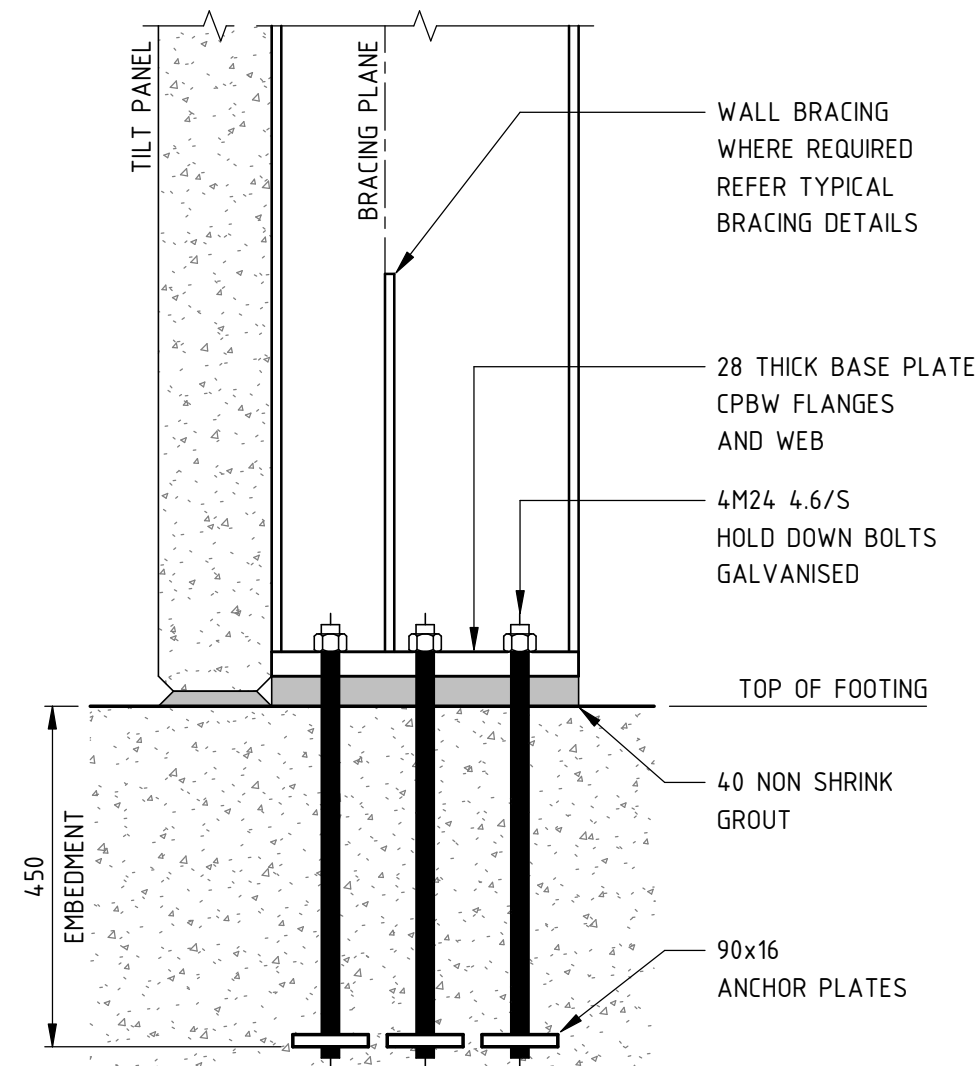


TYPICAL END WALL COLUMN BASE PLATE DETAIL


TYPICAL END WALL COLUMN AND RAFTER DETAIL

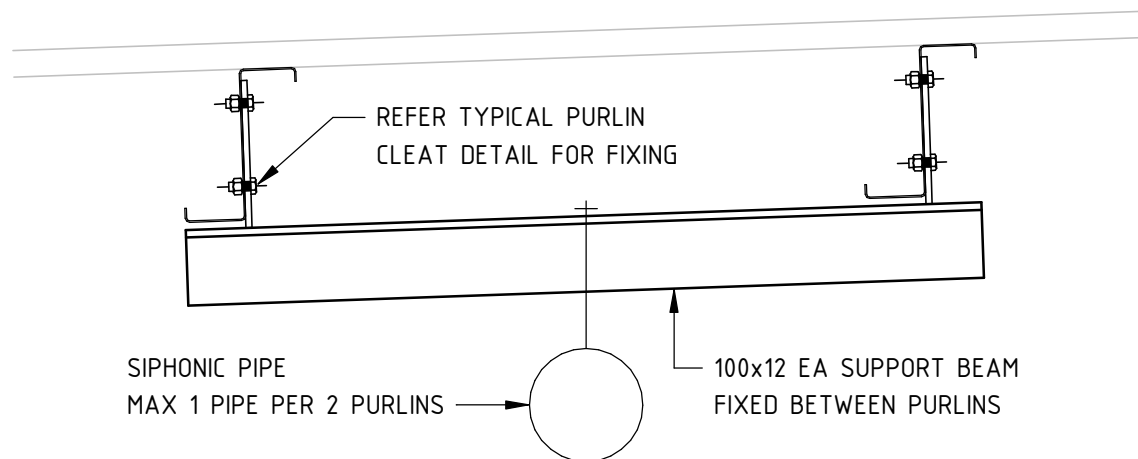


TYPICAL SIPHONIC PIPE SUPPORT FRAME DETAIL

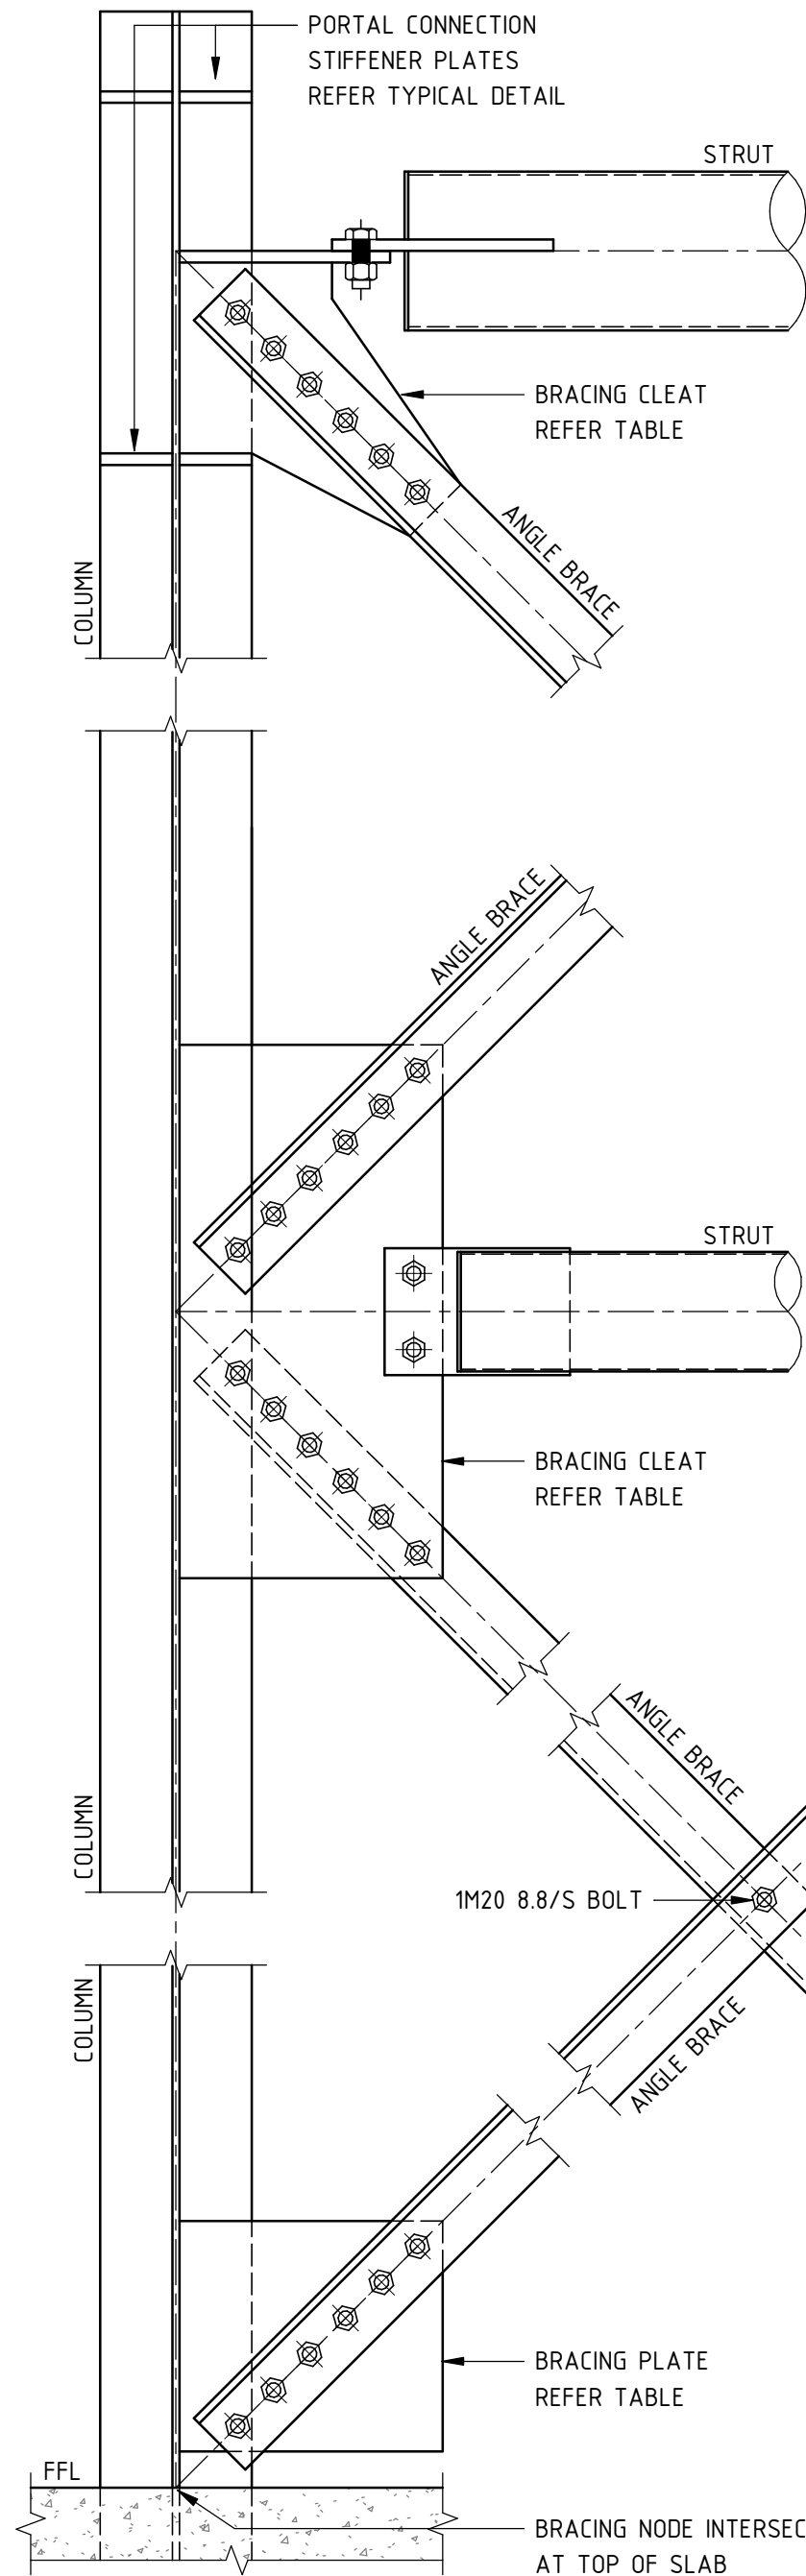

TYPICAL WALL BRACING CONFIGURATIONS
COLUMN FLANGE REMOVED FOR CLARITY

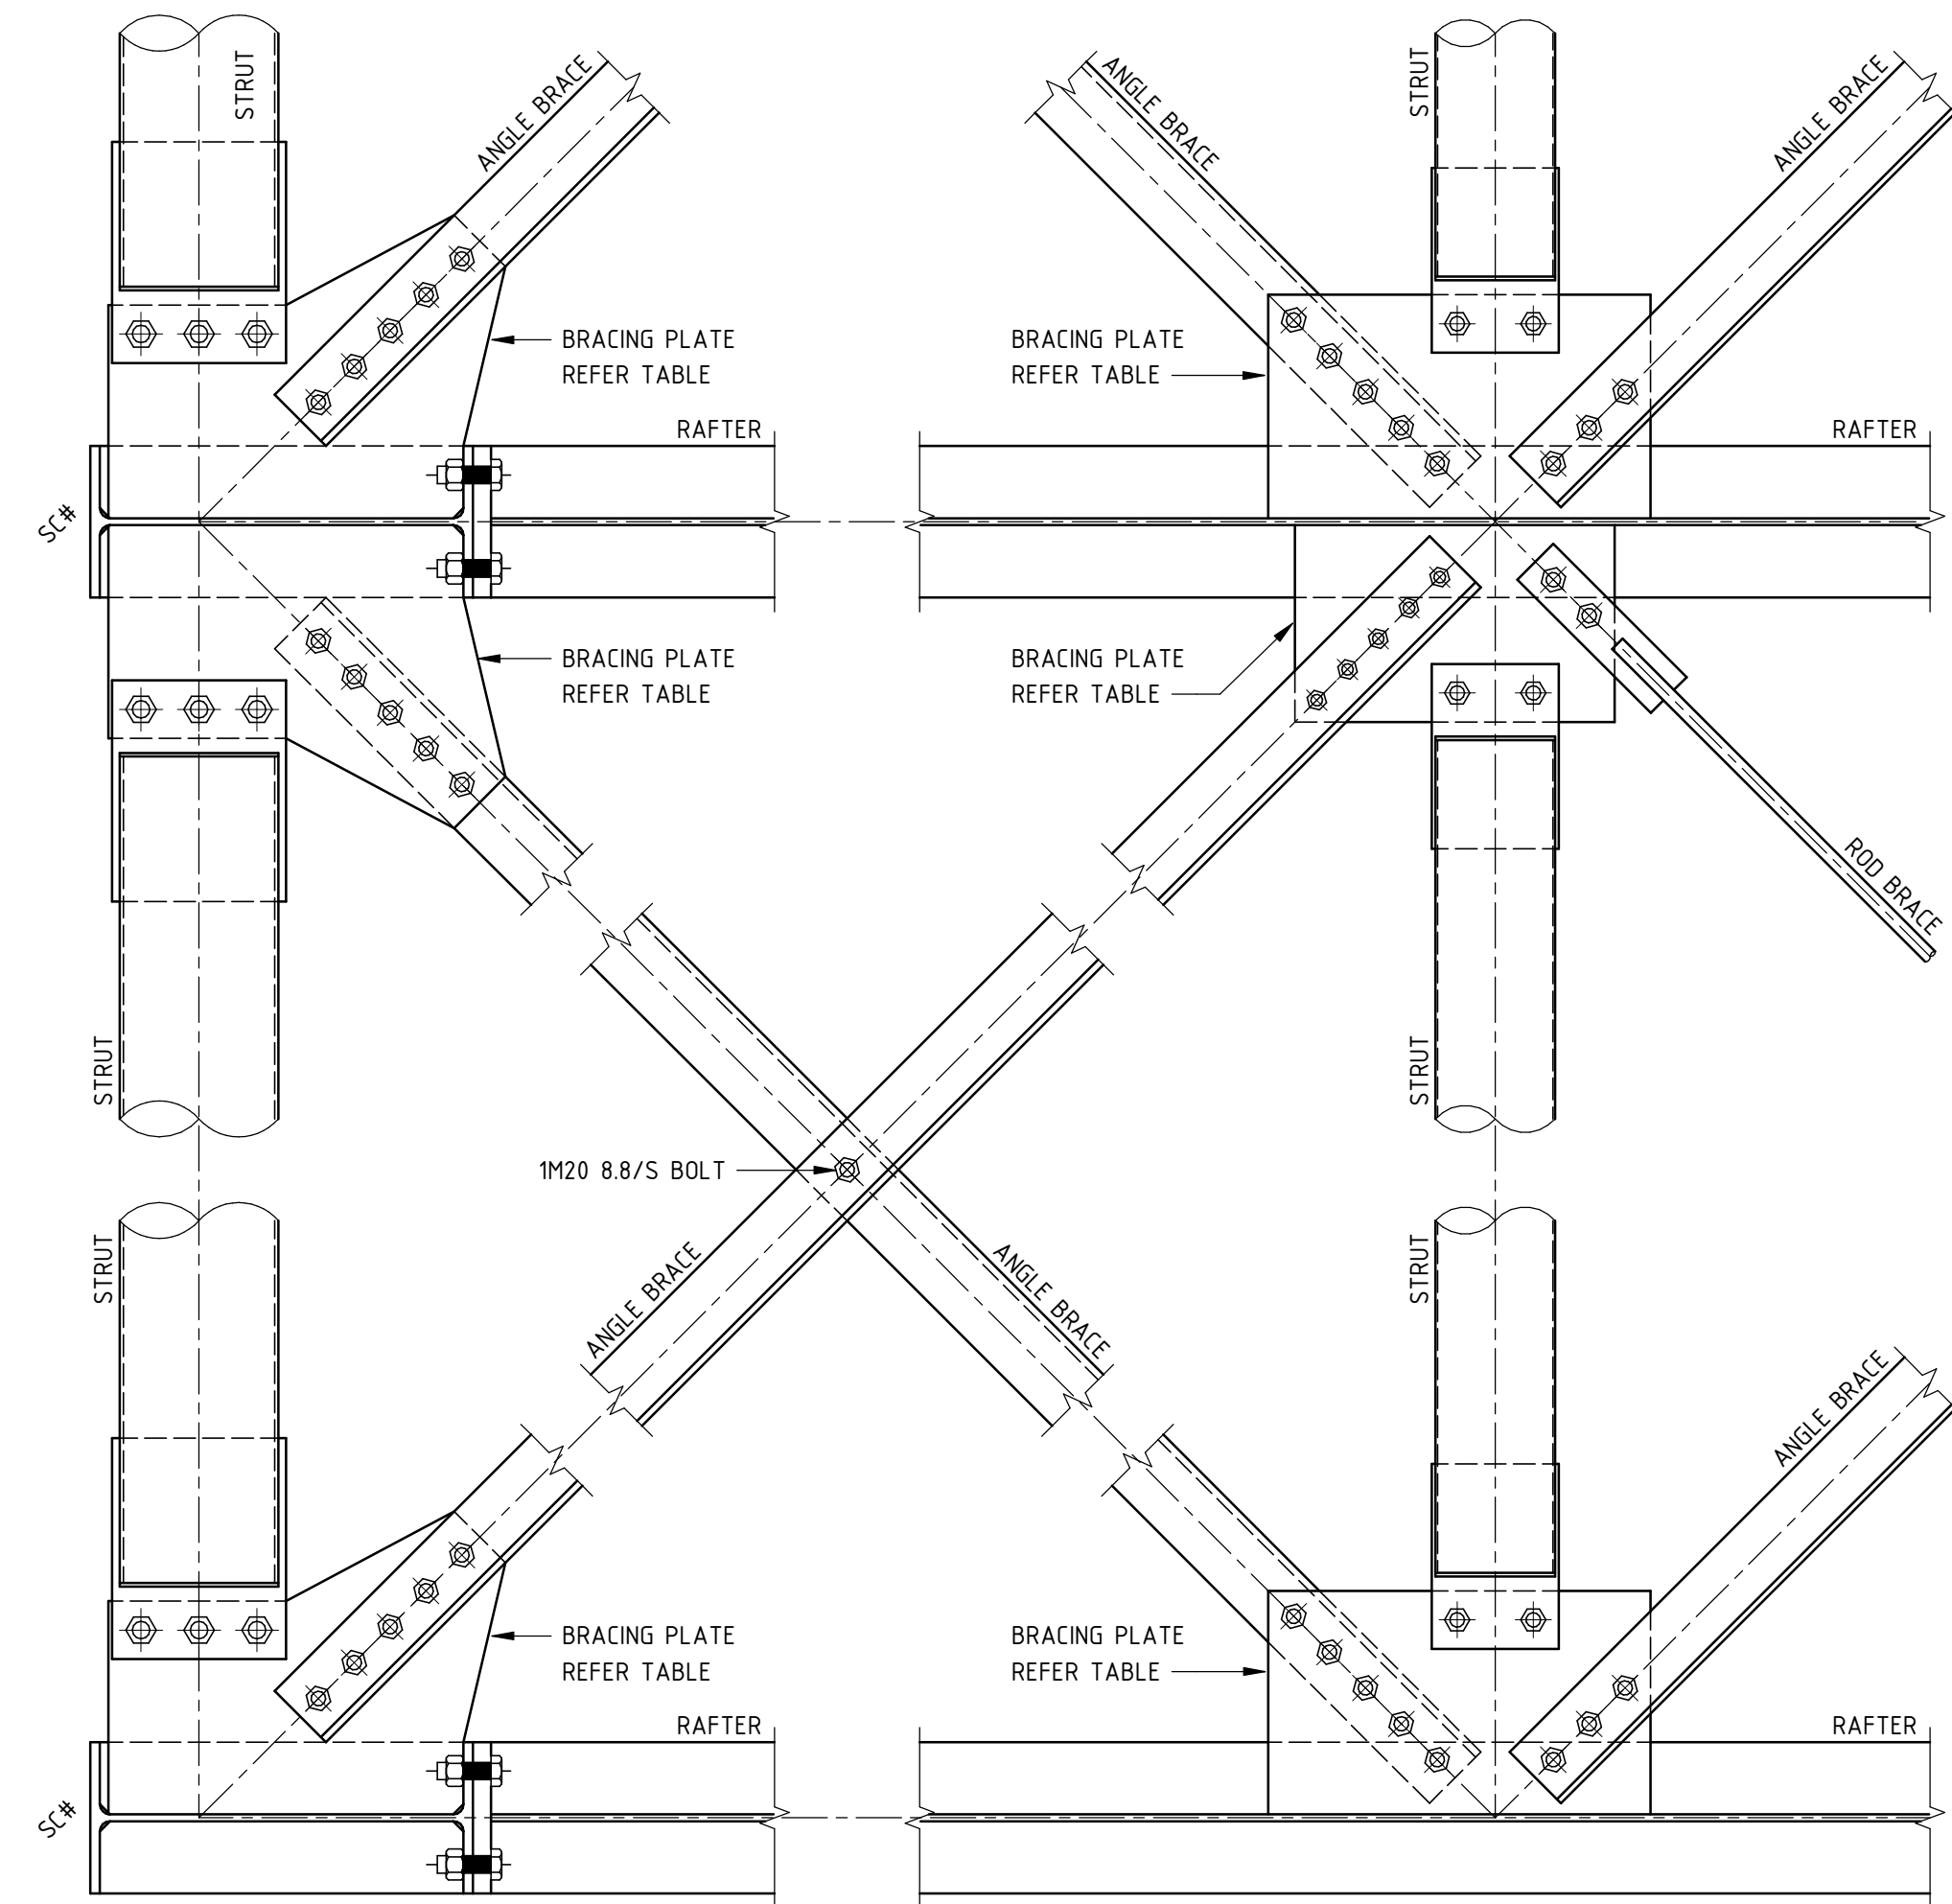


TYPICAL ROOF BRACING CONFIGURATIONS
RAFTER TOP FLANGE REMOVED FOR CLARITY

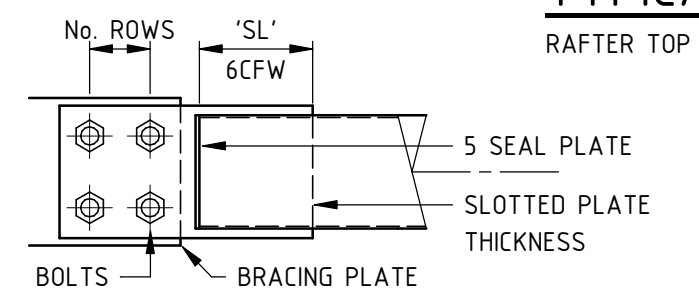


SHS STRUT/WALL BRACE TABLE					
MEMBER	BOLTS 8.8/S	No. ROWS	SLOTTED PLATE	BRACING PLATE	'SL' WELD LENGTH
200 SHS	4M24	2	16	16	320
150 SHS	2M24	1	12	12	120
89 SHS	2M20	2	16	16	140

NOTE: USE THICKER BRACING PLATE AT BRACING INTERSECTIONS

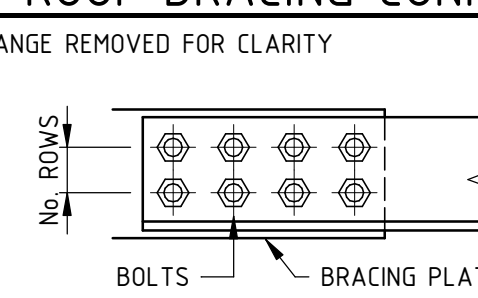


ANGLE BRACING TABLE			
MEMBER	BOLTS 8.8/S	No. ROWS	BRACING PLATE
75 x 8	4M20	1	16


NOTE: USE THICKER BRACING CLEAT AT BRACING INTERSECTIONS

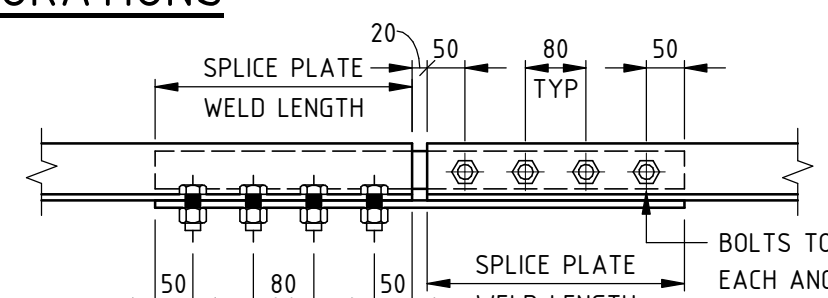


ANGLE SPLICE TABLE				
MEMBER	BOLTS 8.8/S	SPLICE PLATE		
		THICKNESS	WELD CFW	WELD LENGTH
75 EA	4M20	16	6	190

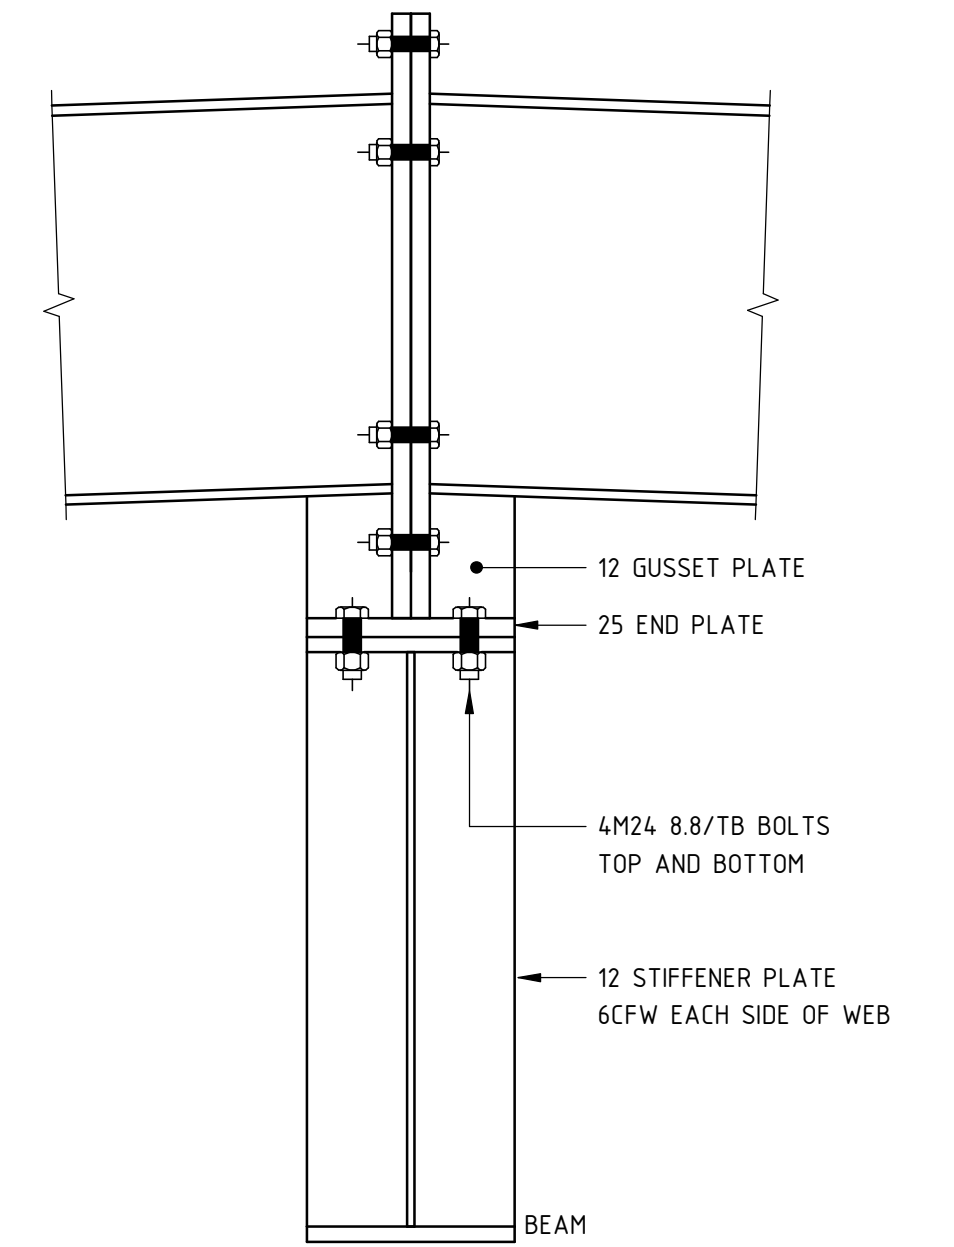


TYPICAL TRANSFER BEAM
SUPPORT CONNECTION DETAIL

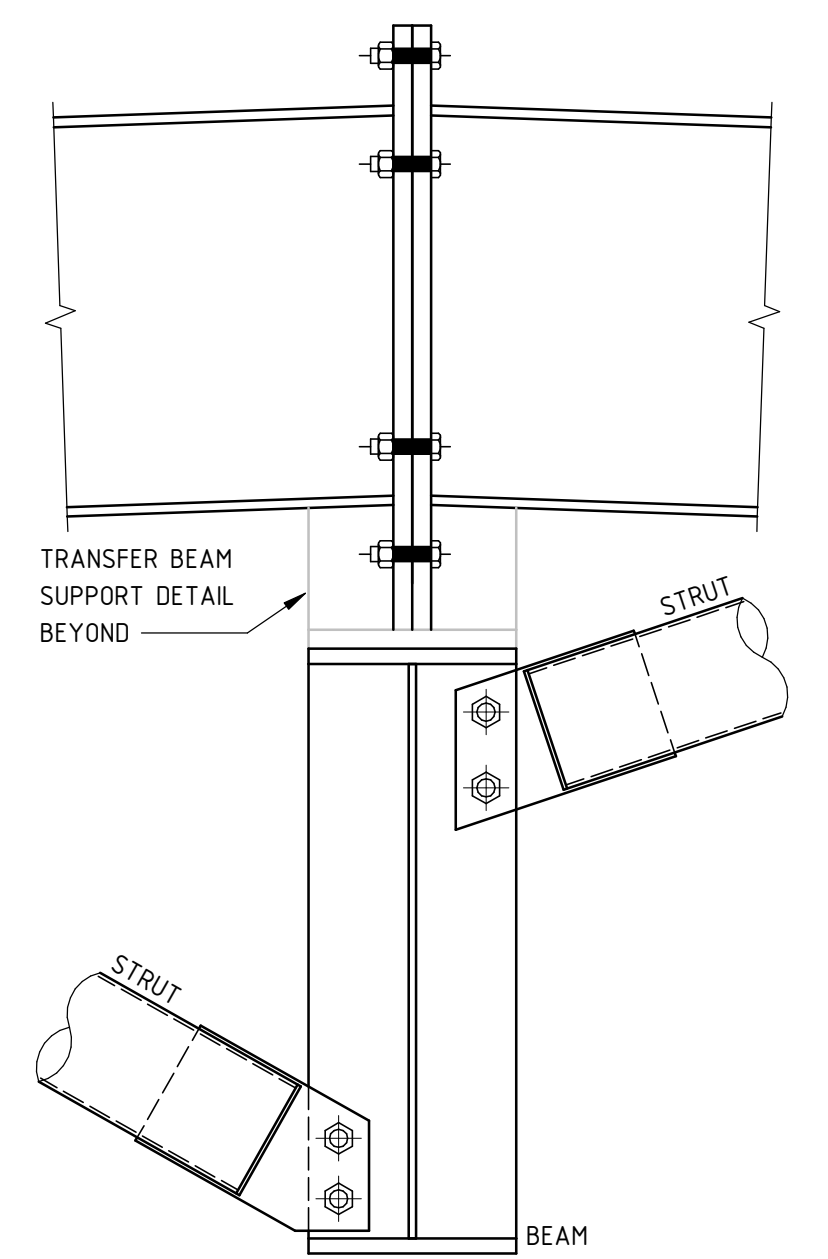


(Z)

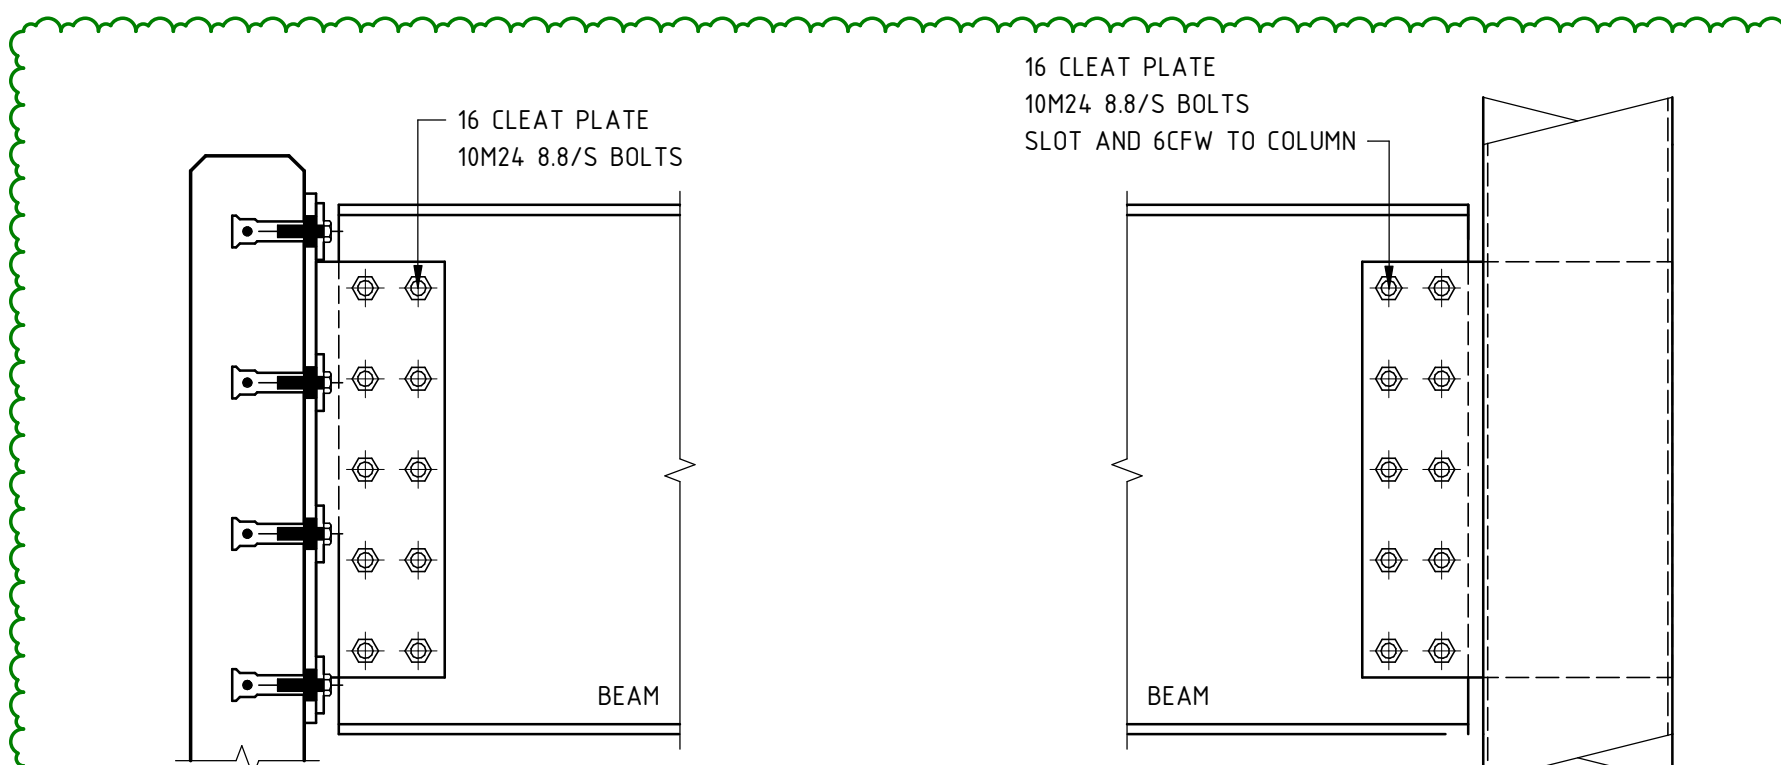

TYPICAL TRANSFER BEAM TO
PRECAST CONNECTION DETAIL

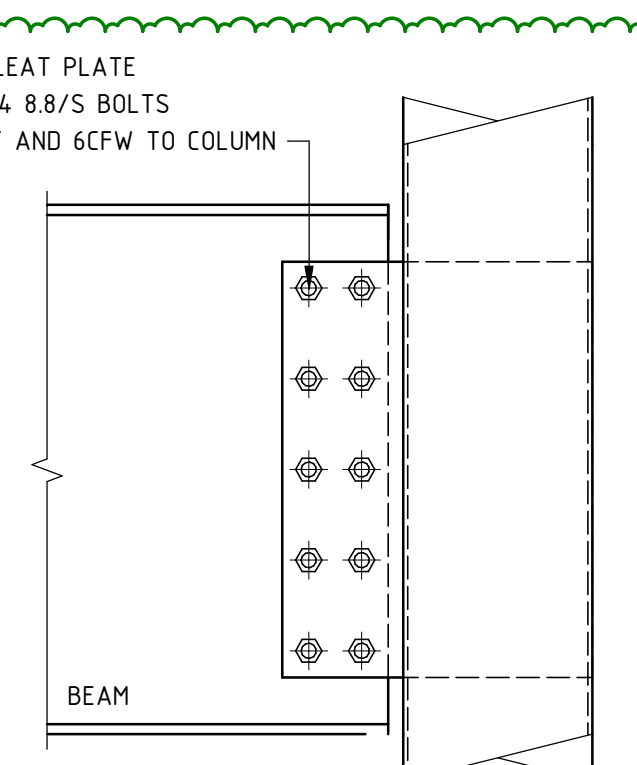

TYPICAL TRANSFER BEAM TO
COLUMN CONNECTION DETAIL

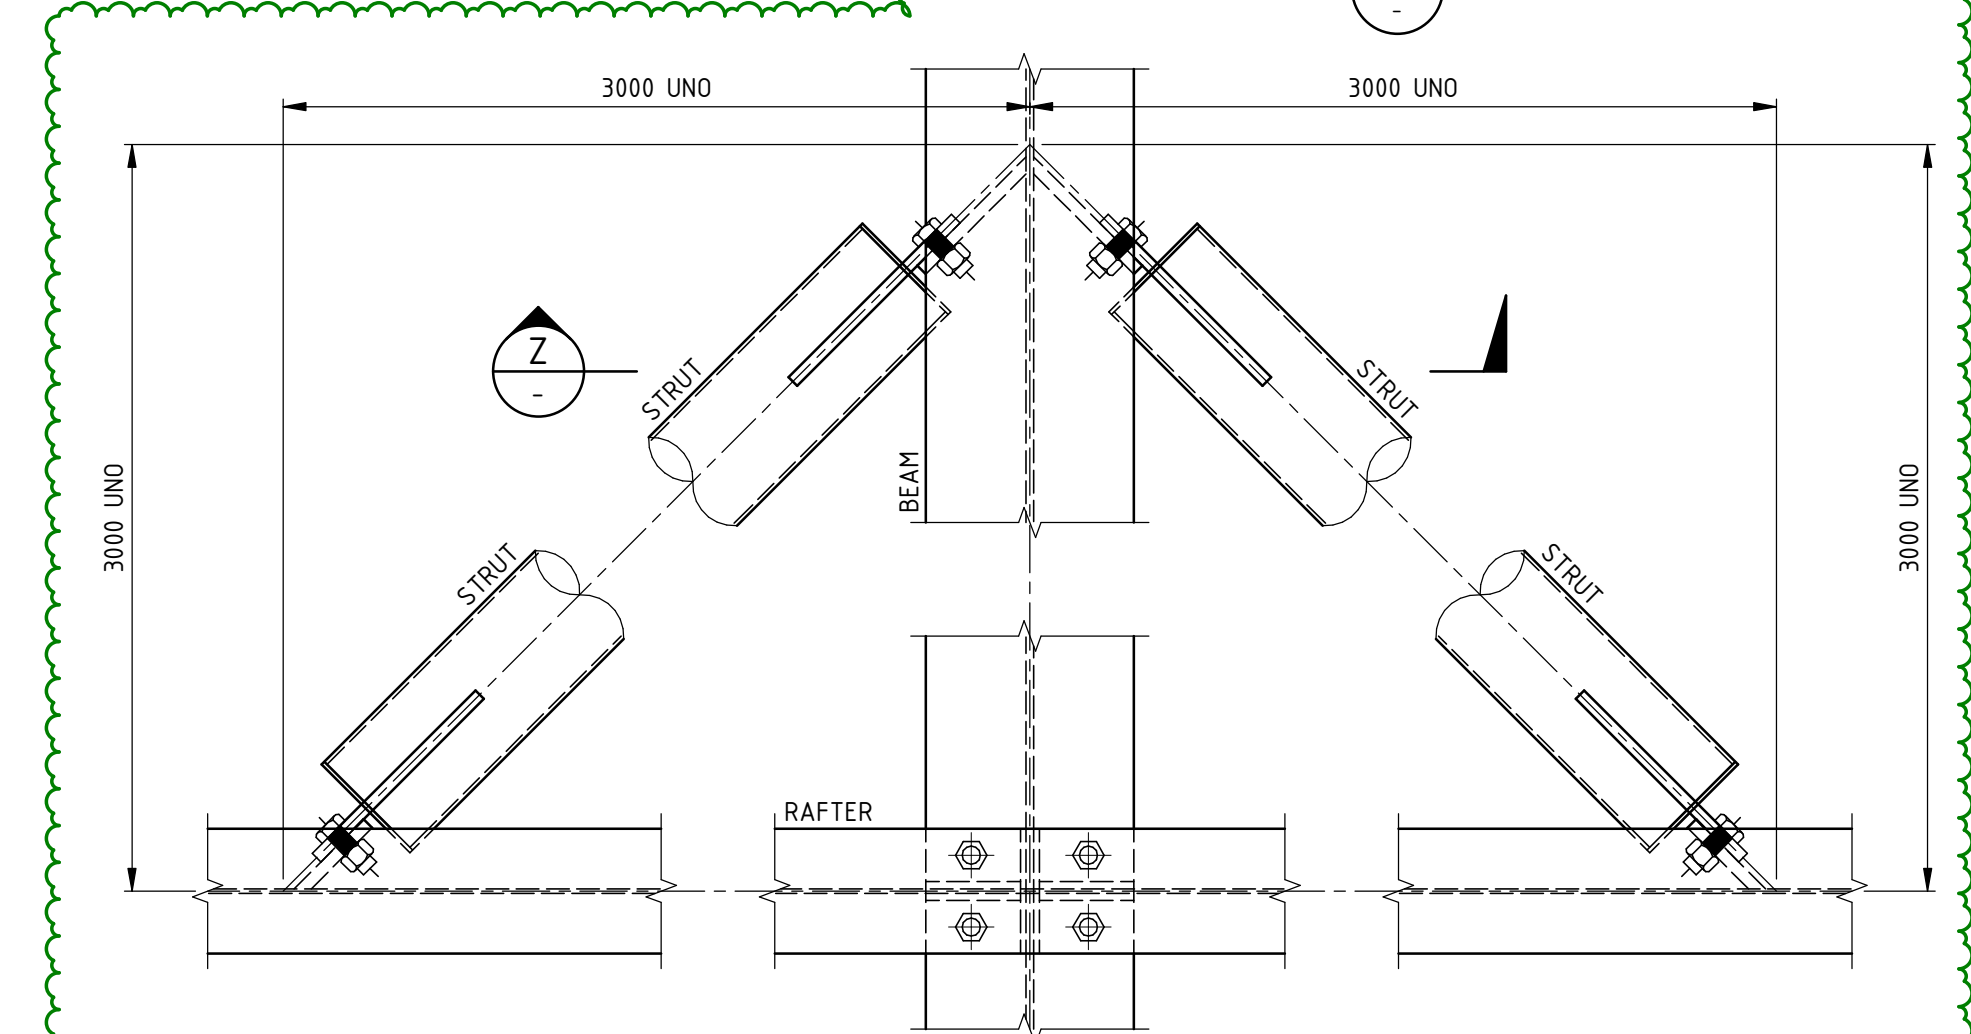

TYPICAL TRANSFER BEAM BRACING DETAIL

COPYRIGHT : REPRODUCTION OF WHOLE OR PART OF THIS DOCUMENT CONSTITUTES AN INFRINGEMENT OF COPYRIGHT. THE INFORMATION, IDEAS, AND CONCEPTS CONTAINED IN THIS DOCUMENT ARE CONFIDENTIAL. THE RECIPIENT(S) OF THIS DOCUMENT IS PROHIBITED FROM DISCLOSING SUCH INFORMATION IDEAS AND CONCEPTS TO ANY PERSON WITHOUT THE PRIOR WRITTEN CONSENT OF THE BRISBANE AIRPORT CORPORATION PTY. LTD.							
NS	BAC APPROVAL	11.06.26	B				
NS	STEEL DETAILS ISSUE	04.06.26	A				
DRN	AMENDMENTS	DATE	REV				

NORTHROP
PROJECT NUMBER: 250946

Drawn: HP	Checked:
Design Coordinated: HP	Compliance Checked: --
Authorised For Issue: NS	Construction Checked: --

SKYGATE PLAY	
TYPICAL STEEL DETAILS - SHEET 3	

 Brisbane Airport		BRISBANE AIRPORT CORPORATION PTY LTD 11 THE CIRCUIT, BRISBANE AIRPORT, QLD 4008, AUSTRALIA PO BOX 61, HAMILTON CENTRAL, QLD 4007, AUSTRALIA T: +61 7 3406 3000 E: INFO@BNE.COM.AU W: BNE.COM.AU					Scale: 1 : 10 Size: A1 Revision: B
Drawing Number	Project No.	Originator	Volume	Level	Type	Discipline	Number
25021	NOR	XX	01	DR	ST	006903	