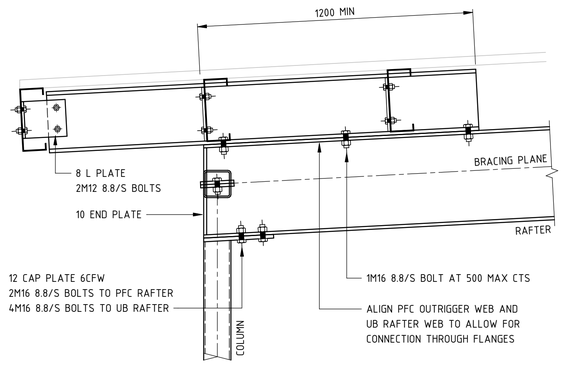

TYPICAL OFFICE COLUMN
TO RAFTER DETAIL

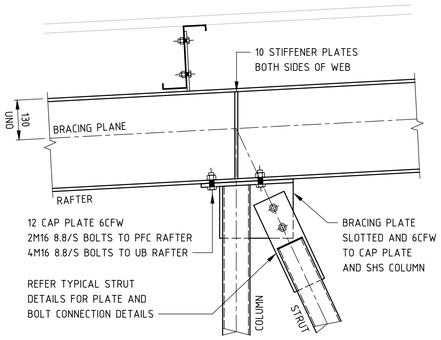

TYPICAL OFFICE COLUMN
TO RAFTER DETAIL

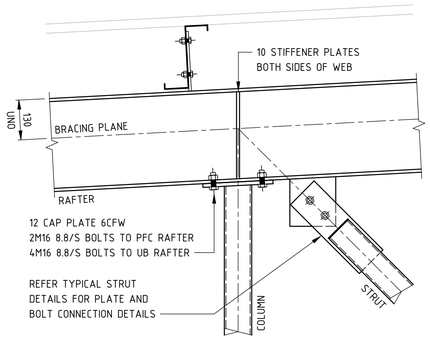

TYPICAL OFFICE COLUMN
TO RAFTER DETAIL

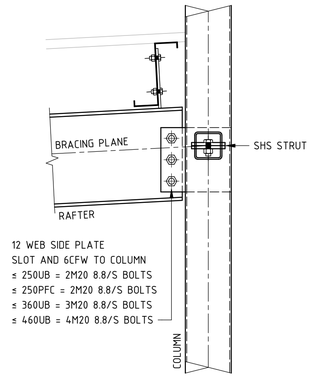

TYPICAL OFFICE COLUMN
TO RAFTER DETAIL

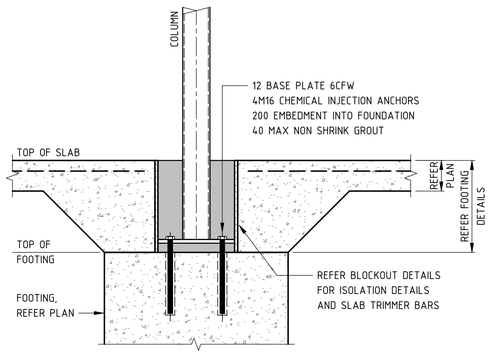

TYPICAL OFFICE COLUMN BASE PLATE DETAIL

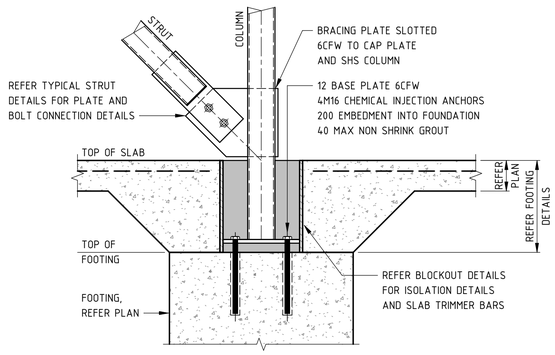

TYPICAL OFFICE COLUMN BASE PLATE DETAIL
AT WALL BRACING

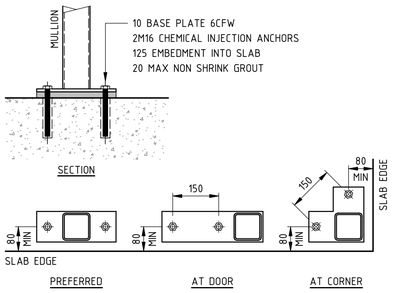

TYPICAL OFFICE MULLION BASE PLATE
TO SLAB DETAILS

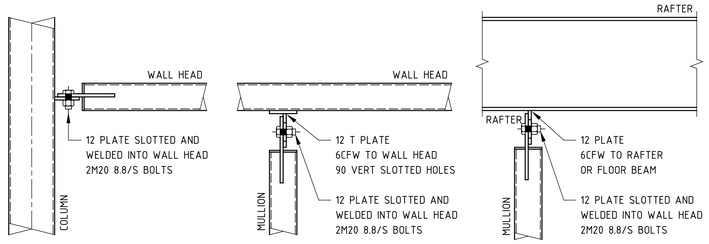

TYPICAL WALL HEAD AND MULLION CONNECTION DETAILS

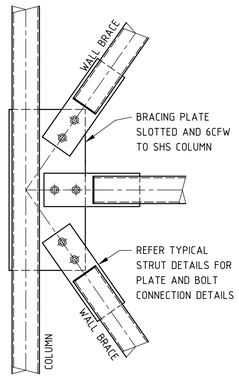

TYPICAL OFFICE WALL BRACE DETAIL

COPYRIGHT :
REPRODUCTION OF WHOLE OR PART OF THIS DOCUMENT CONSTITUTES AN INFRINGEMENT OF COPYRIGHT. THE INFORMATION, IDEAS, AND CONCEPTS CONTAINED IN THIS DOCUMENT ARE CONFIDENTIAL. THE RECIPIENT(S) OF THIS DOCUMENT IS PROHIBITED FROM DISCLOSING SUCH INFORMATION IDEAS AND CONCEPTS TO ANY PERSON WITHOUT THE PRIOR WRITTEN CONSENT OF THE BRISBANE AIRPORT CORPORATION PTY. LTD.

DRN	AMENDMENTS	DATE	REV
NS	STEEL DETAILS ISSUE	04.06.26	A
NS	BAC APPROVAL	11.06.26	B

NORTHROP
PROJECT NUMBER: 250946

Drawn: HP	Checked:
Design Coordinated: HP	Compliance Checked: --
Authorised For Issue: NS	Construction Checked: --

SKYGATE PLAY

TYPICAL STEEL DETAILS SHEET 4

Brisbane Airport
BRISBANE AIRPORT CORPORATION PTY LTD
11 THE CIRCUIT, BRISBANE AIRPORT, QLD, 4008, AUSTRALIA
PO BOX 61, HAMILTON CENTRAL, QLD, 4007, AUSTRALIA
T: +61 7 3406 3000
E: INFO@BNE.COM.AU
W: BNE.COM.AU

Scale: 1 : 10
Size: A1
Revision: B

Drawing Number	Project No.	Originator	Volume	Level	Type	Discipline	Number
	25021	NOR	XX	01	DR	ST	006904

File Path: Autodesk Docs://250946 - BNE Play/25021-NOR-ZZ-ZZ-M3-ST-000001.rvt

Plot Date & Time: 11/06/2026 10:04:11 AM