


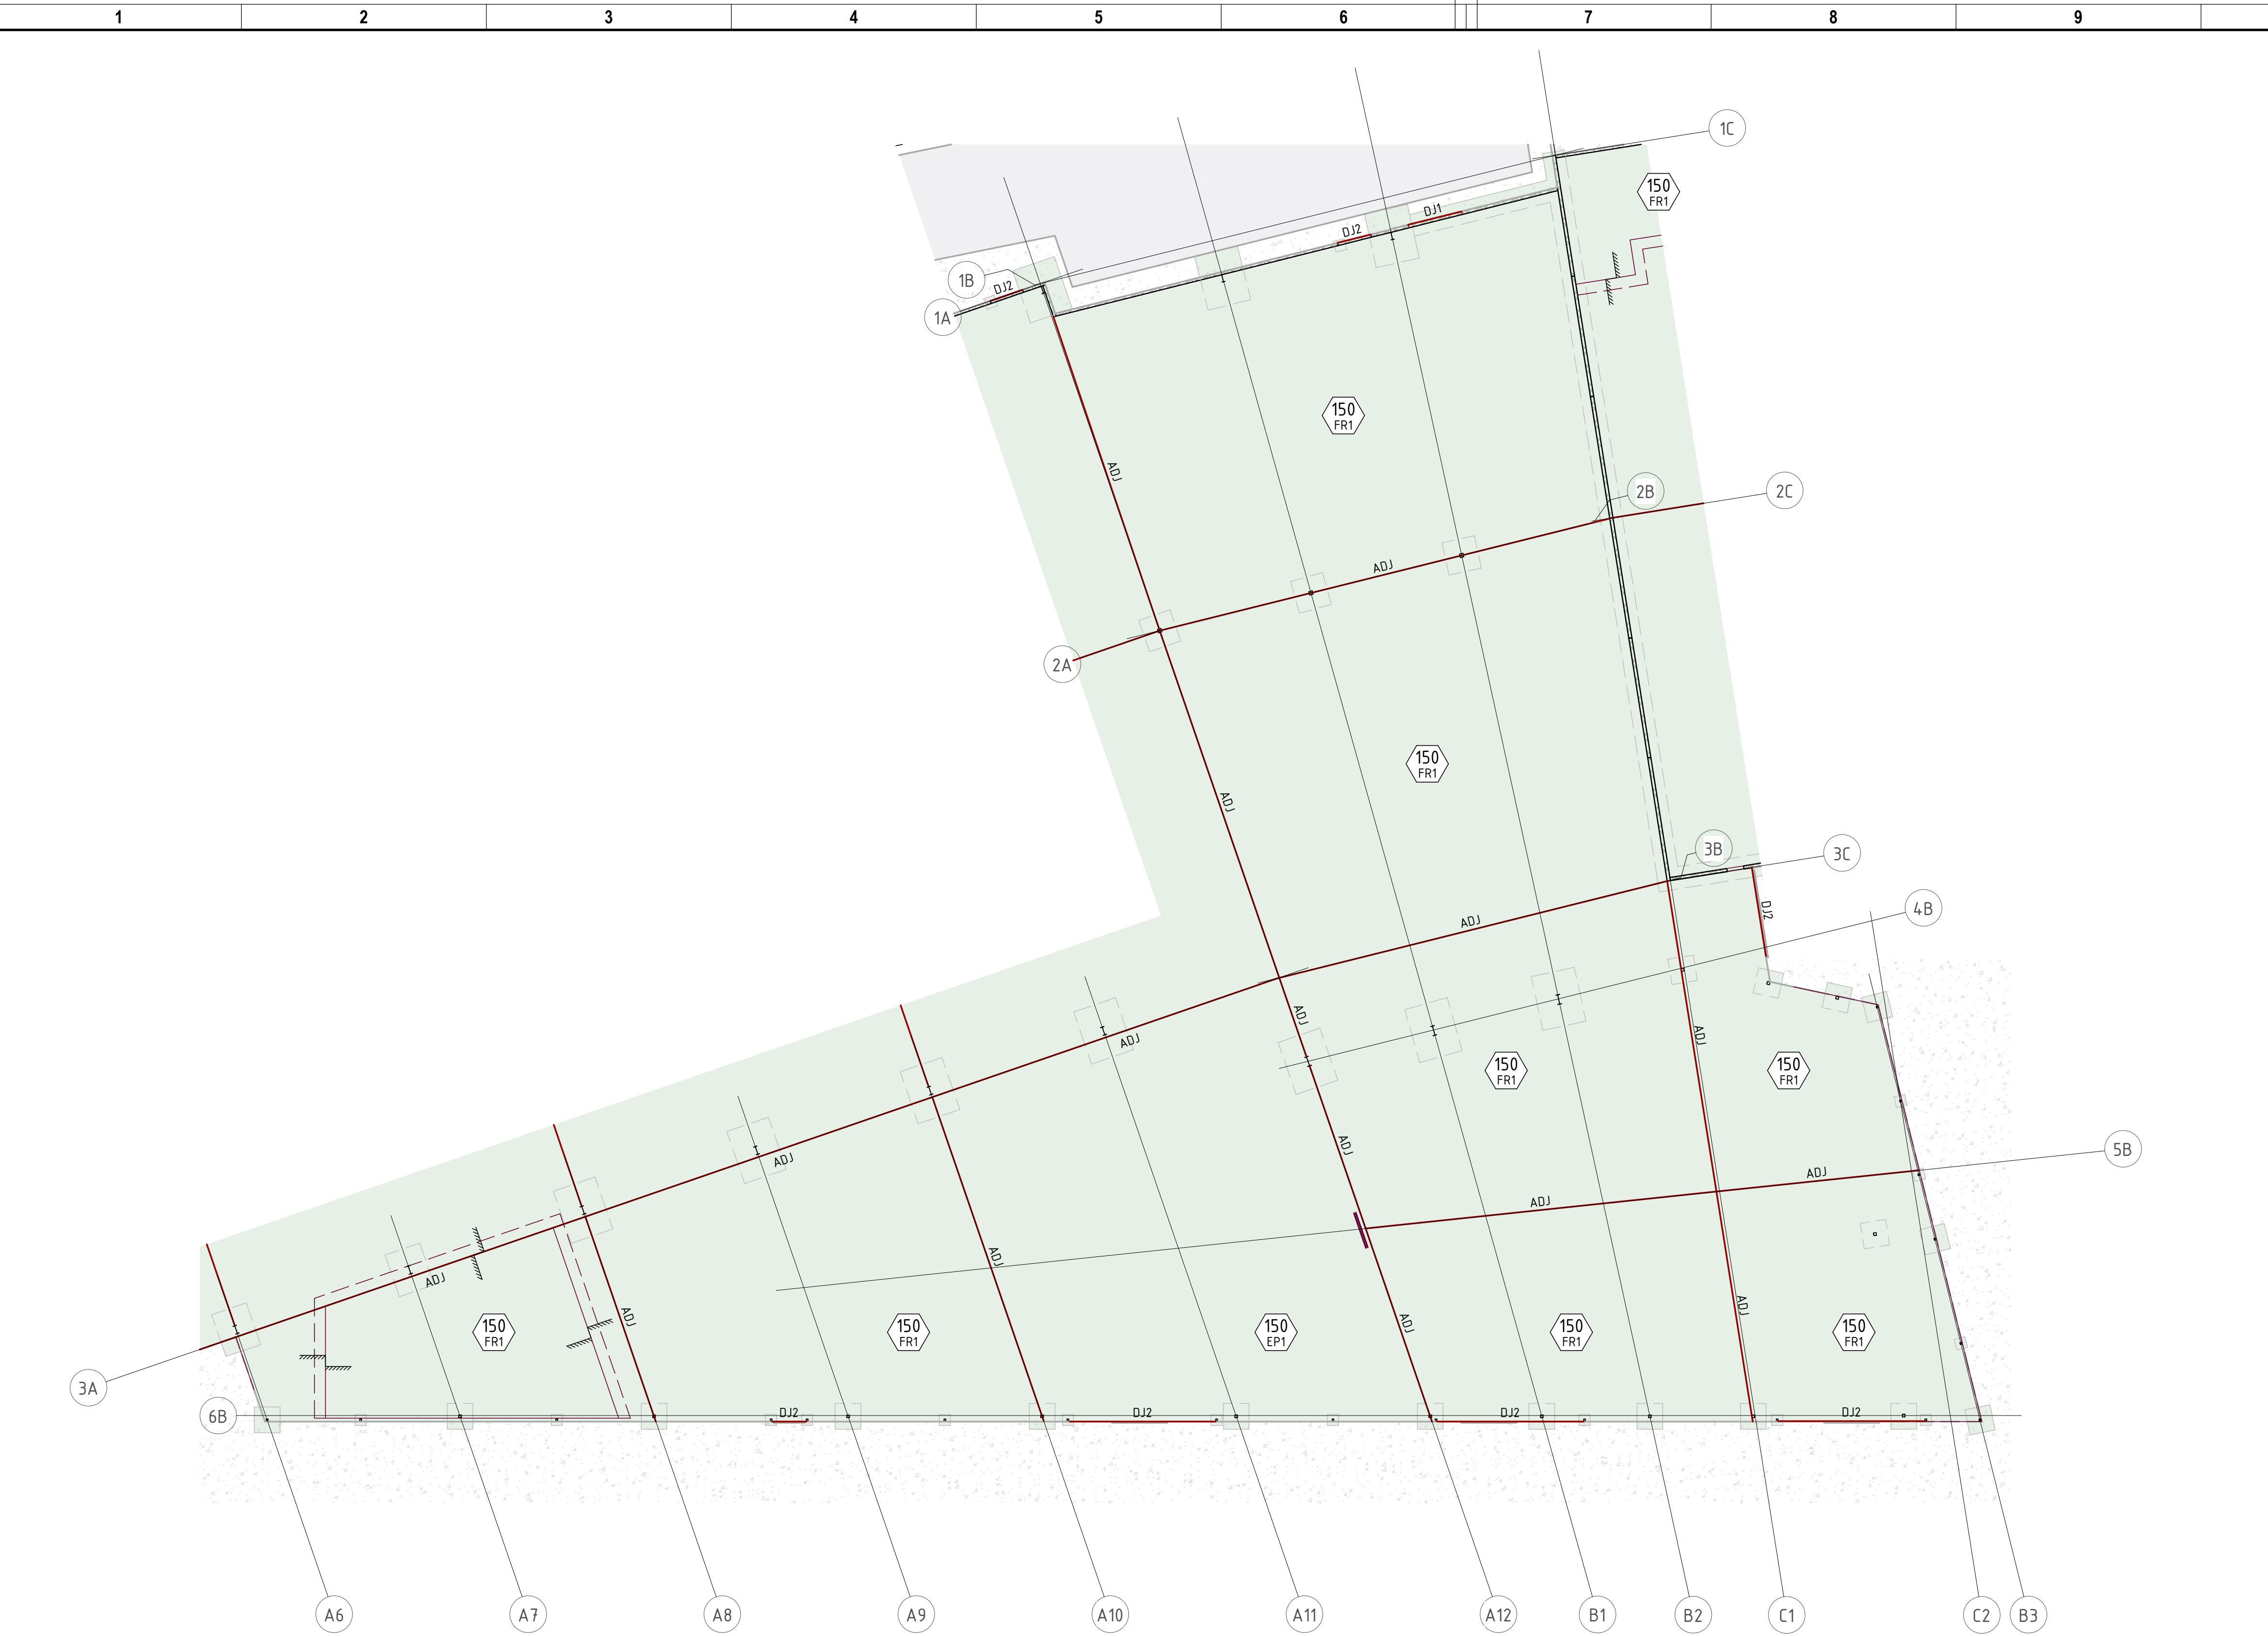

INTERNAL SLAB ON GROUND PLAN - PART 2  
SCALE 1 : 200

| SLAB ON GROUND SCHEDULE         |           |                                                 |                   |
|---------------------------------|-----------|-------------------------------------------------|-------------------|
| MARK                            | THICKNESS | REINFORCEMENT                                   | CONCRETE STRENGTH |
| EXTERNAL JOINTED SLAB ON GROUND |           |                                                 |                   |
| EP1                             | 150       | SL82 TOP                                        | N32               |
| FIBRE SLAB ON GROUND            |           |                                                 |                   |
| FR1                             | 150       | DRAMIX 4D 65/60BG<br>AT 20kg/m³                 | S40               |
| JOINTED SLAB ON GROUND          |           |                                                 |                   |
| SG1                             | 300       | SL102 TOP<br>N16-200 EACHWAY<br>BOTTOM          | N32               |
| SG2                             | 150       | SL82 TOP                                        | N32               |
| SG3                             | 120       | SL82 TOP<br>DJ2 MAX 25m CTRS<br>SJ2 MAX 5m CTRS | N32               |
| SG4                             | 150       | SL92 TOP & BOTTOM                               | N32               |

- SLAB ON GROUND NOTES**
- REFER S0.001-S0.003 FOR CONSTRUCTION NOTES
  - UNLESS NOTED OTHERWISE ON PLAN LOADS AS FOLLOWS:


| AREA OF LOAD | LIVE LOAD | SUPERIMPOSED DEAD LOAD |
|--------------|-----------|------------------------|
| GENERAL      | 4kPa      | 1kPa                   |
| PLANT        | 5kPa      |                        |
  - THE 28 DAY CONCRETE STRENGTH SHALL BE S32
  - THE CLEAR CONCRETE COVER TO ALL REINFORCEMENT SHALL BE:

| COMPONENT     | COVER |     |      |
|---------------|-------|-----|------|
|               | BTM   | TOP | SIDE |
| INTERNAL SLAB | 20    | 20  | N/A  |
| EXTERNAL SLAB | 30    | 40  | N/A  |
| BEAMS         | 50    | 50  | 50   |
  - MINIMUM REINFORCEMENT BAR LAPS SHALL BE:

| BAR SIZE    | TOP BAR | BTM BAR |
|-------------|---------|---------|
| N12         | 600     | 500     |
| N16         | 900     | 700     |
| N20         | 1200    | 950     |
| N24         | 1550    | 1200    |
| N28         | 1950    | 1500    |
| N32         | 2300    | 1800    |
| N36         | 2700    | 2100    |
| TRENCH MESH | 500     | 500     |

LAP MESH 1 SQUARE PLUS 30 MIN  
A TOP BAR HAS 300 MIN CONCRETE UNDER BAR
  - COORDINATE ALL SERVICE PENETRATIONS, SIZE AND LOCATIONS WITH ARCHITECTURAL, MECHANICAL, HYDRAULIC AND ELECTRICAL ENGINEERING DRAWINGS.
  - REFER ARCHITECT FOR SLAB SETOUT INCLUDING BUT NOT LIMITED TO: LEVELS, FALLS, STEPS, RAMPS, SET DOWNS, REBATES, HOBS AND DIMENSIONS.
  - REFER CIVIL ENGINEER FOR BUILDING PAD PREPARATION.
  - PROVIDE TRIMMER BARS AT ALL RE ENTRANT CORNERS, SERVICE PENETRATIONS AND COLUMNS IN ACCORDANCE WITH SLAB TRIMMER DETAILS
  - UNO ALL SLABS TO BE POURED ON 2 LAYERS OF POLYETHYLENE SHEETING OVER CBR15 SUBBASE

- SLAB ON GROUND LEGEND**
- 200 SG1 SLAB THICKNESS
  - SLAB DESCRIPTION REFER SCHEDULE
  - FIBRE SLAB
  - EXTERNAL INSITU SLAB
  - EXTERNAL FOOTPATH SLAB
  - SLAB STEP LOCATION
  - DJ1 DJ2 DOWEL JOINT FOR DETAILS REFER 002901
  - SJ1 SJ2 SAWN JOINT FOR DETAILS REFER 002901
  - BW# LOAD BEARING BLOCK WALL FOR DETAILS REFER 002901
  - PW# PRECAST WALL FOR DETAILS REFER 003991
  - I square STEELWORK COLUMN FOR DETAILS REFER 006902

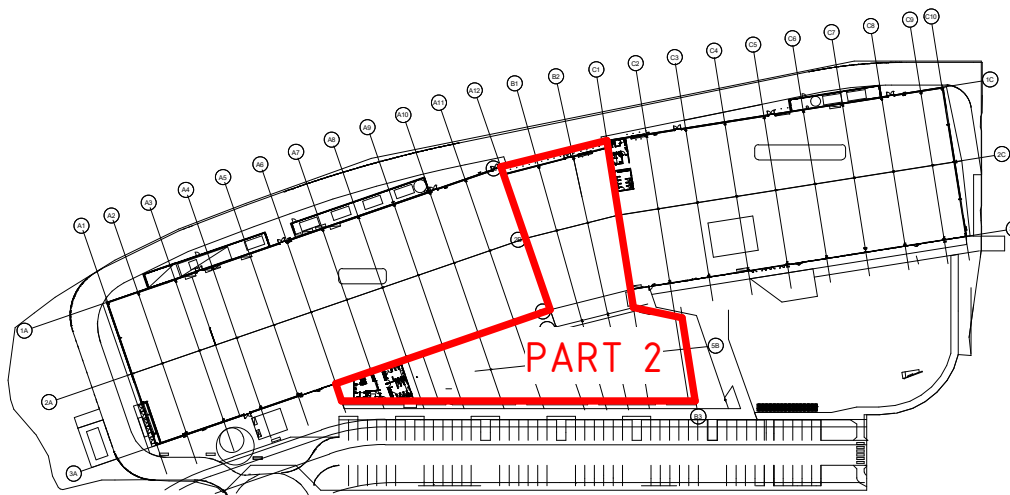

SITE KEY PLAN

COPYRIGHT :  
REPRODUCTION OF WHOLE OR PART OF THIS  
DOCUMENT CONSTITUTES AN INFRINGEMENT  
OF COPYRIGHT. THE INFORMATION, IDEAS,  
AND CONCEPTS CONTAINED IN THIS  
DOCUMENT ARE CONFIDENTIAL. THE  
RECIPIENT(S) OF THIS DOCUMENT IS  
PROHIBITED FROM DISCLOSING SUCH  
INFORMATION IDEAS AND CONCEPTS TO ANY  
PERSON WITHOUT THE PRIOR WRITTEN  
CONSENT OF THE BRISBANE AIRPORT  
CORPORATION PTY. LTD.

|     |              |          |     |
|-----|--------------|----------|-----|
| NS  | BAC APPROVAL | 11.06.26 | A   |
| DRN | AMENDMENTS   | DATE     | REV |

**NORTHROP**  
PROJECT NUMBER: 250946

|                             |                             |
|-----------------------------|-----------------------------|
| Drawn:<br>HP                | Checked:                    |
| Design Coordinated:<br>HP   | Compliance Checked:<br>--   |
| Authorised For Issue:<br>NS | Construction Checked:<br>-- |

SKYGATE PLAY  
  
SLAB ON GROUND PLAN - PART 2

|   |                                                           |            |        |       |      |            |         |                        |
|---|-----------------------------------------------------------|------------|--------|-------|------|------------|---------|------------------------|
| <br><b>Brisbane<br/>Airport</b> | BRISBANE AIRPORT CORPORATION PTY LTD                      |            |        |       |      |            |         | Scale:<br>As indicated |
|   | 11 THE CIRCUIT, BRISBANE AIRPORT,<br>QLD, 4008, AUSTRALIA |            |        |       |      |            |         | Size:<br>A1            |
|   | PO BOX 61, HAMILTON CENTRAL,<br>QLD, 4007, AUSTRALIA      |            |        |       |      |            |         |                        |
|   | T: +61 7 3406 3000<br>E: INFO@BNE.COM.AU<br>W: BNE.COM.AU |            |        |       |      |            |         | Revision:<br>A         |
| Drawing<br>Number   | Project No.                                               | Originator | Volume | Level | Type | Discipline | Number  |                        |
|   | 25021                                                     | - NOR      | - XX   | - 01  | - DR | - ST       | - 00200 |                        |