


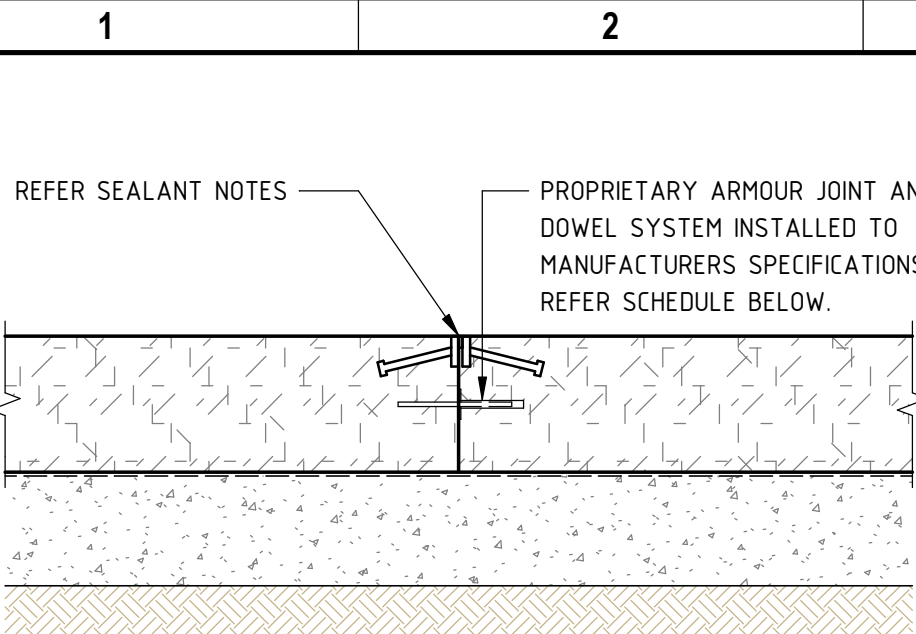


TYPICAL ARMoured DOWEL JOINT (ADJ1)

GDJ1 - SIMILAR - DOWELS TO BE GALVANISED

SCALE 1:10


ARMOUR DOWEL SCHEDULE			
MANUFACTURER	PRODUCT	DOWEL	SPACING
DANLEY	HYPER ARMOURMATE	10 DANLEY DIAMOND	450
PEIKKO	TERAJOINT	150 x 10 PLATE	500
ISEDIO	ARMOURJOINT	150 x 75 x 8 PLATE	430
LESA	LESA TYPE B	DOMINATOR 75/10	400

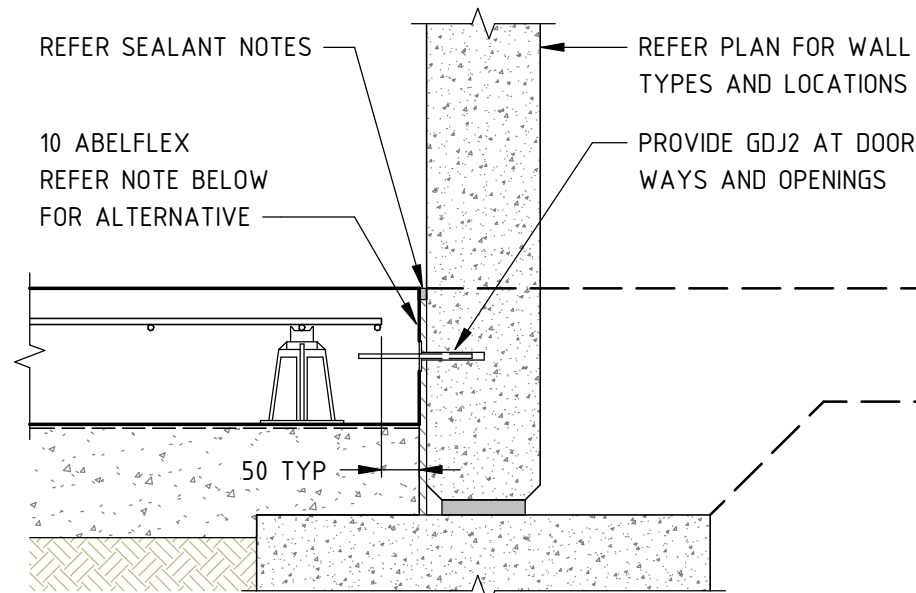

TYPICAL ISOLATION JOINT DETAIL (ISJ)

SCALE 1:10

- ABelflex MAY BE SUBSTITUTED WITH 2 LAYERS OF POLYTHELENE SHEETING OR PAINT SURFACE WITH BONDBREAKER

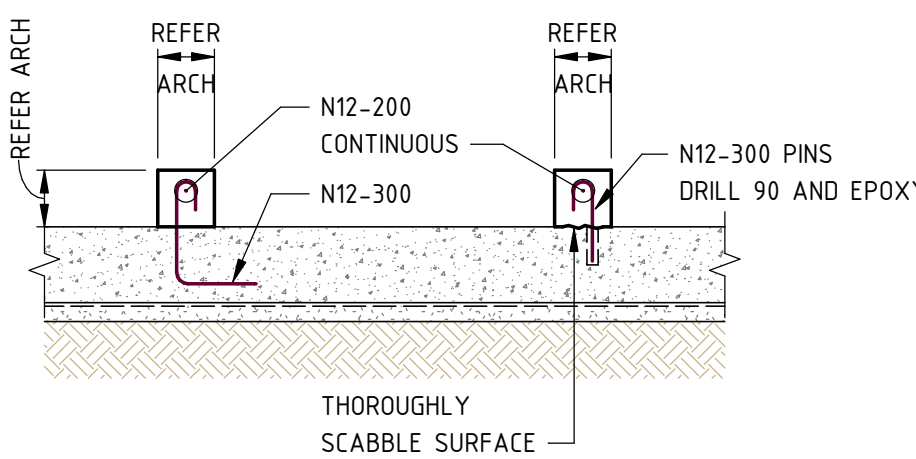


CAST-IN

POST FIX

TYPICAL HOB UNDER 190 WIDE DETAIL

- REFER ARCH FOR HOB LOCATIONS AND SIZE
- EPOXY TO BE RAMSET REO 502 OR APPROVED EQUIVALENT
- CONCRETE STRENGTH AND PARAMETERS TO MATCH SLAB
- PROVIDE SAWN JOINT WHERE HOB CROSSES SLAB JOINT (CUT N12 BAR)

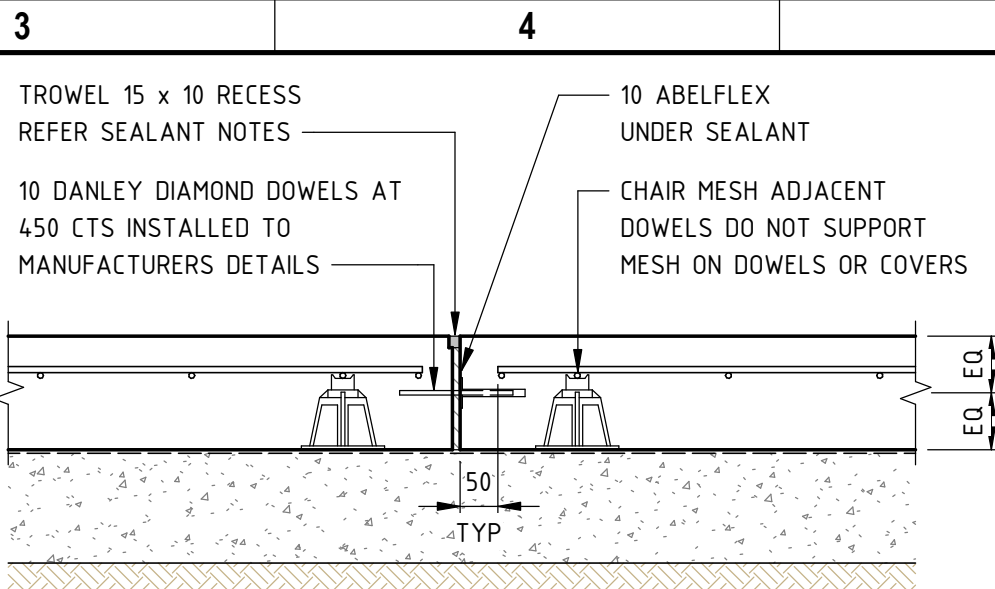


TYPICAL DOWEL JOINT 1 DETAIL (DJ1)

GDJ1 - SIMILAR - DOWELS TO BE GALVANISED


SCALE 1:10

- REFER MANUFACTURERS INSTALLATION GUIDE
- CENTRE LINE OF FIRST DOWEL TO BE 225 FROM CORNERS

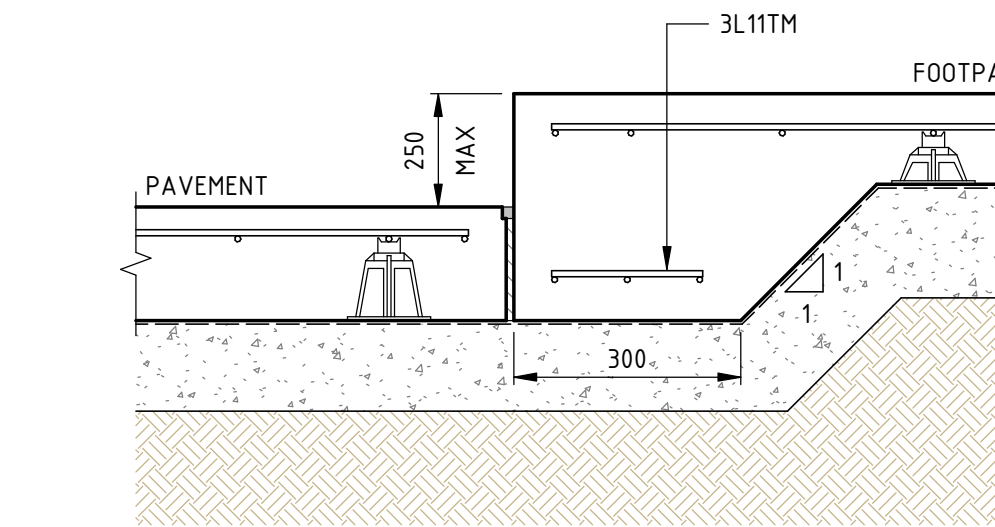

TYPICAL EXTERNAL PAVEMENT KERB STEP TO FOOTPATH SLAB DETAIL

SCALE 1:10

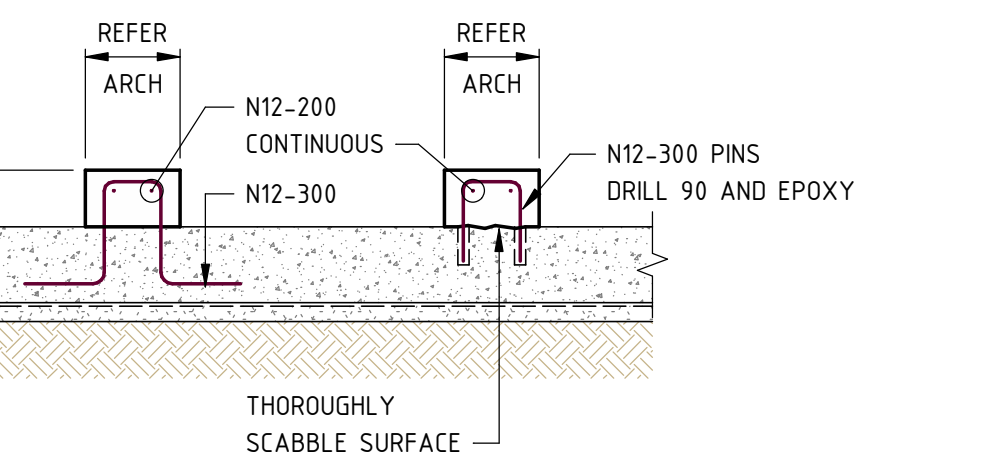


CAST-IN

POST FIX

TYPICAL HOB OVER 191 WIDE DETAIL

- REFER ARCH FOR HOB LOCATIONS AND SIZE
- EPOXY TO BE RAMSET REO 502 OR APPROVED EQUIVALENT
- CONCRETE STRENGTH AND PARAMETERS TO MATCH SLAB
- PROVIDE SAWN JOINT WHERE HOB CROSSES SLAB JOINT (CUT N12 BAR)

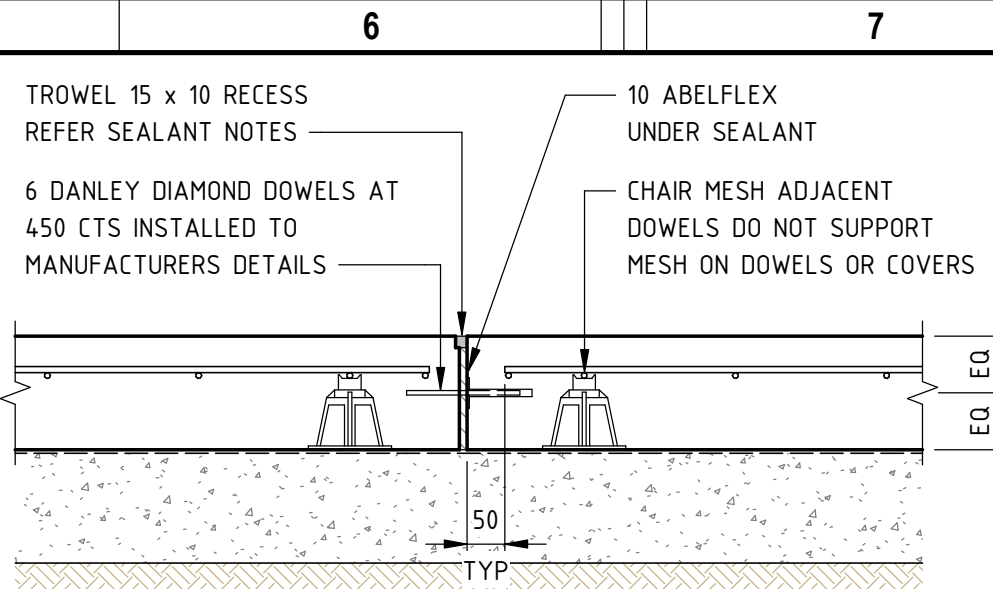


TYPICAL DOWEL JOINT 1 DETAIL (DJ2)

GDJ2 - SIMILAR - DOWELS TO BE GALVANISED


SCALE 1:10

- REFER MANUFACTURERS INSTALLATION GUIDE
- CENTRE LINE OF FIRST DOWEL TO BE 225 FROM CORNERS

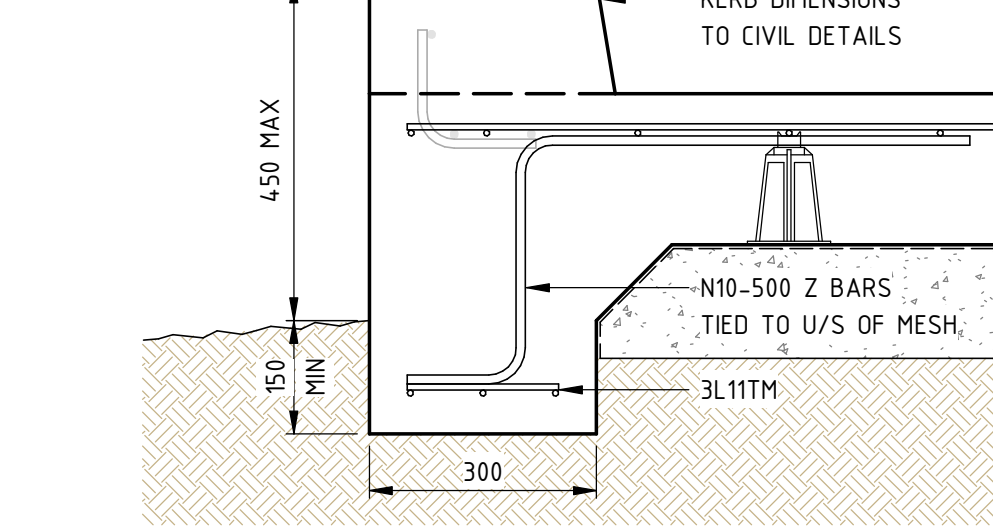


TYPICAL EXTERNAL PAVEMENT KERB AND TURNDOWN DETAIL AT BOUNDARY

SCALE 1:10

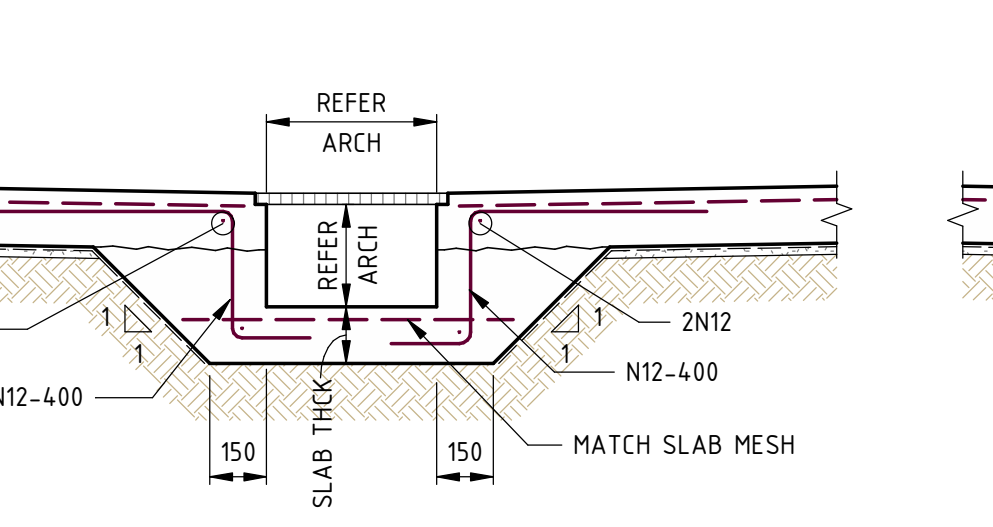

TYPICAL GRATED DRAIN DETAIL


- REFER ARCH FOR HOB LOCATIONS AND SIZE
- EPOXY TO BE RAMSET REO 502 OR APPROVED EQUIVALENT
- CONCRETE STRENGTH AND PARAMETERS TO MATCH SLAB
- PROVIDE SAWN JOINT WHERE HOB CROSSES SLAB JOINT (CUT N12 BAR)

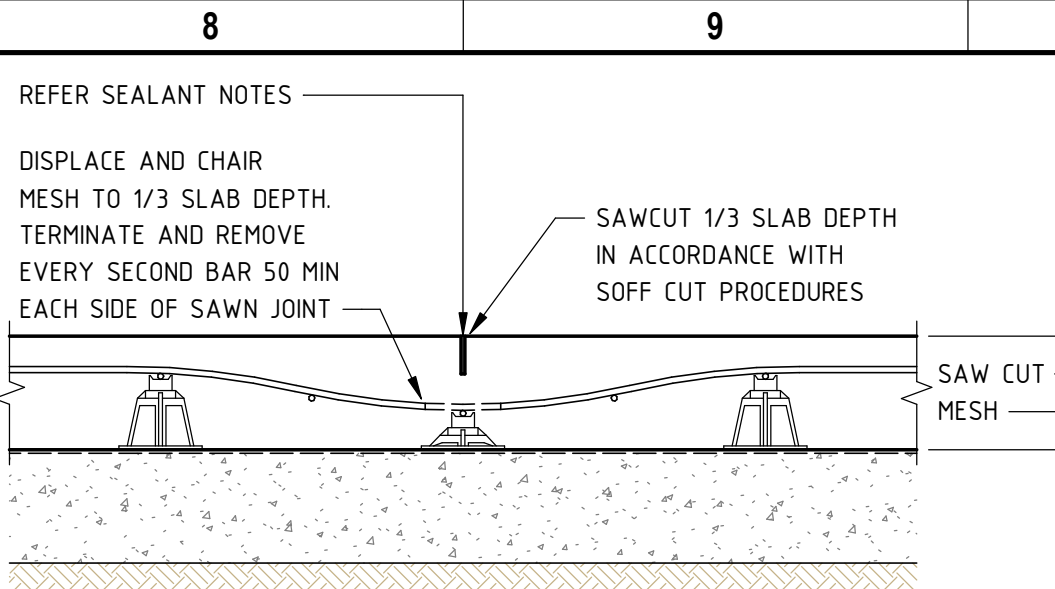

TYPICAL SAWN JOINT 1 DETAIL (SJ1)


SCALE 1:10

- REFER MANUFACTURERS INSTALLATION GUIDE
- CENTRE LINE OF FIRST DOWEL TO BE 225 FROM CORNERS

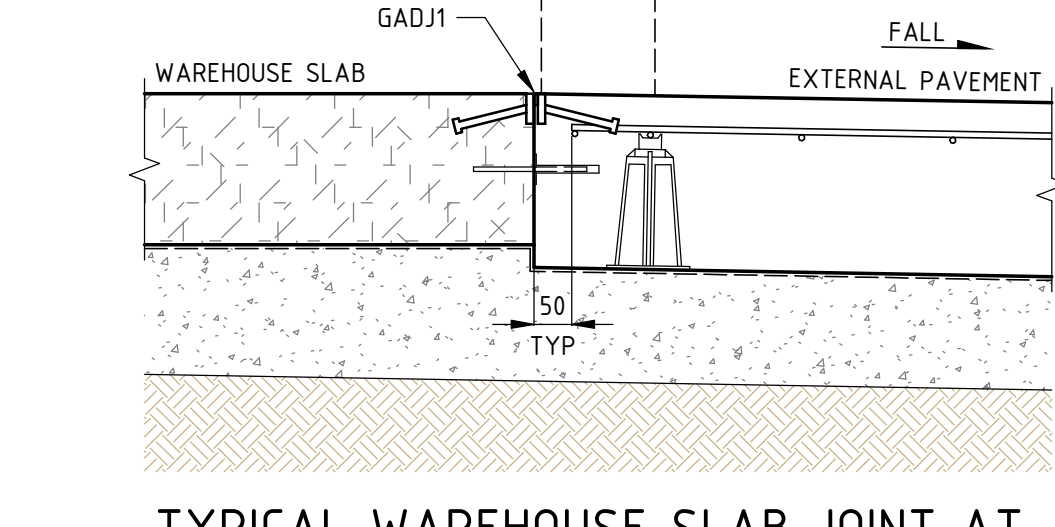


TYPICAL WAREHOUSE SLAB JOINT AT ROLLER DOOR DETAIL

SCALE 1:10

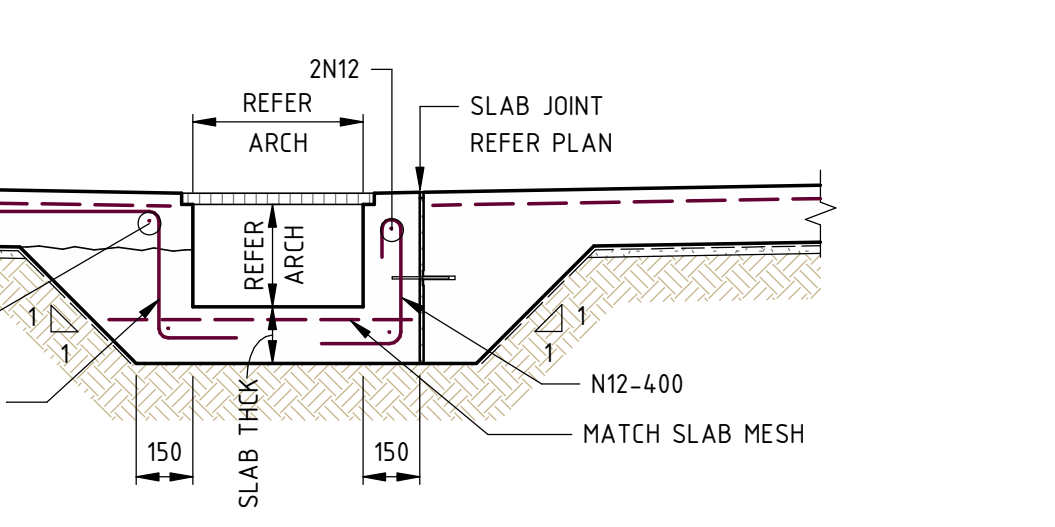

TYPICAL GRATED DRAIN DETAIL AT SLAB JOINT


- REFER ARCH FOR HOB LOCATIONS AND SIZE
- EPOXY TO BE RAMSET REO 502 OR APPROVED EQUIVALENT
- CONCRETE STRENGTH AND PARAMETERS TO MATCH SLAB
- PROVIDE SAWN JOINT WHERE HOB CROSSES SLAB JOINT (CUT N12 BAR)

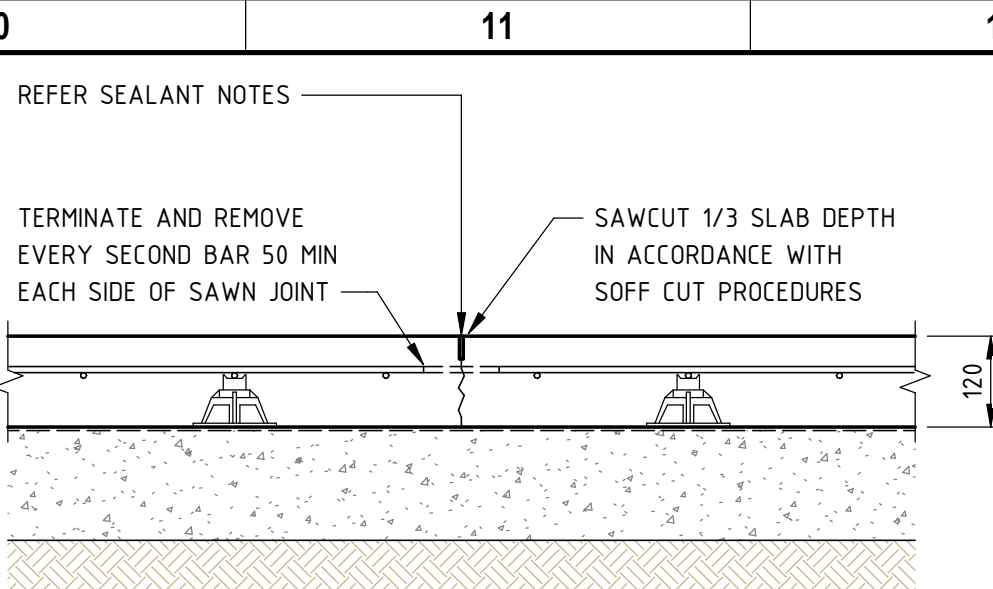

TYPICAL SAWN JOINT 2 DETAIL (SJ2)

SCALE 1:10

- REFER MANUFACTURERS INSTALLATION GUIDE
- CENTRE LINE OF FIRST DOWEL TO BE 225 FROM CORNERS

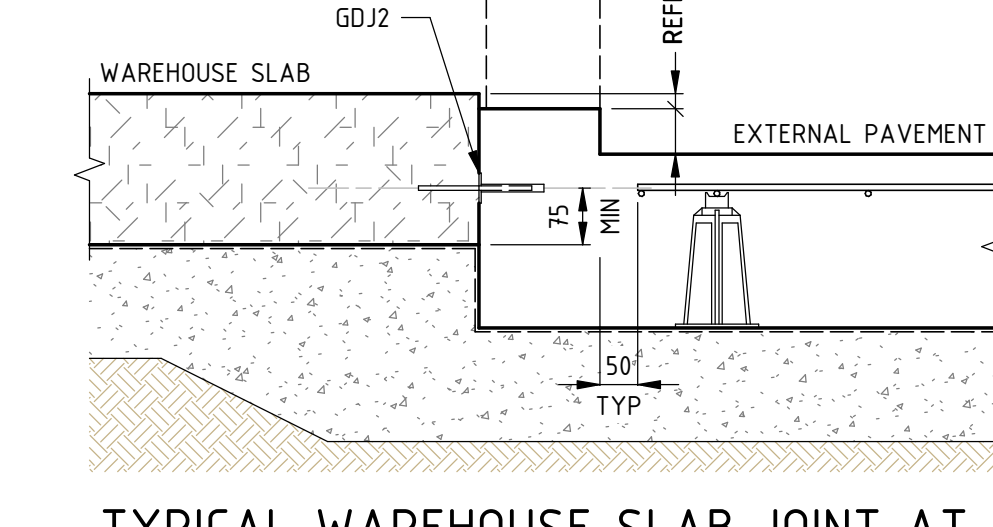


TYPICAL WAREHOUSE SLAB JOINT AT PEDESTRIAN DOOR DETAIL

SCALE 1:10



TYPICAL GRATED DRAIN DETAIL AT SLAB JOINT

- REFER ARCH FOR HOB LOCATIONS AND SIZE
- EPOXY TO BE RAMSET REO 502 OR APPROVED EQUIVALENT
- CONCRETE STRENGTH AND PARAMETERS TO MATCH SLAB
- PROVIDE SAWN JOINT WHERE HOB CROSSES SLAB JOINT (CUT N12 BAR)

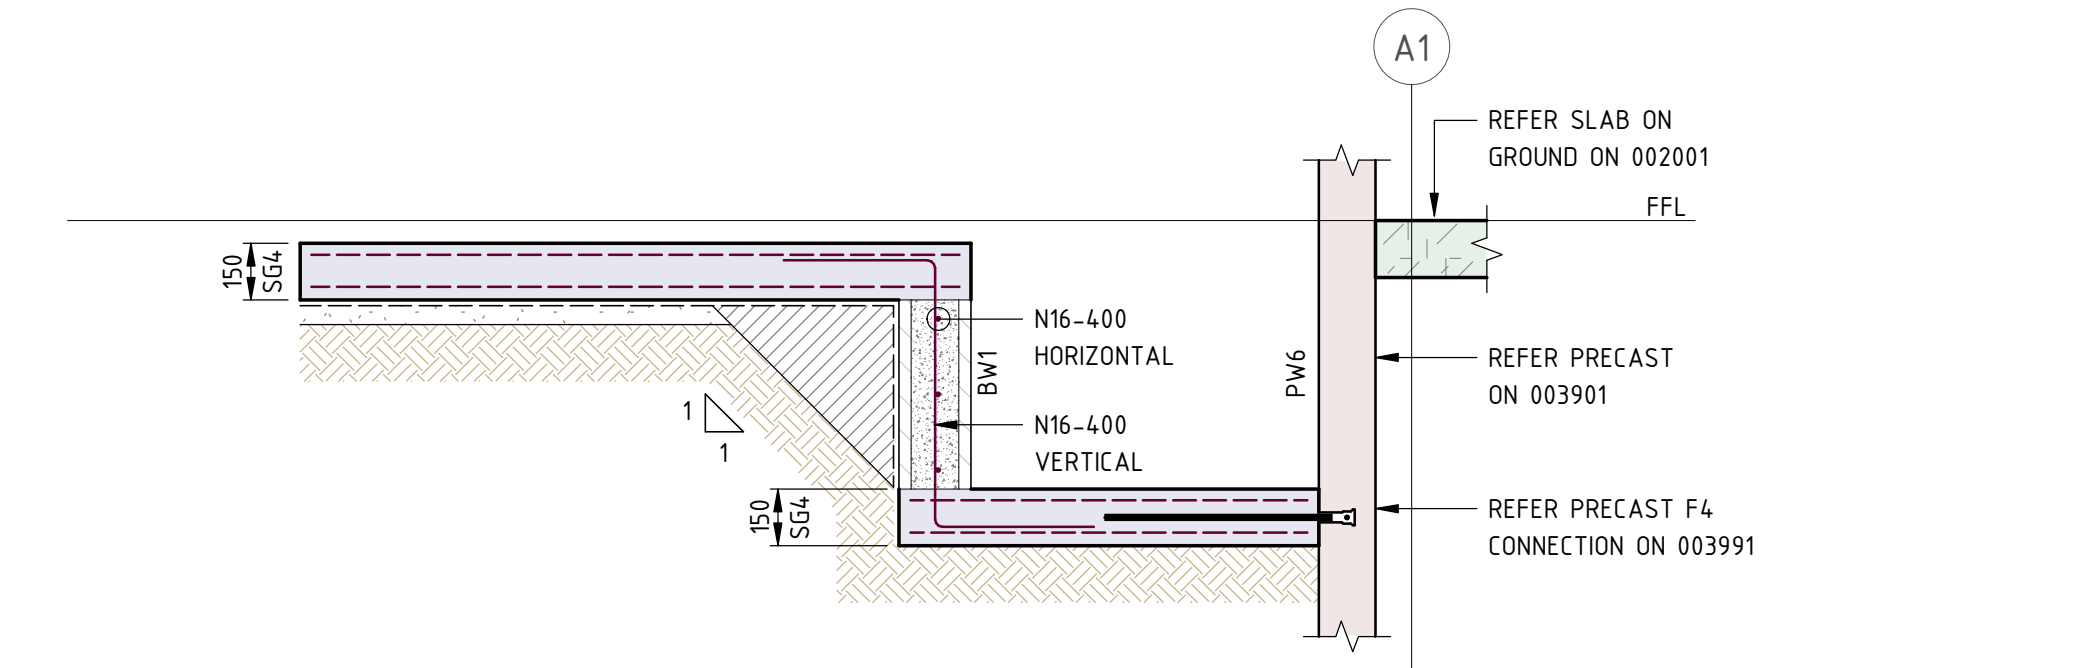

SECTION
SCALE 1 : 20

GF1
002001

SOFF CUT SAWING NOTES	
1.	CONCRETE SAWN JOINTS TO BE CUT USING 'SOFF CUT' BLADE AND SAW WITH SKID PLATE.
2.	SAW CUTS TO BE MADE AS SOON AS POSSIBLE BETWEEN 2-6 HOURS AFTER SLAB POUR.
3.	CONTRACTOR TO MAKE TEST CUT 1.0m LONG AND CHECK FOR CHIPS SPALLING OR SKID MARKS. IF EVIDENT WAIT 30 MINUTES AND CONDUCT ANOTHER TEST CUT.
4.	SAW CUTTING SHOULD FOLLOW THE DIRECTION SLAB IS POURED.
JOINT SEALANT NOTES	
1.	ALL INTERNAL JOINTS TO BE FILLED WITH AN APPROVED SEMI RIGID SEALANT SUCH AS PU40.
2.	ALL EXTERNAL JOINTS TO BE FILLED WITH AN APPROVED FLEXIBLE SEALANT SUCH AS SIKAFLEX.
3.	FOR CHEMICAL OR FUEL STORAGE AREAS REFER MANUFACTURER FOR PRODUCT SUITABILITY.
4.	FOR COLOURED CONCRETE REFER ARCHITECT FOR SEALANT SPECIFICATION.
5.	CONTRACTOR TO USE APPROPRIATE SIZED BACKING RODS AS REQUIRED FOR SEALANT INSTALLATION
6.	ALTERNATIVE SEALANT MANUFACTURERS PRODUCTS MAY BE USED. CONTRACTOR TO SUBMIT TECHNICAL DATA TO NORTHROP CONSULTING FOR APPROVAL.

COPYRIGHT :
REPRODUCTION OF WHOLE OR PART OF THIS DOCUMENT CONSTITUTES AN INFRINGEMENT OF COPYRIGHT. THE INFORMATION, IDEAS, AND CONCEPTS CONTAINED IN THIS DOCUMENT ARE CONFIDENTIAL. THE RECIPIENT(S) OF THIS DOCUMENT IS PROHIBITED FROM DISCLOSING SUCH INFORMATION IDEAS AND CONCEPTS TO ANY PERSON WITHOUT THE PRIOR WRITTEN CONSENT OF THE BRISBANE AIRPORT CORPORATION PTY. LTD.

NS
DRN

BAC APPROVAL
AMENDMENTS

11.06.26
DATE

A
REV

NORTHROP

PROJECT NUMBER: 250946

Drawn:
HP

Checked:
--

Design Coordinated:
HP

Compliance Checked:
--

Authorised For Issue:
NS

Construction Checked:
--

SKYGATE PLAY

TYPICAL SLAB ON GROUND DETAILS - SHEET 1

Brisbane Airport

BRISBANE AIRPORT CORPORATION PTY LTD
11 THE CIRCUIT, BRISBANE AIRPORT,
QLD 4008, AUSTRALIA
PO BOX 61, HAMILTON CENTRAL,
QLD 4007, AUSTRALIA
T: +61 7 3406 3000
E: INFO@BNE.COM.AU
W: BNE.COM.AU

Scale:
As indicated

Size:
A1

Revision:
A

Project No. Originator Volume Level Type Discipline Number

25021 - NOR - XX - 01 - DR - ST - 002901

Plot Date & Time:

11/06/2026 10:03:25 AM