




1 2 3 4 5 6 7 8 9 10 11 12

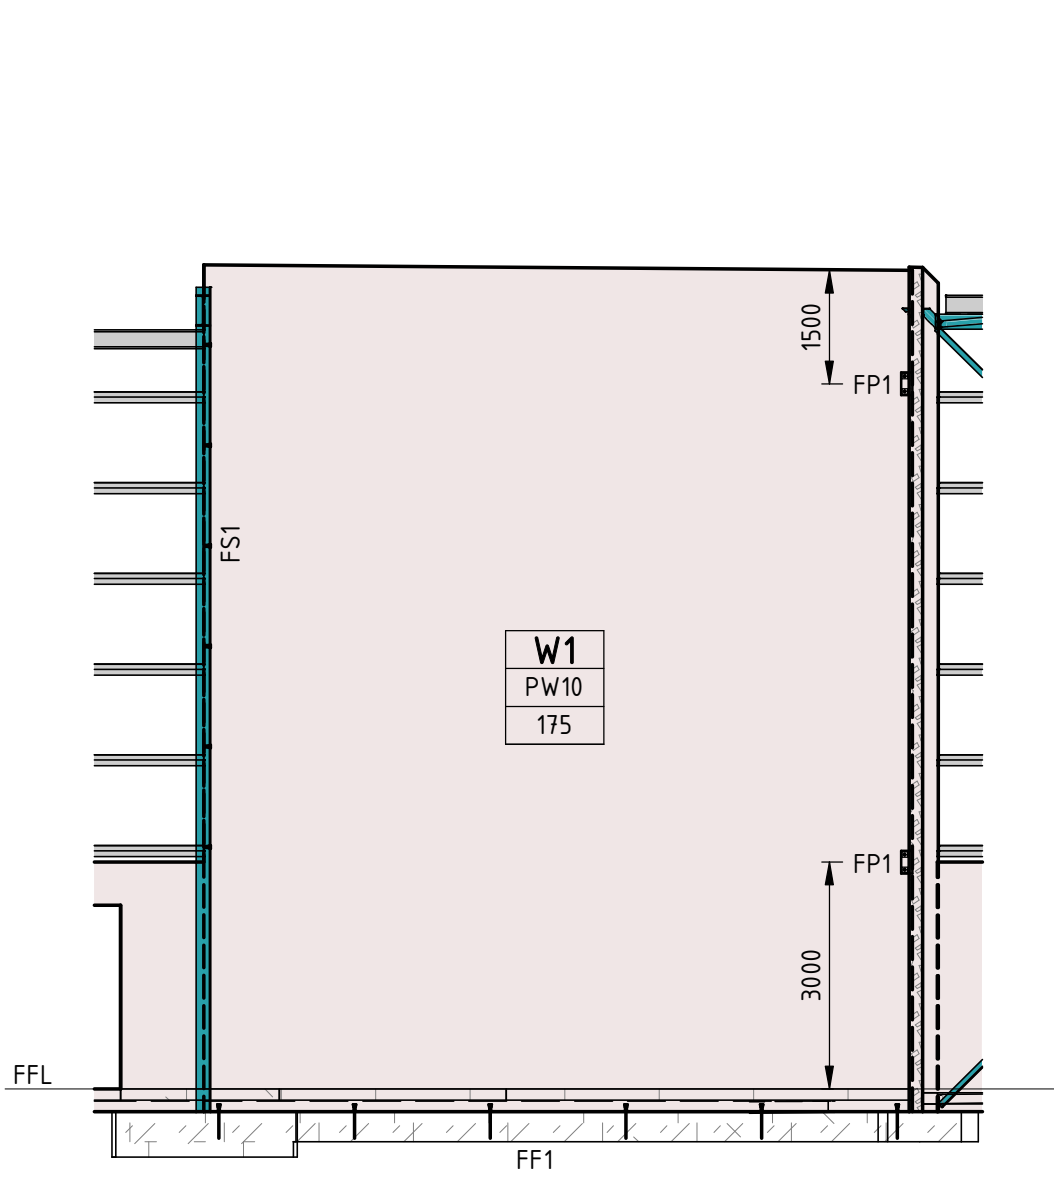


SECTION 1B
SCALE 1 : 100

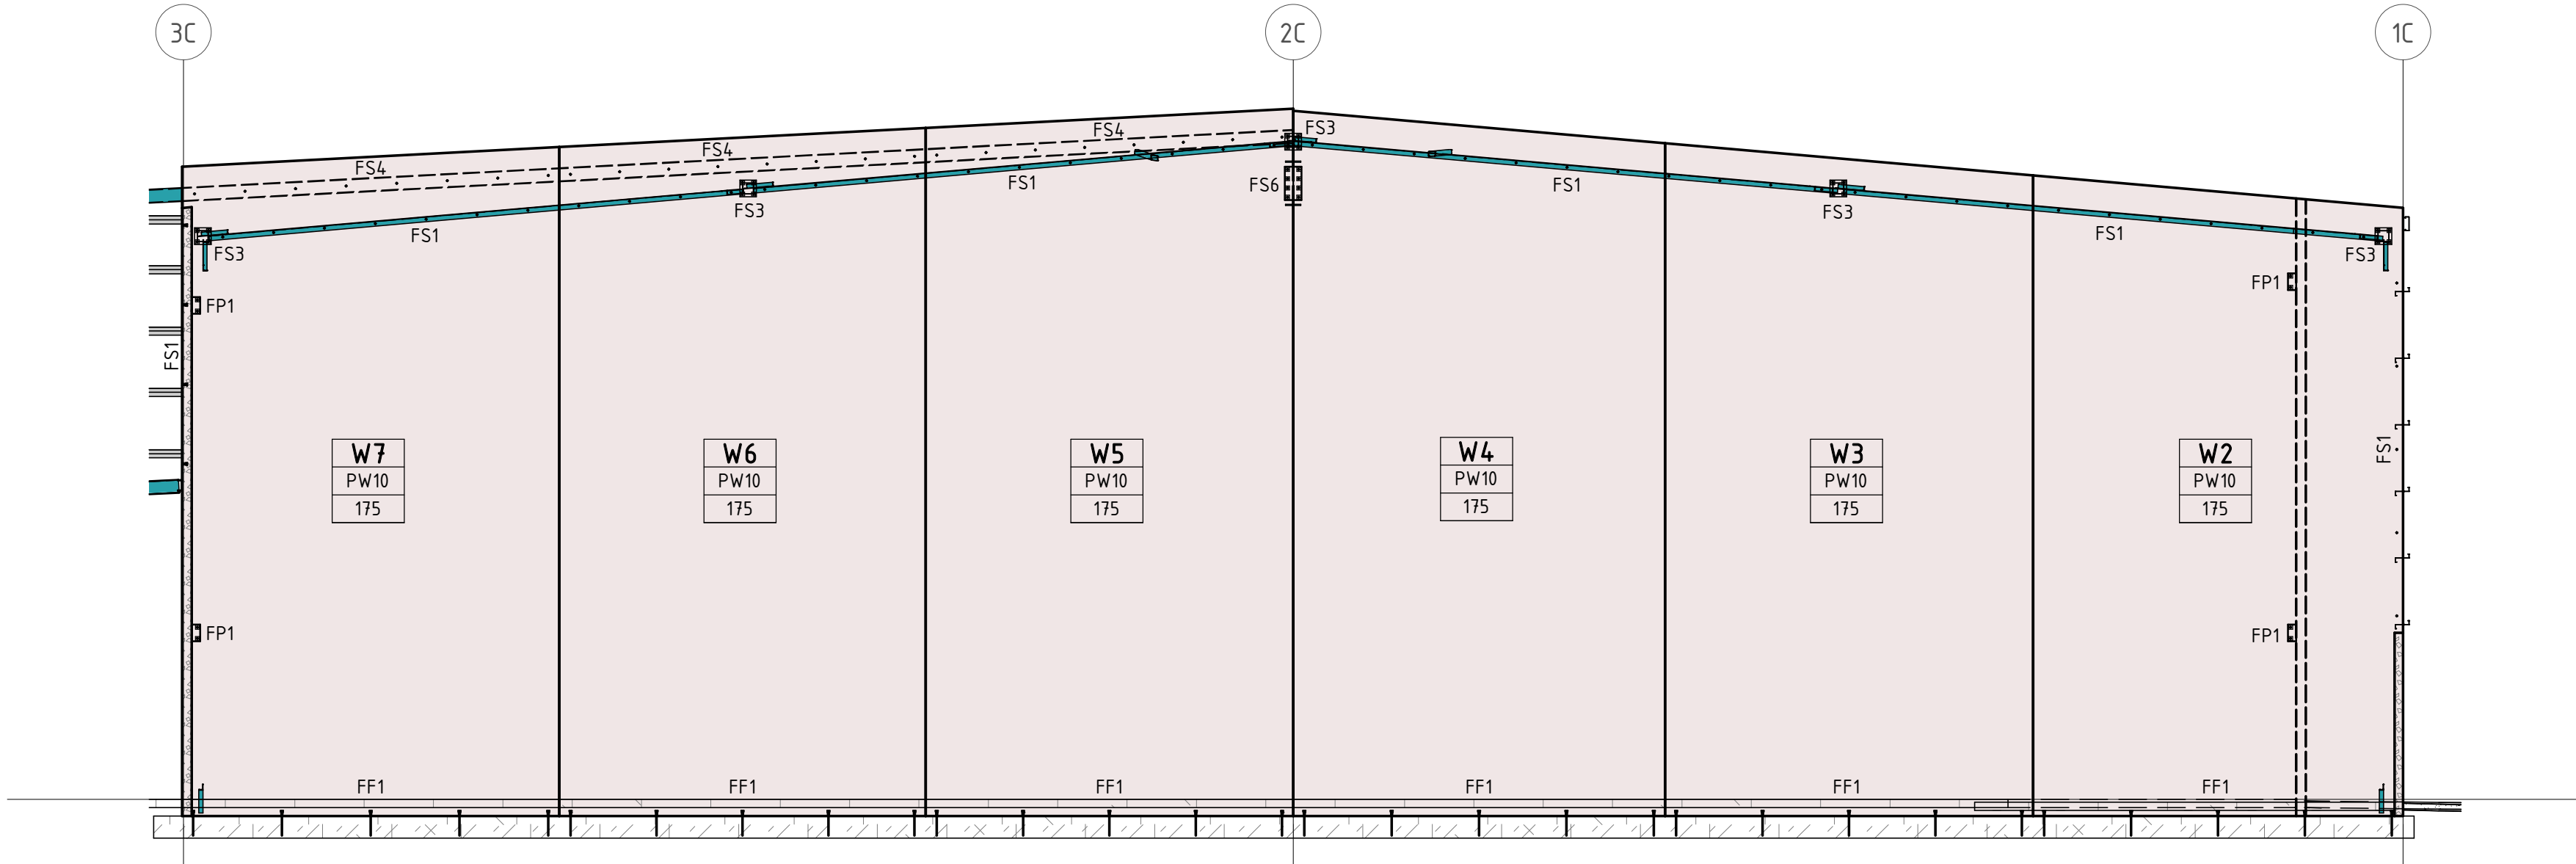


SECTION 2C
SCALE 1 : 100

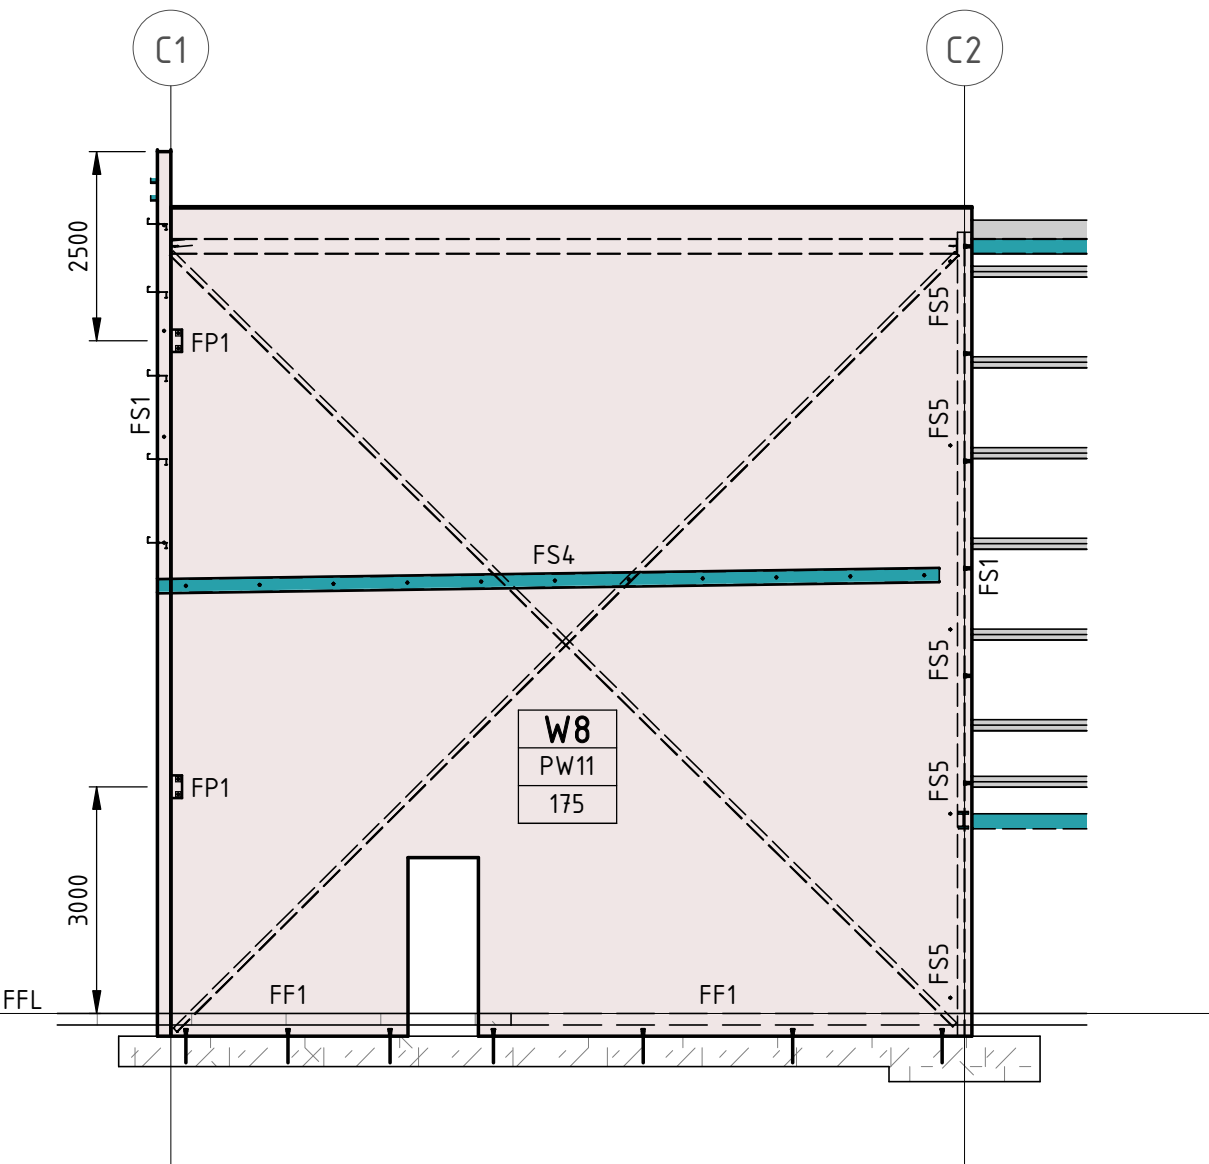


SECTION 3C
SCALE 1 : 100

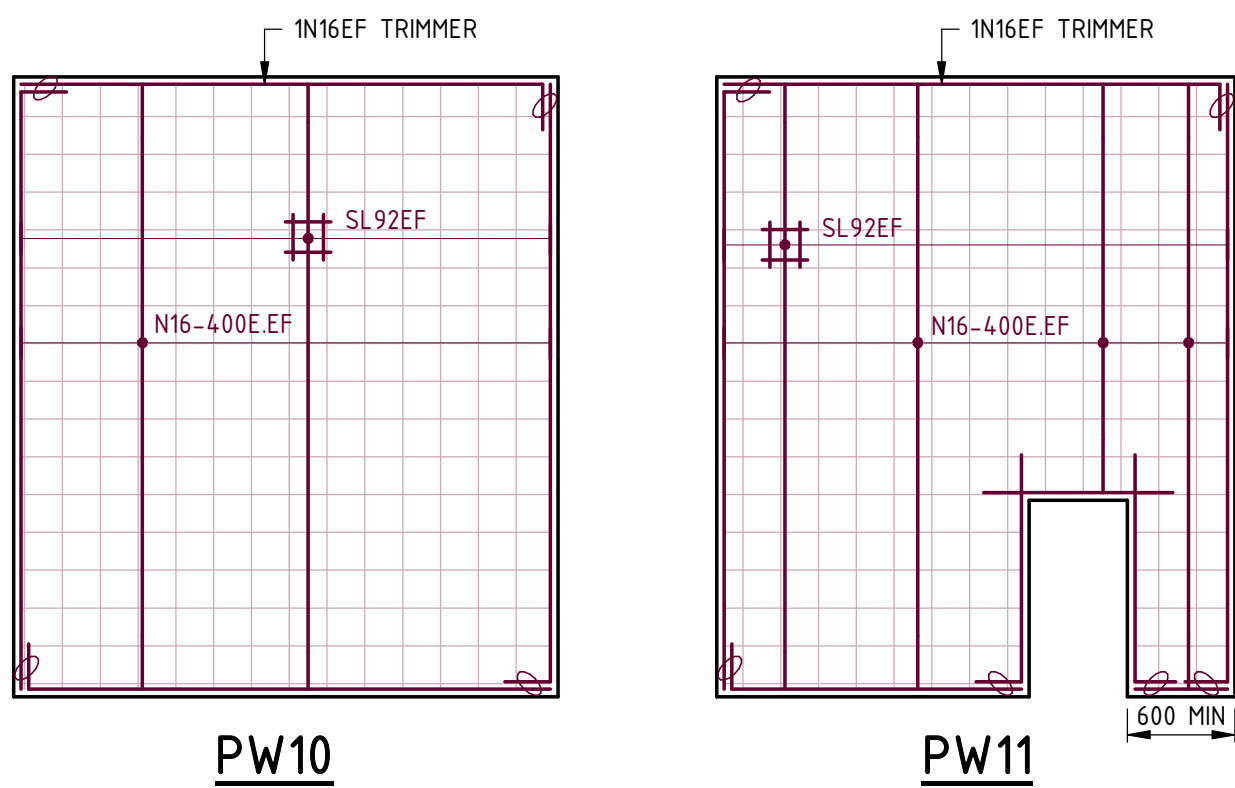


TYPICAL PRECAST TYPE DETAILS
SCALE 1 : 100

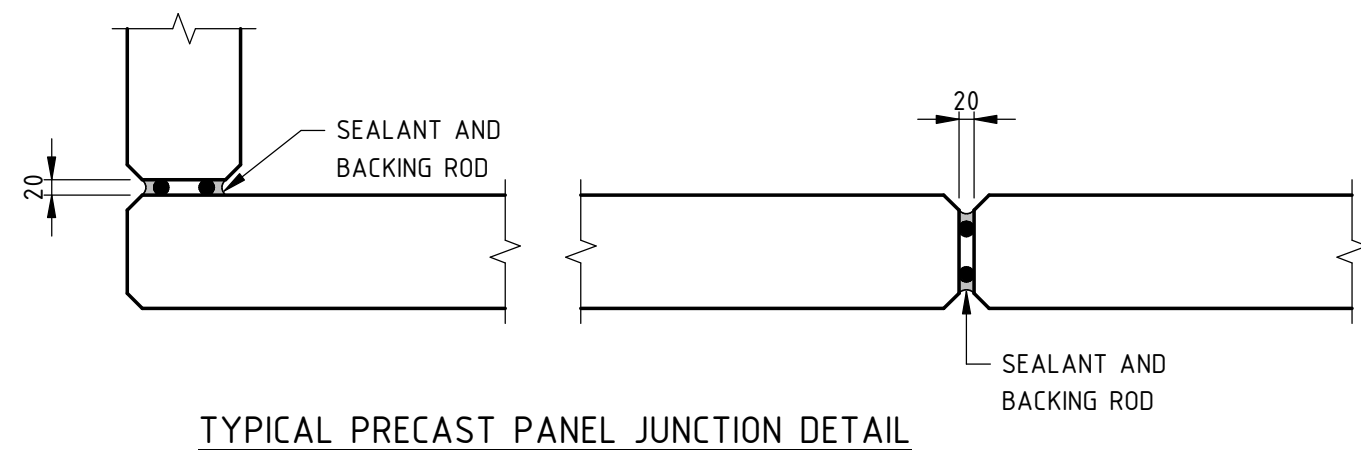


MARK FS1 - TYPICAL PANEL TO
PFC COLUMN FIXING DETAIL

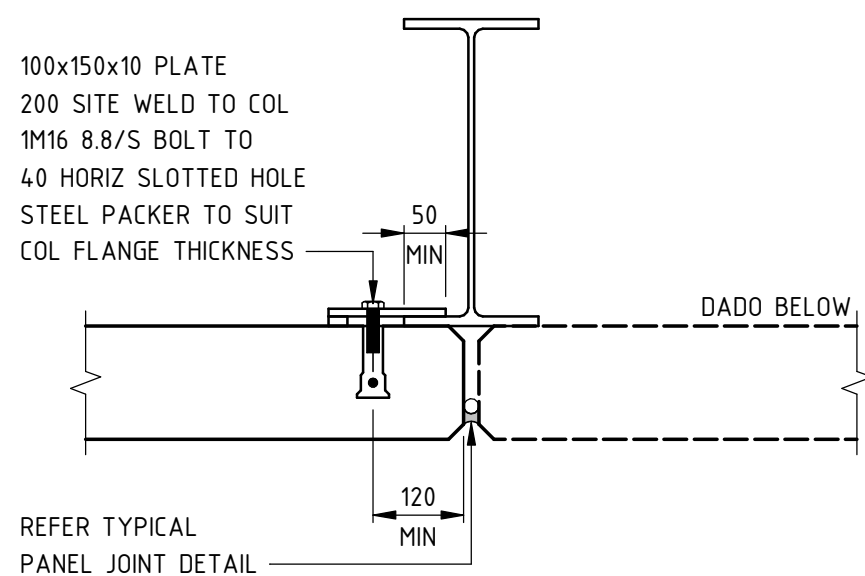


MARK FS5 PRECAST PANEL TO
RAKING ANGLE CONNECTION

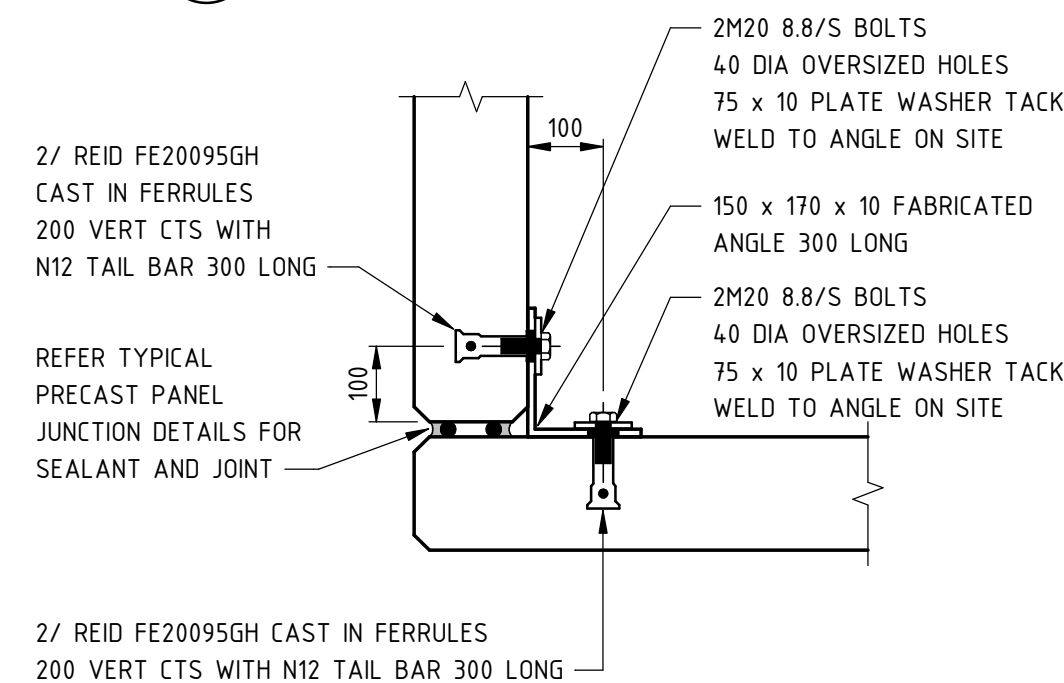


MARK FP1 PRECAST PANEL CORNER CLIP DETAIL

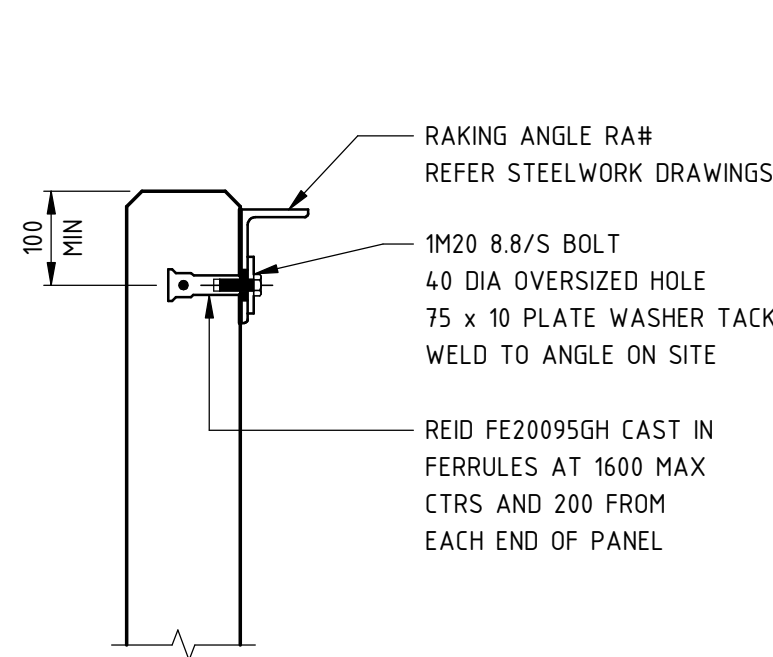


MARK FS2 PRECAST PANEL TO
RAKING ANGLE CONNECTION

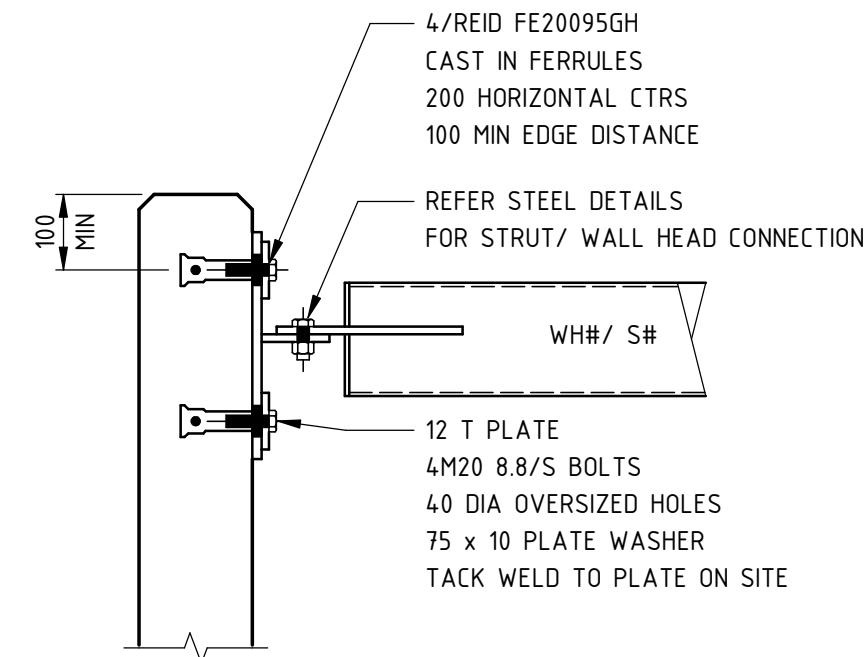


MARK FS3 STRUT/ WALL HEAD TO PRECAST PANEL

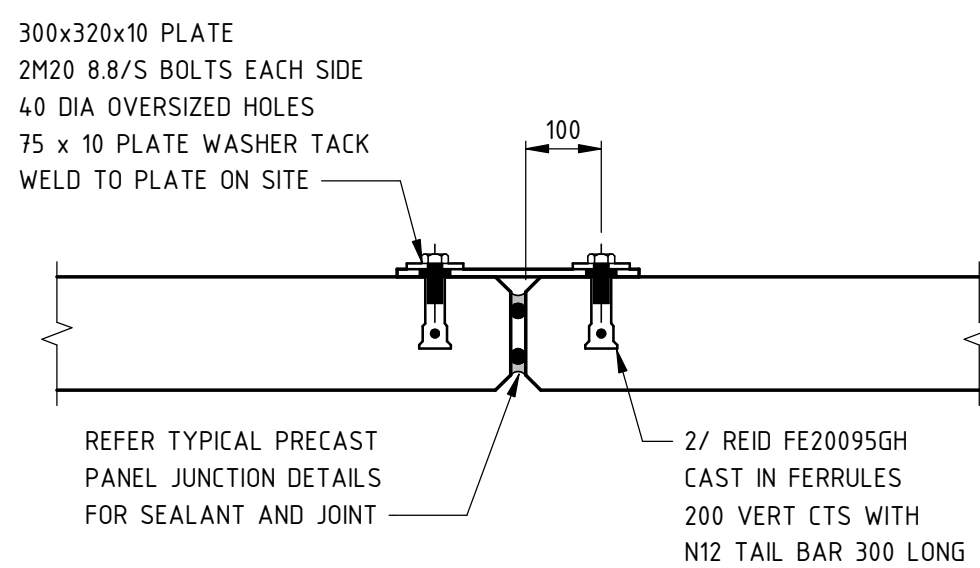


MARK FP2 PRECAST PANEL CLIP DETAIL

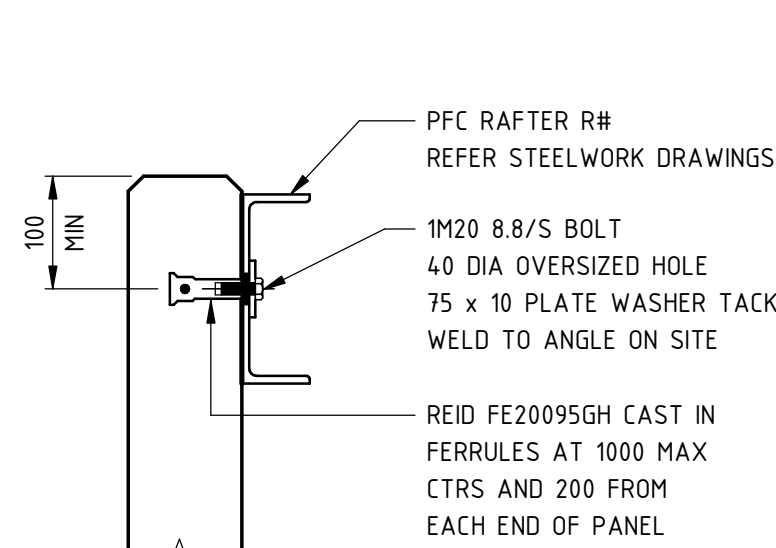

MARK FS4 PRECAST PANEL TO
RAKING ANGLE CONNECTION

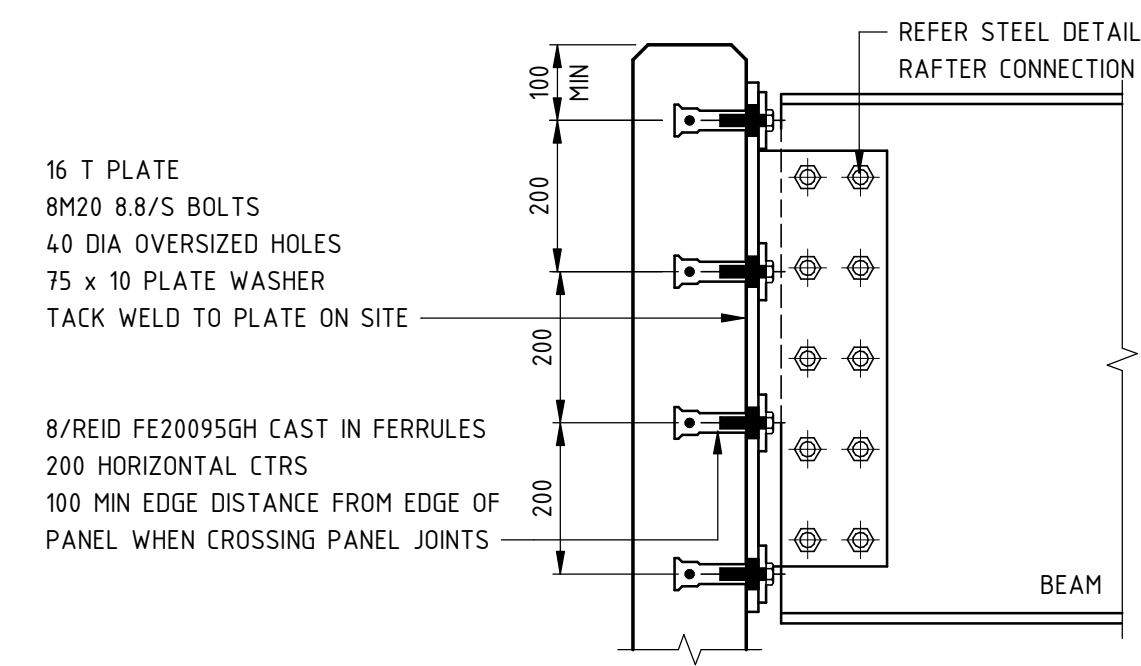

MARK FS6 PRECAST PANEL
TO TRANSFER BEAM

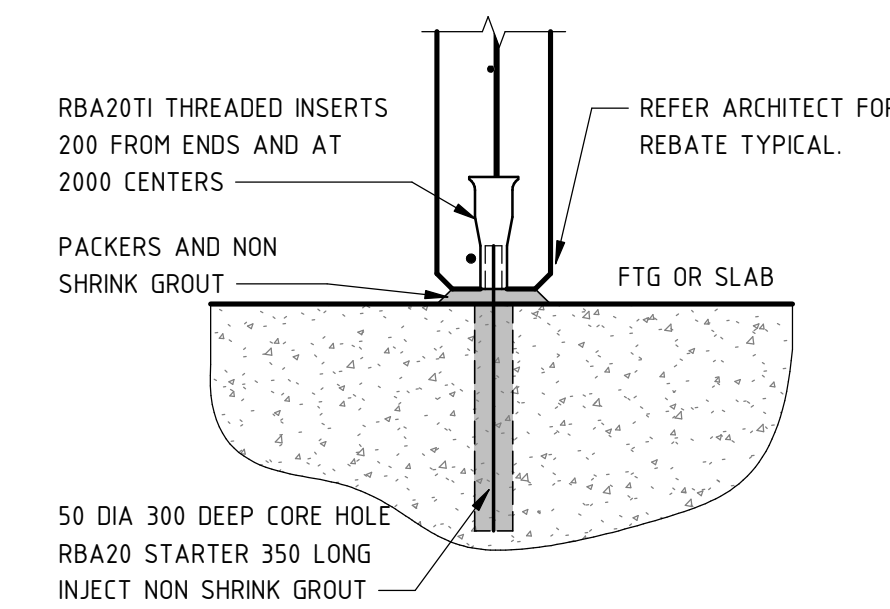

MARK FF1 PRECAST PANEL BASE DETAIL

PRECAST CONCRETE NOTES

1. REFER 00001-00002 FOR CONSTRUCTION NOTES
2. THE CLEAR CONCRETE COVER TO ALL REINFORCEMENT SHALL BE:


COMPONENT	COVER ALL SIDES
PRECAST	40

3. MINIMUM REINFORCEMENT BAR LAPS SHALL BE:


BAR SIZE	BAR LAP
N12	500
N16	600
N20	800
N24	1000
N28	1200
N32	1300
N36	1500

MESH LAP AS PER TYPICAL MESH LAP DETAIL FOR PRECAST

4. THE DESIGN OF THE PRECAST ALLOWS FOR A FIRE RATING OF 120/120/120MINUTES. REFER ARCHITECT FOR FIRE RATING REQUIREMENTS.
5. PROVIDE TEMPORARY PROPPING TO ALL PANELS DURING CONSTRUCTION. PROPPING TO BE DESIGNED AND CERTIFIED BY STRUCTURAL REQ.
6. ALL LIFTING POINTS ARE TO BE DESIGNED AND CERTIFIED BY PRECAST MANUFACTURER.
7. PANELS ARE DESIGNED FOR FINAL LOAD CASE. PRECAST MANUFACTURER TO PROVIDE ADDITIONAL REINFORCEMENT AND SUPPORTS TO ENABLE TRANSPORTATION AND ERECTION OF PRECAST PANELS.
8. CONNECTIONS INDICATED MAY BE NEAR FACE, FAR FACE OR EACH FACE. PRECAST SHOP DETAILER TO USE STEEL WORK AND CONCRETE SLAB PLANS TO CONFIRM CONNECTION LOCATIONS.
9. PANEL THICKNESS NOMINATED ON STRUCTURAL DRAWINGS IS THE MINIMUM STRUCTURAL THICKNESS. ALL ARCHITECTURAL REBATES, PATTERNS OR TEXTURES ARE ADDITIONAL.

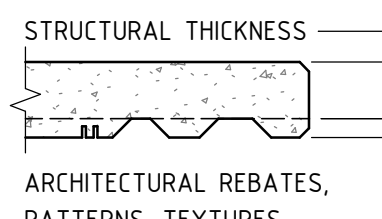

PRECAST CONCRETE LEGEND

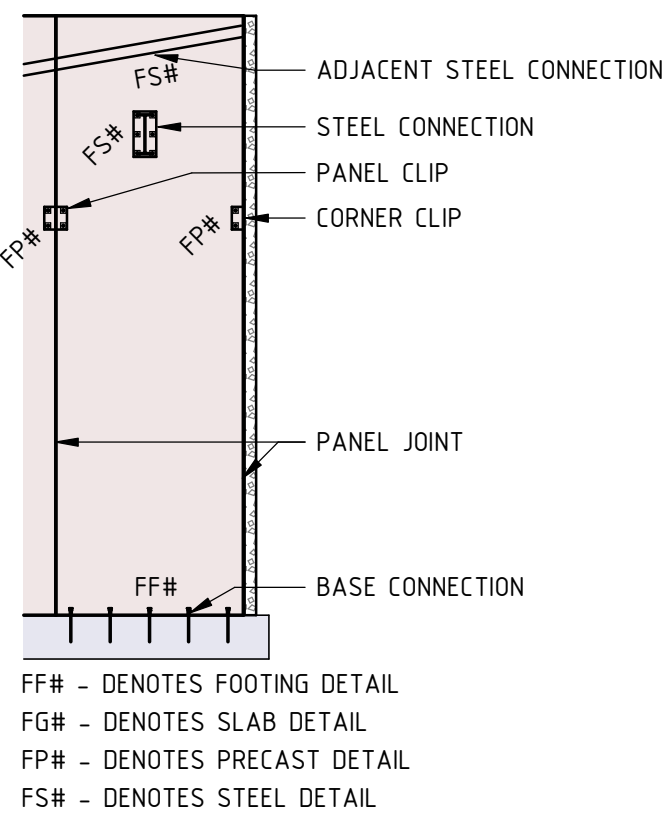

FF# - DENOTES FOOTING DETAIL
FG# - DENOTES SLAB DETAIL
FP# - DENOTES PRECAST DETAIL
FS# - DENOTES STEEL DETAIL

W#	WALL NUMBER
PW11	WALL TYPE REFER DRG S3.901
150	WALL THICKNESS

COPYRIGHT :
REPRODUCTION OF WHOLE OR PART OF THIS
DOCUMENT CONSTITUTES AN INFRINGEMENT
OF COPYRIGHT. THE INFORMATION, IDEAS,
AND CONCEPTS CONTAINED IN THIS
DOCUMENT ARE CONFIDENTIAL. THE
RECIPIENT(S) OF THIS DOCUMENT IS
PROHIBITED FROM DISCLOSING SUCH
INFORMATION IDEAS AND CONCEPTS TO ANY
PERSON WITHOUT THE PRIOR WRITTEN
CONSENT OF THE BRISBANE AIRPORT
CORPORATION PTY. LTD.

NS	BAC APPROVAL	11.06.26	A
DRN	AMENDMENTS	DATE	REV

NORTHROP
PROJECT NUMBER: 250946

Drawn: HP	Checked:
Design Coordinated: HP	Compliance Checked: --
Authorised For Issue: NS	Construction Checked: --

SKYGATE PLAY

TYPICAL PRECAST ELEVATIONS AND DETAILS

Brisbane Airport	BRISBANE AIRPORT CORPORATION PTY LTD 11 THE CIRCUIT, BRISBANE AIRPORT, QLD 4008, AUSTRALIA PO BOX 61, HAMILTON CENTRAL, QLD 4007, AUSTRALIA T: +61 7 3406 3000 E: INFO@BNE.COM.AU W: BNE.COM.AU	Scale: As indicated Size: A1 Revision: A
Drawing Number	Project No. Originator Volume Level Type Discipline Number	
25021	NOR - XX - 01 - DR - ST - 003501	