



SECTION C2
SCALE 1 : 200


SECTION C3
SCALE 1 : 200

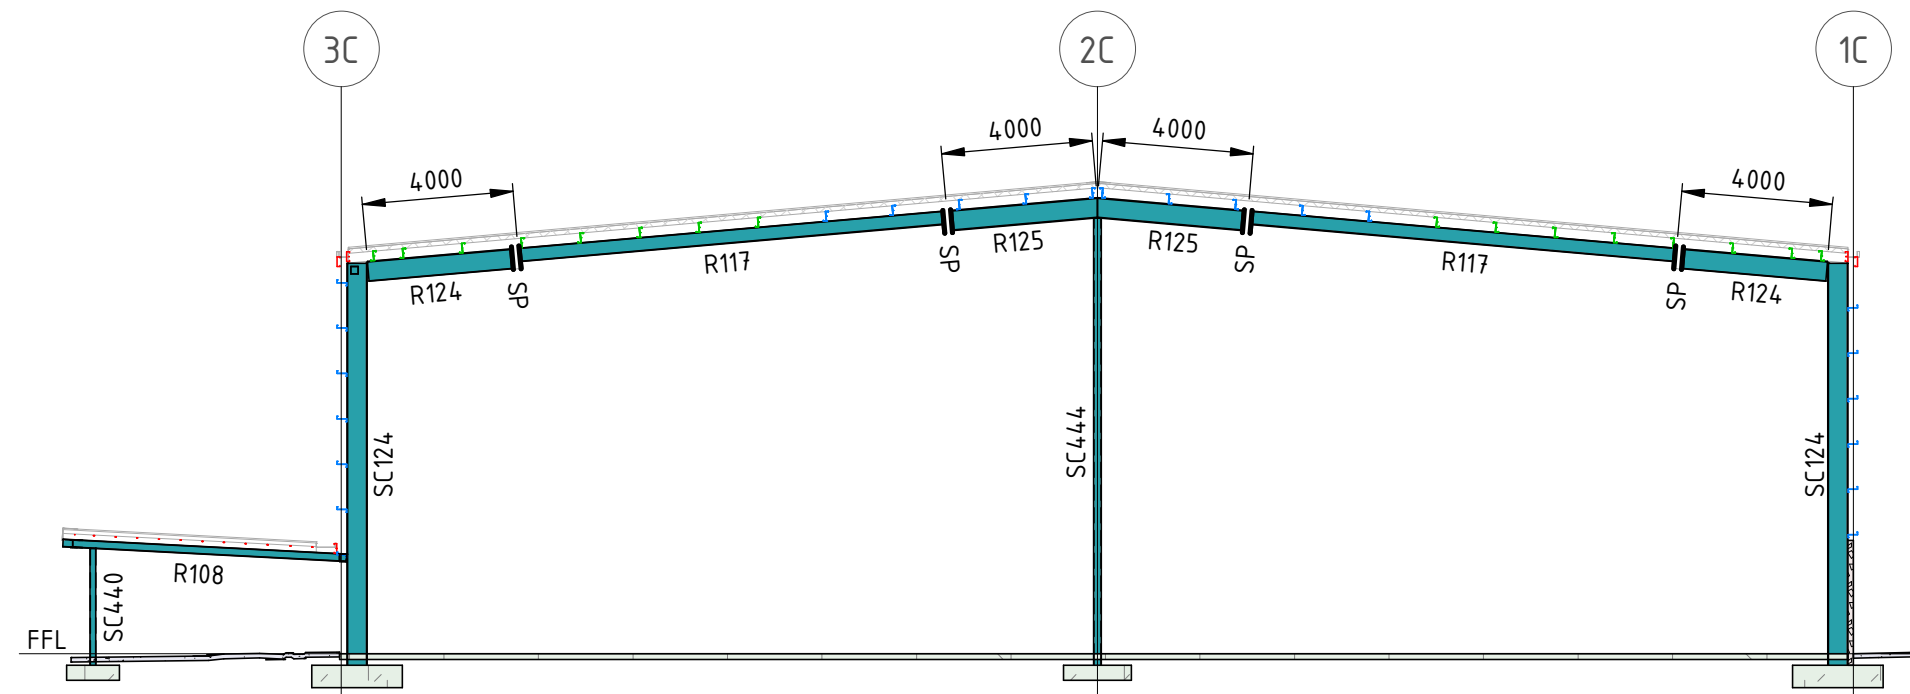


SECTION C4
SCALE 1 : 200

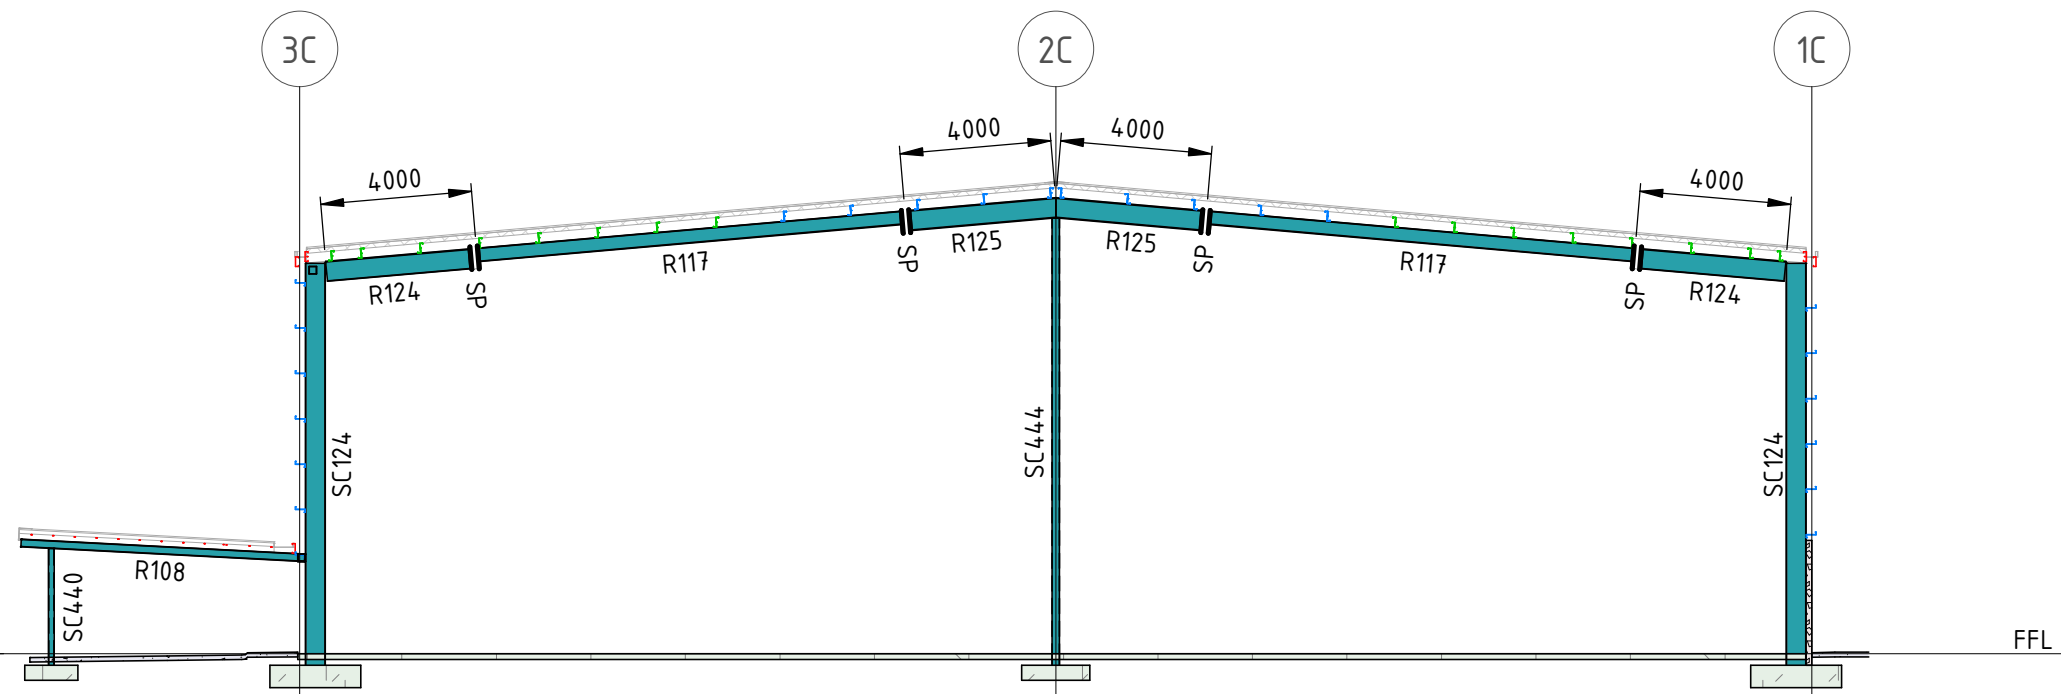


SECTION C5
SCALE 1 : 200

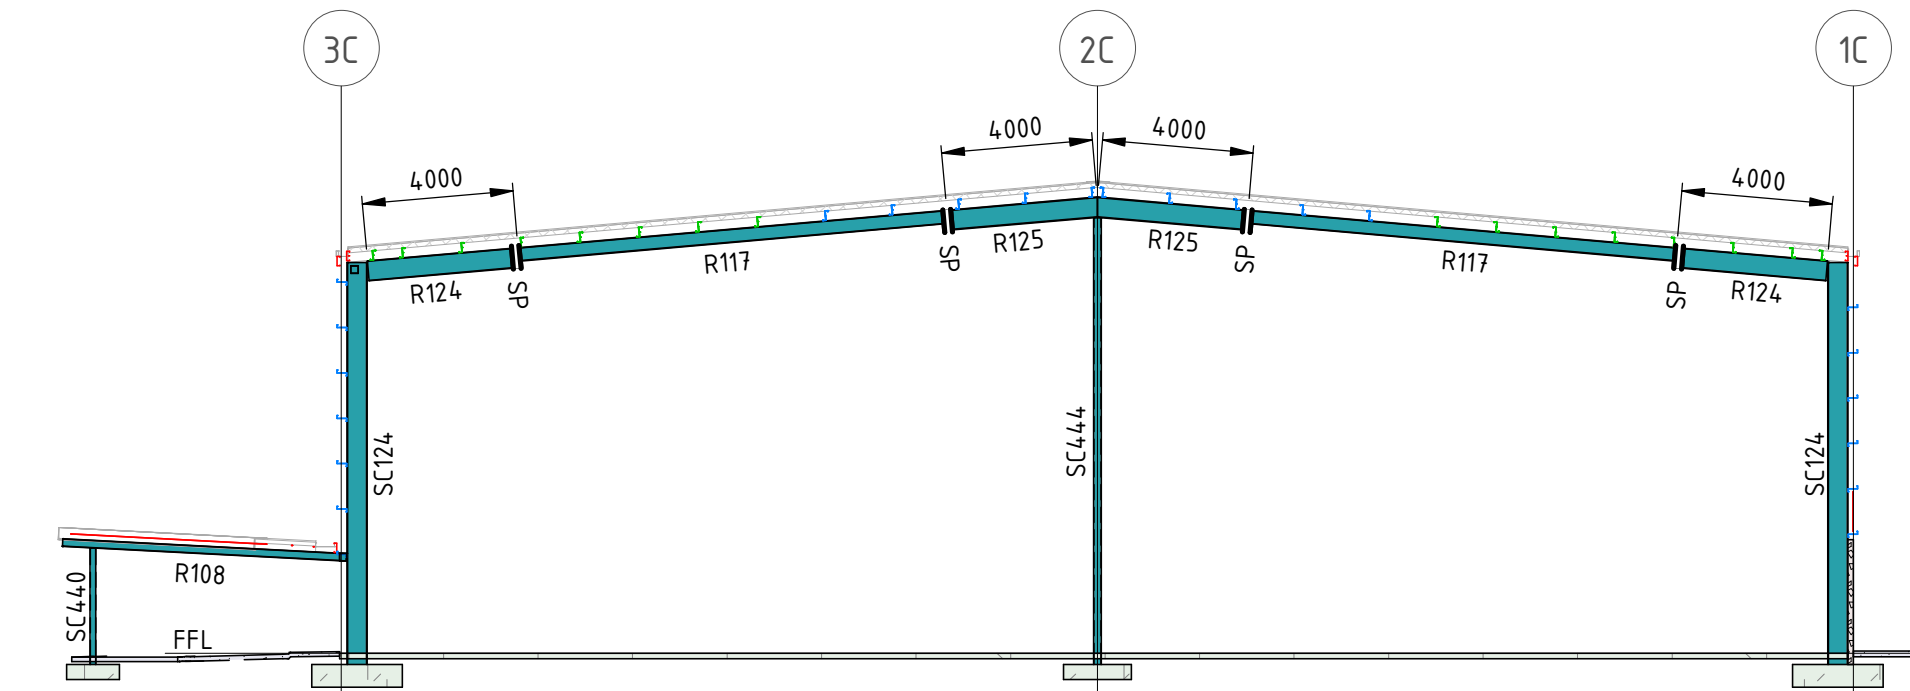


SECTION C6
SCALE 1 : 200

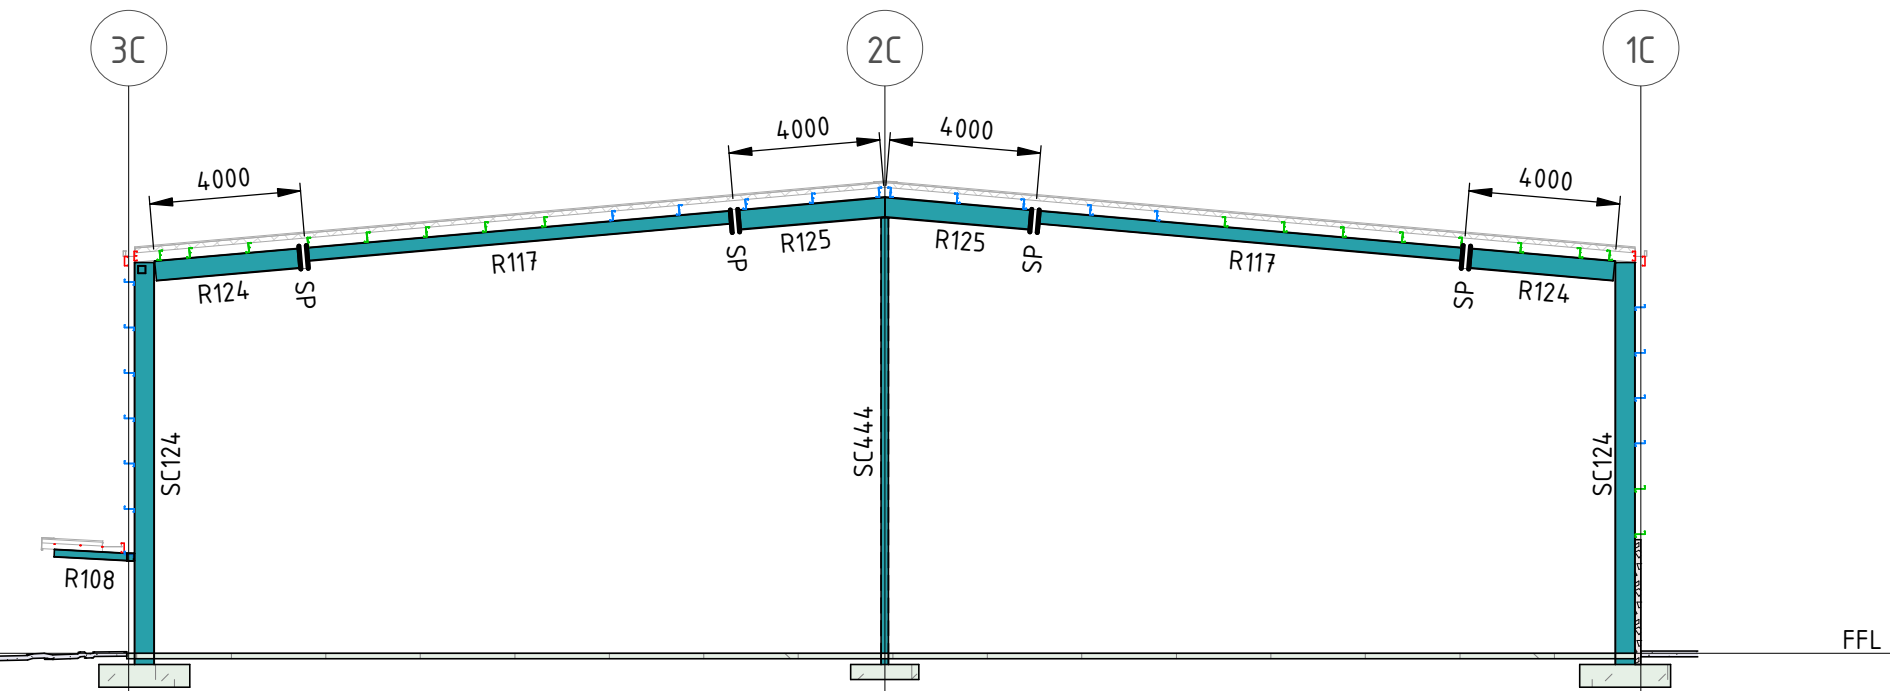


SECTION C7
SCALE 1 : 200

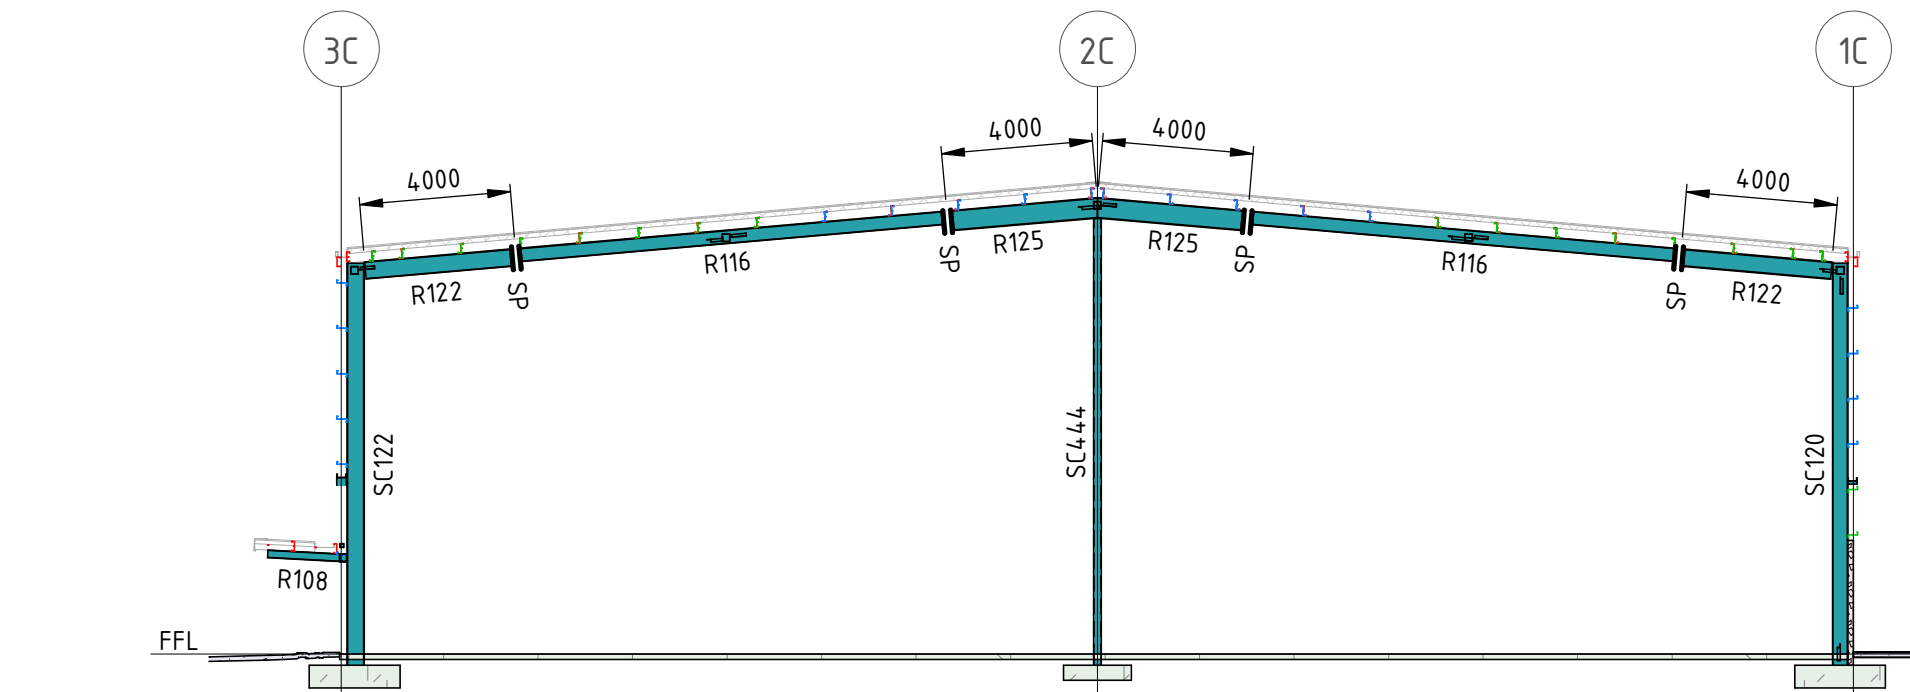

SECTION C8
SCALE 1 : 200

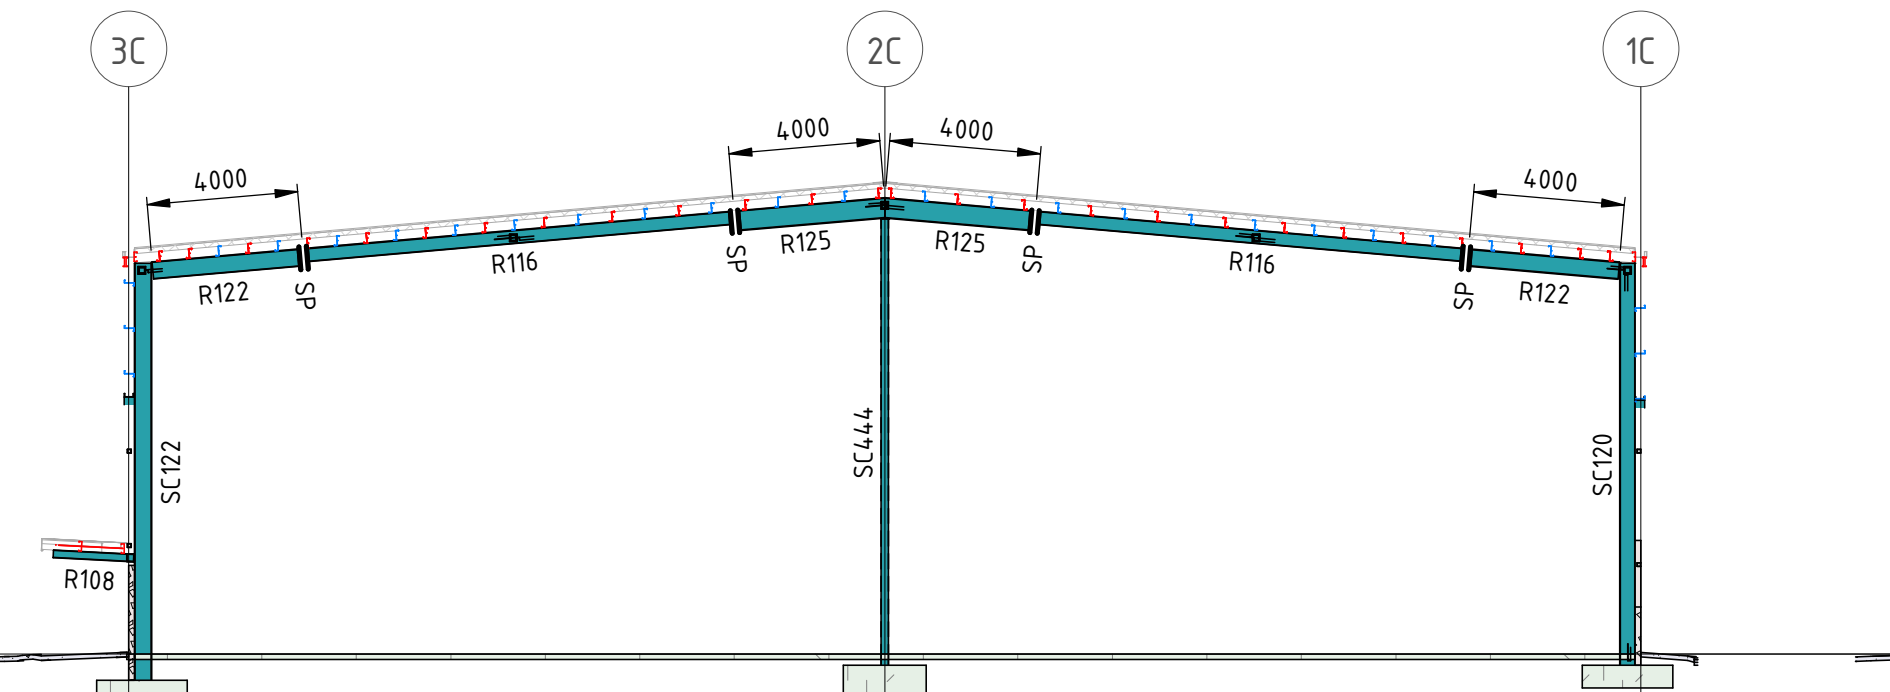

SECTION C9
SCALE 1 : 200

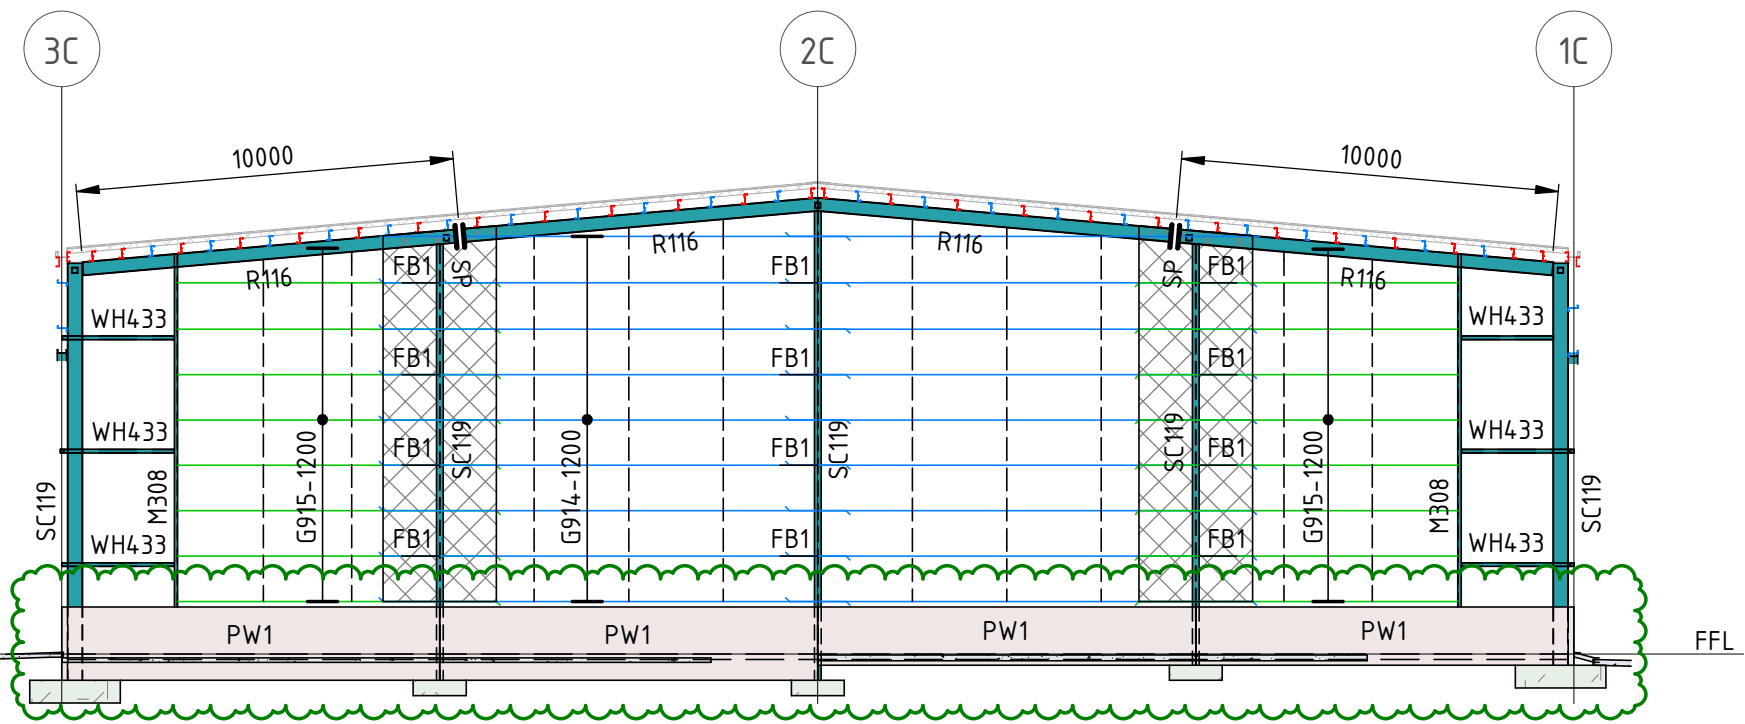


SECTION C10
SCALE 1 : 200

MEMBER SCHEDULE	
MARK	SIZE
COLUMN	
SC119	410 UB 53.7
SC120	410 UB 59.7
SC122	460 UB 74.6
SC124	530 UB 82.0
SC440	150 x 150 x 5.0 SHS
SC444	200 x 200 x 6.0 SHS
SC446	250 x 250 x 6.0 SHS
MULLION	
M308	250 PFC
M433	100 x 100 x 5.0 SHS
BEAM	
B306	200 PFC
B308	250 PFC
OUTRIGGER	
OR308	250 PFC
RAFTER	
R108	200 UB 25.4
R116	360 UB 44.7
R117	360 UB 50.7
R122	460 UB 74.6
R124	530 UB 82.0
R125	530 UB 92.4
ROOF BRACING	
RB249	89x89x5.0SHS
RB725	75 x 75 x 8 EA
STRUT	
S440	150x150x5.0SHS
S444	200x200x6.0SHS
TRANSFER BEAM	
TB136	800 WB 146
WALL BRACING	
WB725	75 x 75 x 8 EA
WALL HEAD	
WH433	100x100x5.0SHS
GIRT	
G914	EZ250-15
G915	EZ250-19
G946	EC250-24
PURLIN	
P914	EZ250-15
P915	EZ250-19
P916	EZ250-24
P946	EC250-24

ELEVATIONS AND SECTIONS NOTES

- REFER S0.001-S0.003 FOR CONSTRUCTION NOTES
- ALL PURLINS AND GIRTS TO BE STRAMIT EXACTA. ANY ALTERNATIVE TO BE APPROVED BY NORTHROP CONSULTING ENGINEERS PRIOR TO FABRICATION.
- REFER ARCHITECTURAL DRAWINGS FOR ALL ROOF PENETRATION LOCATIONS.
- THE EXACT LOCATION OF PENETRATION TRIMMING PURLIN AND GIRTS ARE TO BE CONFIRMED WITH SERVICE PROVIDER PRIOR TO FABRICATION.

ELEVATIONS AND SECTIONS LEGEND

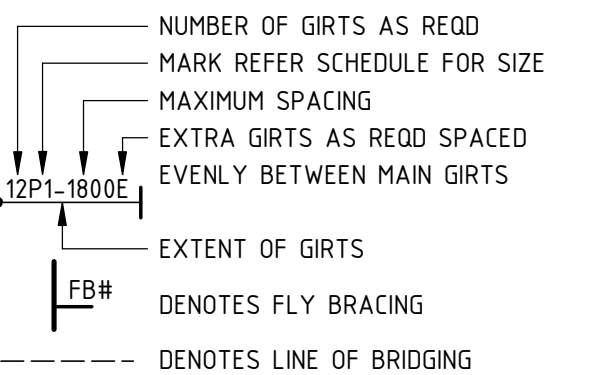

- GIRT COLOURS**
- REFER MEMBER SCHEDULE FOR SIZE MARKS
- 1.0mm C/Z GIRT THICKNESS
 - 1.2mm C/Z GIRT THICKNESS
 - 1.5mm C/Z GIRT THICKNESS
 - 1.9mm C/Z GIRT THICKNESS
 - 2.4mm C/Z GIRT THICKNESS
 - 3.0mm C/Z GIRT THICKNESS

- GIRT LAPS**
- ALL GIRT LAPS TO BE 15% OF THE LARGEST ADJACENT SPAN UNLESS NOTED OTHERWISE
- DENOTES GIRT LAPS TO BE 20% OF LARGEST ADJACENT SPAN
 - DENOTES GIRT LAPS TO BE 25% OF LARGEST ADJACENT SPAN
 - DENOTES GIRT LAPS TO BE 30% OF LARGEST ADJACENT SPAN
 - DENOTES GIRT LAPS TO BE 35% OF LARGEST ADJACENT SPAN

COPYRIGHT : REPRODUCTION OF WHOLE OR PART OF THIS DOCUMENT CONSTITUTES AN INFRINGEMENT OF COPYRIGHT. THE INFORMATION, IDEAS, AND CONCEPTS CONTAINED IN THIS DOCUMENT ARE CONFIDENTIAL. THE RECIPIENT(S) OF THIS DOCUMENT IS PROHIBITED FROM DISCLOSING SUCH INFORMATION IDEAS AND CONCEPTS TO ANY PERSON WITHOUT THE PRIOR WRITTEN CONSENT OF THE BRISBANE AIRPORT CORPORATION PTY. LTD.							
NS	BAC APPROVAL	11.06.26	C				
NS	STEEL DETAILS ISSUE	04.06.26	B				
NS	PRELIM STEEL ISSUE	29.05.26	A				
DRN	AMENDMENTS	DATE	REV				

NORTHROP
PROJECT NUMBER: 250946

Drawn: HP	Checked:
Design Coordinated: HP	Compliance Checked: --
Authorised For Issue: NS	Construction Checked: --

SKYGATE PLAY
BUILDING SECTIONS - SHEET 5

 Brisbane Airport		BRISBANE AIRPORT CORPORATION PTY LTD 11 THE CIRCUIT, BRISBANE AIRPORT, QLD, 4008, AUSTRALIA PO BOX 61, HAMILTON CENTRAL, QLD, 4007, AUSTRALIA T: +61 7 3408 3000 E: INFO@BNE.COM.AU W: BNE.COM.AU					Scale: As indicated Size: A1 Revision: C
Drawing Number	Project No.	Originator	Volume	Level	Type	Discipline	Number
	25021	- NOR	XX	01	DR	ST	00650