



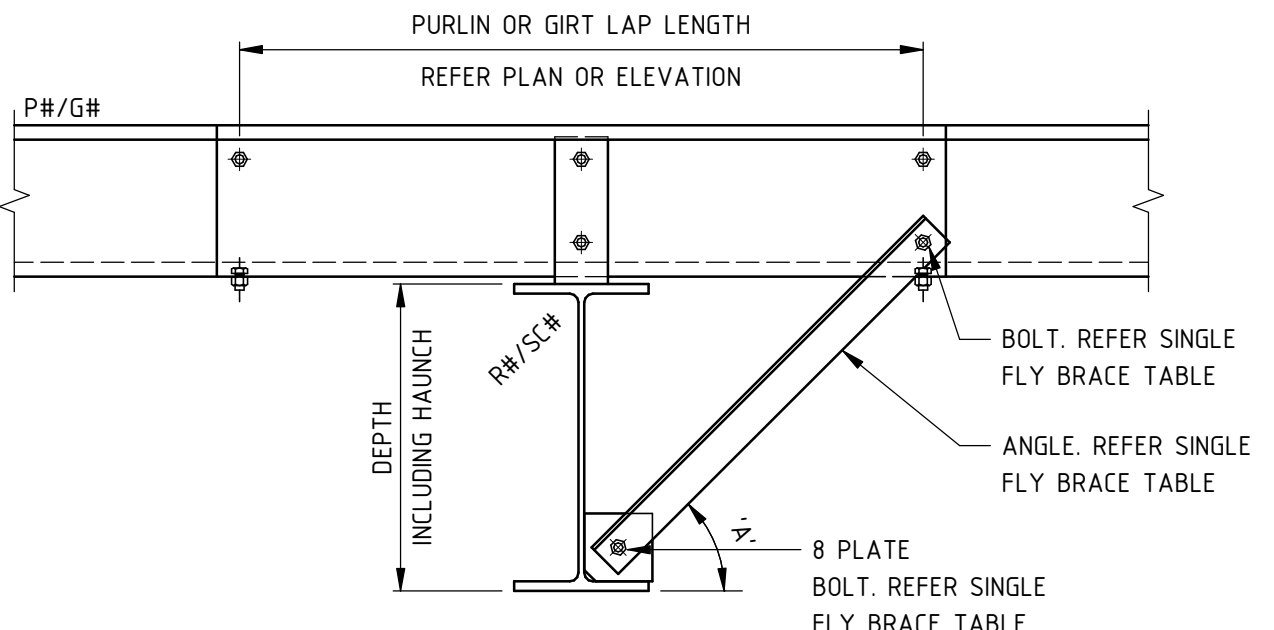

TYPICAL FLY BRACE (FB1)
SINGLE SIDE FIXING DETAIL

SINGLE FLY BRACE TABLE		
DEPTH	ANGLE	BOLT
UP TO 420	40 x 5 EA	1M12 8.8/S
421 TO 795	65 x 5 EA	1M16 8.8/S


MAXIMUM MEMBER SIZE FOR THIS DETAIL 800WB122
MAXIMUM FLY BRACE ANGLE 'A' = 45°

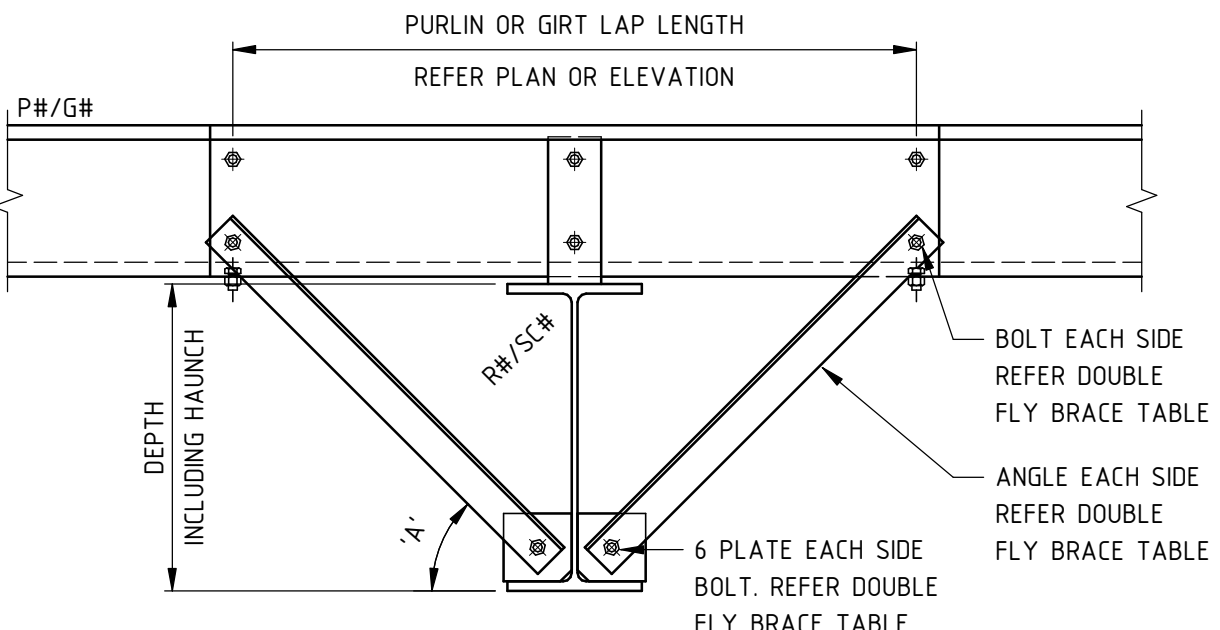


TYPICAL FLY BRACE (FB2)
DOUBLE SIDE FIXING DETAIL

DOUBLE FLY BRACE TABLE		
DEPTH	ANGLE	BOLT
UP TO 320	40 x 5 EA	1M12 8.8/S
321 TO 620	50 x 5 EA	1M12 8.8/S
621 TO 900	65 x 5 EA	1M16 8.8/S


MAXIMUM MEMBER SIZE FOR THIS DETAIL 900WB175
MAXIMUM FLY BRACE ANGLE 'A' = 45°

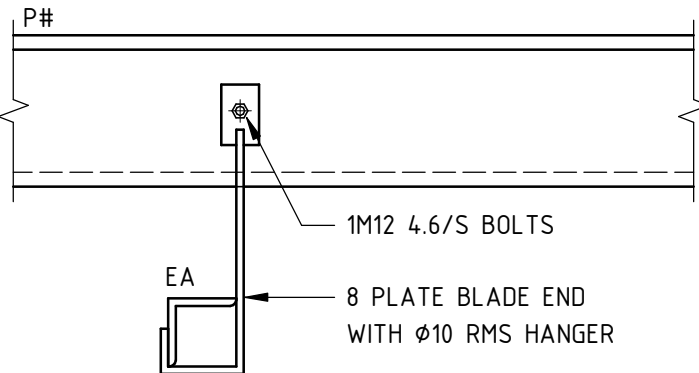


TYPICAL EA SAG ROD DETAIL

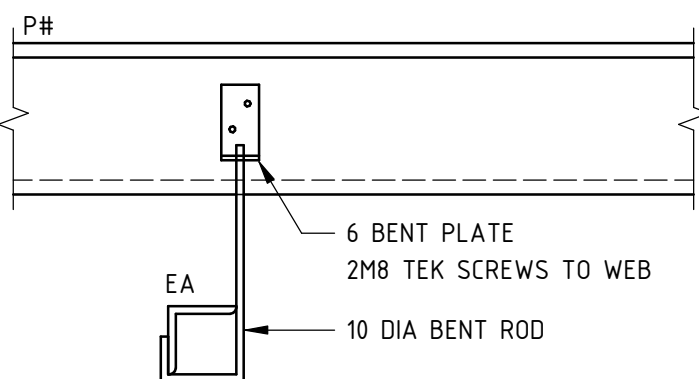


TYPICAL EA SAG ROD DETAIL

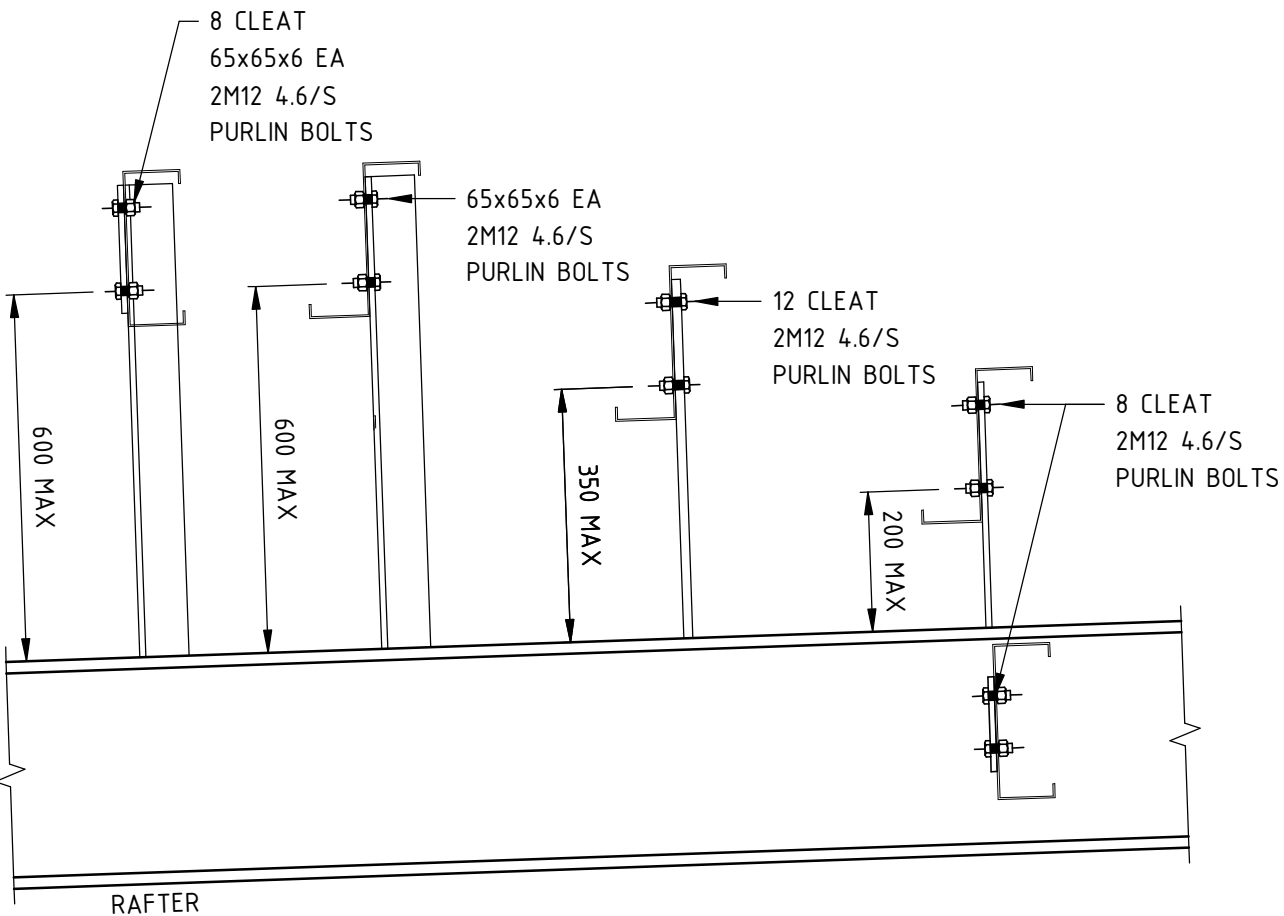

TYPICAL PURLIN AND CEILING JOIST CLEAT DETAIL
100 TO 250 PURLINS, C PURLINS SIMILAR

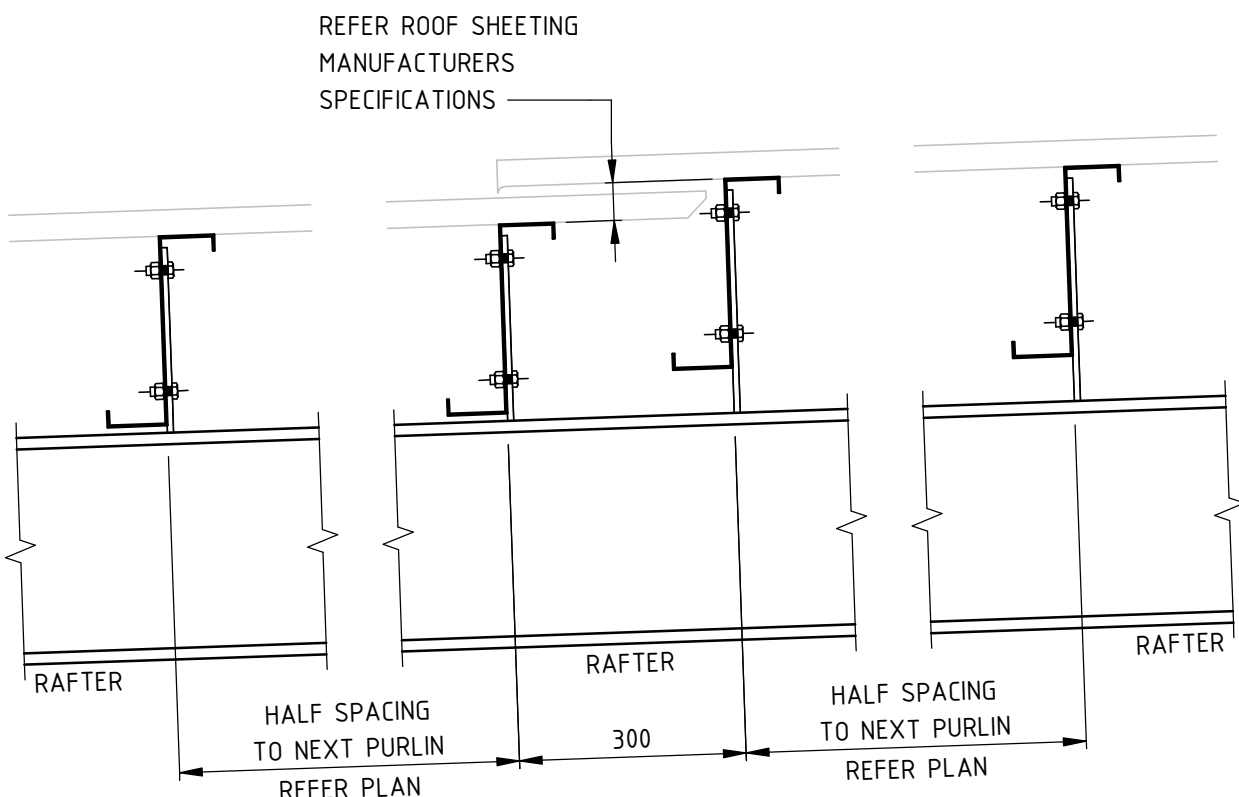


TYPICAL ROOF EXPANSION JOINT DETAIL

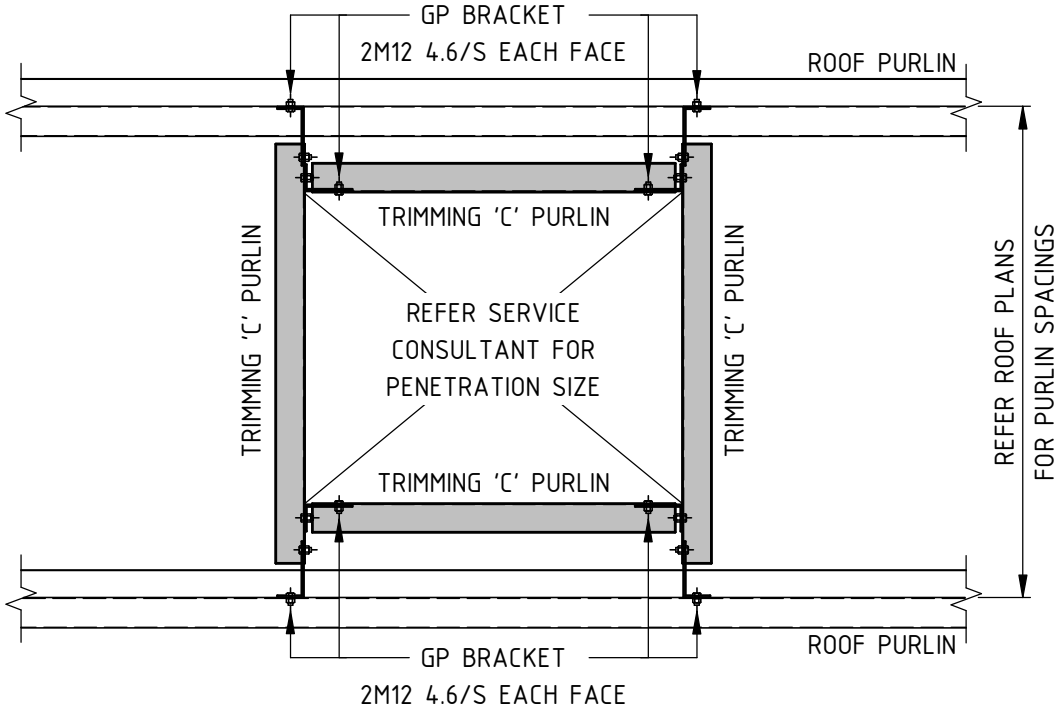

TYPICAL ROOF PENETRATION TRIMMING DETAIL

SCALE 1:20
· TRIMMING PURLINS N.S.O.P.
· TRIMMING PURLINS TO BE 24 GAUGE AND SAME DEPTH AS ROOF PURLINS
· REFER SERVICE PROVIDER FOR PENETRATION LOCATION AND SIZE.
· THIS DETAIL ONLY APPLIES TO PENETRATIONS SMALLER THAN ROOF PURLIN SPACINGS

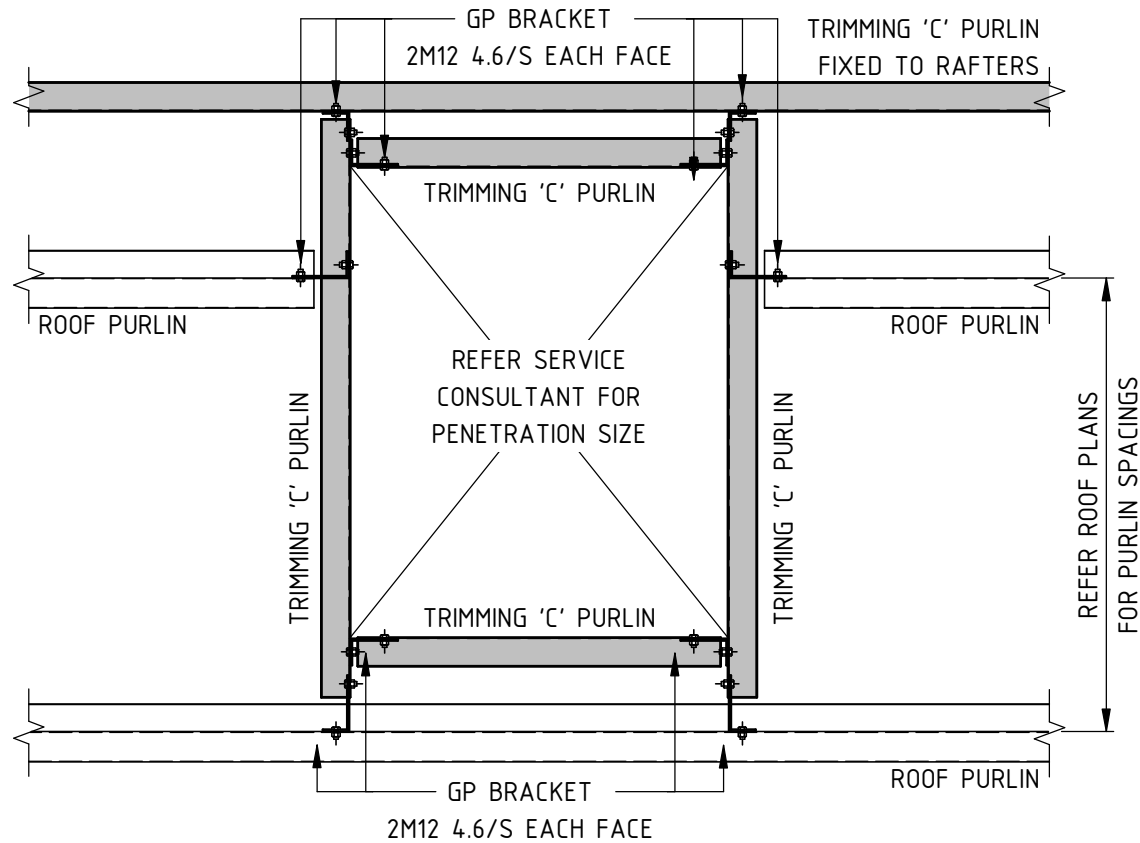

TYPICAL ROOF PENETRATION TRIMMING DETAIL

SCALE 1:20
· TRIMMING PURLINS N.S.O.P.
· TRIMMING PURLINS TO BE 24 GAUGE AND SAME DEPTH AS ROOF PURLINS
· REFER SERVICE PROVIDER FOR PENETRATION LOCATION AND SIZE.
· 1 ROOF PURLIN MAXIMUM TO BE CUT.

COPYRIGHT :
REPRODUCTION OF WHOLE OR PART OF THIS
DOCUMENT CONSTITUTES AN INFRINGEMENT
OF COPYRIGHT. THE INFORMATION, IDEAS,
AND CONCEPTS CONTAINED IN THIS
DOCUMENT ARE CONFIDENTIAL. THE
RECIPIENT(S) OF THIS DOCUMENT IS
PROHIBITED FROM DISCLOSING SUCH
INFORMATION IDEAS AND CONCEPTS TO ANY
PERSON WITHOUT THE PRIOR WRITTEN
CONSENT OF THE BRISBANE AIRPORT
CORPORATION PTY. LTD.

NS	BAC APPROVAL	11.06.26	B
NS	STEEL DETAILS ISSUE	04.06.26	A
DRN	AMENDMENTS	DATE	REV

NORTHROP
PROJECT NUMBER: 250946

Drawn: HP	Checked:
Design Coordinated: HP	Compliance Checked: --
Authorised For Issue: NS	Construction Checked: --

SKYGATE PLAY

TYPICAL STEEL DETAILS SHEET 5

	BRISBANE AIRPORT CORPORATION PTY LTD 11 THE CIRCUIT, BRISBANE AIRPORT, QLD 4008, AUSTRALIA PO BOX 61, HAMILTON CENTRAL, QLD 4507, AUSTRALIA T: +61 7 3406 3000 E: INFO@BNE.COM.AU W: BNE.COM.AU							Scale: As indicated
								Size: A1
								Revision: B
Drawing Number	Project No.	Originator	Volume	Level	Type	Discipline	Number	
	25021	- NOR	- XX	- 01	- DR	- ST	- 006905	