


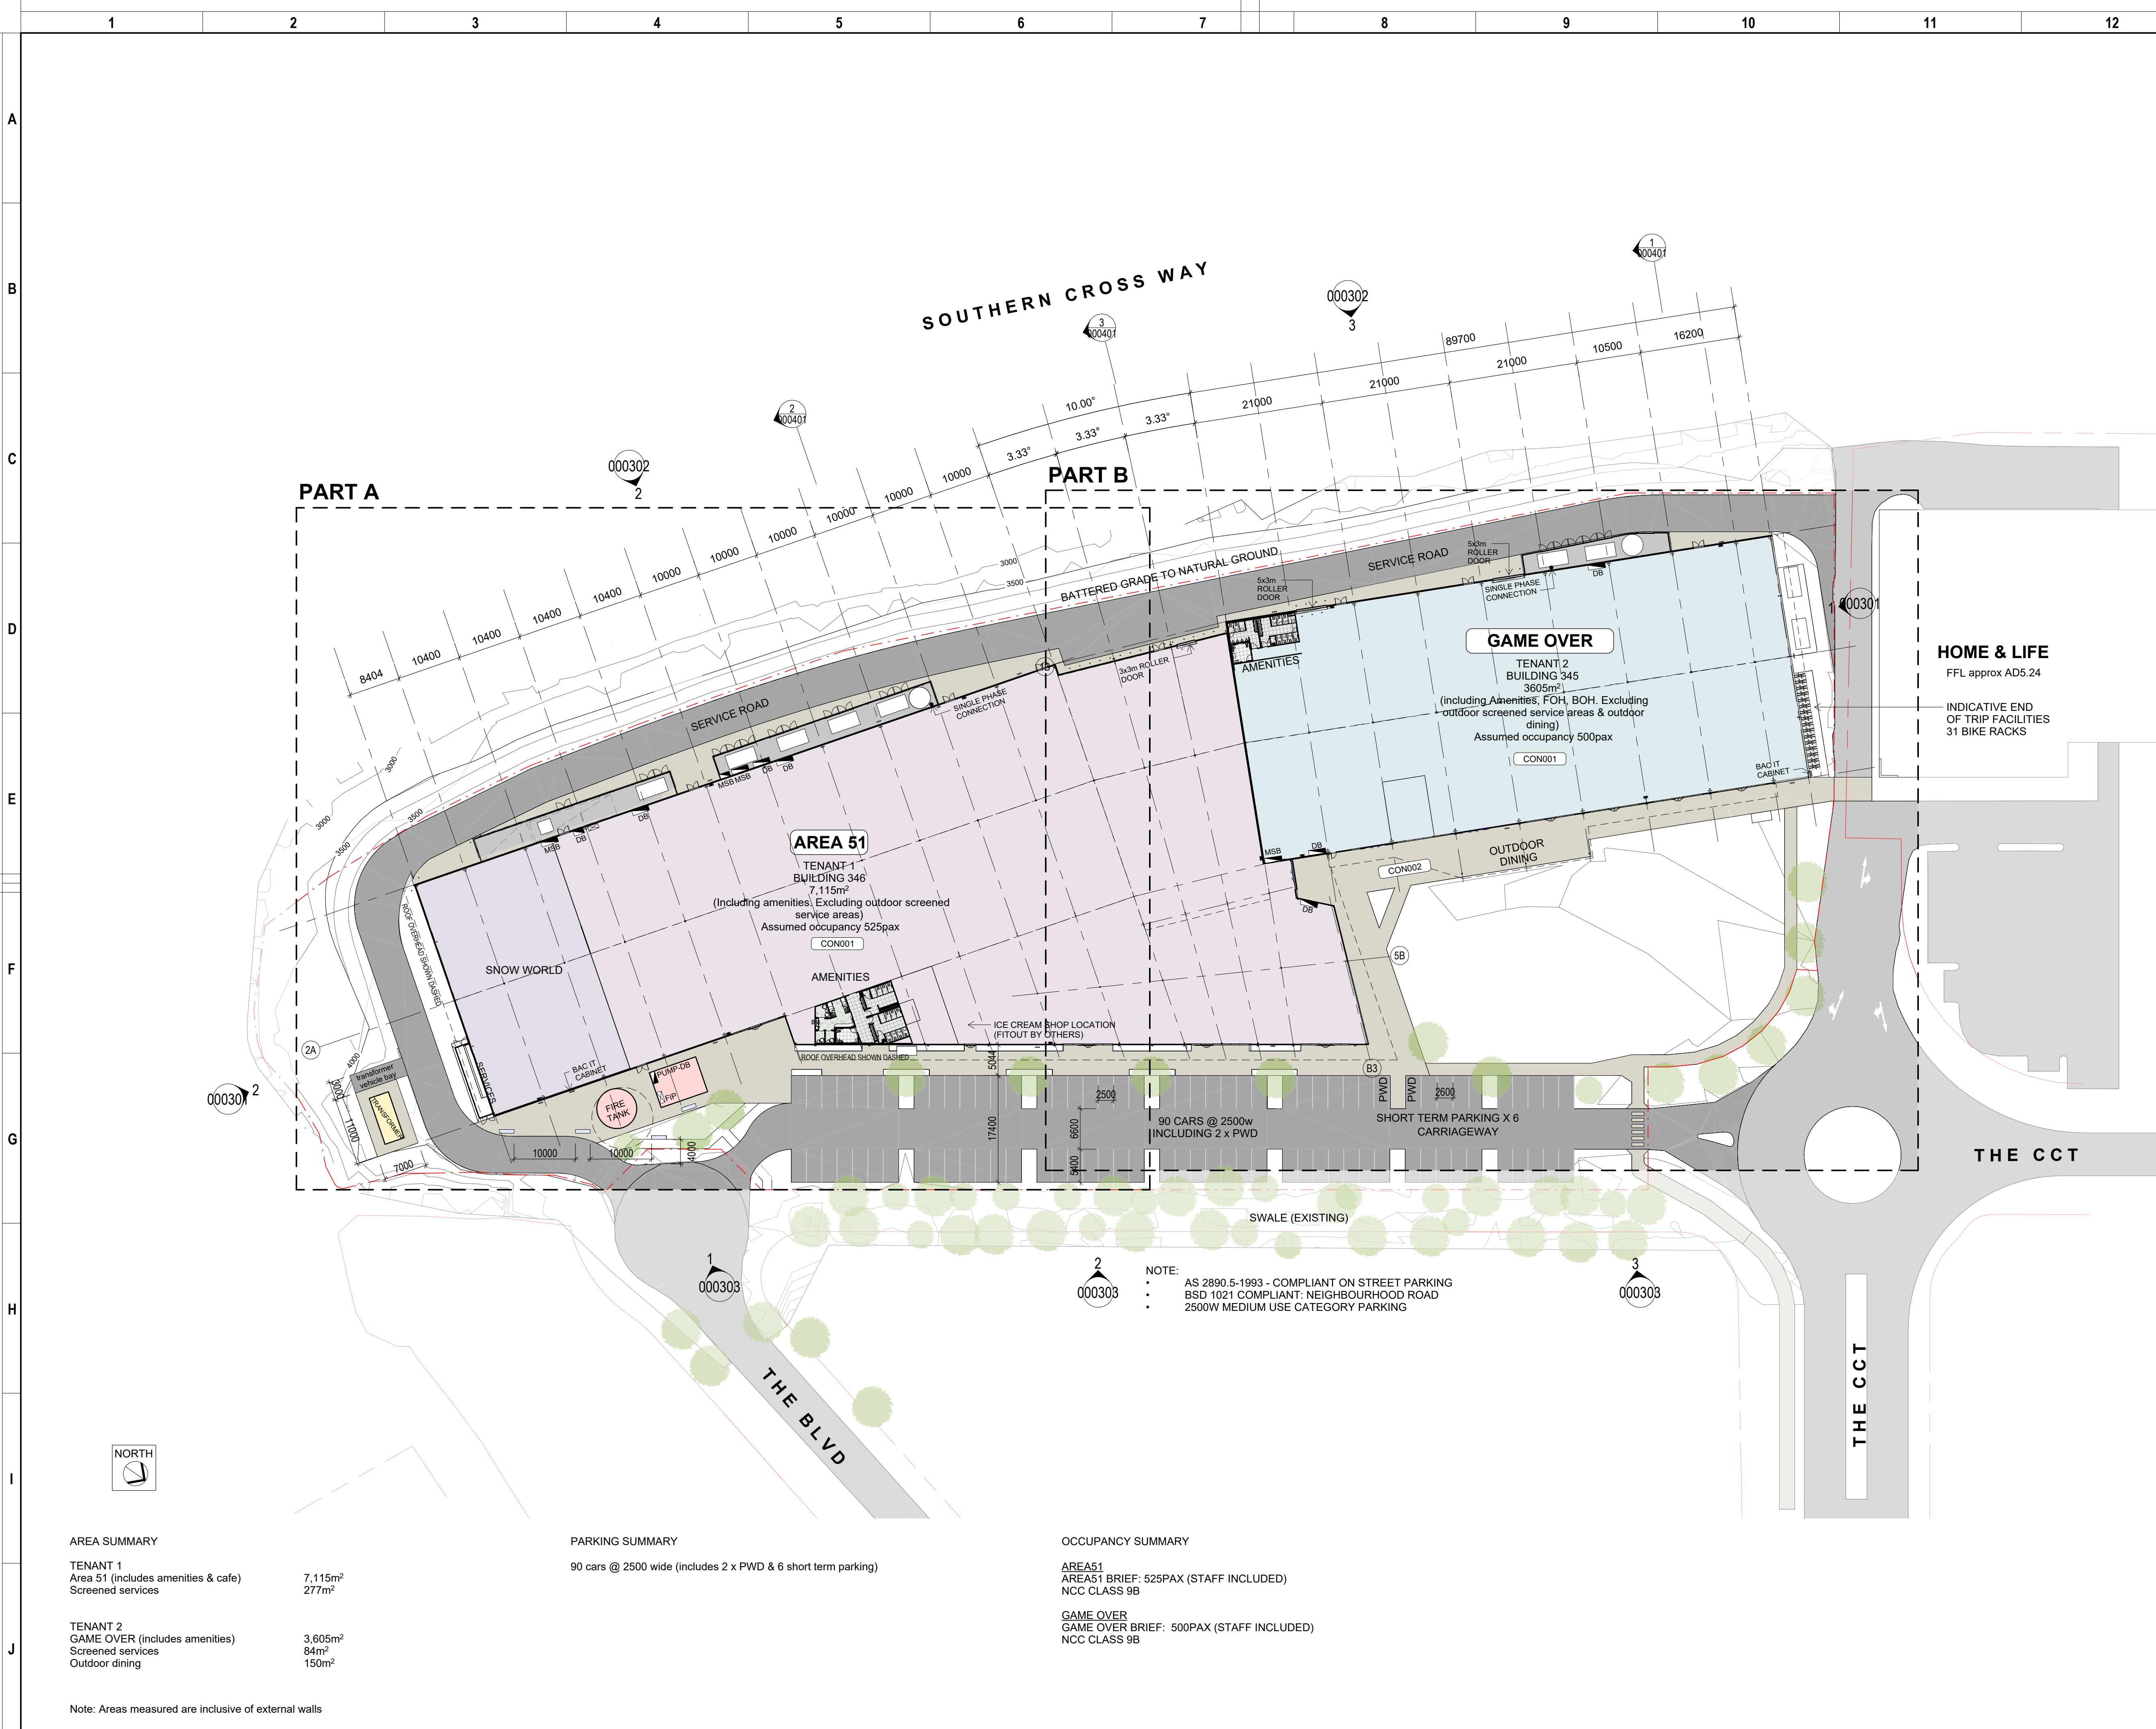

DRN	AMENDMENTS	DATE	REV
JB	FOR COORDINATION	05.06.2026	A

TAG LEGEND	
BCT1	Baby Change Tables
BIN1	WASTE BIN - RECESSED
BIN2	NAPPY BIN - IN CUPBOARD
BOL.001	BOLLARD - FIXED
BOL.002	BOLLARD - REMOVABLE
CLD.006	PRECAST CONCRETE
COL	STRUCTURAL COLUMN - REFER STRUCTURAL ENGINEER
CON.001	CONCRETE SLAB
CON.002	CONCRETE SLAB - EXTERNAL HARDSTAND
CT1	CURTAIN TRACK
DP	DOWNPIPE
FH	DOUBLE PILLAR FIRE HYDRANT REFER HYD. ENG.
FHR	FIRE HOSE REEL REFER HYD. ENG.
FLW.003	FLOOR DRAIN
GPO.1	GPO SINGLE
GPOC	GPO SINGLE - CLEANERS
M-FTL1	WET AREA TILES - FLOOR
M-FTL2	WET AREA TILES - FLOOR
M-STL1	WET AREA TILES - SKIRTING
M-TIL2	WET AREA - WALL TILE
M-VNL1	SHEET VINYL - FLOOR
MCT1	PRIVACY CURTAIN
MEC.001	MECHANICAL DUCT - REFER MECHANICAL ENGINEER
MR2	MIRROR 2
MR3	MIRROR 3
SCR.001	ALUMINIUM LOUVRE SCREEN TYPE 1
SD3	SOAP DISPENSER
SNK2	SINK - CLEANERS
STR.001	STRUCTURAL COLUMN - REFER STRUCTURAL ENGINEER
T1	WC STANDARD
T2	WC - AMBULANT
T4	WC - UNIVERSAL
THR1	TOILET ROLL HOLDER
TMV	THERMOSTATIC MIXING VALVE
TP1	TAP - WALL MOUNTED SENSOR
TRH2	TOILET ROLL HOLDER
UR1	URINAL - WALL HUNG
UR4	URINAL - TROUGH

Archipelago

Archipelago
Level 3, 189 George Street, Brisbane QLD 4000
T +61 7 3236 4806 www.archipelago.com.au
© ARCHIPELAGO ARCHITECTS PTY. LTD. All Rights Reserved
This work is copyright and cannot be reproduced or copied by any means without written permission of Archipelago Architects Pty Ltd. Any
license, express or implied, to use this document for any purpose
whatsoever is restricted to the terms of the agreement between Archipelago Architects Pt
y Ltd and the instructing party.

SKYGATE PLAY	
TENANCY PLAN	

Drawn JB	Checked DC
Design Coordinated	Compliance Checked
Authorised For Issue DC	Construction Checked

Brisbane Airport Brisbane Airport Corporation Pty Ltd 11 The Circuit Brisbane Airport QLD 4008 PO Box 61 Hamilton QLD 4007 Australia Telephone : 61 7 3406 3000 Facsimile : 61 7 3406 3111 Email : info@bne.com.au www.brisbaneairport.com.au ABN 54 076 870 650		Scale 1 : 500
Project No. 25021 - ARC - XX - 01 - DR - AR - 000200		Size A1
Drawing No.		Revision A
Project No. Originator Volume Level Type Discipline Number		Number