


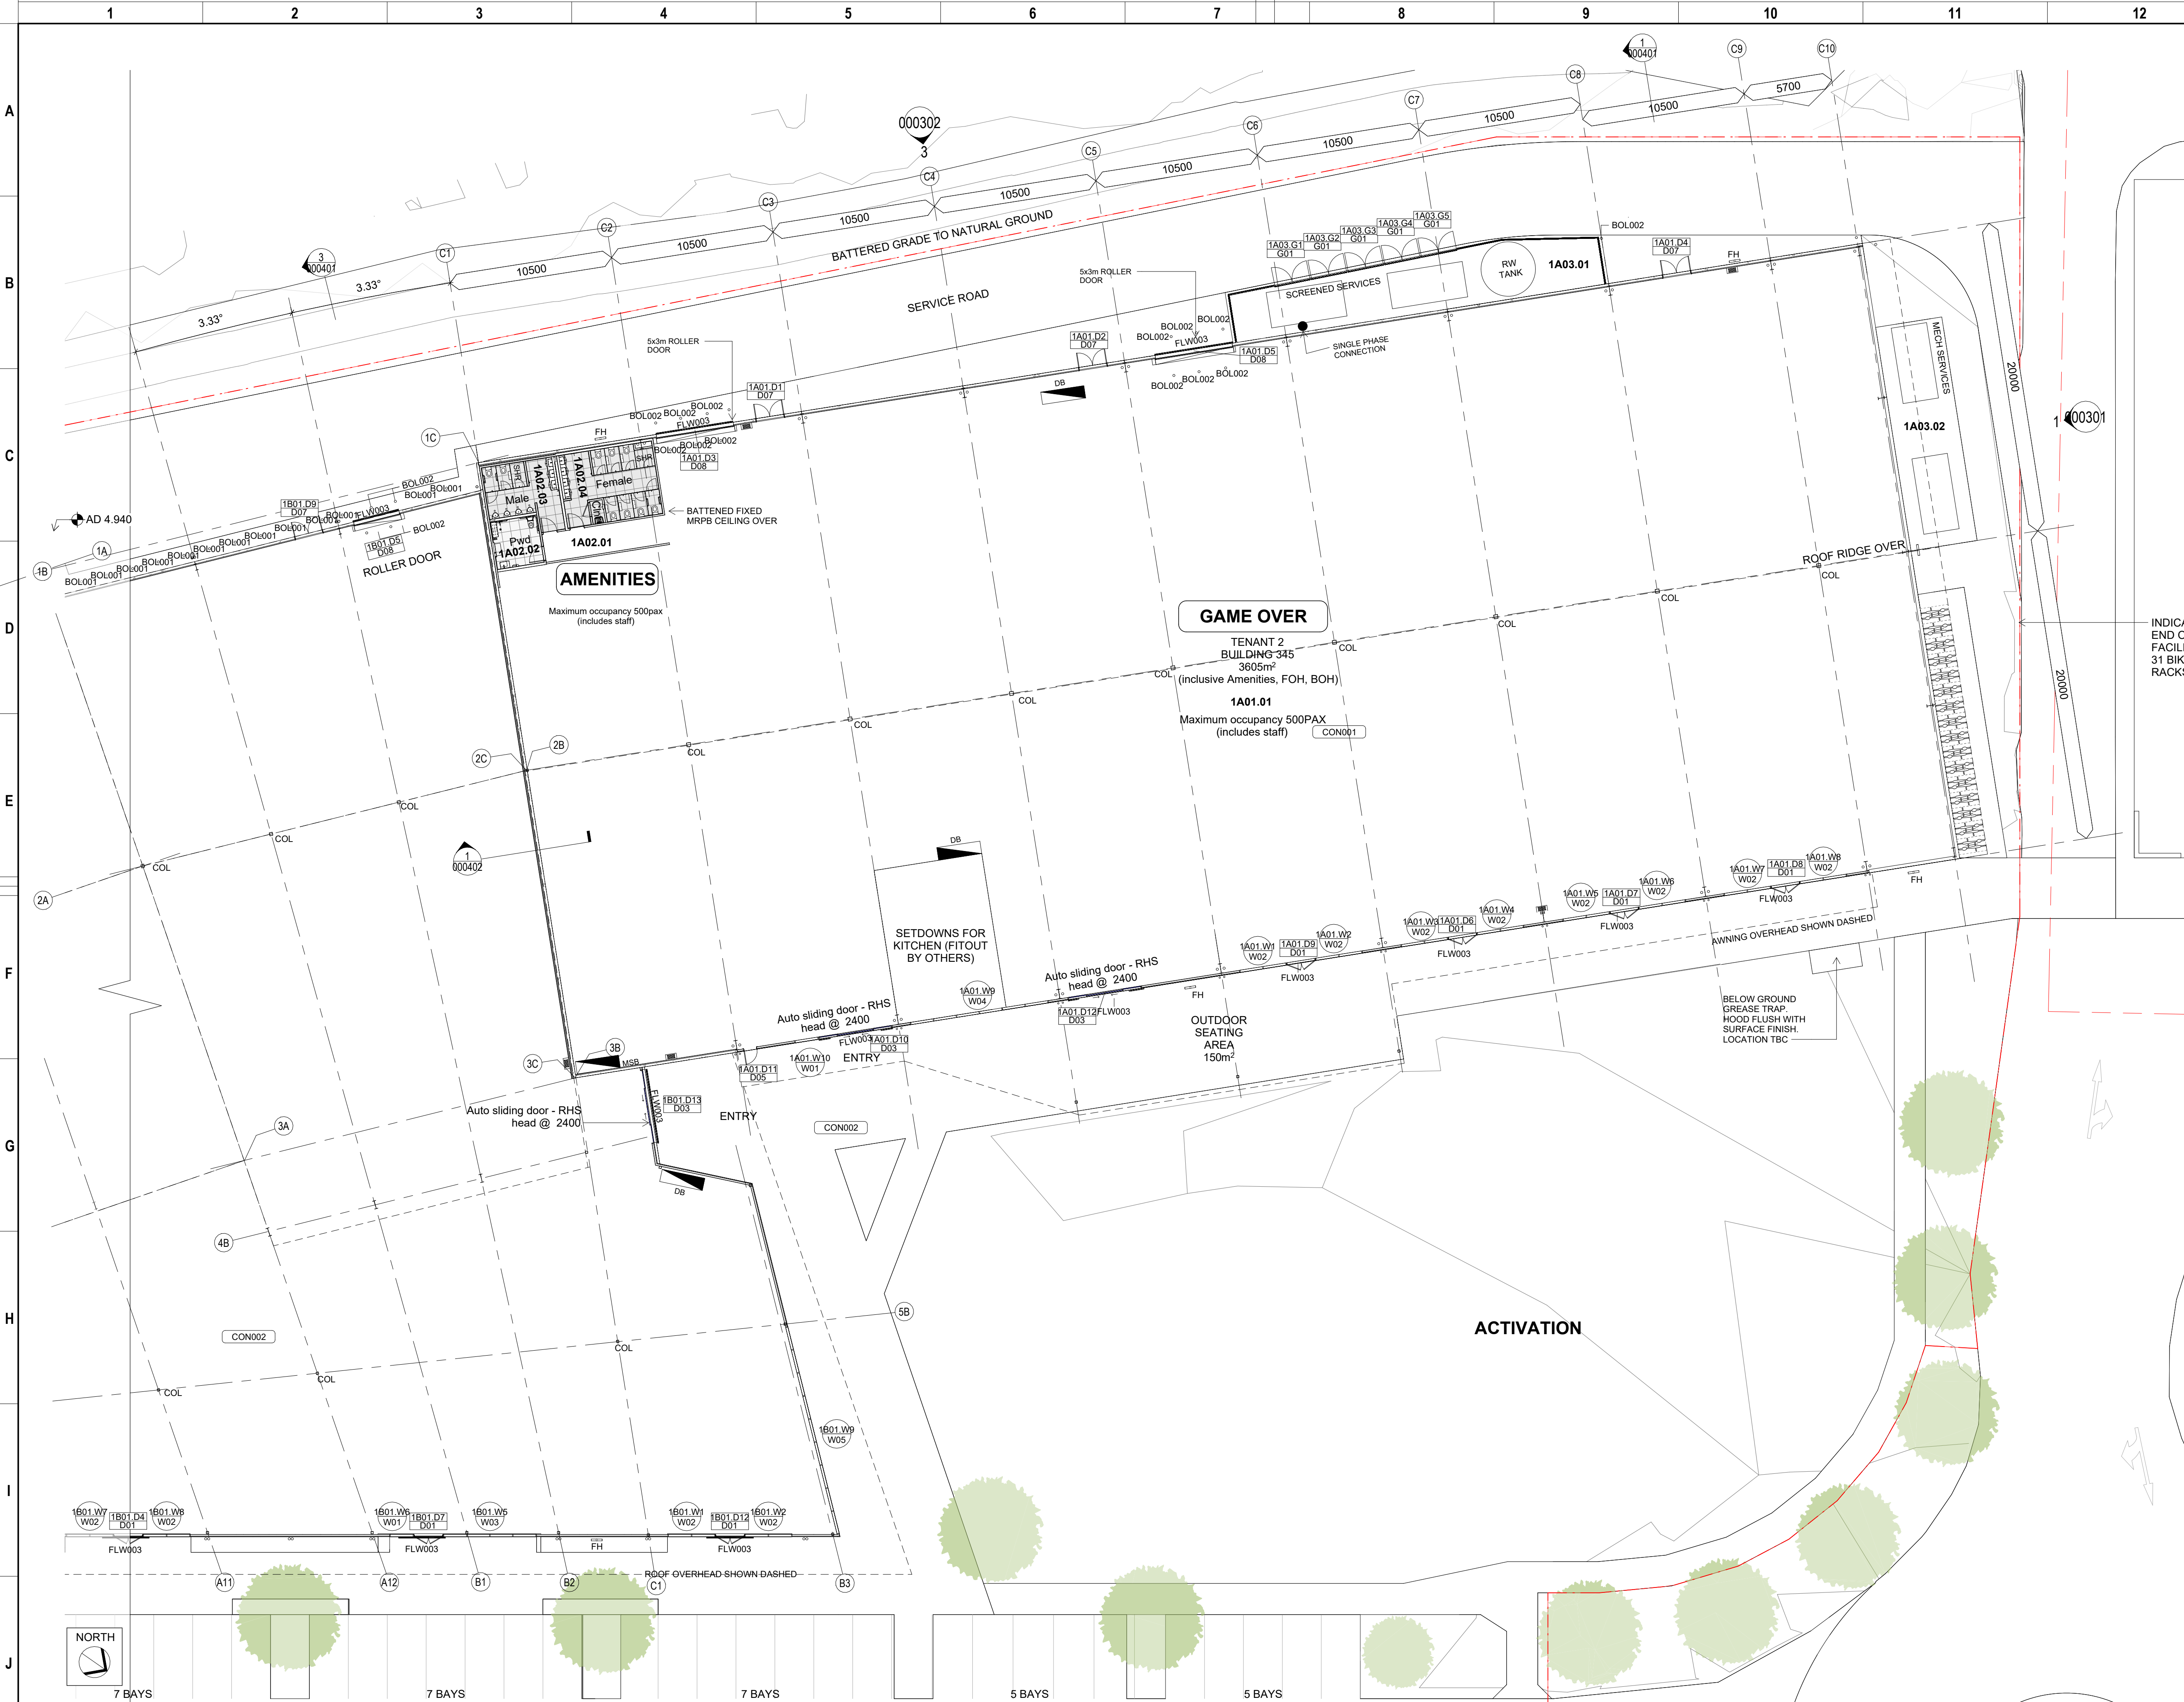

COPYRIGHT :
REPRODUCTION OF WHOLE OR PART OF THIS DOCUMENT
CONSTITUTES AN INFRINGEMENT OF COPYRIGHT. THE
INFORMATION, IDEAS AND CONCEPTS CONTAINED IN THIS
DOCUMENT ARE CONFIDENTIAL. THE RECIPIENT(S) OF
THIS DOCUMENT IS PROHIBITED FROM DISCLOSING SUCH
INFORMATION IDEAS AND CONCEPTS TO ANY PERSON
WITHOUT THE PRIOR WRITTEN CONSENT OF THE
BRISBANE AIRPORT CORPORATION PTY. LTD.

DRN	AMENDMENTS	DATE	REV
JB	FOR COORDINATION	15.05.2026	A
JB	FOR COORDINATION	05.06.2026	B

TAG LEGEND

BCT1	Baby Change Tables
BIN1	WASTE BIN - RECESSED
BOL001	BOLLARD - FIXED
BOL002	BOLLARD - REMOVABLE
CLD006	PRECAST CONCRETE
COL	STRUCTURAL COLUMN - REFER STRUCTURAL ENGINEER
CON001	CONCRETE SLAB
CON002	CONCRETE SLAB - EXTERNAL HARDSTAND
DP	DOWNSPIPE
FH	DOUBLE PILLAR FIRE HYDRANT REFER HYD. ENG.
FHR	FIRE HOSE REEL REFER HYD. ENG.
FLW003	FLOOR DRAIN
GPOC	GPO SINGLE - CLEANERS
M-FTL1	WET AREA TILES - FLOOR
M-FTL2	WET AREA TILES - FLOOR
M-STL1	WET AREA TILES - SKIRTING
M-TIL2	WET AREA - WALL TILE
MEC001	MECHANICAL DUCT - REFER MECHANICAL ENGINEER
MR2	MIRROR 2
SCR001	ALUMINIUM LOUVRE SCREEN TYPE 1
SD3	SOAP DISPENSER
SNK2	SINK - CLEANERS
STR001	STRUCTURAL COLUMN - REFER STRUCTURAL ENGINEER
T1	WC STANDARD
T2	WC - AMBULANT
T4	WC - UNIVERSAL
THR1	TOILET ROLL HOLDER
TMV	THERMOSTATIC MIXING VALVE
TP1	TAP - WALL MOUNTED SENSOR
TRH2	TOILET ROLL HOLDER
UR1	URINAL - WALL HUNG

Archipelago

Archipelago
Level 3, 189 George Street, Brisbane QLD 4000
T +61 7 3236 4805 www.archipelago.com.au
© ARCHIPELAGO ARCHITECTS PTY. LTD. All Rights Reserved
This work is copyright and cannot be reproduced or copied by any means without written permission of Archipelago Architects Pty Ltd. Any license, express or implied, to use this document for any purpose whatsoever is restricted to the terms of the agreement between Archipelago Architects Pty Ltd and the instructing party.

SKYGATE PLAY

GENERAL ARRANGEMENT - PART B

Drawn JB	Checked DC
Design Coordinated	Compliance Checked
Authorised For Issue DC	Construction Checked

Brisbane Airport	Brisbane Airport Corporation Pty Ltd 11 The Circuit Brisbane Airport QLD 4008 Telephone: 61 7 3406 3000 Facsimile: 61 7 3406 3111 Email: info@bne.com.au www.brisbaneairport.com.au ABN 54 076 870 650	Scale 1 : 200 Size A1 Revision B
------------------	--	---

Project No.	Originator	Volume	Level	Type	Discipline	Number
25021	ARC	XX	01	DR	AR	000202