


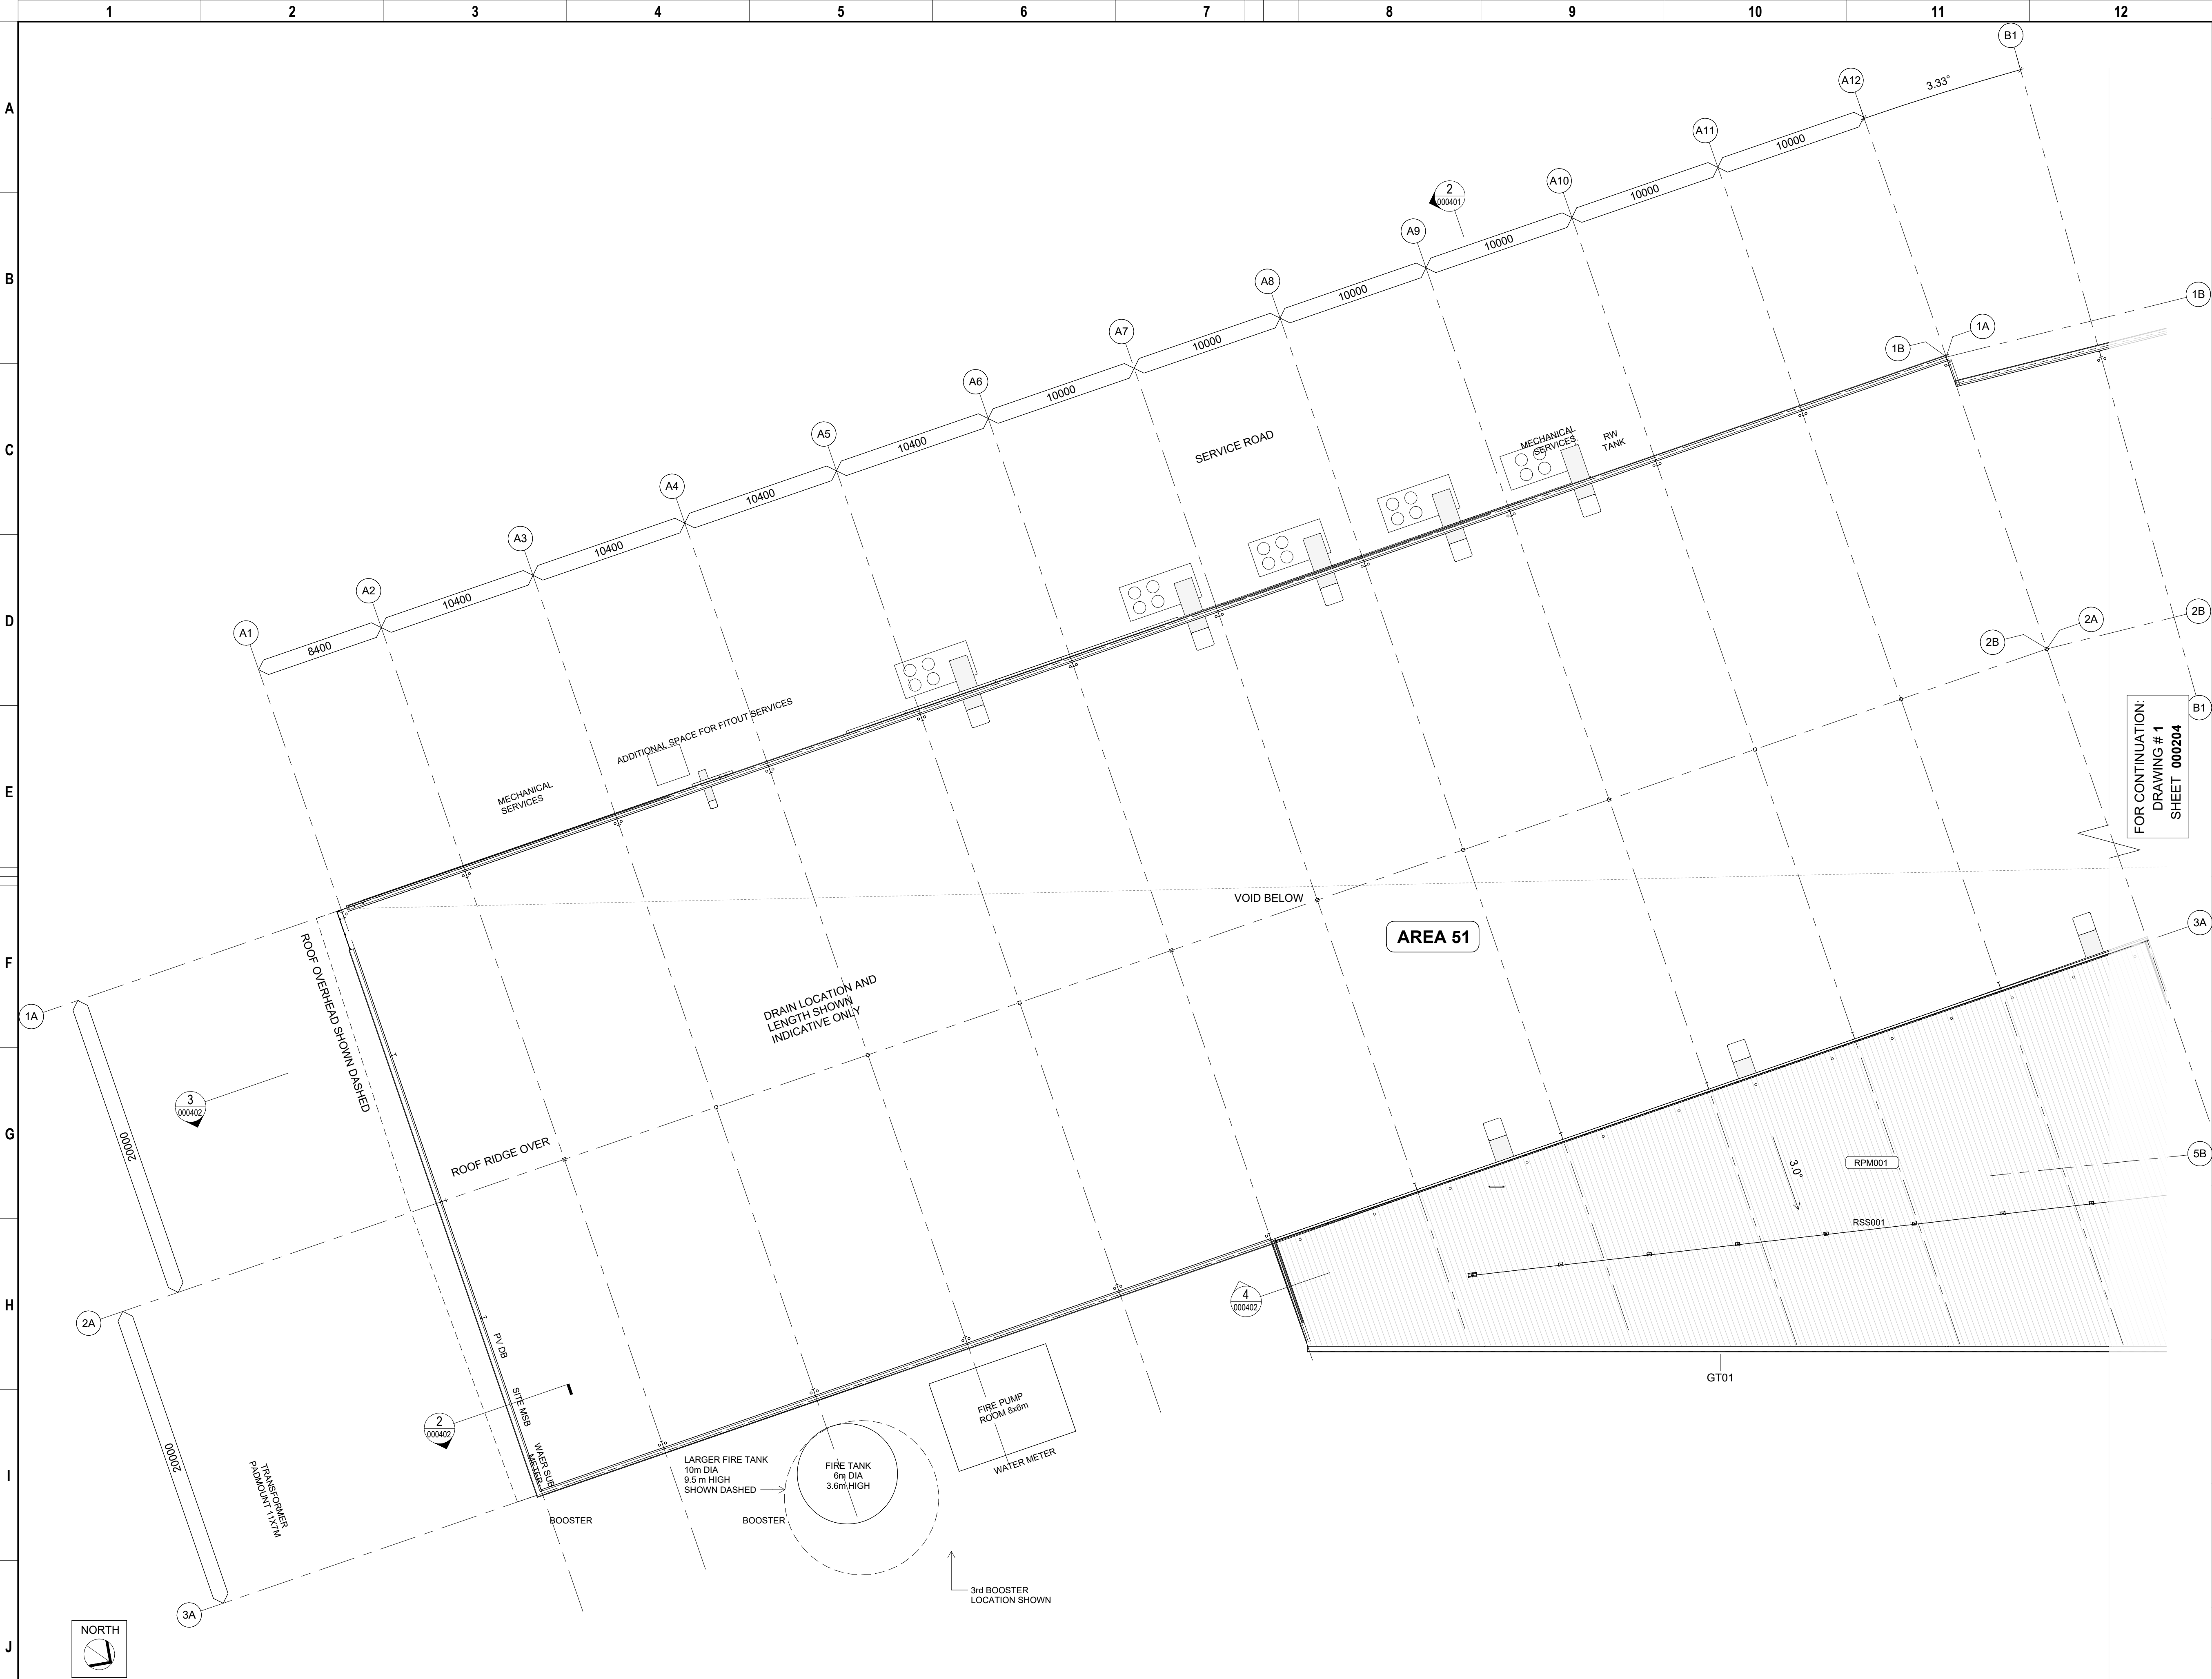

COPYRIGHT:
REPRODUCTION OF WHOLE OR PART OF THIS DOCUMENT
CONSTITUTES AN INFRINGEMENT OF COPYRIGHT. THE
INFORMATION, IDEAS AND CONCEPTS CONTAINED IN THIS
DOCUMENT ARE CONFIDENTIAL. THE RECIPIENT(S) OF
THIS DOCUMENT IS PROHIBITED FROM DISCLOSING SUCH
INFORMATION IDEAS AND CONCEPTS TO ANY PERSON
WITHOUT THE PRIOR WRITTEN CONSENT OF THE
BRISBANE AIRPORT CORPORATION PTY. LTD.

DRN	AMENDMENTS	DATE	REV
JB	FOR COORDINATION	04.12.2025	1
DC	FOR COORDINATION	21.01.2026	2
JB	60% DD ISSUE 2	05.02.2026	3

TAG LEGEND	
CLD004	PROFILED METAL SHEET CLADDING - REFER TO SECTION J REPORT
CLD005	DANFALON SINGLE GLAZED TRANSLUCENT CLADDING
COL	STRUCTURAL COLUMN - REFER STRUCTURAL ENGINEER
DP	DOWNPIPE
GT01	COLORBOND FOLDED STEEL GUTTER
MEC001	MECHANICAL DUCT - REFER MECHANICAL ENGINEER
MLV001	MECHANICAL EXHAUST LOUVRE
RPM001	INSULATED ROOF PANEL
RSS001	ROOF SAFETY SYSTEM
STR001	STRUCTURAL COLUMN - REFER STRUCTURAL ENGINEER

FOR CONTINUING:
DRAWING # 1
SHEET 000204

Archipelago
Archipelago
Level 3, 189 George Street, Brisbane QLD 4000
T +617 3236 4806 www.archipelago.com.au
© ARCHIPELAGO ARCHITECTS PTY. LTD. All Rights Reserved
This work is copyright and cannot be reproduced or copied by any means without written permission of Archipelago Architects Pty Ltd. Any license, express or implied, to use this document for any purpose whatsoever is restricted to the terms of the agreement between Archipelago Architects Pty Ltd and the instructing party.

SKYGATE PLAY

GENERAL ARRANGEMENT - PART A - HIGH LEVEL

Drawn JB	Checked DC
Design Coordinated	Compliance Checked
Authorised For Issue	Construction Checked



Brisbane Airport Corporation Pty Ltd
11 The Circuit Brisbane Airport QLD 4008
PO Box 61 Hamilton QLD 4007 Australia

Telephone : 61 7 3406 3000
Facsimile : 61 7 3406 3111
Email : info@bne.com.au
www.brisbaneairport.com.au

ABN 54 076 870 650

Scale
1 : 200

Size
A1

Revision
3

Project No.	Originator	Volume	Level	Type	Discipline	Number
25021	- ARC	- XX	- 01	- DR	- AR	- 000203

Drawing No.