
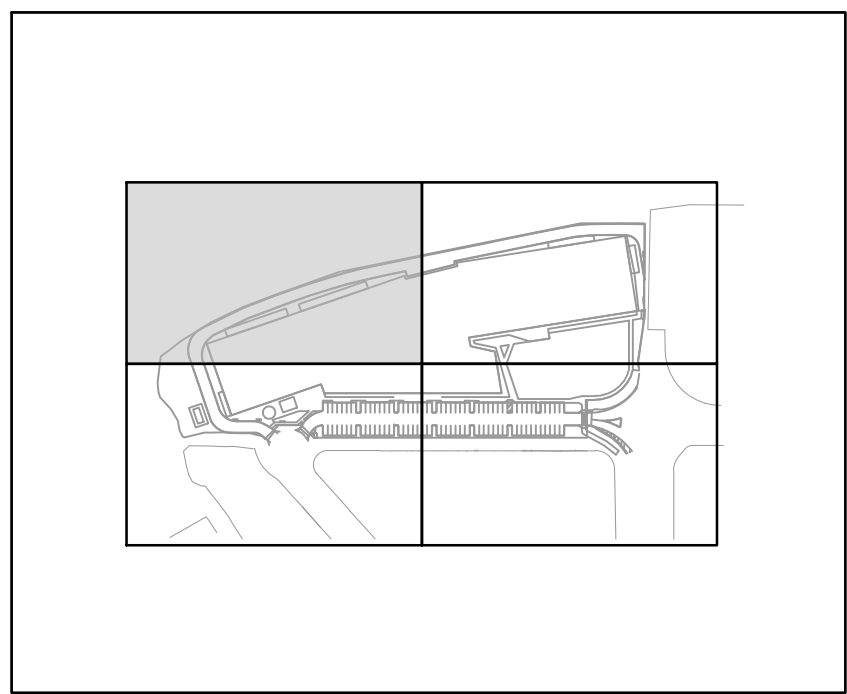


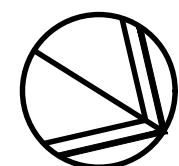

KEY PLAN
NTS

LEGEND

- EXISTING PROPERTY BOUNDARY
XX XX
EXISTING CONTOUR MAJOR
XX XX
PROPOSED CONTOUR MINOR
E
EXISTING ELECTRICITY
E-UG
EXISTING ELECTRICITY (UNDERGROUND)
HV
EXISTING ELECTRICITY (HIGH VOLTAGE)
W
EXISTING WATER
R
EXISTING RECYCLE WATER
IRR
EXISTING IRRIGATION
SWD
EXISTING STORMWATER
S
EXISTING SEWER MAIN
RM
EXISTING SEWER MAIN (RAISING MAIN)
COMS
EXISTING COMMUNICATION
PROPOSED SLAB DROP EDGE IN ACCORDANCE WITH STRUCTURAL DETAILS
WORKS BOUNDARY

- PROPOSED CONCRETE HARDSTAND PAVEMENT IN ACCORDANCE WITH STRUCTURAL ENGINEERS SPECIFICATION
PROPOSED LANDSCAPE AREA, REFER TO LANDSCAPE DRAWINGS FOR DETAILS
PROPOSED 600mm AC REINSTATEMENT STRIP REFER TO DWG 000220 FOR DETAILS
PROPOSED CONCRETE FOOTPATH IN ACCORDANCE WITH IPWEA STD DRG PSD-302
PROPOSED PRECAST CONCRETE ISLAND REFER TO CIVILMART DWG 0913R FOR DETAILS
PROPOSED WATER MAIN
PROPOSED SEWER MAIN
PROPOSED INTEGRAL KERB REFER TO DRAWING 000351
PROPOSED ROOF EXTEND REFER TO ARCHITECTURAL DWG FOR DETAILS
PROPOSED STORMWATER DRAINAGE

- PROPOSED STORMWATER HEADWALL
PROPOSED STORMWATER MANHOLE
PROPOSED STORMWATER PIT
PROPOSED STORMWATER STRUCTURE NUMBER
PROPOSED SEWER STRUCTURE NUMBER

NOTES:


- FOR FULL EXISTING FEATURE LEGENDS REFER TO 000020.
- FOR ROADWORKS & STORMWATER DRAINAGE DETAILS REFER TO 000351 DRAWING.
- ALL WORKS TO BE CARRIED OUT STRICTLY IN ACCORDANCE WITH NORTHPROP SPECIFICATION NOTES FOUND WITHIN 000010 SERIES DRAWINGS. NORTHPROP WILL NOT BE HELD LIABLE FOR NON-COMPLIANT WORKS.
- FOR RETAINING WALL AND GUARDRAIL SPECIFICATION, REFER TO STRUCTURAL DRAWINGS.

THRESHOLD NOTES:

- PROVIDE A 50mm LEVEL DIFFERENCE BETWEEN THE INTERNAL AND EXTERNAL SLABS AT ALL ROLLER SHUTTER DOORS UNDER AWNINGS.
- PROVIDE A 50mm LEVEL DIFFERENCE BETWEEN THE INTERNAL AND EXTERNAL SLABS OF THE BUILDING ALONG OTHER EDGES.
- PROVIDE A 35mm LEVEL DIFFERENCE BETWEEN THE INSIDE AND OUTSIDE SLABS AT THE OFFICES AND ALL DDA COMPLIANT DOORS. REFER TO ARCHITECT DRAWINGS FOR LOCATION OF DDA COMPLIANT DOORS.

WARNING

UNDERGROUND SERVICES
UNDERGROUND SERVICES EXIST IN THIS AREA. UNDERGROUND SERVICE LOCATIONS AND DEPTHS TO BE CONFIRMED PRIOR TO COMMENCEMENT OF CONSTRUCTION WORKS.

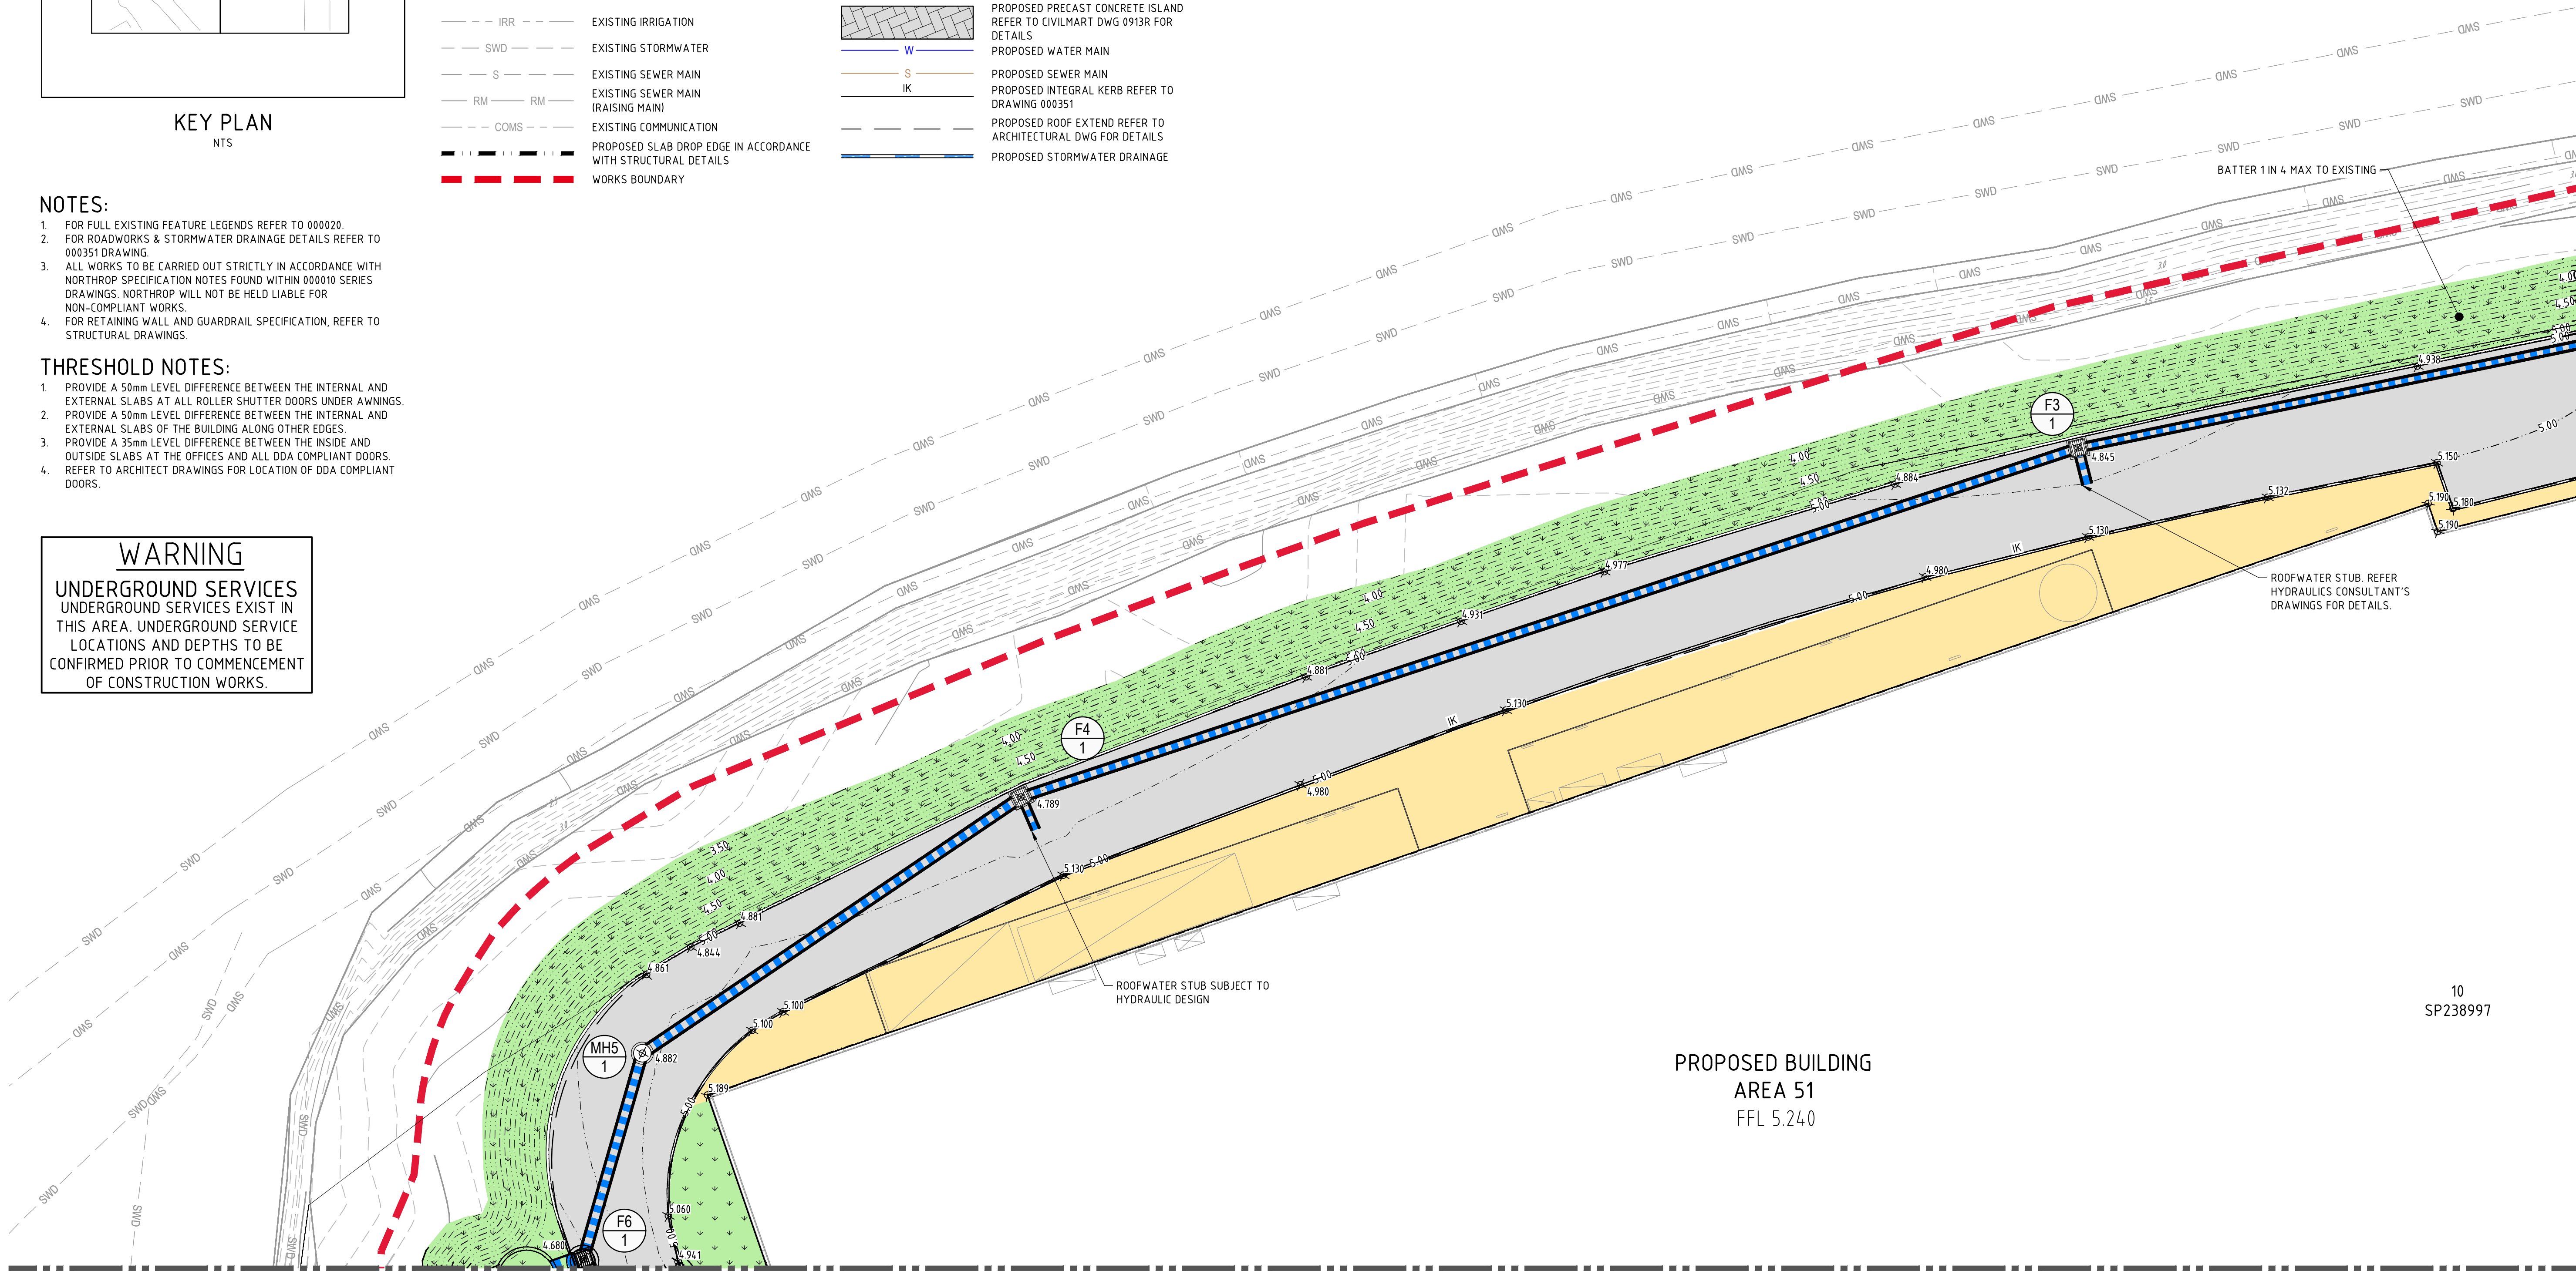

FOR CONTINUATION REFER TO SHEET 000213

NOT FOR CONSTRUCTION

SCALE 1:200 @ A1

COPYRIGHT :
REPRODUCTION OF WHOLE OR PART OF THIS DOCUMENT CONSTITUTES AN INFRINGEMENT OF COPYRIGHT. THE INFORMATION, IDEAS AND CONCEPTS CONTAINED IN THIS DOCUMENT ARE CONFIDENTIAL. THE RECIPIENT(S) OF THIS DOCUMENT IS PROHIBITED FROM DISCLOSING SUCH INFORMATION IDEAS AND CONCEPTS TO ANY PERSON WITHOUT THE PRIOR WRITTEN CONSENT OF THE BRISBANE AIRPORT CORPORATION PTY. LTD.

JD	PRELIMINARY DESIGN 30%	01.09.25	A
JD	ISSUED FOR TENDER	23.12.25	B
JD	ISSUED FOR TENDER	28.01.26	C
LQ	ISSUED FOR TENDER	30.01.26	D
LQ	ISSUED FOR TENDER	09.02.26	E
MM	ISSUED FOR APPROVAL	11.06.26	F
DRN	AMENDMENTS	DATE	REV

XENIA

NORTHROP
Brisbane
The Annex, Level 8, 12 Creek Street, Brisbane QLD 4000
GPO BOX 423 Brisbane QLD 4001
(07) 3365 0400 brisbane@northrop.com.au
ABN 81 094 433 100

Drawn
M.MANLAPIT
11.06.26
Design Coordinated
R.MITCHELL
11.06.26
Authorised For Issue
S.KILLORAN
11.06.26

Checked
A.TATHAM
11.06.26
Compliance Checked
S.KILLORAN
11.06.26
Construction Checked
N/A

SKYGATE PLAY
BRISBANE AIRPORT
ROADWORKS & STORMWATER
DRAINAGE LAYOUT PLAN
SHEET 1 OF 4

	BRISBANE AIRPORT CORPORATION PTY LTD 11 THE CIRCUIT, BRISBANE AIRPORT QLD 4008 PO BOX 61, HAMILTON CENTRAL QLD 4007 AUSTRALIA T +61 734063000 E INFO@BNE.COM.AU W BNE.COM.AU										Scale AS ABOVE
	Project No.	Originator	Volume	Level	Type	Discipline	Number	Revision	F		
Drawing Number	25021	- NRP	- XX	- XX	- DR	- CI	- 000211				