


NOTES:

1. FOR FULL EXISTING FEATURE LEGENDS REFER TO 000020.
2. FOR ROADWORKS & STORMWATER DRAINAGE DETAILS REFER TO 000351 DRAWING.
3. ALL WORKS TO BE CARRIED OUT STRICTLY IN ACCORDANCE WITH NORTHROP SPECIFICATION NOTES FOUND WITHIN 000010 SERIES DRAWINGS. NORTHROP WILL NOT BE HELD LIABLE FOR NON-COMPLIANT WORKS.
4. FOR RETAINING WALL AND GUARDRAIL SPECIFICATION, REFER TO STRUCTURAL DRAWINGS.

THRESHOLD NOTES:

1. PROVIDE A 50mm LEVEL DIFFERENCE BETWEEN THE INTERNAL AND EXTERNAL SLABS AT ALL ROLLER SHUTTER DOORS UNDER AWNINGS.
2. PROVIDE A 50mm LEVEL DIFFERENCE BETWEEN THE INTERNAL AND EXTERNAL SLABS OF THE BUILDING ALONG OTHER EDGES.
3. PROVIDE A 35mm LEVEL DIFFERENCE BETWEEN THE INSIDE AND OUTSIDE SLABS AT THE OFFICES AND ALL DDA COMPLIANT DOORS.
4. REFER TO ARCHITECT DRAWINGS FOR LOCATION OF DDA COMPLIANT DOORS.

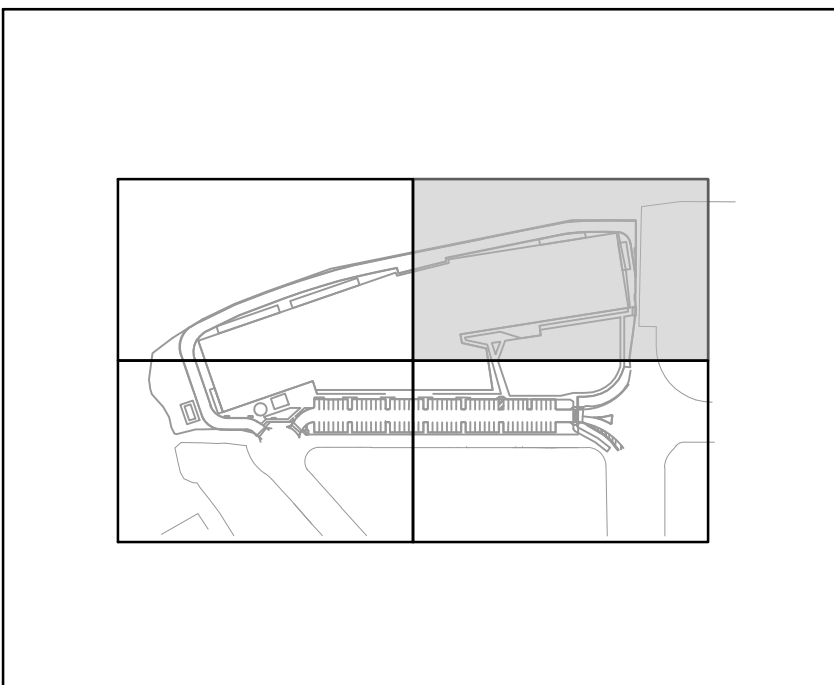

KEY PLAN
NTS

LEGEND

- EXISTING PROPERTY BOUNDARY
- EXISTING CONTOUR MAJOR
- PROPOSED CONTOUR MINOR
- EXISTING ELECTRICITY
- EXISTING ELECTRICITY (UNDERGROUND)
- EXISTING ELECTRICITY (HIGH VOLTAGE)
- EXISTING WATER
- EXISTING RECYCLE WATER
- EXISTING IRRIGATION
- EXISTING STORMWATER
- EXISTING SEWER MAIN
- EXISTING SEWER MAIN (RAISING MAIN)
- EXISTING COMMUNICATION
- PROPOSED SLAB DROP EDGE IN ACCORDANCE WITH STRUCTURAL DETAILS
- WORKS BOUNDARY
- PROPOSED CONCRETE HARDSTAND PAVEMENT IN ACCORDANCE WITH STRUCTURAL ENGINEERS SPECIFICATION
- PROPOSED LANDSCAPE AREA. REFER TO LANDSCAPE DRAWINGS FOR DETAILS
- PROPOSED 600mm AC REINSTATEMENT STRIP REFER TO DWG 000220 FOR DETAILS
- PROPOSED CONCRETE FOOTPATH IN ACCORDANCE WITH IPWEA STD DRG PSD-302
- PROPOSED PRECAST CONCRETE ISLAND REFER TO CIVILMART DWG 0913R FOR DETAILS
- PROPOSED WATER MAIN
- PROPOSED SEWER MAIN
- PROPOSED INTEGRAL KERB REFER TO DRAWING 000351
- PROPOSED ROOF EXTEND REFER TO ARCHITECTURAL DWG FOR DETAILS
- PROPOSED STORMWATER DRAINAGE
- PROPOSED STORMWATER HEADWALL
- PROPOSED STORMWATER MANHOLE
- PROPOSED STORMWATER PIT

WARNING
UNDERGROUND SERVICES
UNDERGROUND SERVICES EXIST IN THIS AREA. UNDERGROUND SERVICE LOCATIONS AND DEPTHS TO BE CONFIRMED PRIOR TO COMMENCEMENT OF CONSTRUCTION WORKS.

NOT FOR CONSTRUCTION

SCALE 1:200@ A1

COPYRIGHT : REPRODUCTION OF WHOLE OR PART OF THIS DOCUMENT CONSTITUTES AN INFRINGEMENT OF COPYRIGHT. THE INFORMATION, IDEAS AND CONCEPTS CONTAINED IN THIS DOCUMENT ARE CONFIDENTIAL. THE RECIPIENT(S) OF THIS DOCUMENT IS PROHIBITED FROM DISCLOSING SUCH INFORMATION IDEAS AND CONCEPTS TO ANY PERSON WITHOUT THE PRIOR WRITTEN CONSENT OF THE BRISBANE AIRPORT CORPORATION PTY. LTD.							
MM	ISSUED FOR APPROVAL	11.06.26	A				
DRN	AMENDMENTS	DATE	REV				

XENIA

NORTHROP
Brisbane
The Annex, Level 8, 12 Creek Street, Brisbane QLD 4000
(07) 3365 0400 brisbane@northrop.com.au
ABN 81 094 433 100

Drawn
M.MANLAPIT
11.06.26
Design Coordinated
R.MITCHELL
11.06.26
Authorised For Issue
S.KILLORAN
11.06.26

Checked
A.TATHAM
11.06.26
Compliance Checked
S.KILLORAN
11.06.26
Construction Checked
N/A

SKYGATE PLAY
BRISBANE AIRPORT
ROADWORKS & STORMWATER
DRAINAGE LAYOUT PLAN
SHEET 2 OF 4

Brisbane Airport		BRISBANE AIRPORT CORPORATION PTY LTD 11 THE CIRCUIT, BRISBANE AIRPORT QLD 4008 PO BOX 81, HAMILTON CENTRAL QLD 4007 AUSTRALIA T +61 734063000 E INFO@BNE.COM.AU W BNE.COM.AU		Scale AS ABOVE
Drawing Number		Project No.		Size A1
25021 - NRP		Originator		Revision A
		Volume		Number
		Level		
		Type		
		Discipline		
		Number		