


PROPOSED BUILDING
AREA 51

PROPOSED BUILDING
AREA 51

LEGEND

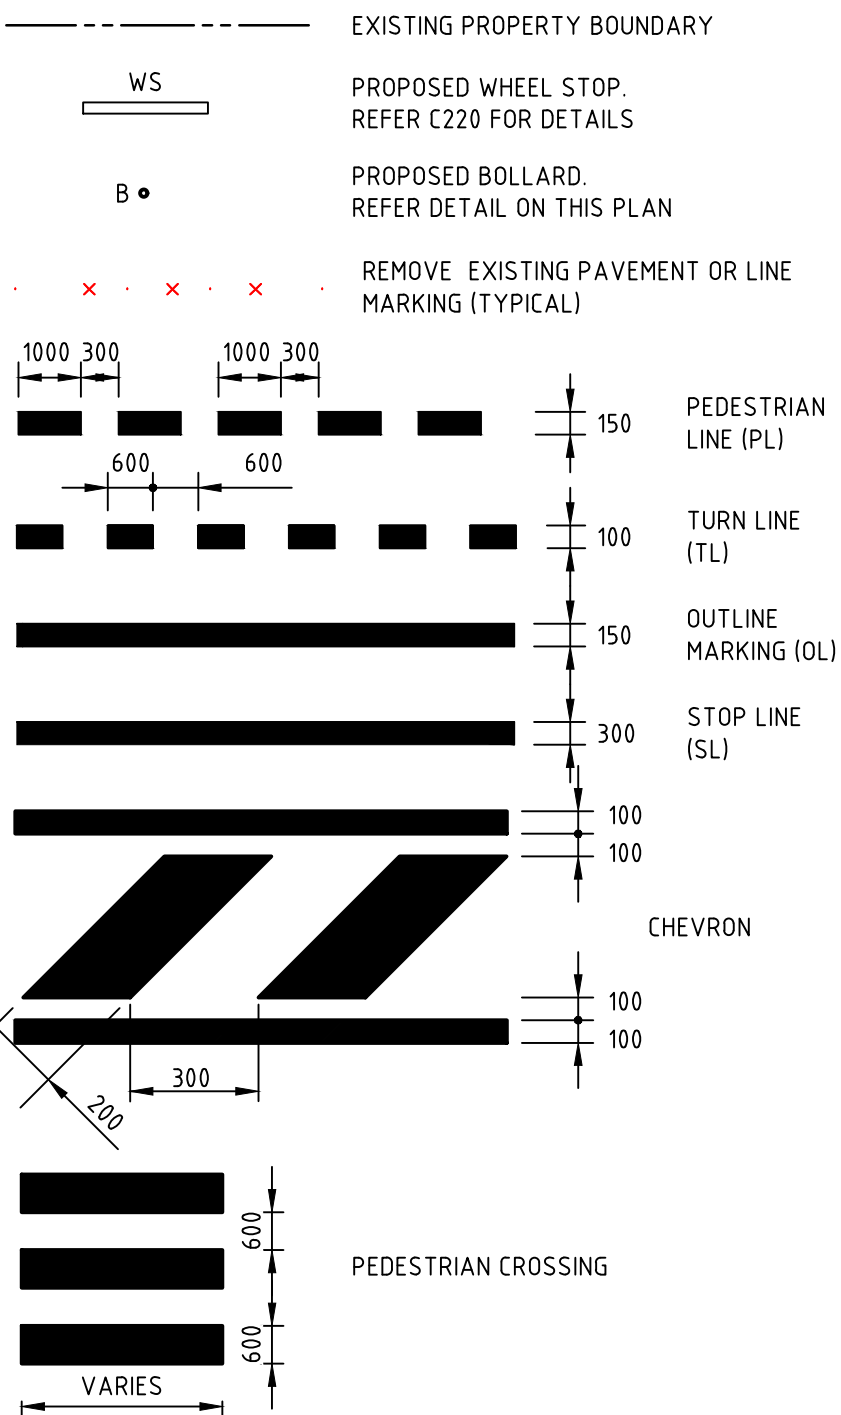

NOTE:

- ALL WORKS TO BE CARRIED OUT STRICTLY IN ACCORDANCE WITH NORTHROP SPECIFICATION NOTES FOUND WITHIN 000010 SERIES DRAWINGS. NORTHROP WILL NOT BE HELD LIABLE FOR NON-COMPLIANT WORKS.
- ALL SIGNAGE, LINEMARKING & REFLECTORISED PAVEMENT MARKERS ARE TO BE IN ACCORDANCE WITH THE CURRENT DEPARTMENT OF TRANSPORT & MAIN ROADS 'MANUAL OF UNIFORM TRAFFIC CONTROL DEVICES' (M.U.T.C.D.).
- ALL LINEMARKING TO BE REFLECTORISED WHITE.
- FINAL SIGN LOCATIONS TO BE DETERMINED ON SITE BY THE SUPERINTENDENT.
- EXISTING LINEMARKING MADE REDUNDANT BY NEW LINEMARKING IS TO BE REMOVED BY ROUTING OR OTHER METHOD APPROVED BY DEPARTMENT OF TRANSPORT & MAIN ROADS.
- ALL TRAFFIC SIGNS TO BE SIZE 'B' UNLESS NOTED OTHERWISE.
- FOR TRAFFIC SIGN SUPPORT DETAILS, REFER QUEENSLAND TRANSPORT STANDARD DRAWING NO.'S 1360 & 1362.
- ALL SIGN MATERIAL TO BE CLASS 1.

NOT FOR CONSTRUCTION

SCALE 1:200 @ A1

COPYRIGHT : REPRODUCTION OF WHOLE OR PART OF THIS DOCUMENT CONSTITUTES AN INFRINGEMENT OF COPYRIGHT. THE INFORMATION, IDEAS AND CONCEPTS CONTAINED IN THIS DOCUMENT ARE CONFIDENTIAL. THE RECIPIENT(S) OF THIS DOCUMENT IS PROHIBITED FROM DISCLOSING SUCH INFORMATION IDEAS AND CONCEPTS TO ANY PERSON WITHOUT THE PRIOR WRITTEN CONSENT OF THE BRISBANE AIRPORT CORPORATION PTY. LTD.

MM	ISSUED FOR APPROVAL	11.06.26	A
DRN	AMENDMENTS	DATE	REV

XENIA

NORTHROP

Brisbane

The Annex, Level 8, 12 Creek Street, Brisbane QLD 4000

GPO BOX 423 Brisbane QLD 4001

(07) 3365 0400 brisbane@northrop.com.au

ABN 81 094 433 100

Drawn
M.MANLAPIT
11.06.26

Design Coordinated
R.MITCHELL
11.06.26

Authorised For Issue
S.KILLORAN
11.06.26

Checked
A.TATHAM
11.06.26

Compliance Checked
S.KILLORAN
11.06.26

Construction Checked
N/A

SKYGATE PLAY
BRISBANE AIRPORT

SIGNS AND LINEMARKING
LAYOUT PLAN

Brisbane Airport

BRISBANE AIRPORT CORPORATION PTY LTD
11 THE CIRCUIT, BRISBANE AIRPORT QLD 4008
PO BOX 61, HAMILTON CENTRAL
QLD 4007 AUSTRALIA
T +61 734063000
E INFO@BNE.COM.AU
W BNE.COM.AU

Scale
AS ABOVE

Size
A1

Revision
A

Drawing Number	Project No.	Originator	Volume	Level	Type	Discipline	Number
	25021	- NRP	- XX	- XX	- DR	- CI	- 000231