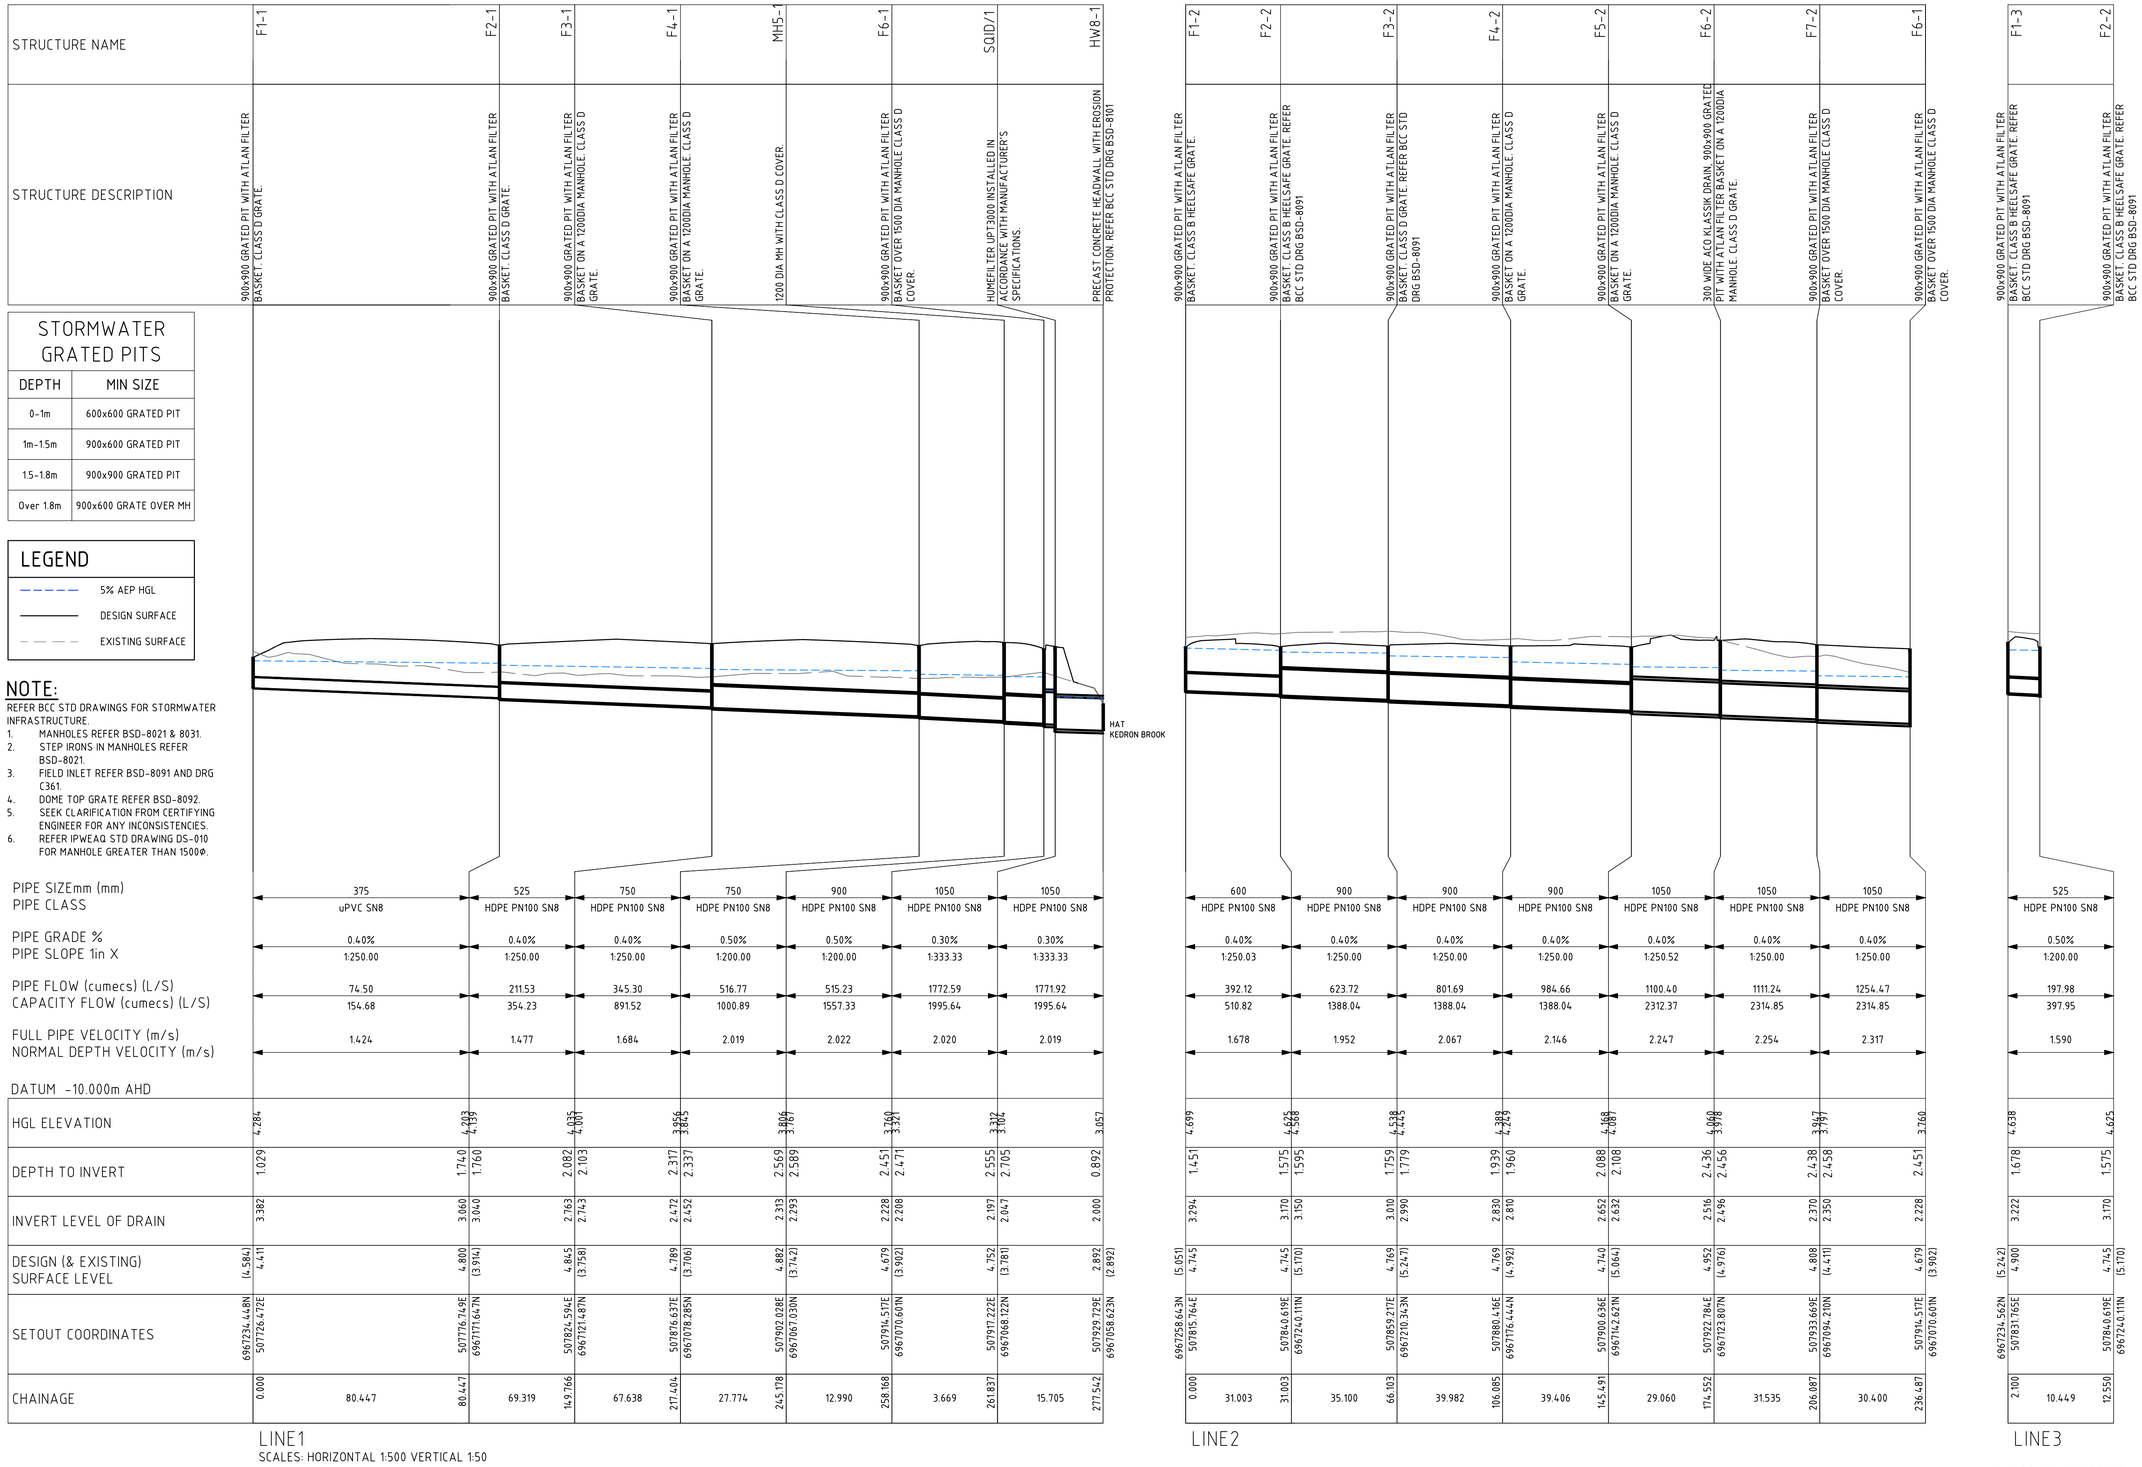


## STORMWATER GRATED PITS

| DEPTH | MIN SIZE |
|---|---|
| 0-1m | 600x600 GRATED PIT |
| 1m-1.5m | 900x600 GRATED PIT |
| 1.5-1.8m | 900x900 GRATED PIT |
| Over 1.8m | 900x600 GRATE OVER MH |

## LEGEND

- 5% AEP HGL
- DESIGN SURFACE
- EXISTING SURFACE

## NOTE:

REFER BCC STD DRAWINGS FOR STORMWATER INFRASTRUCTURE.

1. MANHOLES REFER BSD-8021 & 8031.
2. STEP IRONS IN MANHOLES REFER BSD-8021.
3. FIELD INLET REFER BSD-8091 AND DRG C361.
4. DOME TOP GRATE REFER BSD-8092.
5. SEEK CLARIFICATION FROM CERTIFYING ENGINEER FOR ANY INCONSISTENCIES.
6. REFER IPWEAQ STD DRAWING DS-010 FOR MANHOLE GREATER THAN 1500Ø.

COPYRIGHT :
REPRODUCTION OF WHOLE OR PART OF THIS DOCUMENT CONSTITUTES AN INFRINGEMENT OF COPYRIGHT. THE INFORMATION, IDEAS AND CONCEPTS CONTAINED IN THIS DOCUMENT ARE CONFIDENTIAL. THE RECIPIENT(S) OF THIS DOCUMENT IS PROHIBITED FROM DISCLOSING SUCH INFORMATION IDEAS AND CONCEPTS TO ANY PERSON WITHOUT THE PRIOR WRITTEN CONSENT OF THE BRISBANE AIRPORT CORPORATION PTY. LTD.

| DRN | AMENDMENTS | DATE | REV |
|---|---|---|---|
| JD | PRELIMINARY DESIGN 30% | 01.09.25 | A |
| JD | ISSUED FOR TENDER | 23.12.25 | B |
| JD | ISSUED FOR TENDER | 28.01.26 | C |
| LQ | ISSUED FOR TENDER | 30.01.26 | D |
| MM | ISSUED FOR APPROVAL | 11.06.26 | E |

XENIA

NORTHROP
Brisbane
The Annex, Level 8, 12 Creek Street, Brisbane QLD 4000
GPO BOX 423 Brisbane QLD 4001
(07) 3365 0400 brisbane@northrop.com.au
ABN 81 094 433 100

| | |
|---|---|
| Drawn M.MANLAPIT 11.06.26 | Checked A.TATHAM 11.06.26 |
| Design Coordinated R.MITCHELL 11.06.26 | Compliance Checked S.KILLORAN 11.06.26 |
| Authorised For Issue S.KILLORAN 11.06.26 | Construction Checked N/A |

**SKYGATE PLAY**
**BRISBANE AIRPORT**

STORMWATER DRAINAGE
LONGITUDINAL SECTIONS

Brisbane Airport
BRISBANE AIRPORT CORPORATION PTY LTD
11 THE CIRCUIT, BRISBANE AIRPORT QLD 4008
PO BOX 61, HAMILTON CENTRAL QLD 4007 AUSTRALIA
T +61734063000
E INFO@BNE.COM.AU
W BNE.COM.AU

Scale AS ABOVE
Size A1
Revision E

| Drawing Number | Project No. | Originator | Volume | Level | Type | Discipline | Number |
|---|---|---|---|---|---|---|---|
| | 25021 | NRP | XX | XX | DR | CI | 000321 |