
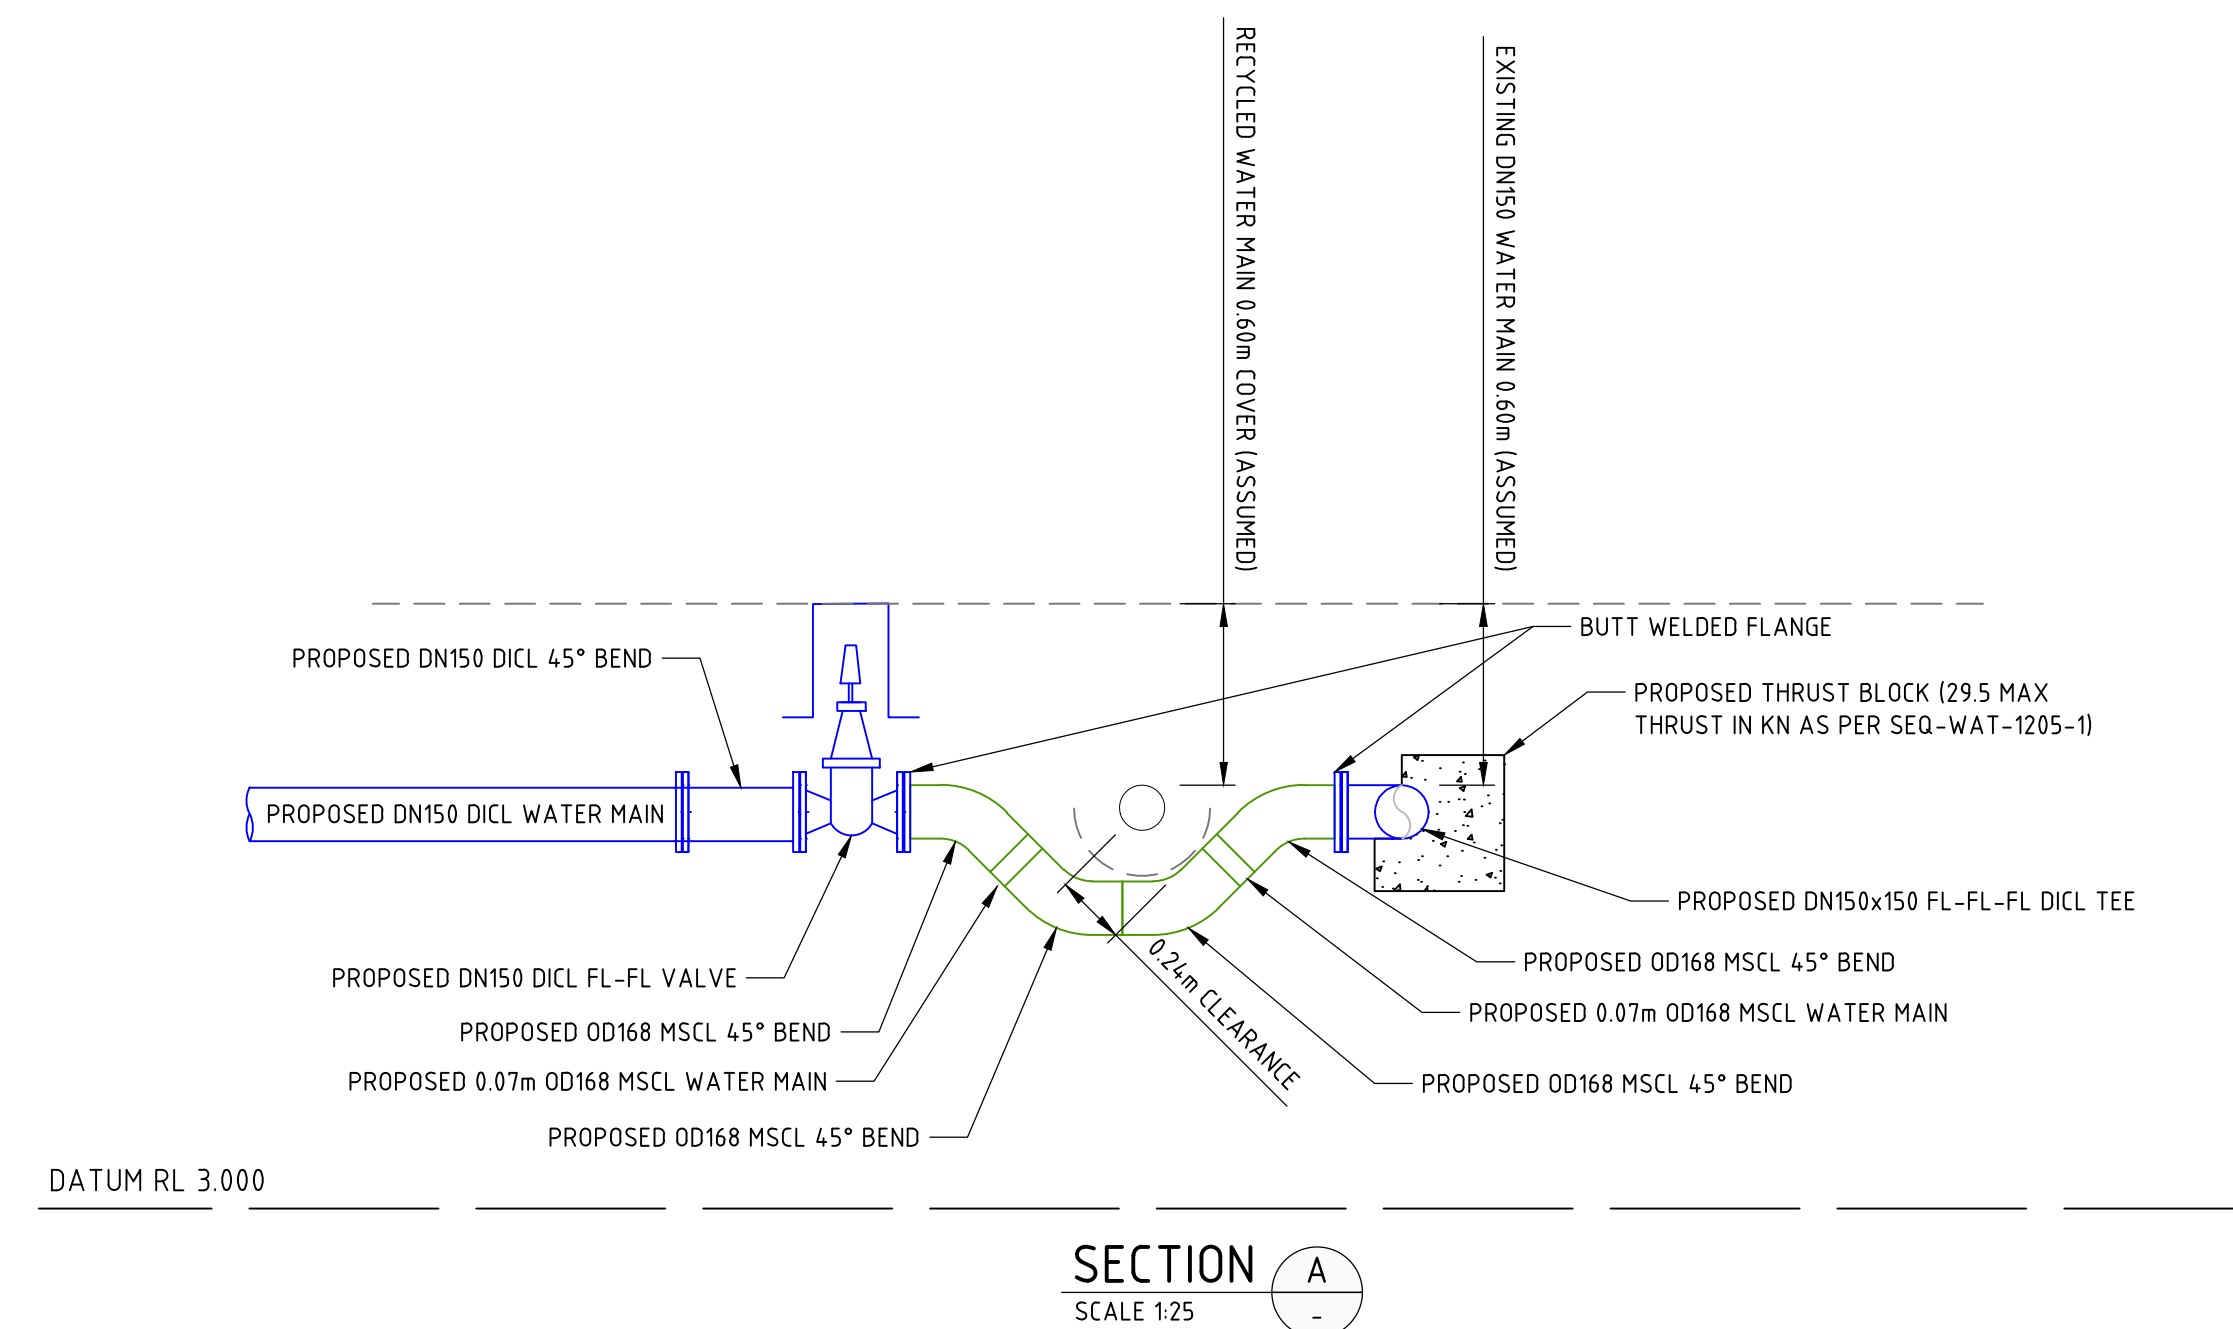
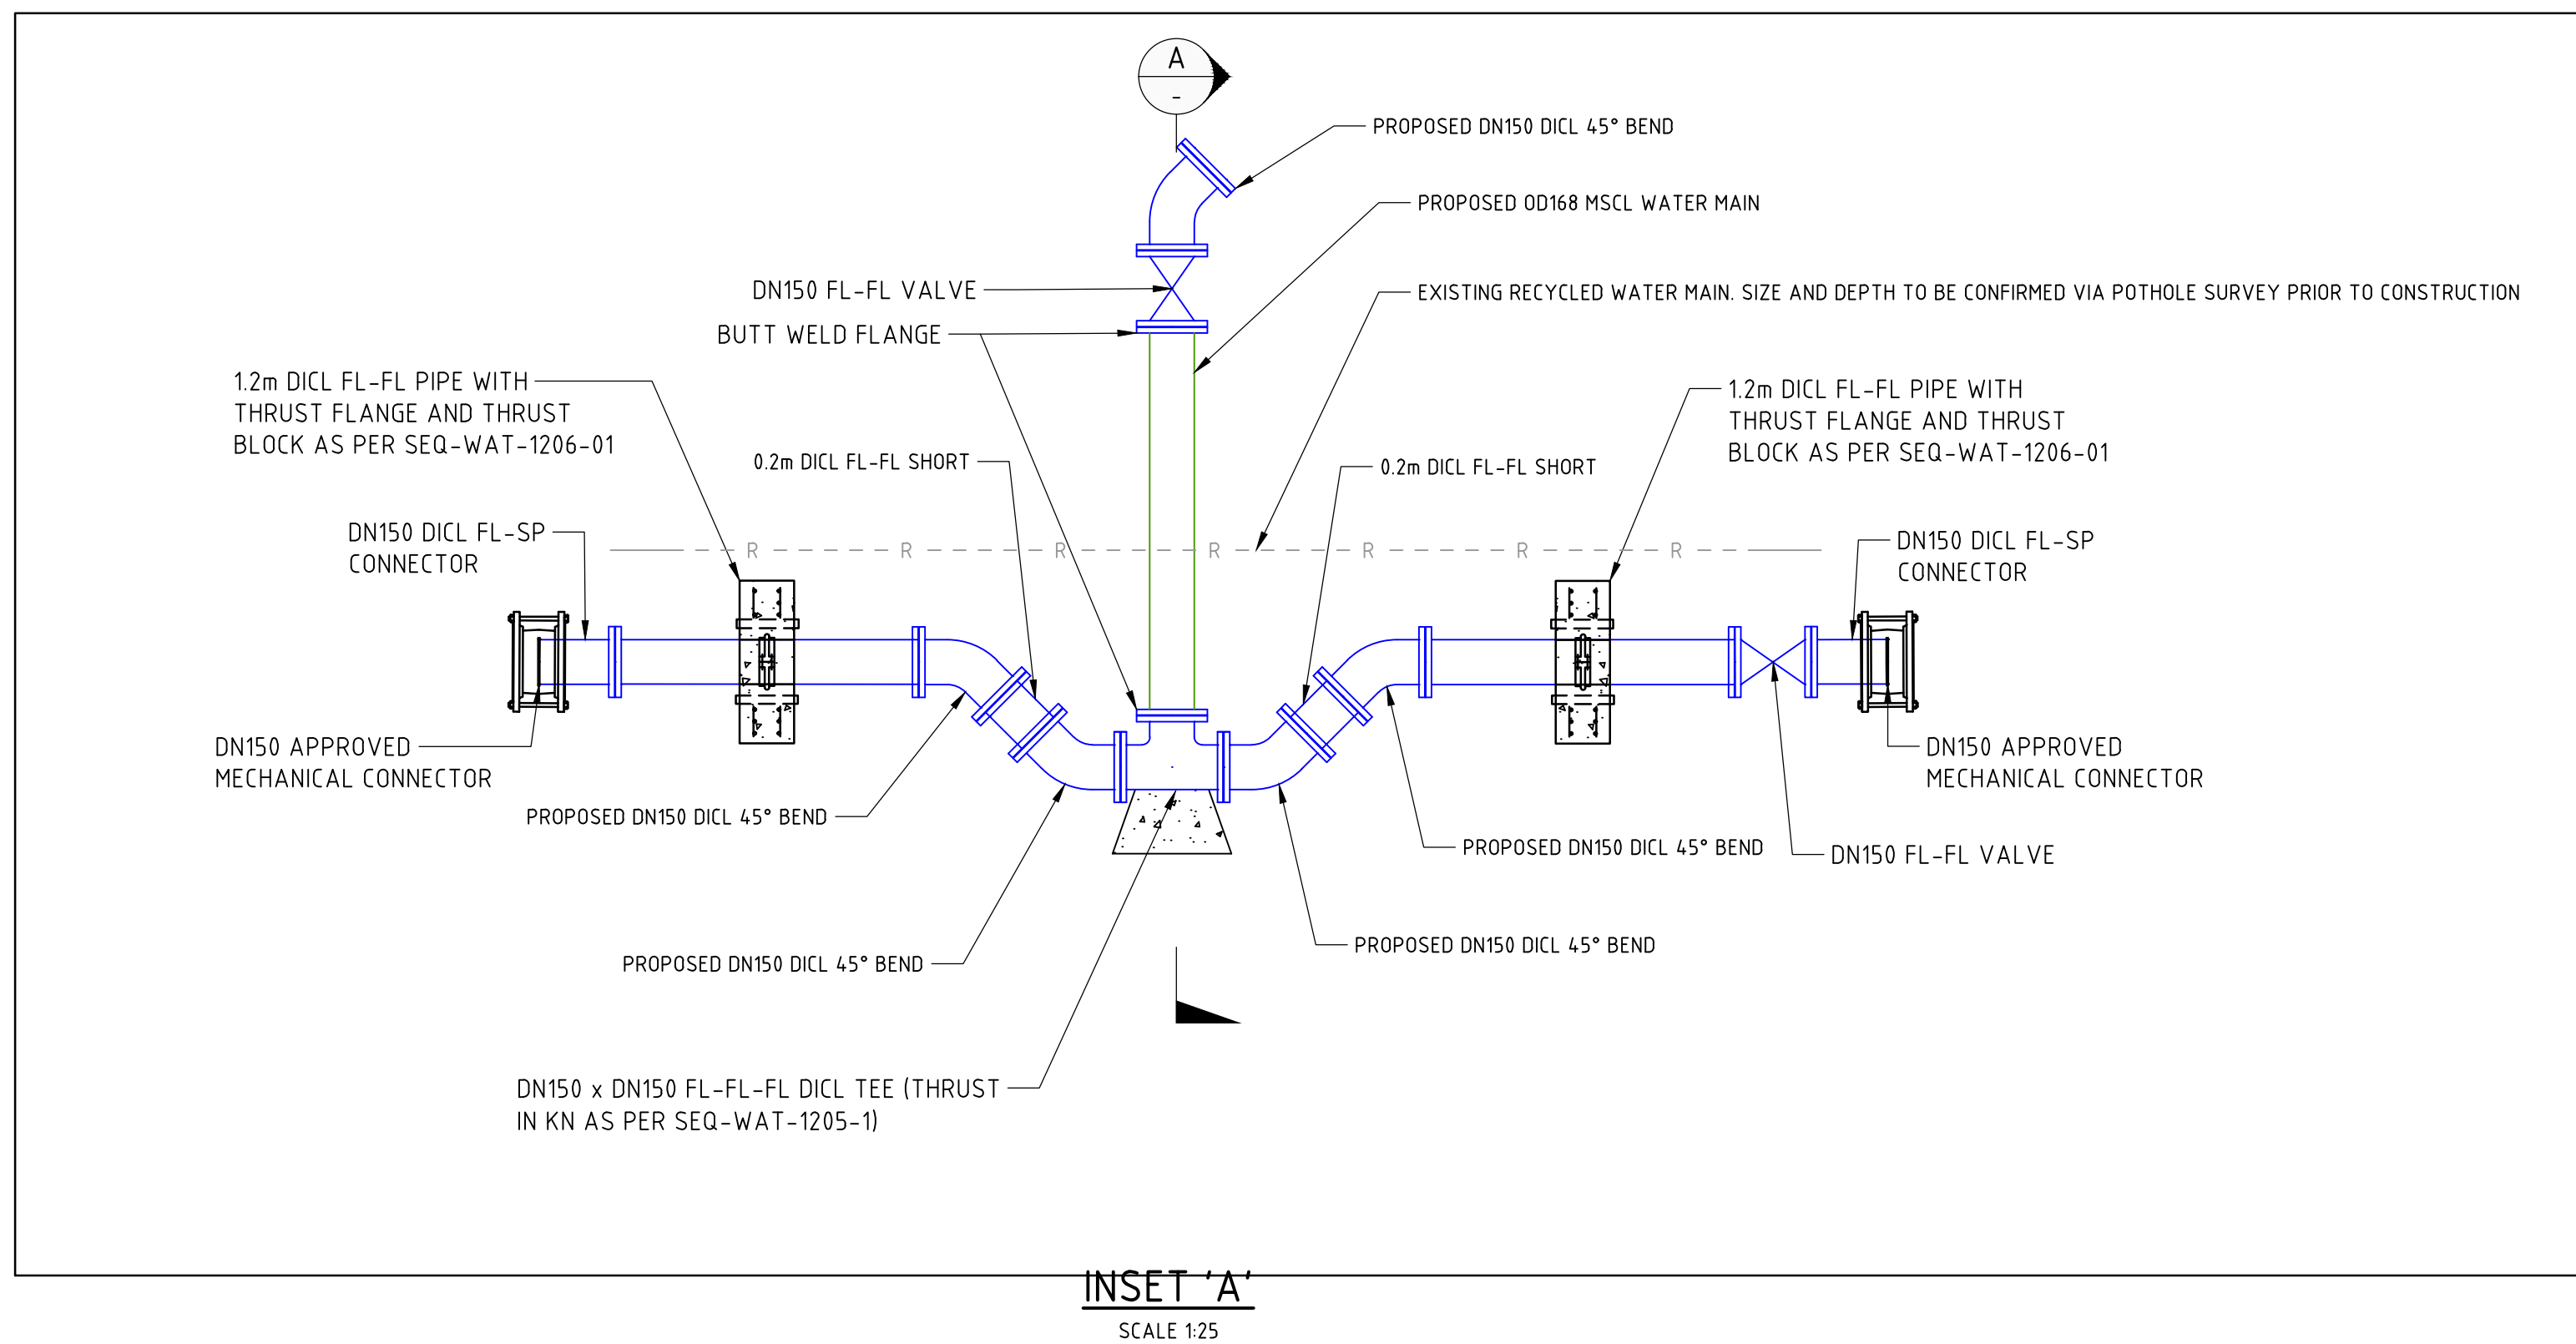
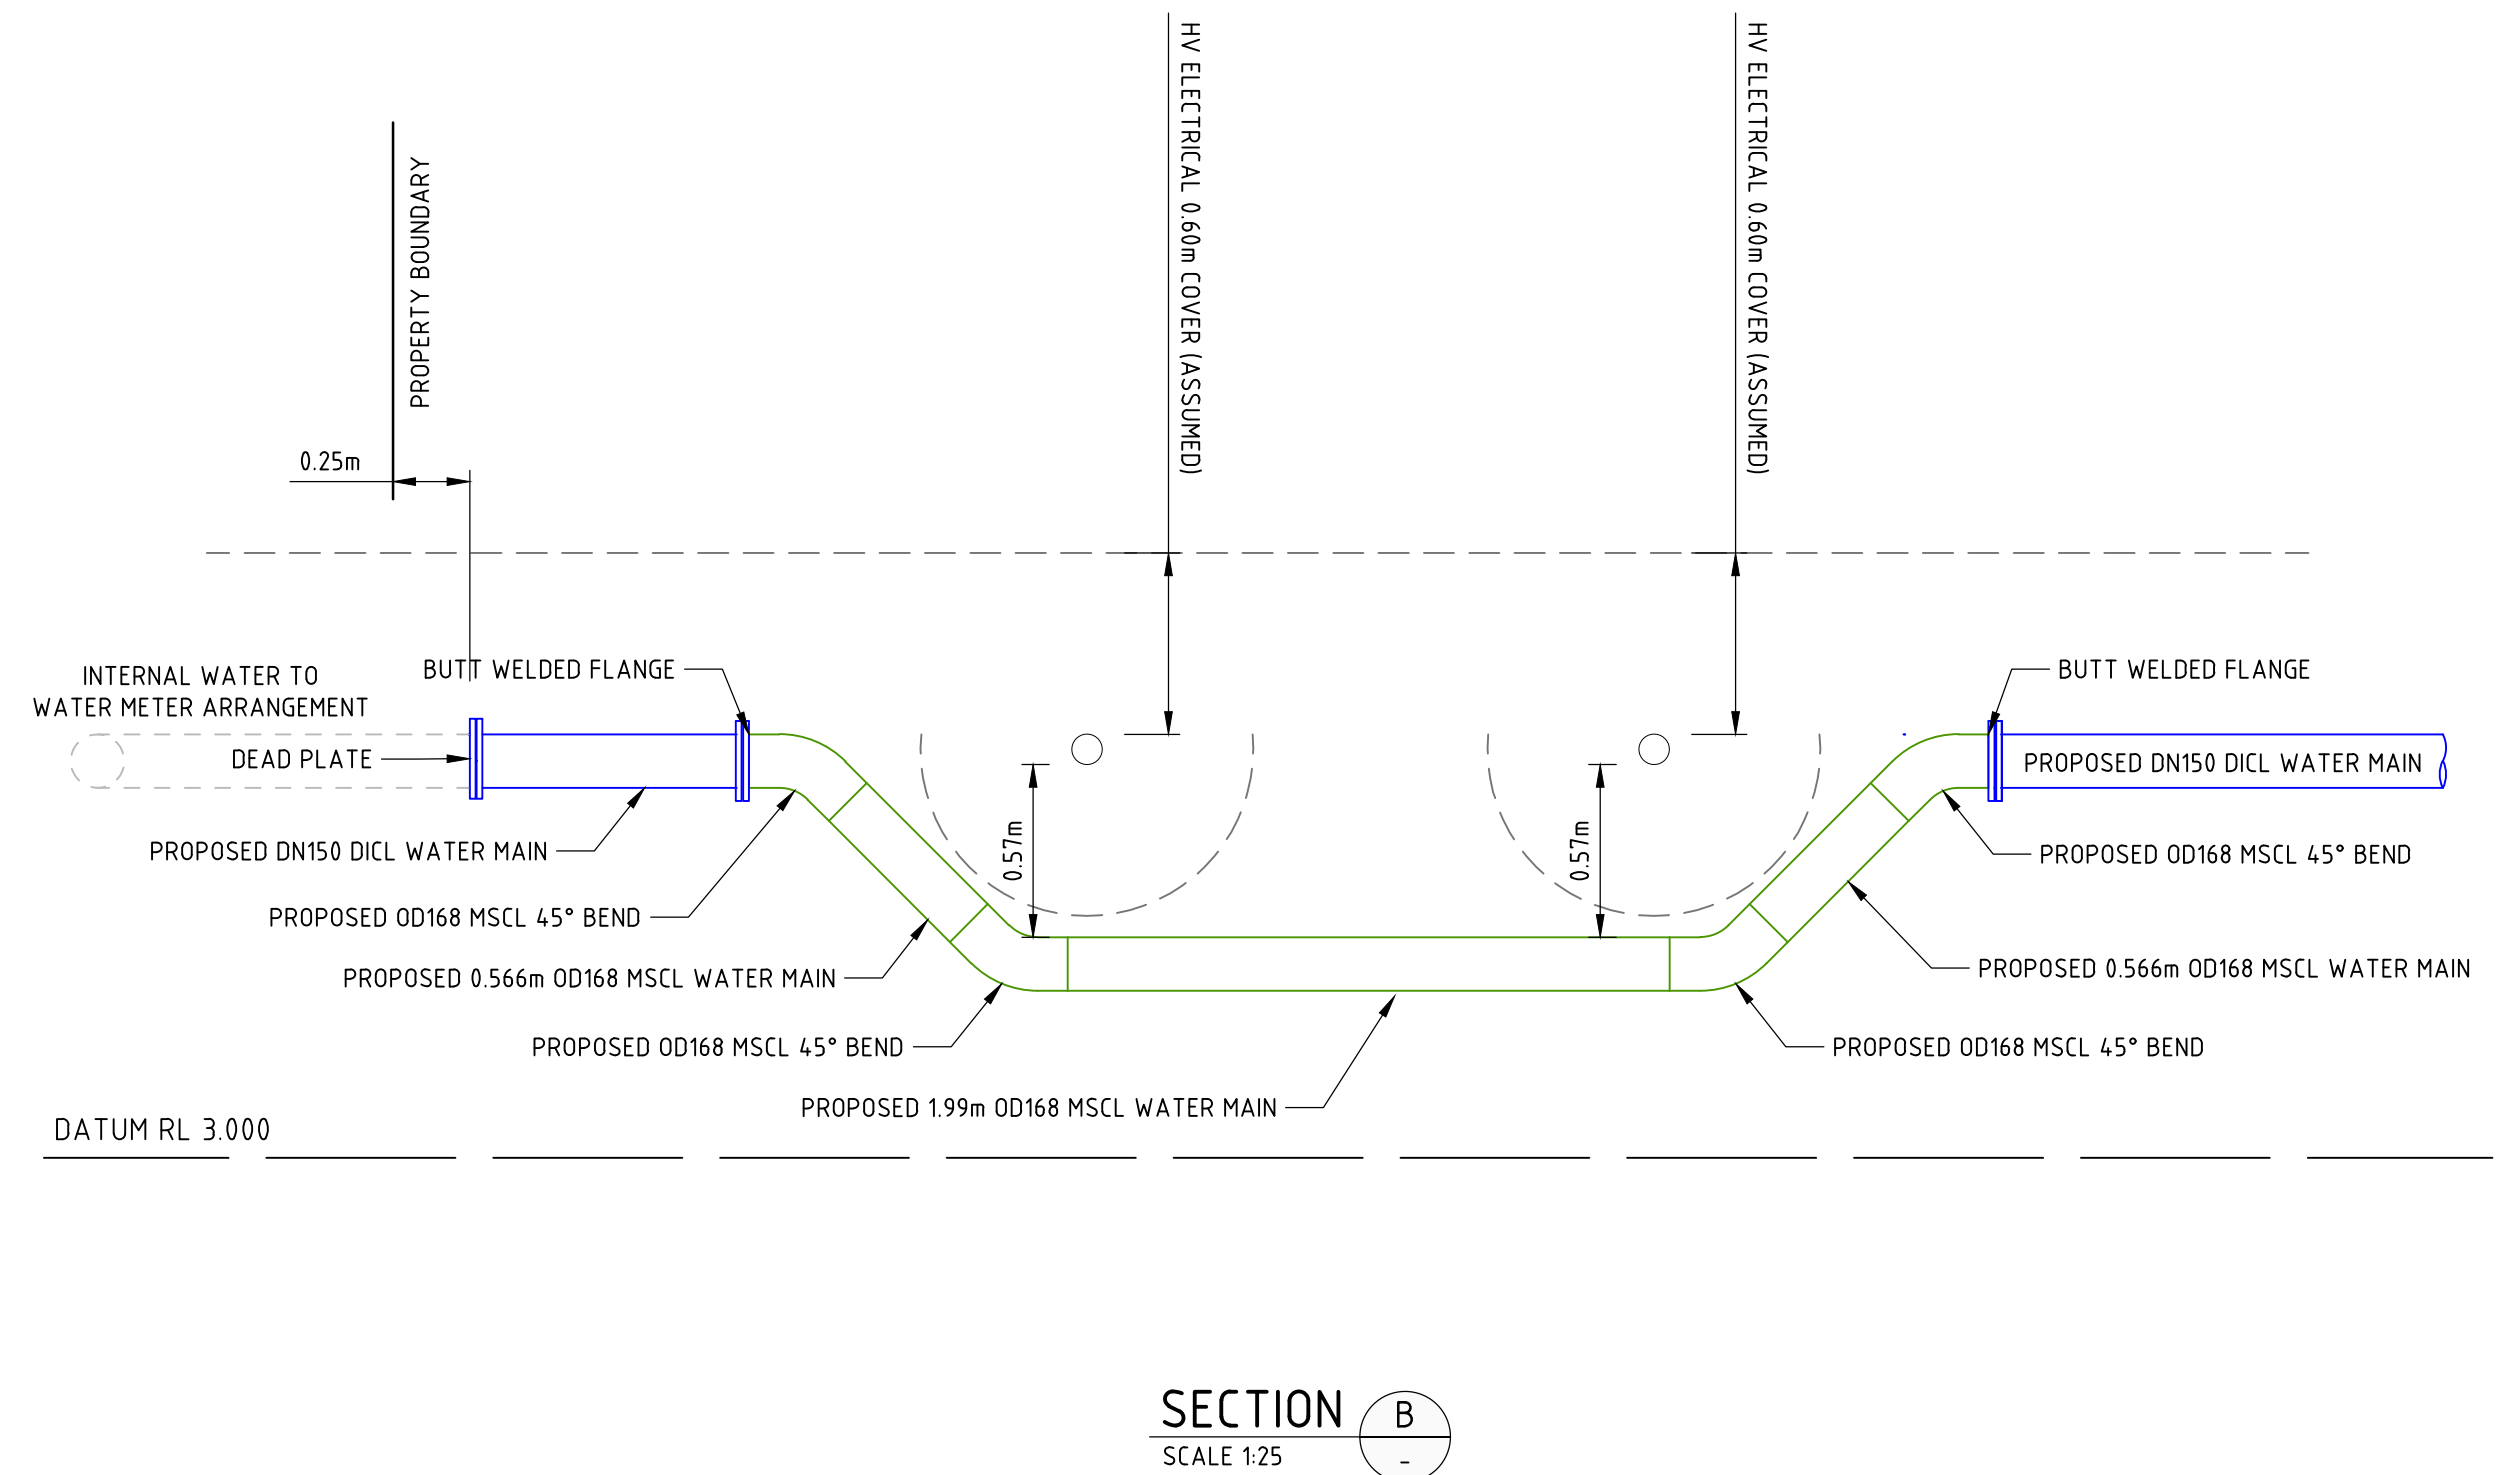


NOTE: POTHOLE SURVEY REQUIRED FOR EXISTING SERVICES AT PROPOSED CONNECTION LOCATION. LEVELS TO BE PROVIDED TO ENGINEER TO CONFIRM PROPOSED CONNECTION DETAILS PRIOR TO CONSTRUCTION.

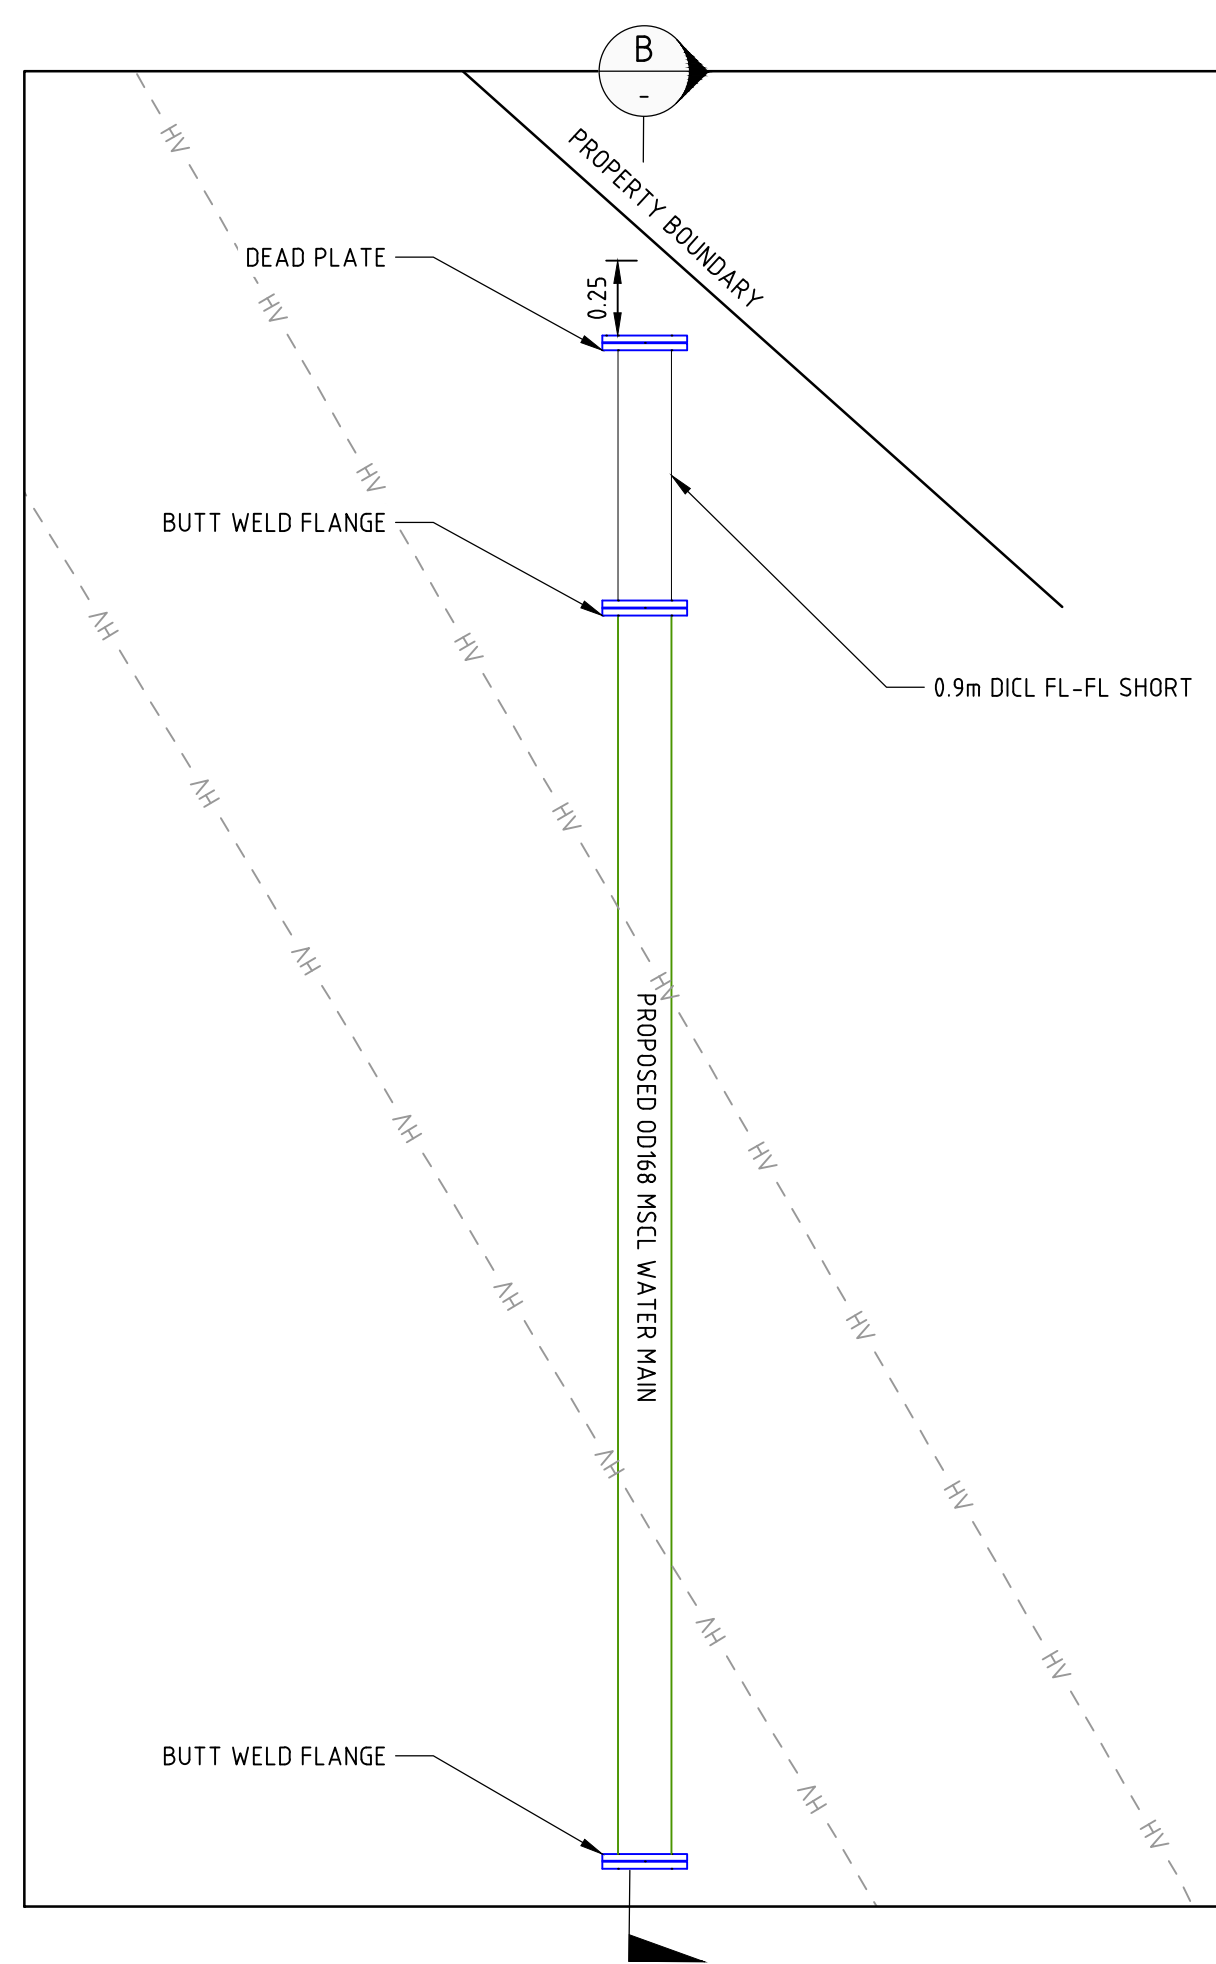

FOR APPROVAL

SCALE 1:25@A1

COPYRIGHT : REPRODUCTION OF WHOLE OR PART OF THIS DOCUMENT CONSTITUTES AN INFRINGEMENT OF COPYRIGHT. THE INFORMATION IDEAS AND CONCEPTS CONTAINED IN THIS DOCUMENT ARE CONFIDENTIAL. THE RECIPIENT(S) OF THIS DOCUMENT IS PROHIBITED FROM DISCLOSING SUCH INFORMATION IDEAS AND CONCEPTS TO ANY PERSON WITHOUT THE PRIOR WRITTEN CONSENT OF THE BRISBANE AIRPORT CORPORATION PTY. LTD	MM	ISSUED FOR APPROVAL	11.06.26	A
	DRN	AMENDMENTS	DATE	REV

XENIA

NORTHROP
Brisbane
The Annex, Level 8, 12 Creek Street, Brisbane QLD 4000
GPO BOX 423 Brisbane QLD 4001
(07) 3365 0400 brisbane@northrop.com.au
ABN 81 094 433 100

Drawn	M.MANLAPIT
Design Coordinated	R.MITCHELL
Authorised For Issue	S.KILLORAN

Checked A.TATHAM 11.06.26	
Compliance Checked S.KILLORAN 11.06.26	
Construction Checked N/A	

SKYGATE PLAY BRISBANE AIRPORT WATER RETICULATION DETAILS



BRISBANE AIRPORT CORPORATION PTY LTD
11 THE CIRCUIT, BRISBANE AIRPORT QLD 4008
PO BOX 61, HAMILTON CENTRAL
QLD 4007 AUSTRALIA
T +61734063000
E INFO@BNE.COM.AU
WBNE.COM.AU

Scale	AS ABOVE
Size	A1
Revision	A

Drawing Number	Project No.	Originator	Volume	Level	Type	Discipline	Number
	25021	- NRP	- XX	- XX	- DR	- CI	- 000502