


ESC LEGEND:

ROCK PAD CONSTRUCTION ENTRANCE TO
IECA STD. DRG. EXIT-01

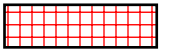

SEDIMENT FENCE TO IECA STD. DRGS.
SF-1 AND SF-02




GULLY INLET PROTECTION
SEDIMENT TRAP REFER DR-07 FOR
DETAILS




LEGEND

	EXISTING PROPERTY BOUNDARY
	EXISTING CONTOUR MAJOR
	PROPOSED CONTOUR MINOR
	EXISTING ELECTRICITY
	EXISTING ELECTRICITY (UNDERGROUND)
	EXISTING ELECTRICITY (HIGH VOLTAGE)
	EXISTING WATER
	EXISTING RECYCLE WATER
	EXISTING IRRIGATION
	EXISTING STORMWATER
	EXISTING SEWER MAIN
	EXISTING SEWER MAIN (RAISING MAIN)
	EXISTING COMMUNICATION
	PROPOSED RETAINING WALL
	WORKS BOUNDARY
	PROPOSED CONCRETE HARDSTAND PAVEMENT IN ACCORDANCE WITH STRUCTURAL ENGINEERS SPECIFICATION
	PROPOSED BUILDING. REFER TO ARCHITECTURAL DRAWINGS FOR DETAILS.
	PROPOSED LANDSCAPE AREA. REFER TO LANDSCAPE DRAWINGS FOR DETAILS
	PROPOSED 600mm AC REINSTATEMENT STRIP REFER TO DWG C-220 FOR DETAILS
	PROPOSED CONCRETE FOOTPATH IN ACCORDANCE WITH IPWEA STD DRG PSD-302
	PROPOSED PRECAST CONCRETE ISLAND REFER TO CIVILMART DWG 0913R FOR DETAILS
	PROPOSED WATER MAIN
	PROPOSED SEWER MAIN
	PROPOSED INTEGRAL KERB REFER TO DRAWING C-220
	PROPOSED ROOF EXTEND REFER TO ARCHITECTURAL DWG FOR DETAILS
	PROPOSED STORMWATER DRAINAGE
	PROPOSED STORMWATER HEADWALL
	PROPOSED STORMWATER MANHOLE
	PROPOSED STORMWATER PIT
	PROPOSED STORMWATER STRUCTURE NUMBER
	PROPOSED SEWER STRUCTURE NUMBER

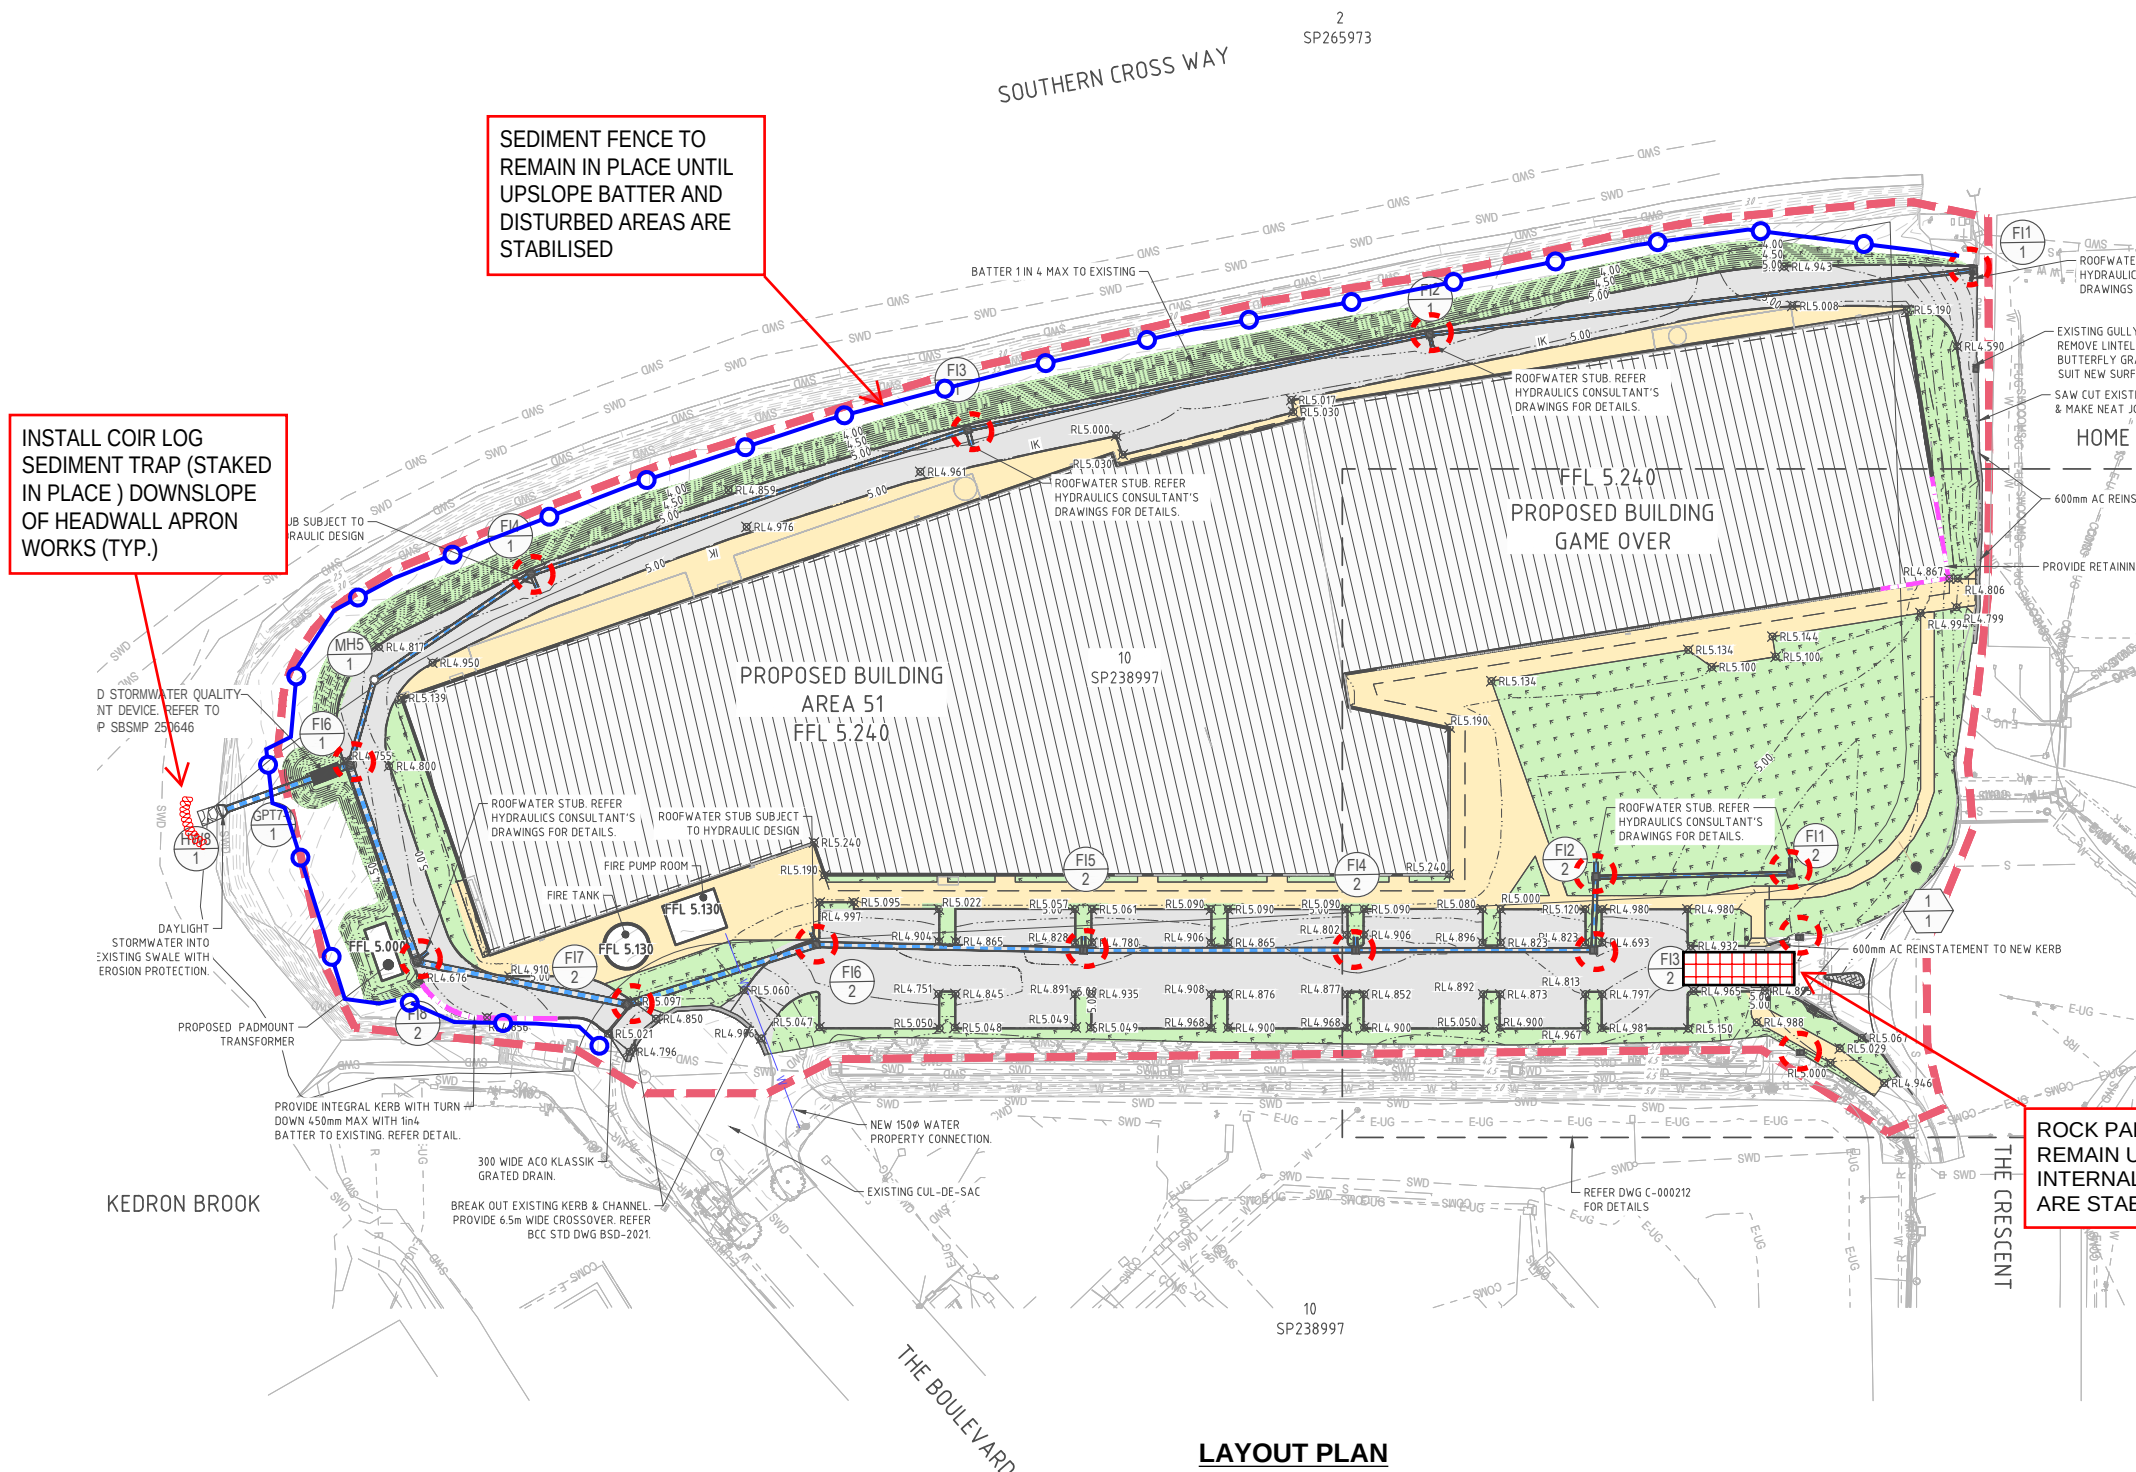

ORIGINAL DRAWINGS PROVIDED BY NORTHROP CONSULTING ENGINEERS

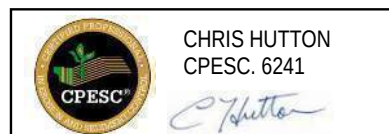

89 CASLICK LANE,
BROADWATER, QLD.
PH: (MOB) 0400 643 883

APPROVED
DATE
26-05-2026
CHRIS HUTTON - CPESC No. 6241

CLIENT
NORTHROP CONSULTING ENGINEERS

PROJECT
SKYGATE PLAY

LOCATION
LOT SKG26, THE CIRCUIT, BRISBANE AIRPORT

DRAWING TITLE
EROSION AND SEDIMENT CONTROL - CIVIL WORKS AND STABILISATION PHASE

JOB No.
ESC-0606

DRAWING No. / REVISION
DR-06 / a