


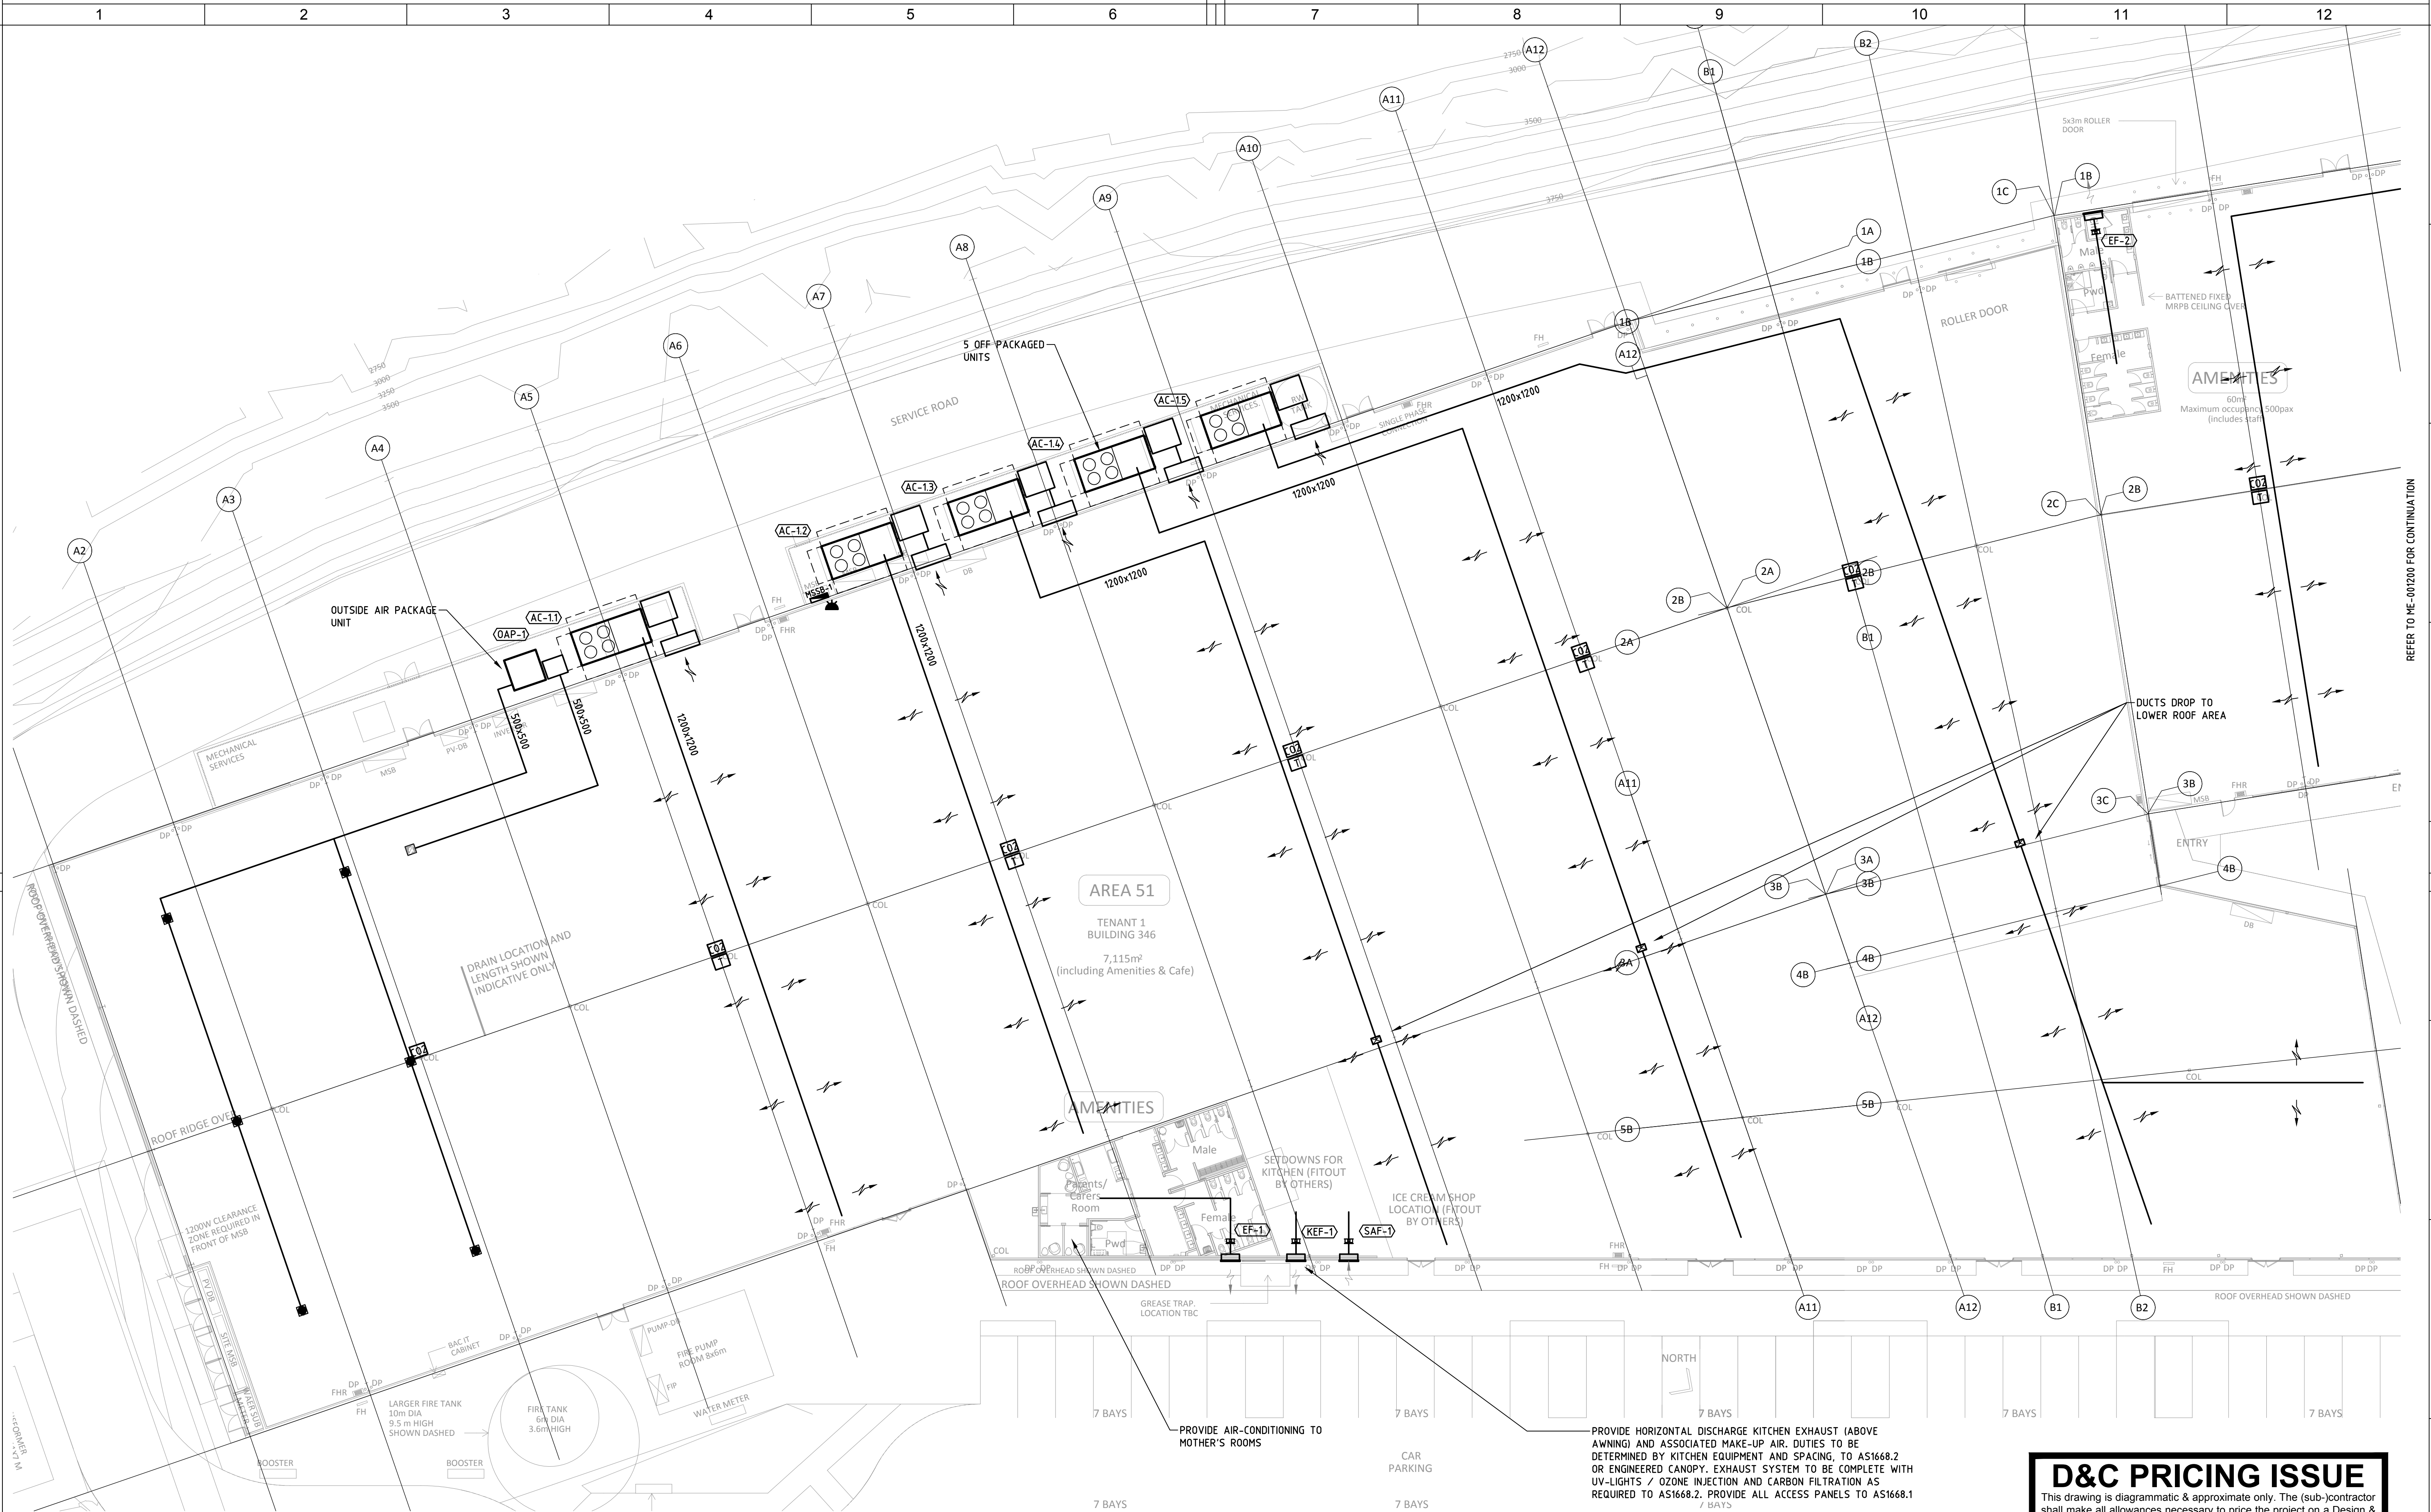

revision notes

Copyright :
REPRODUCTION OF WHOLE OR PART OF
THIS DOCUMENT CONSTITUTES AN
INFRINGEMENT OF COPYRIGHT. THE
INFORMATION, IDEAS AND CONCEPTS
CONTAINED IN THIS DOCUMENT ARE
CONFIDENTIAL. THE RECIPIENT(S) OF THIS
DOCUMENT IS PROHIBITED FROM
DISCLOSING SUCH INFORMATION IDEAS
AND CONCEPTS TO ANY PERSON WITHOUT
THE PRIOR WRITTEN CONSENT OF THE
BRISBANE AIRPORT CORPORATION PTY. LTD

NB

DH

DRN

D&C PRICING ISSUE

04/02/26

B

D&C PRICING ISSUE

17/12/25

A

AMENDMENTS

DATE

REV

Ashburner
Francis

T 07 3510 8888

E brisbane@ashburnerfrancis.com.au

877 Stanley Street East, East Brisbane QLD 4168

BRISBANE | TOOWOOMBA | TOWNSVILLE | DARWIN

Archipelago

Level 5, 188 George Street, Brisbane QLD 4000

T +61 7 3238 4848 www.archipelago.com.au

© ARCHPELAGO ARCHITECTS PTY LTD. All Rights Reserved

This work is copyright and cannot be reproduced or copied by any means without written
permission of Archipelago Architects Pty Ltd. Any
unauthorised use of this document for any purpose
whatsoever is prohibited in the terms of the agreement between Archipelago Architects Pty
Ltd and the retaining party.

Drawn
DH

Design Coordinated

Authorised For Issue

Checked
SS

Compliance Checked

Construction Checked

SKYGATE PLAY
THE CIRCUIT, BRISBANE AIRPORT

MECHANICAL SERVICES
GROUND FLOOR - AIR CONDITIONING
AND VENTILATION LAYOUT 1

Brisbane
Airport

Project No.

Originator

Volume

Level

Type

Role

Number

25021

-

ASH

-

XX

-

XX

-

DR

-

ME

-

001100

Scale
1:200

Size
A1

Revision
B

D&C PRICING ISSUE

This drawing is diagrammatic & approximate only. The (sub-)contractor shall make all allowances necessary to price the project on a Design & Construct methodology. Where items are not specifically shown or included, but are required, the (sub-)contractor shall make all allowances for such items to ensure compliant system(s) are provided that satisfy the client's expectations & operational requirements.

File:

Pentable:

Printer:

User:

Plot Date & Time: