


STEELWORK PLAN NOTES

1. REFER S0.001-S0.003 FOR CONSTRUCTION NOTES
2. UNLESS NOTED OTHERWISE ON PLAN LOADS AS FOLLOWS:

ROOF LIVE LOADS	
GENERAL	25 kg/m²
SUPERIMPOSED DEAD LOAD	
ROOF SHEETING	6 kg/m²
CEILING AND INSULATION	15 kg/m²
SERVICES	15 kg/m²
SOLAR	10 kg/m²

3. ALL EXTERNAL STEELWORK TO BE HOT DIPPED GALVANISED


STEELWORK LEGEND

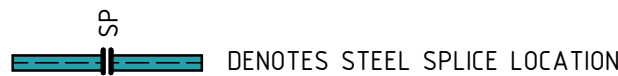

DENOTES STEEL SPLICE LOCATION


MEMBER SCHEDULE

MARK	SIZE
COLUMN	
SC119	410 UB 53.7
SC120	410 UB 59.7
SC121	460 UB 67.1
SC122	460 UB 74.6
SC124	530 UB 82.0
SC440	150 x 150 x 5.0 SHS
SC444	200 x 200 x 6.0 SHS
HANGING COLUMN	
HC444	200 x 200 x 6.0 SHS
MULLION	
M308	250 PFC
M433	100 x 100 x 5.0 SHS
BEAM	
B308	250 PFC
B309	300 PFC
OUTRIGGER	
OR308	250 PFC
RAFTER	
R108	200 UB 25.4
R114	310 UB 40.4
R116	360 UB 44.7
R117	360 UB 50.7
R119	410 UB 53.7
R120	410 UB 59.7
R121	460 UB 67.1
R122	460 UB 74.6
R124	530 UB 82.0
R125	530 UB 92.4
R126	610 UB 101
R308	250 PFC
R309	300 PFC
RAKING ANGLE	
RA728	90 x 90 x 8 EA
ROOF BRACING	
RB725	75 x 75 x 8 EA
STRUT	
S440	150x150x5.0SHS
S444	200x200x6.0SHS
WALL BRACING	
WB430	89x89x6.0SHS
WB725	75 x 75 x 8 EA
WALL HEAD	
WH433	100x100x5.0SHS
WH437	125x125x5.0SHS

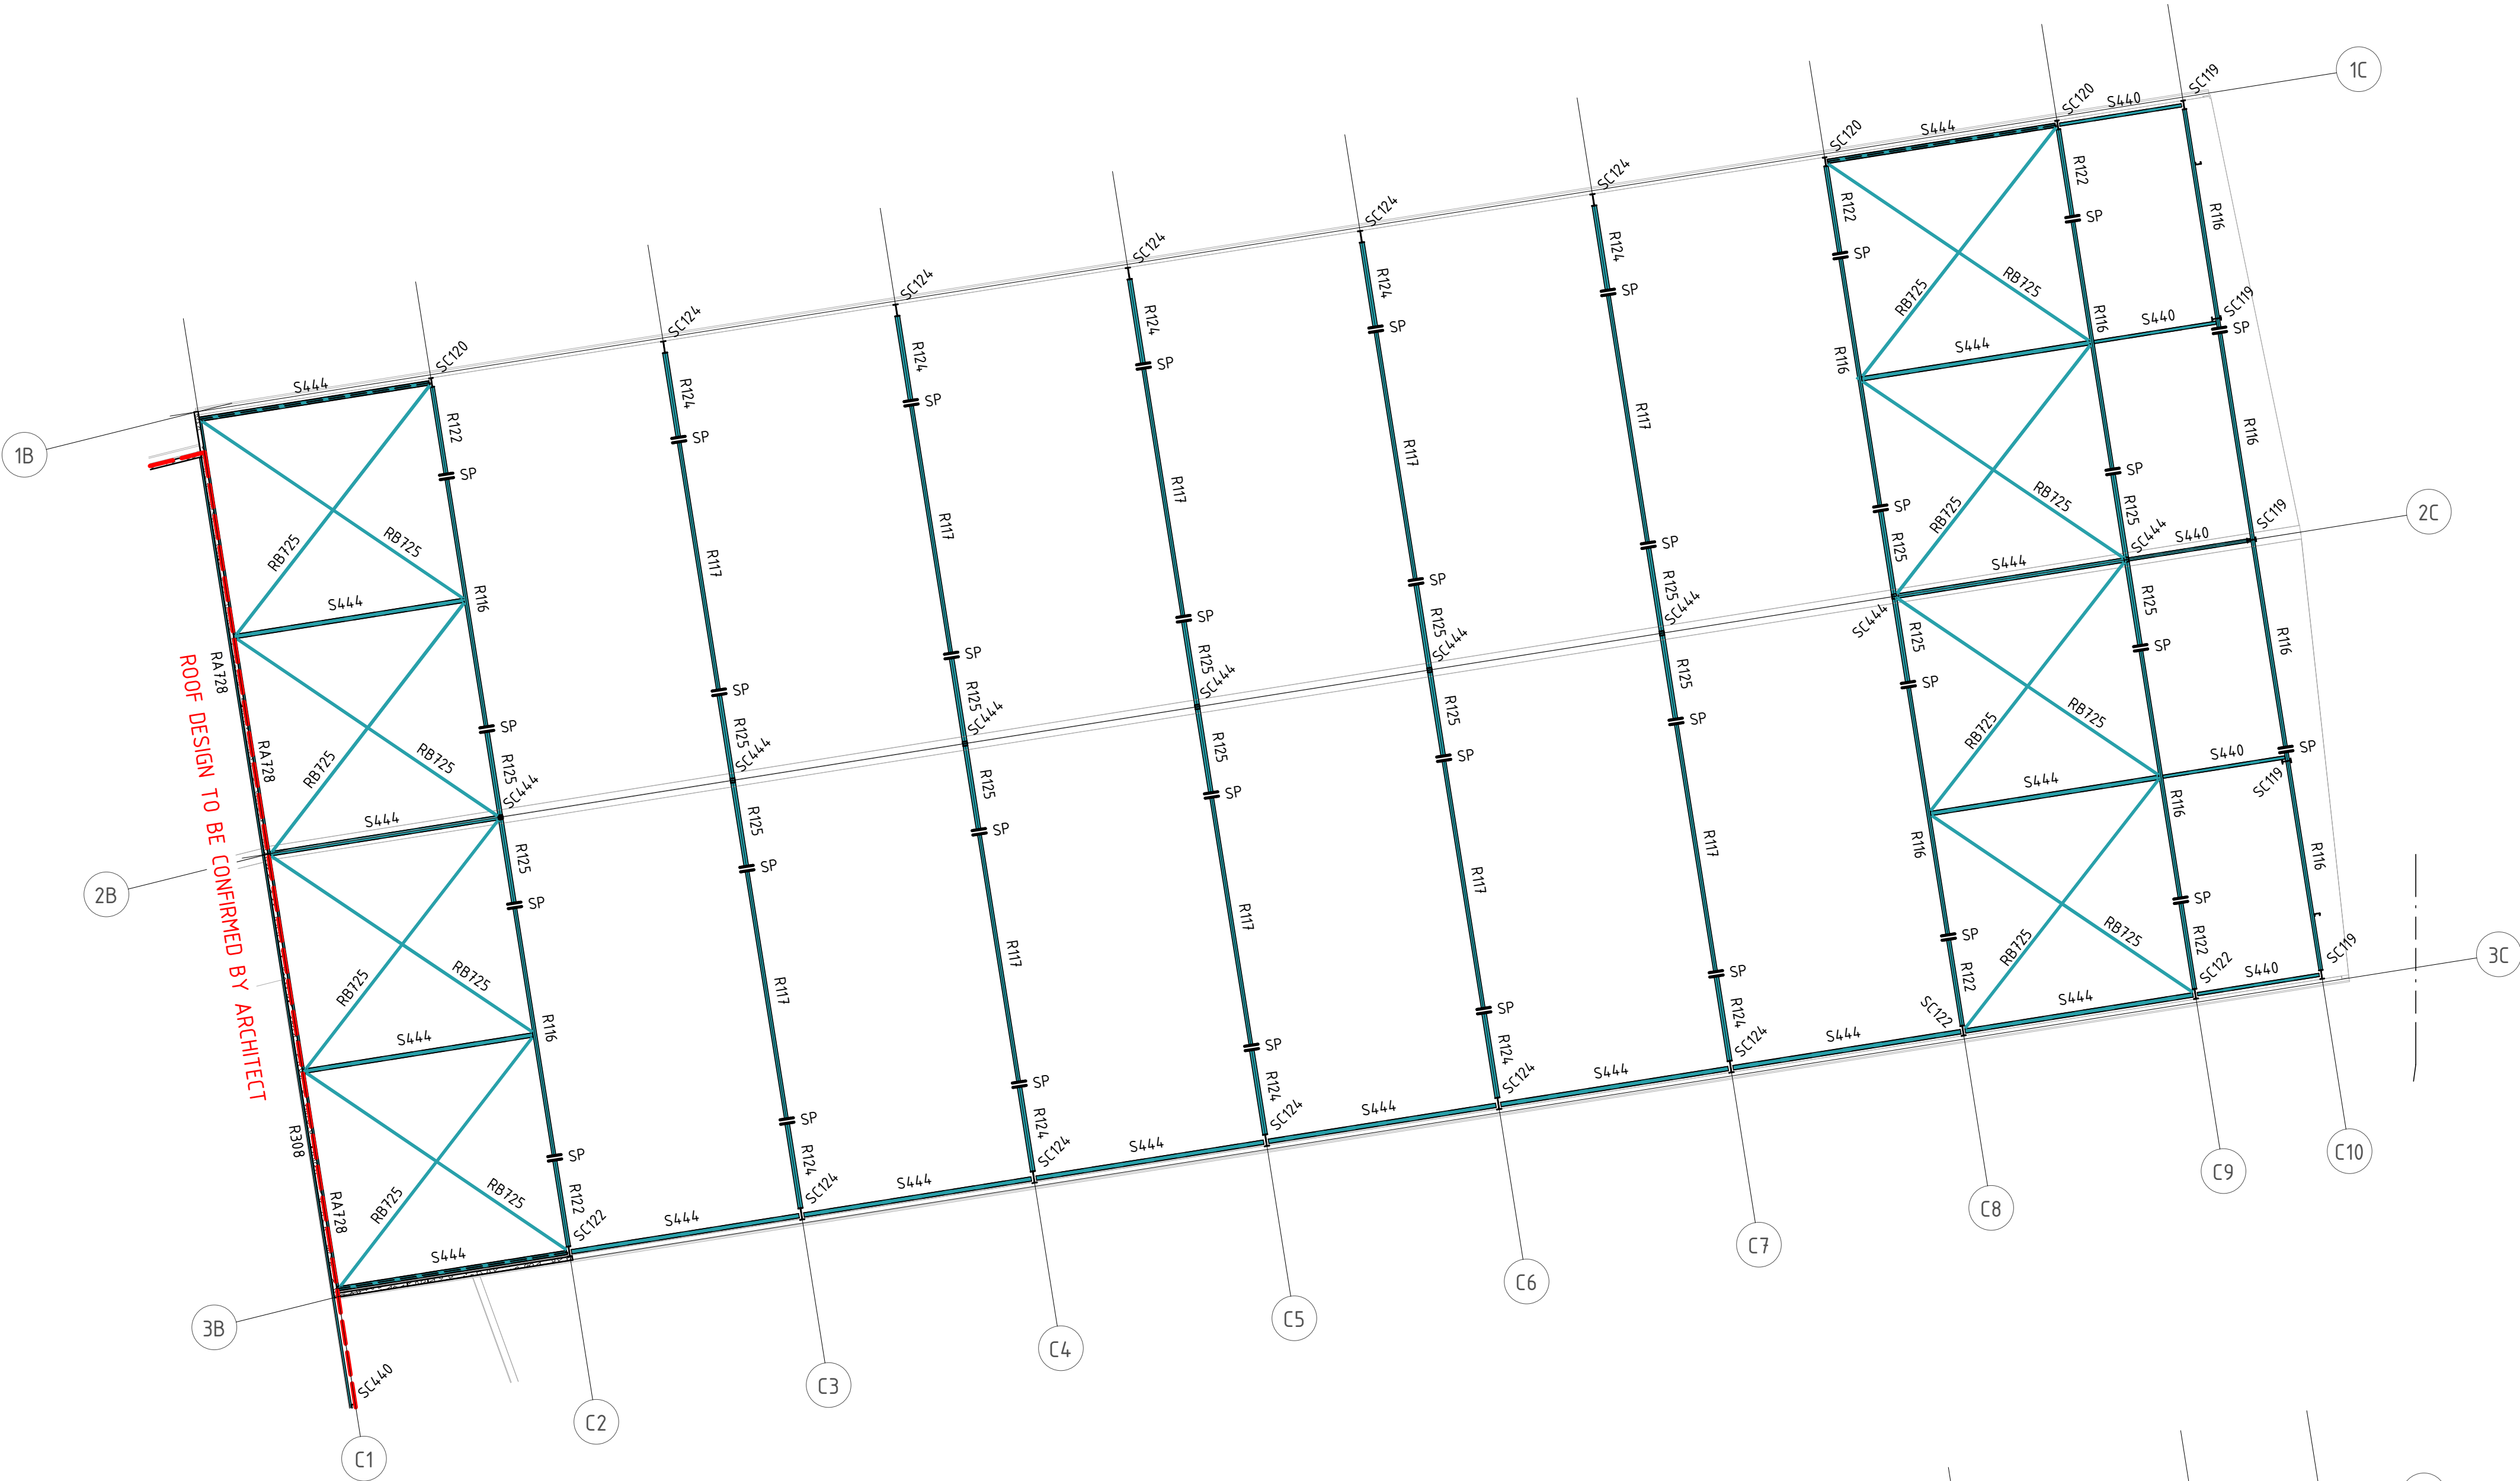

UPPER FRAMING ROOF PLAN - PART 3

SCALE 1 : 200

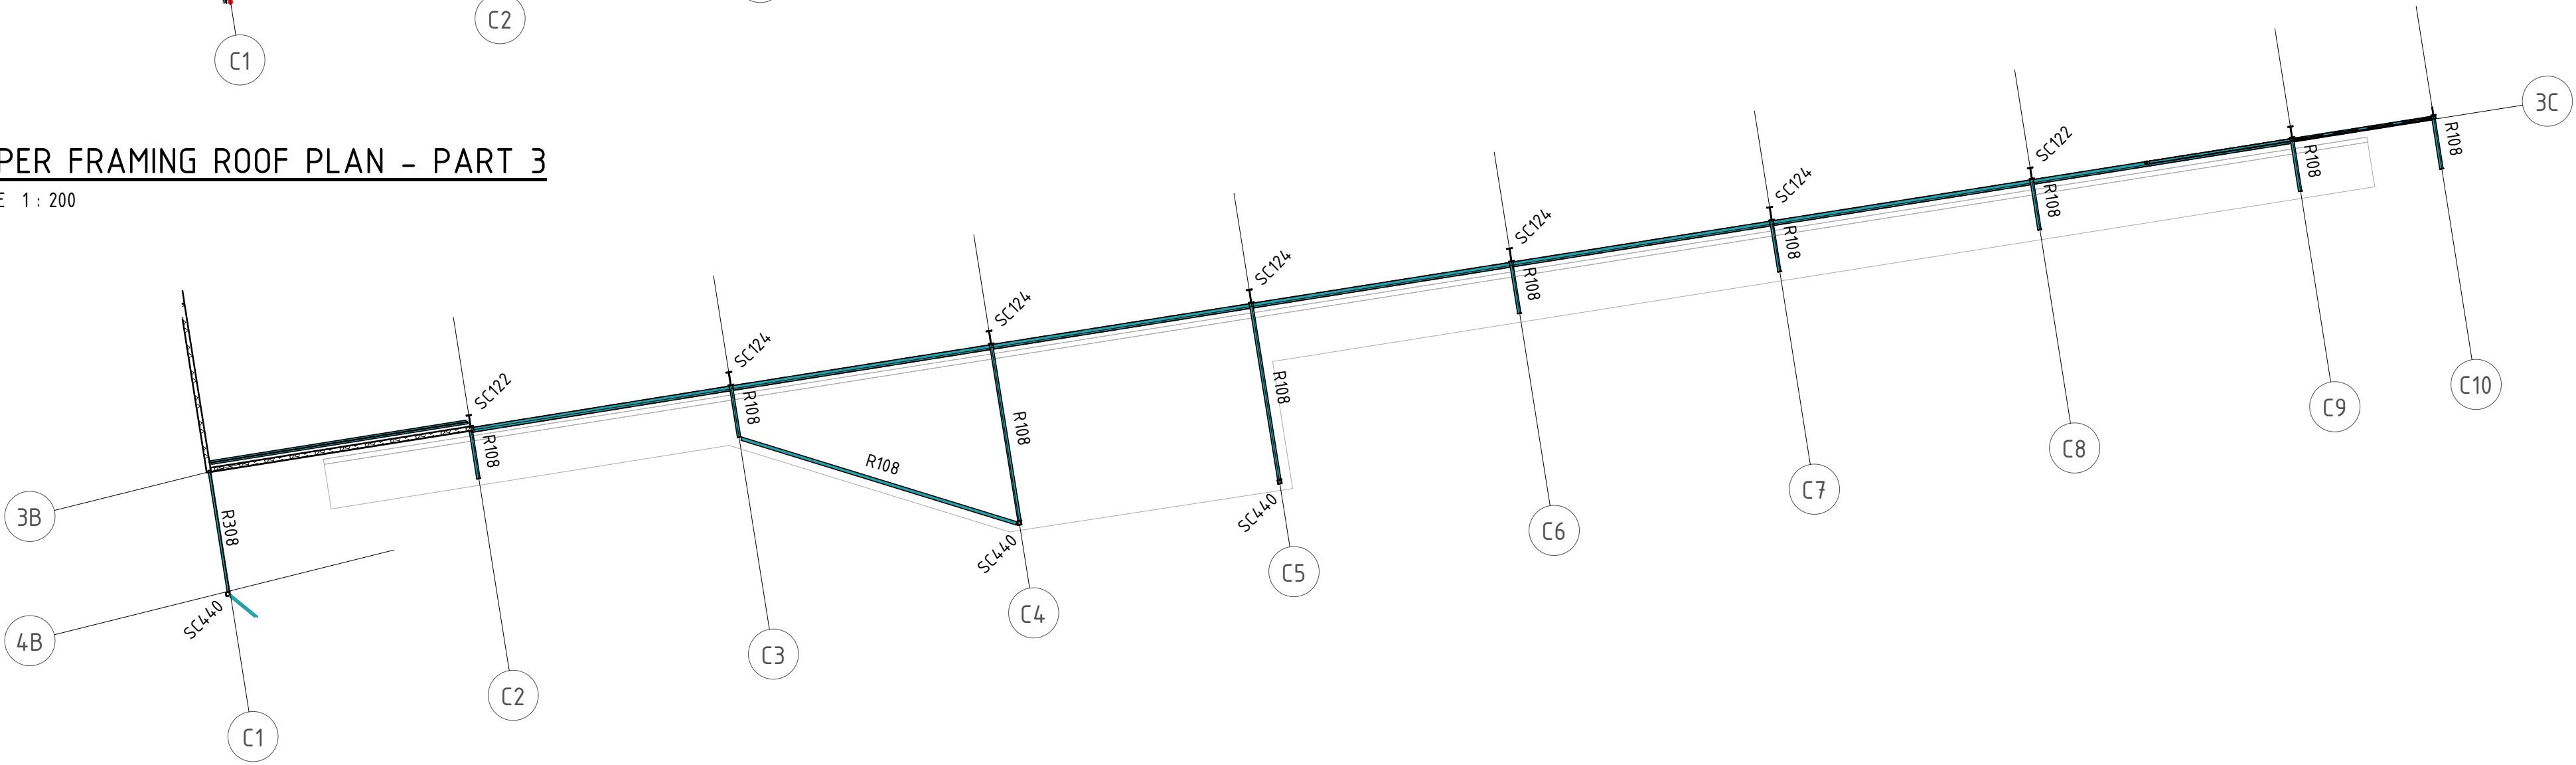

LOWER FRAMING ROOF PLAN - PART 2

SCALE 1 : 200

COPYRIGHT :
REPRODUCTION OF WHOLE OR PART OF THIS
DOCUMENT CONSTITUTES AN INFRINGEMENT
OF COPYRIGHT. THE INFORMATION, IDEAS,
AND CONCEPTS CONTAINED IN THIS
DOCUMENT ARE CONFIDENTIAL. THE
RECIPIENT(S) OF THIS DOCUMENT IS
PROHIBITED FROM DISCLOSING SUCH
INFORMATION IDEAS AND CONCEPTS TO ANY
PERSON WITHOUT THE PRIOR WRITTEN
CONSENT OF THE BRISBANE AIRPORT
CORPORATION PTY. LTD.

NS	PRELIM STEEL ISSUE	29.05.26	A
DRN	AMENDMENTS	DATE	REV

NORTHROP
PROJECT NUMBER: 250946

Drawn: HP	Checked:
Design Coordinated: HP	Compliance Checked: --
Authorised For Issue: NS	Construction Checked: --

SKYGATE PLAY

ROOF FRAMING PLAN - PART 3

	BRISBANE AIRPORT CORPORATION PTY LTD 11 THE CIRCUIT, BRISBANE AIRPORT, QLD 4008, AUSTRALIA PO BOX 61, HAMILTON CENTRAL, QLD 4007, AUSTRALIA T: +61 7 3406 3000 E: INFO@BNE.COM.AU W: BNE.COM.AU		Scale: As indicated
	Project No. Originator Volume Level Type Discipline Number 25021 - NOR - XX - 01 - DR - ST - 006003		Size: A1 Revision: A