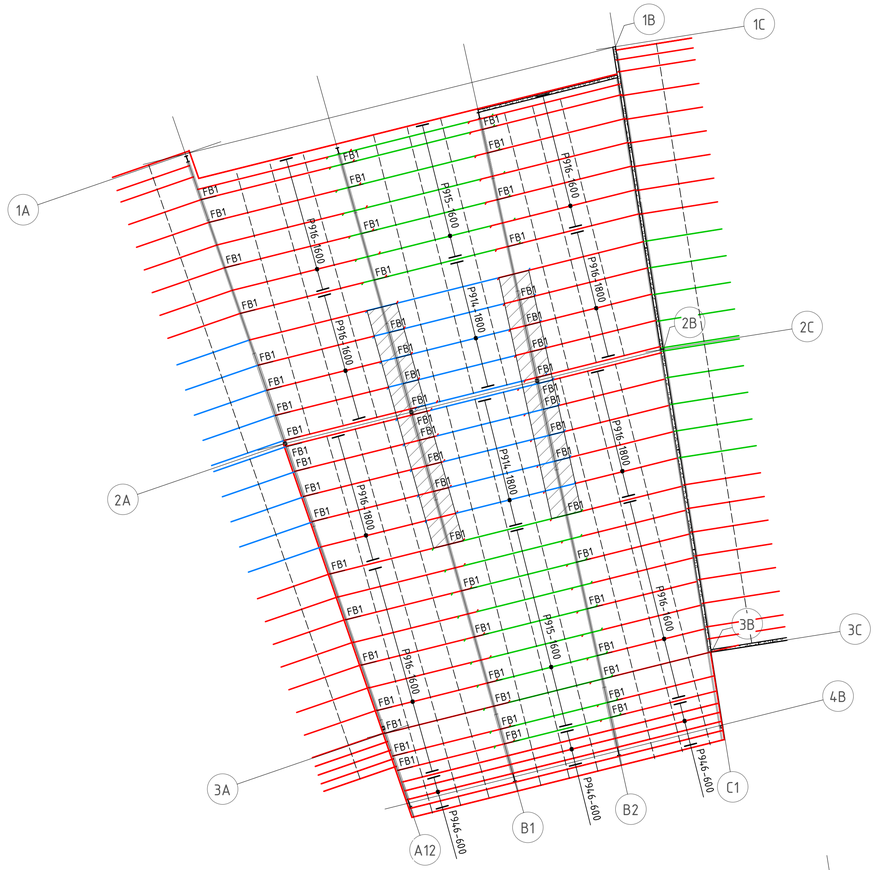

UPPER PURLIN PLAN - PART 2

SCALE 1 : 200

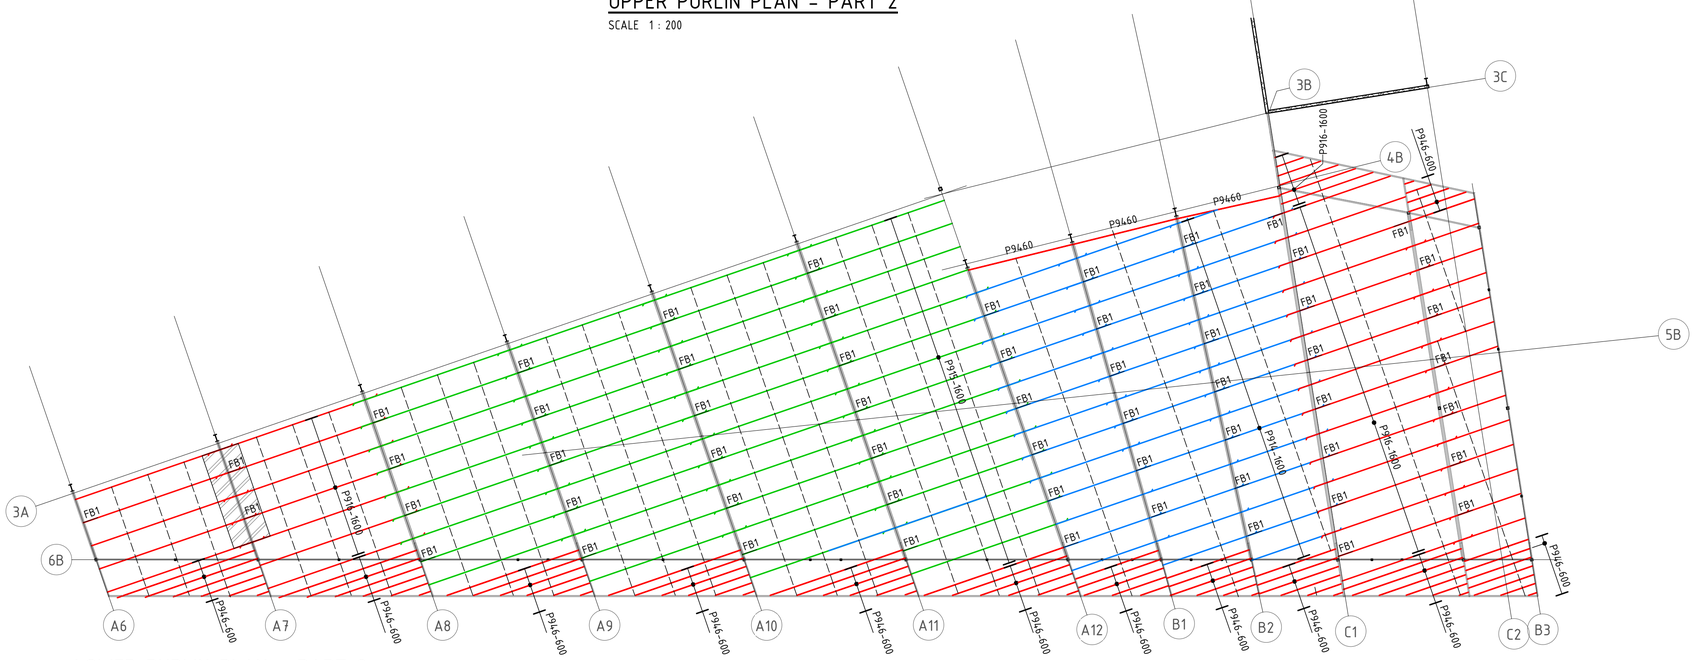

LOWER PURLIN PLAN - PART 2

SCALE 1 : 200

PURLIN PLAN NOTES

1. REFER S0.001-S0.003 FOR CONSTRUCTION NOTES
2. ALL PURLINS AND GIRTS TO BE STRAMIT EXACTA. ANY ALTERNATIVE TO BE APPROVED BY NORTHROP CONSULTING ENGINEERS PRIOR TO FABRICATION.
3. REFER ARCHITECTURAL DRAWINGS FOR ALL ROOF PENETRATION LOCATIONS.
4. THE EXACT LOCATION OF PENETRATION TRIMMING PURLIN AND GIRTS ARE TO CONFIRMED WITH SERVICE PROVIDER PRIOR TO FABRICATION.

PURLIN PLAN LEGEND

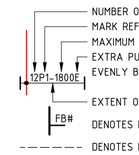

- NUMBER OF PURLINS AS REQD
- MARK REFER SCHEDULE FOR SIZE
- MAXIMUM SPACING
- EXTRA PURLINS AS REQD SPACED EVENLY BETWEEN MAIN PURLINS
- EXTENT OF PURLINS
- DENOTES FLY BRACING
- DENOTES LINE OF BRIDGING

PURLIN COLOURS

REFER MEMBER SCHEDULE FOR SIZE MARKS

- **1.0mm** C/Z PURLIN THICKNESS
- **1.2mm** C/Z PURLIN THICKNESS
- **1.5mm** C/Z PURLIN THICKNESS
- **1.9mm** C/Z PURLIN THICKNESS
- **2.4mm** C/Z PURLIN THICKNESS
- **3.0mm** C/Z PURLIN THICKNESS

PURLIN LAPS

ALL PURLIN LAPS TO BE 15% OF THE LARGEST ADJACENT SPAN UNLESS NOTED OTHERWISE

- DENOTES PURLIN LAPS TO BE **20%** OF LARGEST ADJACENT SPAN
- DENOTES PURLIN LAPS TO BE **25%** OF LARGEST ADJACENT SPAN
- DENOTES PURLIN LAPS TO BE **30%** OF LARGEST ADJACENT SPAN

PURLIN SCHEDULE

MARK	SIZE
GIRT	
G946	EC250-24
PURLIN	
P914	EZ250-15
P915	EZ250-19
P916	EZ250-24
P946	EC250-24

COPYRIGHT :
REPRODUCTION OF WHOLE OR PART OF THIS DOCUMENT CONSTITUTES AN INFRINGEMENT OF COPYRIGHT. THE INFORMATION, IDEAS, AND CONCEPTS CONTAINED IN THIS DOCUMENT ARE CONFIDENTIAL. THE RECIPIENT(S) OF THIS DOCUMENT IS PROHIBITED FROM DISCLOSING SUCH INFORMATION IDEAS AND CONCEPTS TO ANY PERSON WITHOUT THE PRIOR WRITTEN CONSENT OF THE BRISBANE AIRPORT CORPORATION PTY. LTD.

NS	PRELIM STEEL ISSUE	29.05.26	A
DRN	AMENDMENTS	DATE	REV

NORTHROP
PROJECT NUMBER: 250946

Drawn: HP	Checked:
Design Coordinated: HP	Compliance Checked: --
Authorised For Issue: NS	Construction Checked: --

SKYGATE PLAY

ROOF PURLIN PLAN - PART 2

BRISBANE AIRPORT CORPORATION PTY LTD
11 THE CIRCUIT, BRISBANE AIRPORT, QLD, 4008, AUSTRALIA
PO BOX 61, HAMILTON CENTRAL, QLD, 4007, AUSTRALIA
T: +61 7 3406 3000
E: INFO@BNE.COM.AU
W: BNE.COM.AU

Scale:	Size:	Revision:
As indicated	A1	A

Drawing Number	Project No.	Originator	Volume	Level	Type	Discipline	Number
	25021	NOR	XX	01	DR	ST	006012

File Path: Autodesk Docs://250946 - BNE Play/25021-NOR-ZZ-ZZ-M3-ST-000001.rvt

Plot Date & Time: 29/05/2026 11:44:52 AM