


PURLIN PLAN NOTES

1. REFER S0.001-S0.003 FOR CONSTRUCTION NOTES
2. ALL PURLINS AND GIRTS TO BE STRAMIT EXACTA.
ANY ALTERNATIVE TO BE APPROVED BY NORTHROP
CONSULTING ENGINEERS PRIOR TO FABRICATION.
3. REFER ARCHITECTURAL DRAWINGS FOR ALL ROOF
PENETRATION LOCATIONS.
4. THE EXACT LOCATION OF PENETRATION TRIMMING
PURLIN AND GIRTS ARE TO CONFIRMED WITH
SERVICE PROVIDER PRIOR TO FABRICATION.

PURLIN PLAN LEGEND

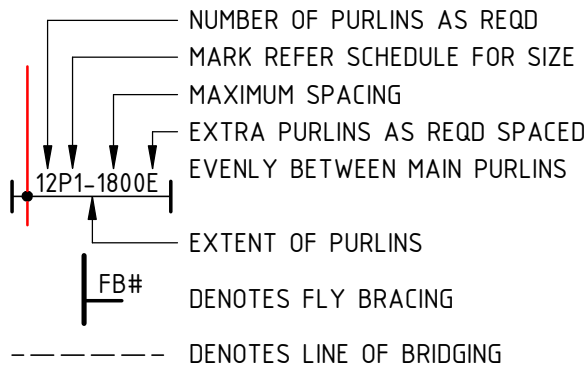


PURLIN COLOURS

- REFER MEMBER SCHEDULE FOR SIZE MARKS
- 1.0mm C/Z PURLIN THICKNESS
- 1.2mm C/Z PURLIN THICKNESS
- 1.5mm C/Z PURLIN THICKNESS
- 1.9mm C/Z PURLIN THICKNESS
- 2.4mm C/Z PURLIN THICKNESS
- 3.0mm C/Z PURLIN THICKNESS


PURLIN LAPS

ALL PURLIN LAPS TO BE 15% OF THE LARGEST
ADJACENT SPAN UNLESS NOTED OTHERWISE

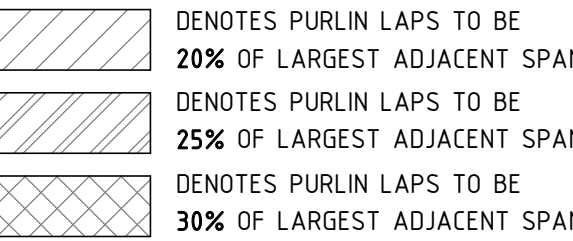


PURLIN SCHEDULE

MARK	SIZE
GIRT	
G946	EC250-24
PURLIN	
P914	EZ250-15
P915	EZ250-19
P916	EZ250-24
P946	EC250-24

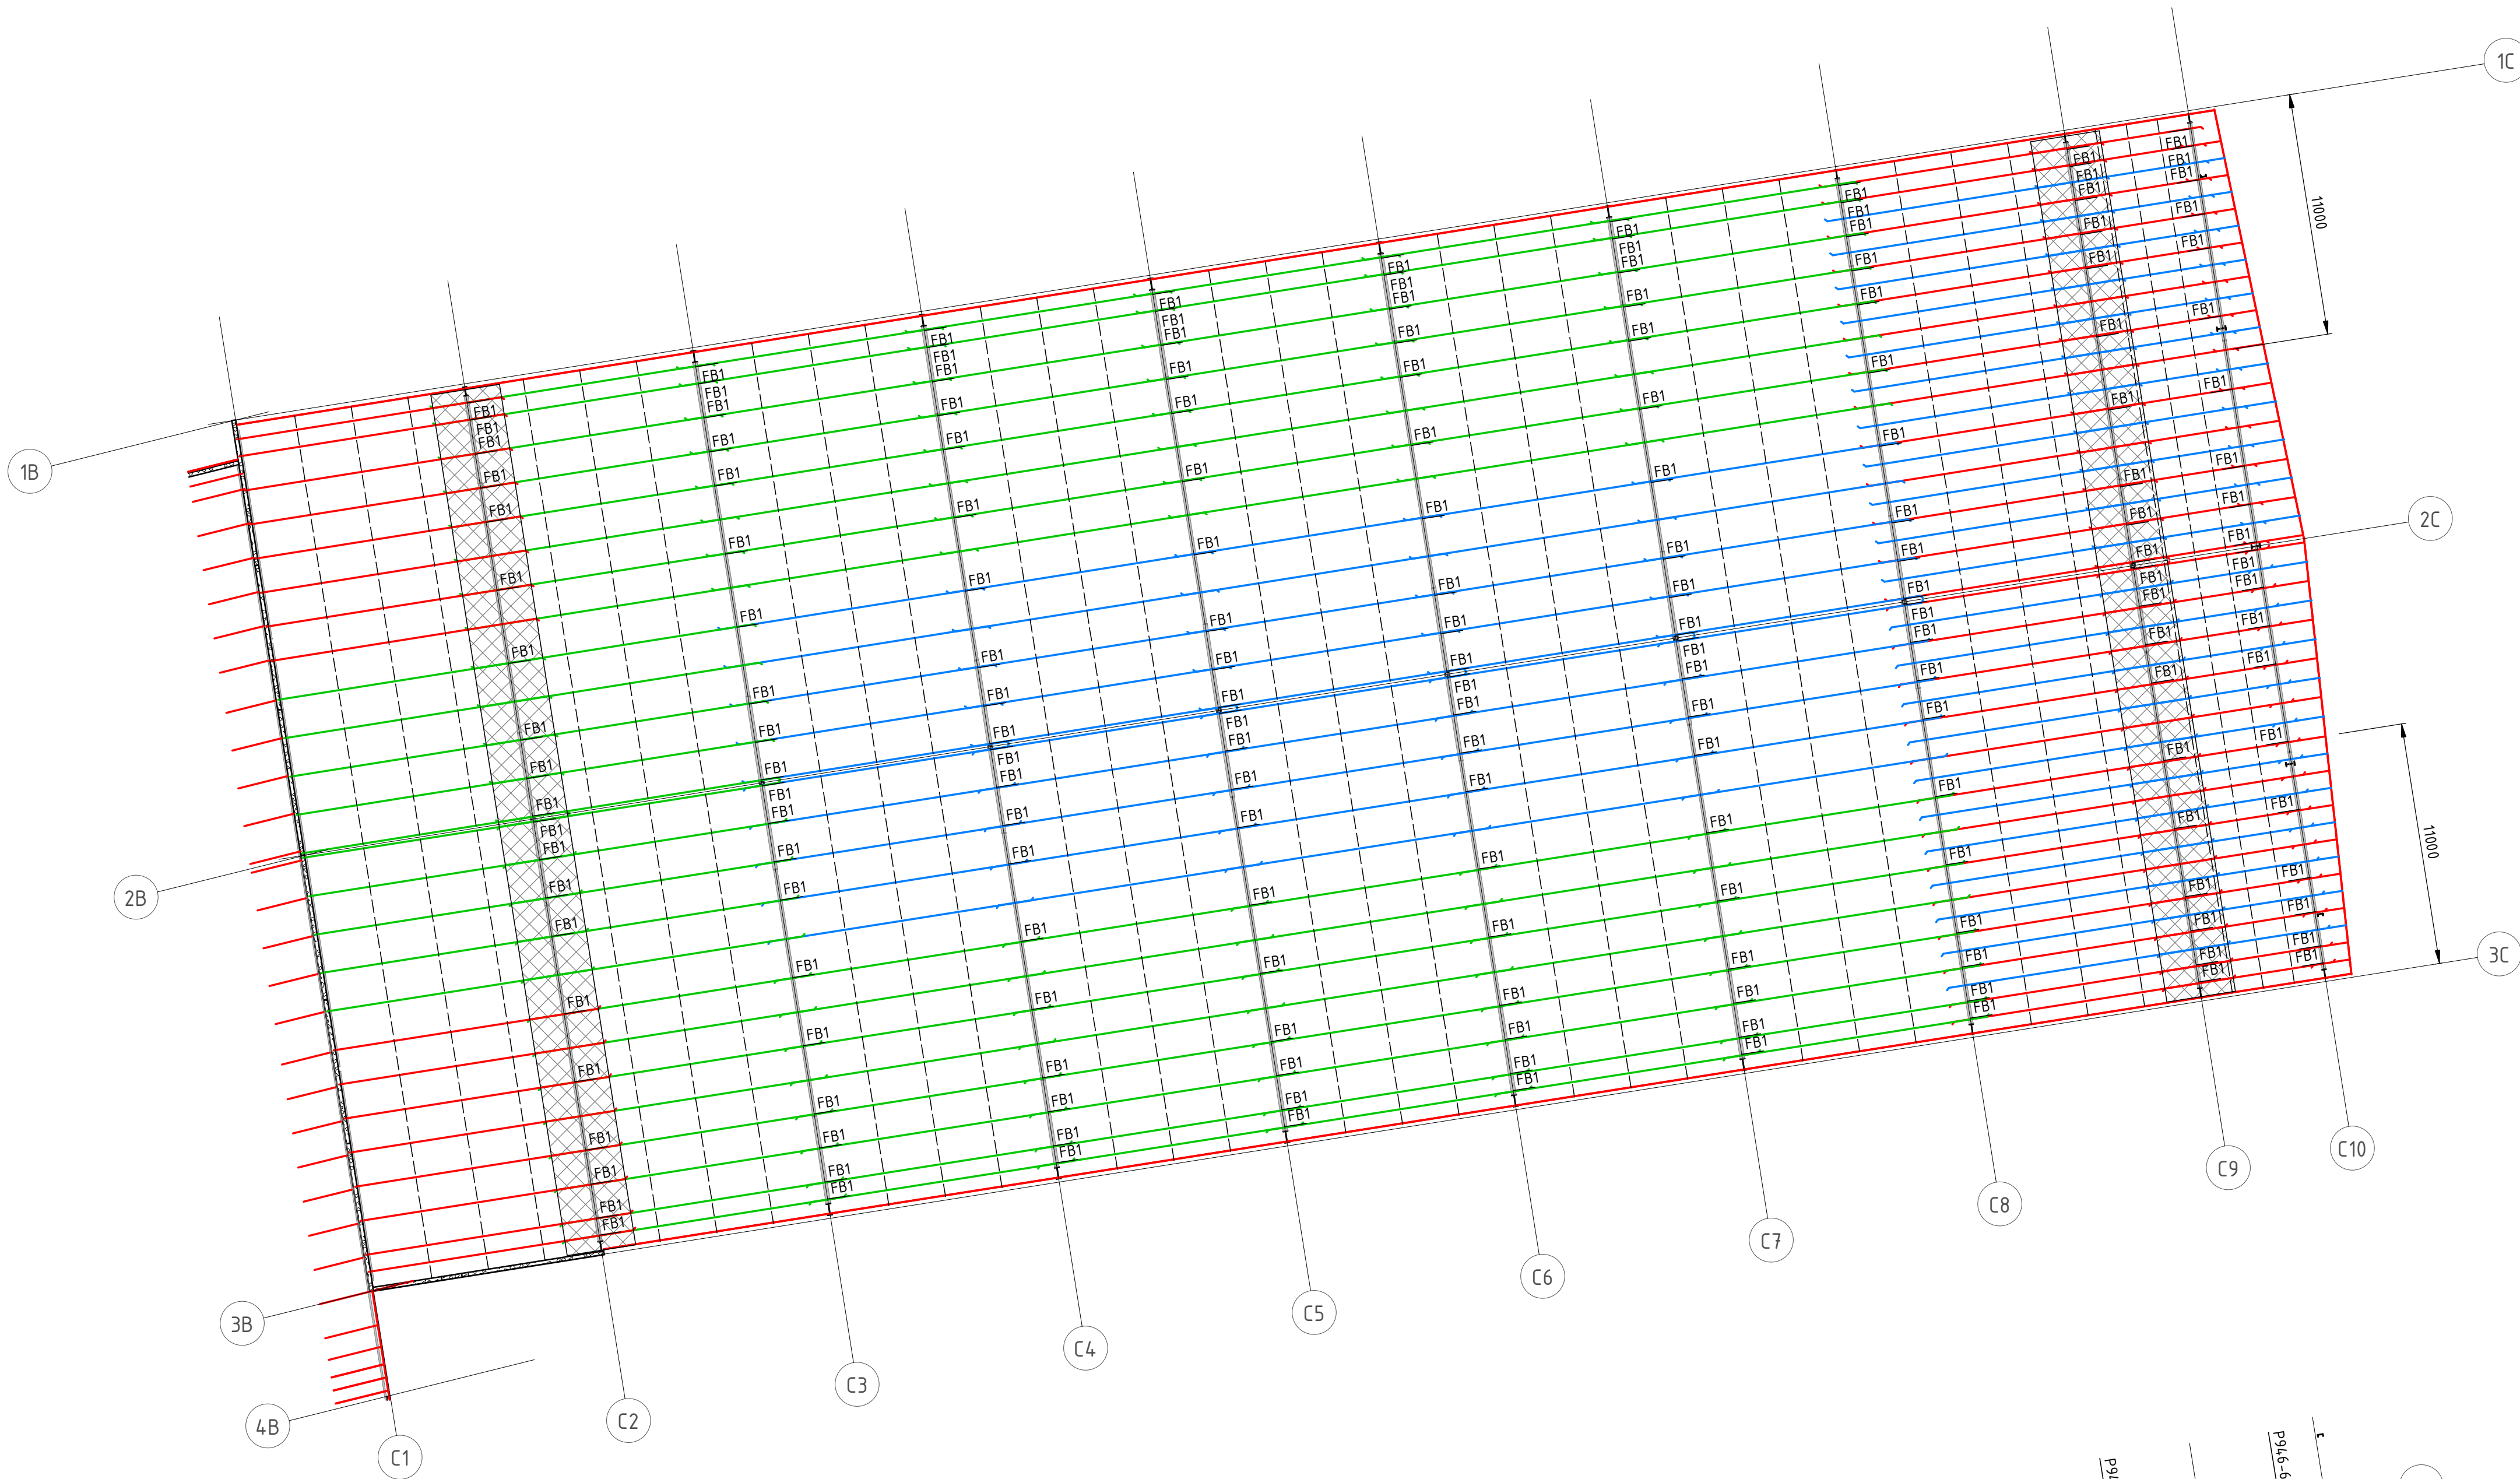

UPPER PURLIN PLAN - PART 3
SCALE 1 : 200

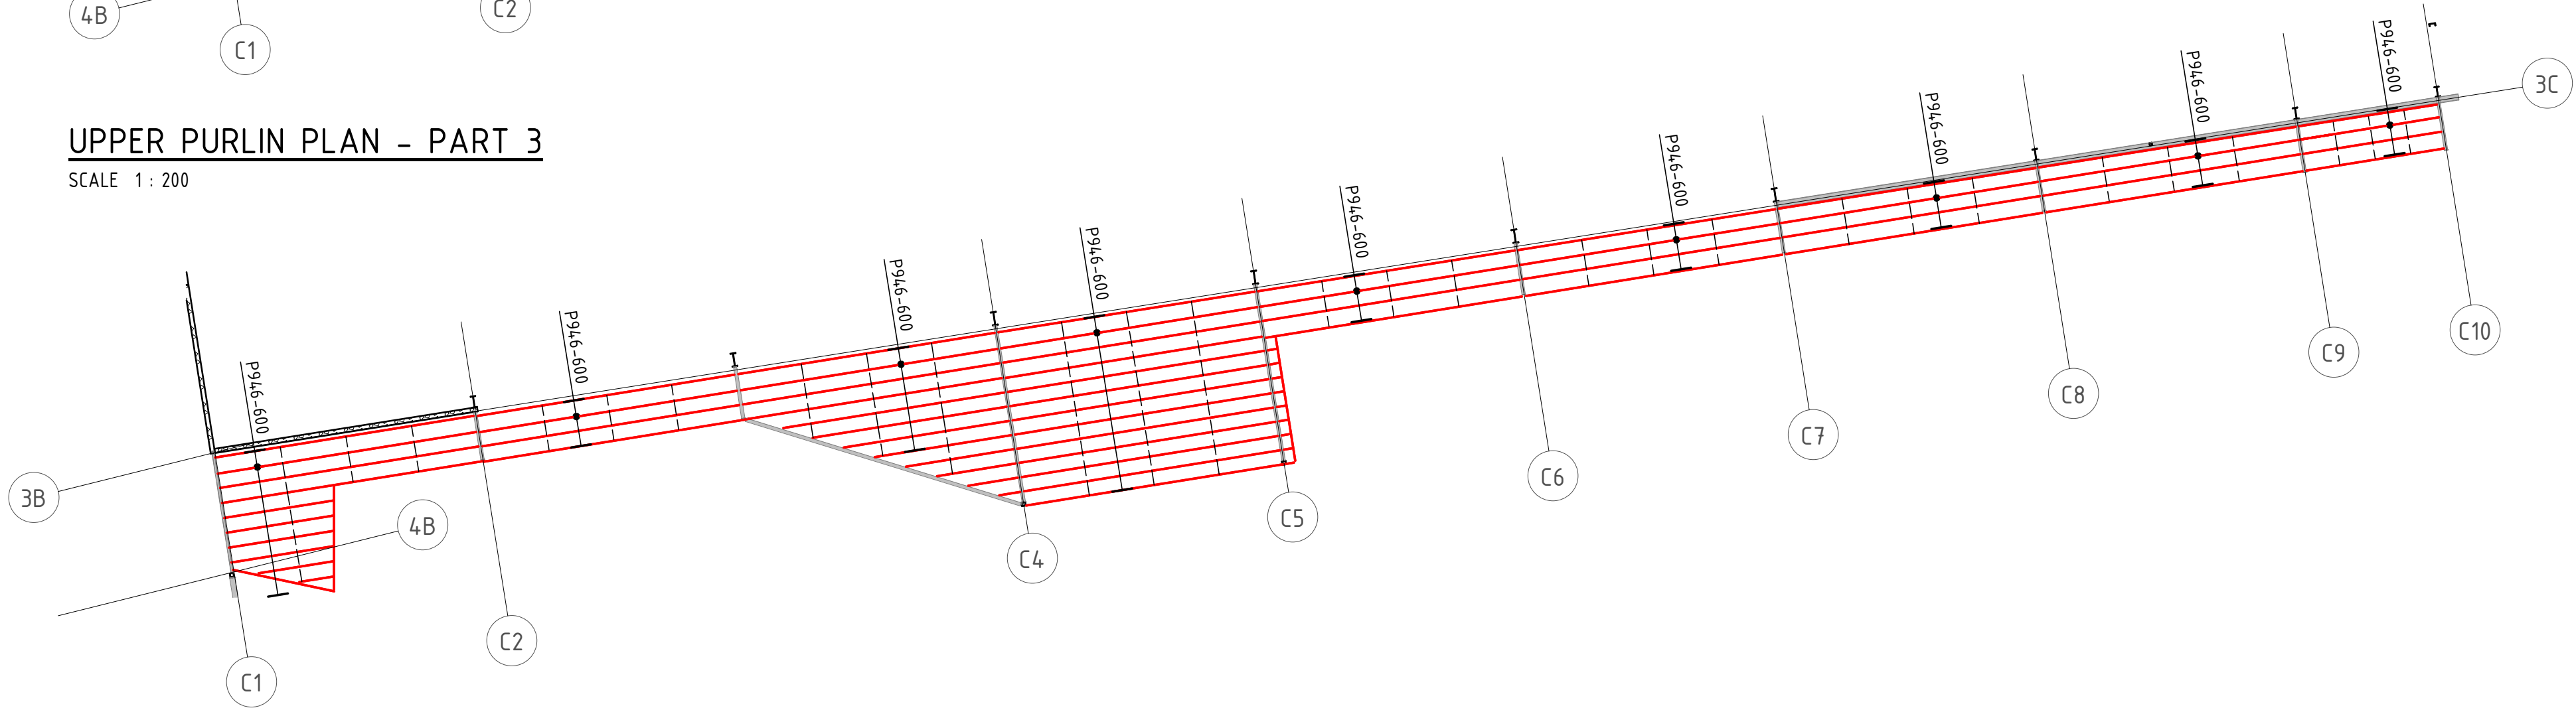

LOWER FRAMING ROOF PLAN - PART 2
SCALE 1 : 200