



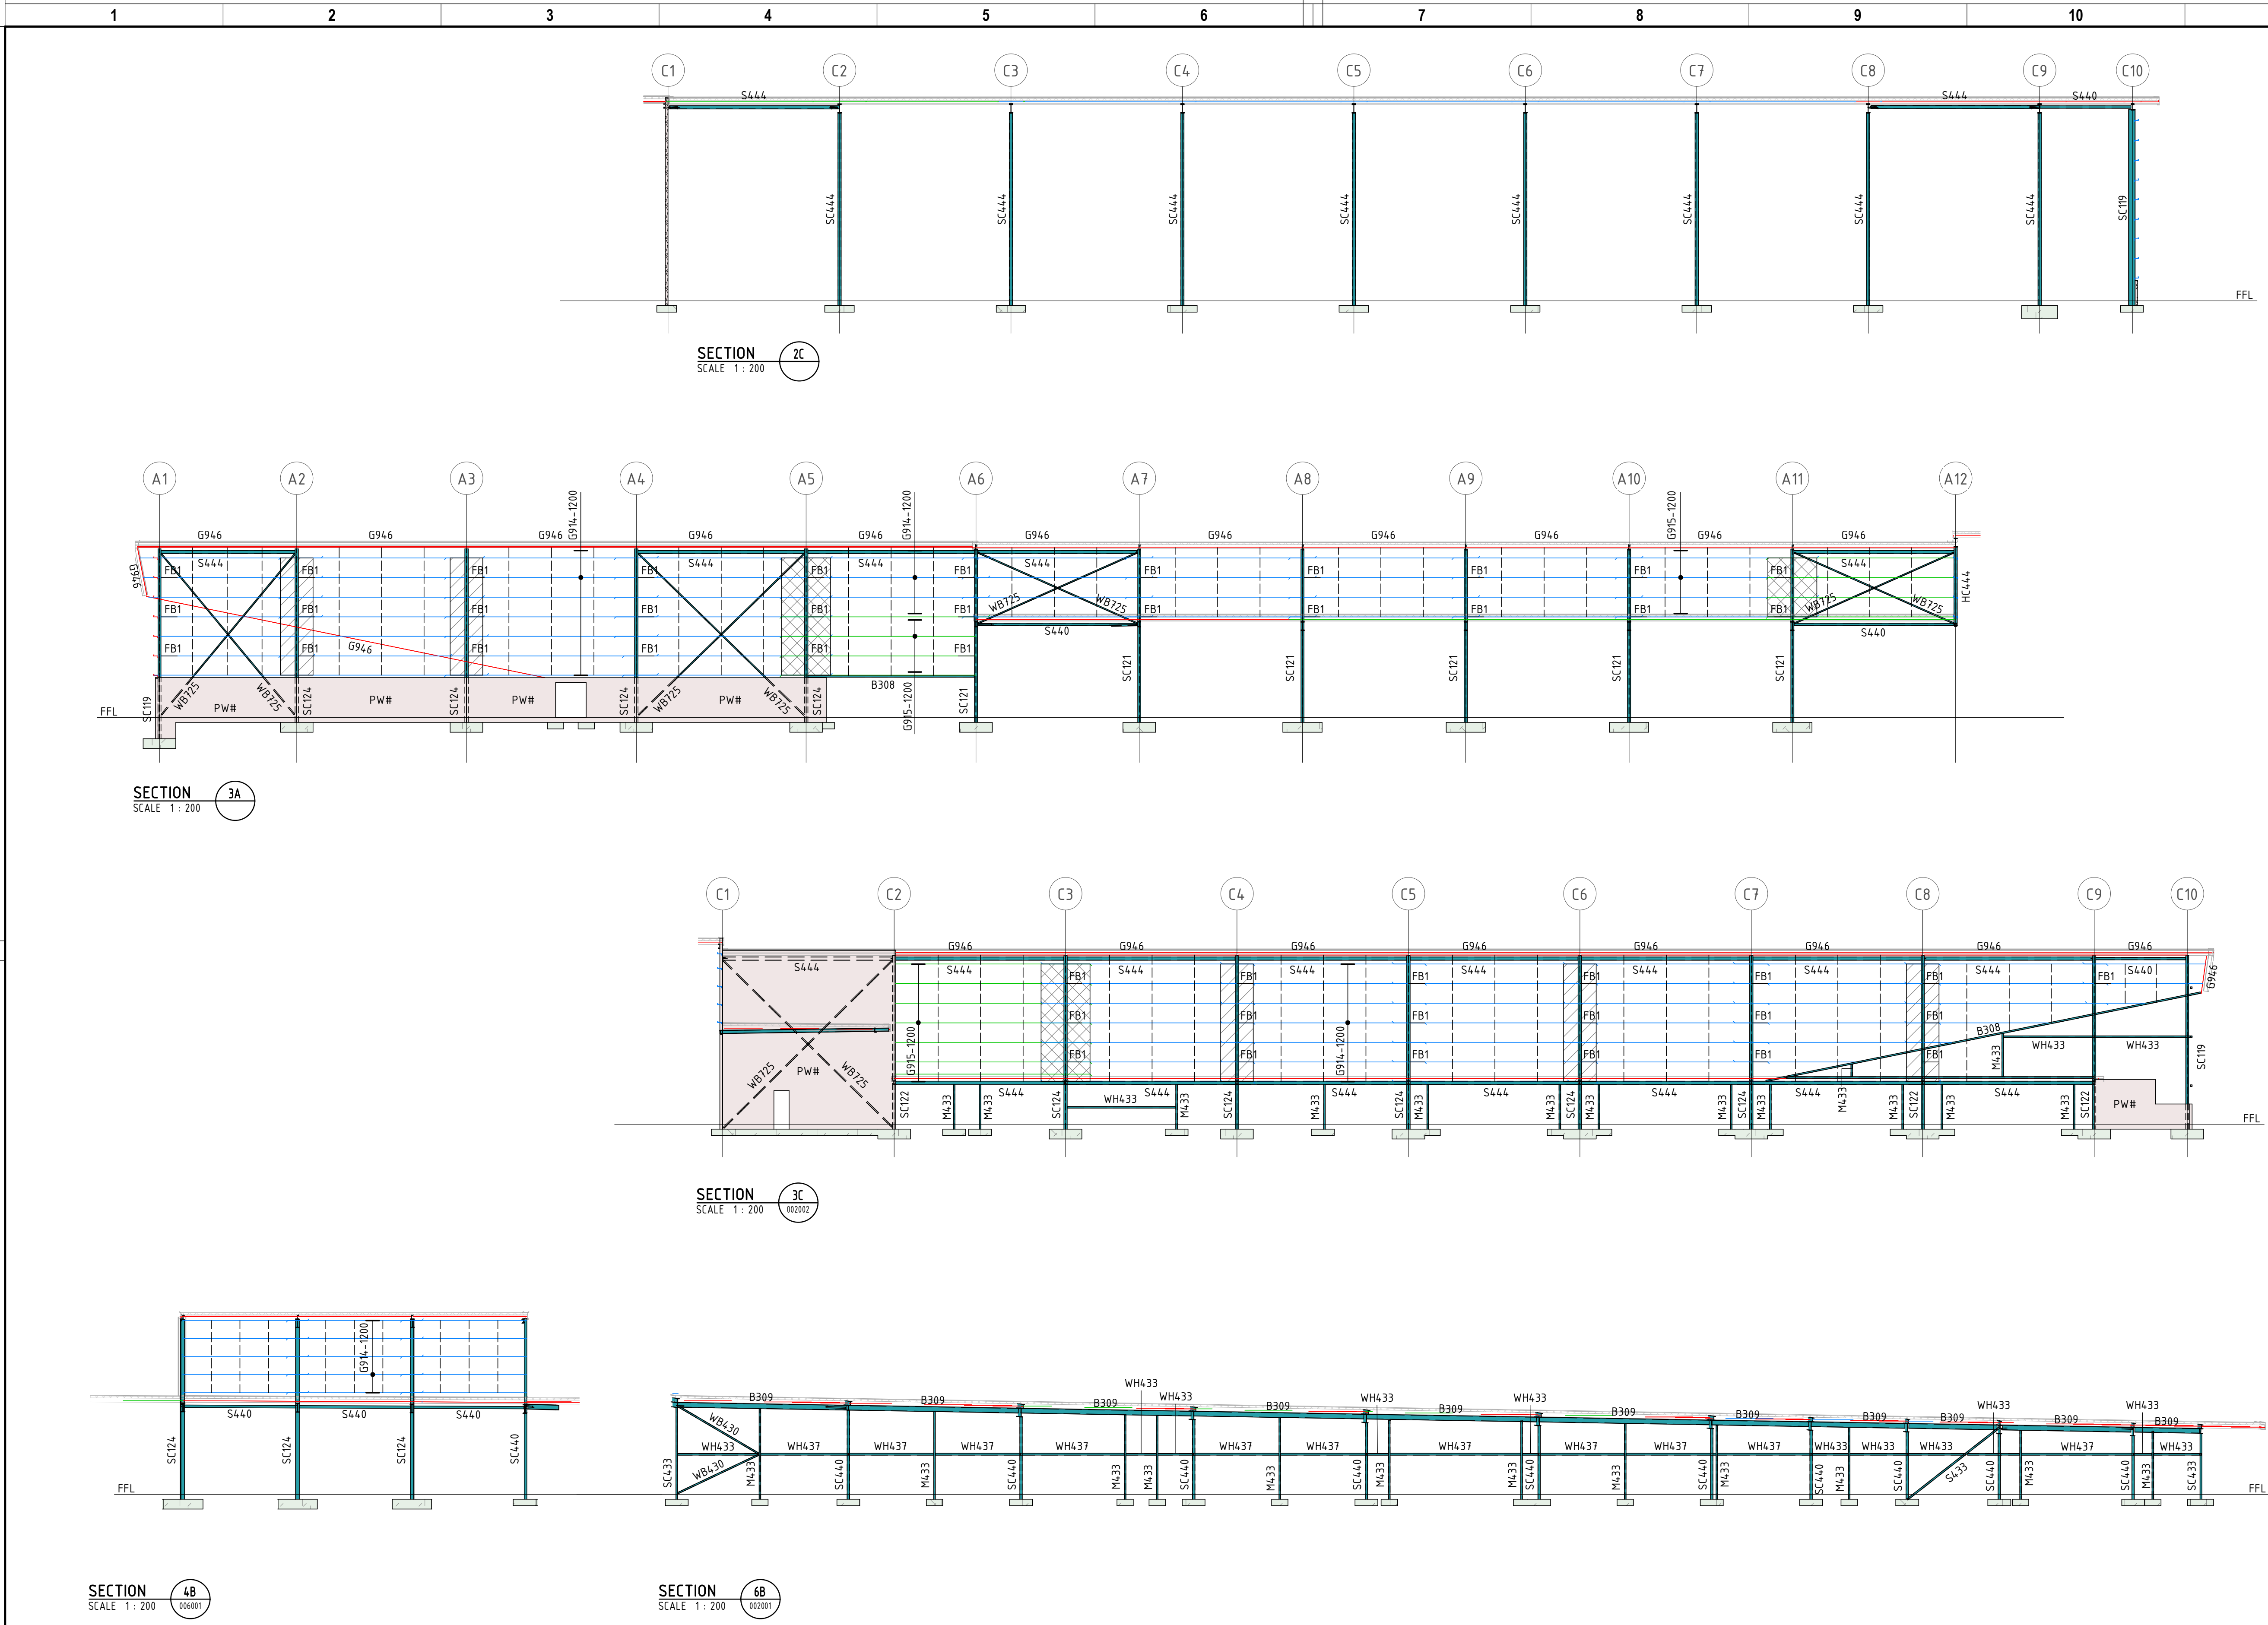

ELEVATIONS AND SECTIONS NOTES

- REFER S0.001-S0.003 FOR CONSTRUCTION NOTES
- ALL PURLINS AND GIRTS TO BE STRAMIT EXACTA. ANY ALTERNATIVE TO BE APPROVED BY NORTHROP CONSULTING ENGINEERS PRIOR TO FABRICATION.
- REFER ARCHITECTURAL DRAWINGS FOR ALL ROOF PENETRATION LOCATIONS.
- THE EXACT LOCATION OF PENETRATION TRIMMING PURLIN AND GIRTS ARE TO CONFIRMED WITH SERVICE PROVIDER PRIOR TO FABRICATION.

ELEVATIONS AND SECTIONS LEGEND

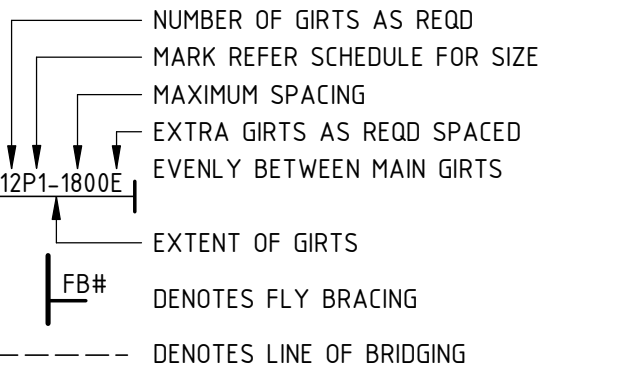

GIRT COLOURS

- REFER MEMBER SCHEDULE FOR SIZE MARKS
- 1.0mm C/Z GIRT THICKNESS
 - 1.2mm C/Z GIRT THICKNESS
 - 1.5mm C/Z GIRT THICKNESS
 - 1.9mm C/Z GIRT THICKNESS
 - 2.4mm C/Z GIRT THICKNESS
 - 3.0mm C/Z GIRT THICKNESS

GIRT LAPS

ALL GIRT LAPS TO BE 15% OF THE LARGEST ADJACENT SPAN UNLESS NOTED OTHERWISE

- DENOTES GIRT LAPS TO BE 20% OF LARGEST ADJACENT SPAN
- DENOTES GIRT LAPS TO BE 25% OF LARGEST ADJACENT SPAN
- DENOTES GIRT LAPS TO BE 30% OF LARGEST ADJACENT SPAN
- DENOTES GIRT LAPS TO BE 35% OF LARGEST ADJACENT SPAN

MEMBER SCHEDULE

MARK	SIZE
COLUMN	
SC119	410 UB 53.7
SC121	460 UB 67.1
SC122	460 UB 74.6
SC124	530 UB 82.0
SC433	100 x 100 x 5.0 SHS
SC440	150 x 150 x 5.0 SHS
SC444	200 x 200 x 6.0 SHS
HANGING COLUMN	
HC444	200 x 200 x 6.0 SHS
MULLION	
M433	100 x 100 x 5.0 SHS
BEAM	
B306	200 PFC
B308	250 PFC
B309	300 PFC
OUTRIGGER	
OR308	250 PFC
RAFTER	
R108	200 UB 25.4
R114	310 UB 40.4
R116	360 UB 44.7
R120	410 UB 59.7
R121	460 UB 67.1
R124	530 UB 82.0
R125	530 UB 92.4
R308	250 PFC
R309	300 PFC
RAKING ANGLE	
RAT28	90 x 90 x 8 EA
ROOF BRACING	
RB725	75 x 75 x 8 EA
STRUT	
S433	100x100x5.0SHS
S440	150x150x5.0SHS
S444	200x200x6.0SHS
WALL BRACING	
WB430	89x89x6.0SHS
WB725	75 x 75 x 8 EA
WALL HEAD	
WH433	100x100x5.0SHS
WH437	125x125x5.0SHS
GIRT	
G914	EZ250-15
G915	EZ250-19
G916	EZ250-24
G946	EC250-24
PURLIN	
P914	EZ250-15
P915	EZ250-19
P916	EZ250-24

COPYRIGHT :
REPRODUCTION OF WHOLE OR PART OF THIS
DOCUMENT CONSTITUTES AN INFRINGEMENT
OF COPYRIGHT. THE INFORMATION, IDEAS,
AND CONCEPTS CONTAINED IN THIS
DOCUMENT ARE CONFIDENTIAL. THE
RECIPIENT(S) OF THIS DOCUMENT IS
PROHIBITED FROM DISCLOSING SUCH
INFORMATION IDEAS AND CONCEPTS TO ANY
PERSON WITHOUT THE PRIOR WRITTEN
CONSENT OF THE BRISBANE AIRPORT
CORPORATION PTY. LTD.

NS	STEEL DETAILS ISSUE	04.06.26	B
NS	PRELIM STEEL ISSUE	29.05.26	A
DRN	AMENDMENTS	DATE	REV

NORTHROP
PROJECT NUMBER: 250946

Drawn: HP	Checked:
Design Coordinated: HP	Compliance Checked: --
Authorised For Issue: NS	Construction Checked: --

SKYGATE PLAY

BUILDING SECTIONS - SHEET 2

Brisbane Airport		Scale: As indicated
11 THE CIRCUIT, BRISBANE AIRPORT, QLD 4008, AUSTRALIA PO BOX 61, HAMILTON CENTRAL, QLD 4007, AUSTRALIA T: +61 7 3406 3000 E: INFO@BRISBANE.COM.AU W: WWW.BRISBANE.COM.AU		Size: A1
Project No. Originator Volume Level Type Discipline Number		Revision: B
25021 - NOR - XX - 01 - DR - ST - 006502		