



SECTION A9
SCALE 1 : 200

SECTION A10
SCALE 1 : 200

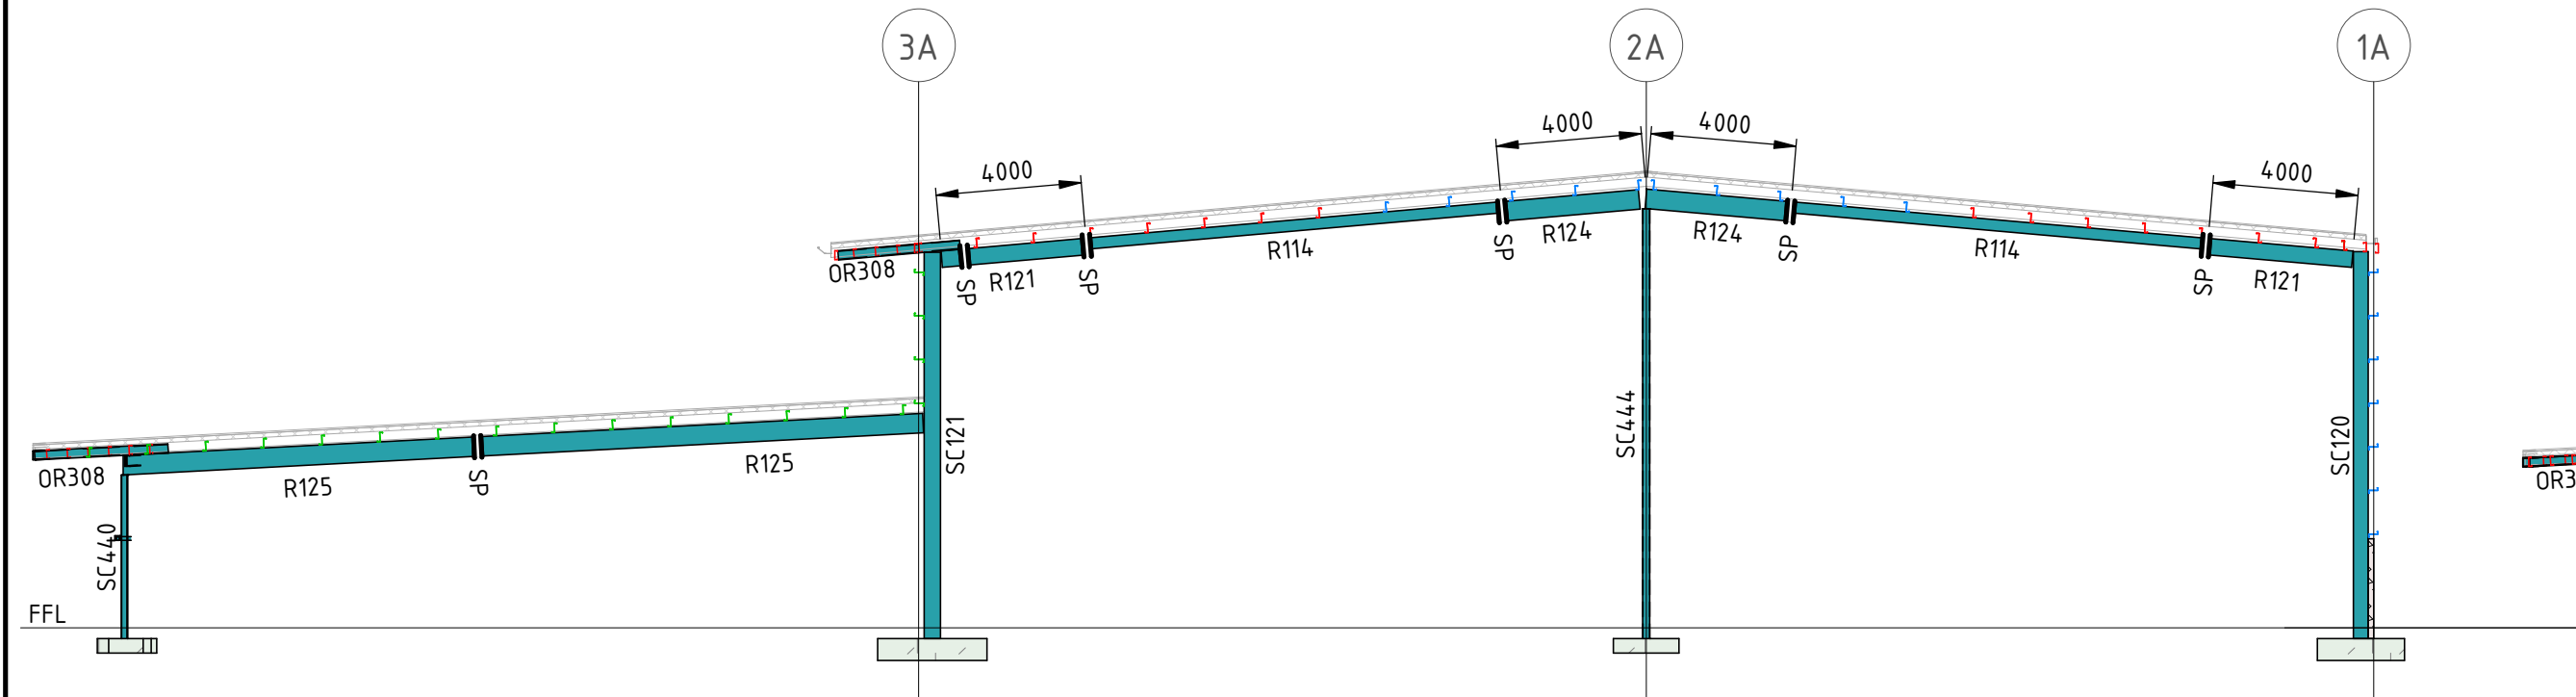


SECTION A11
SCALE 1 : 200


SECTION A12
SCALE 1 : 200

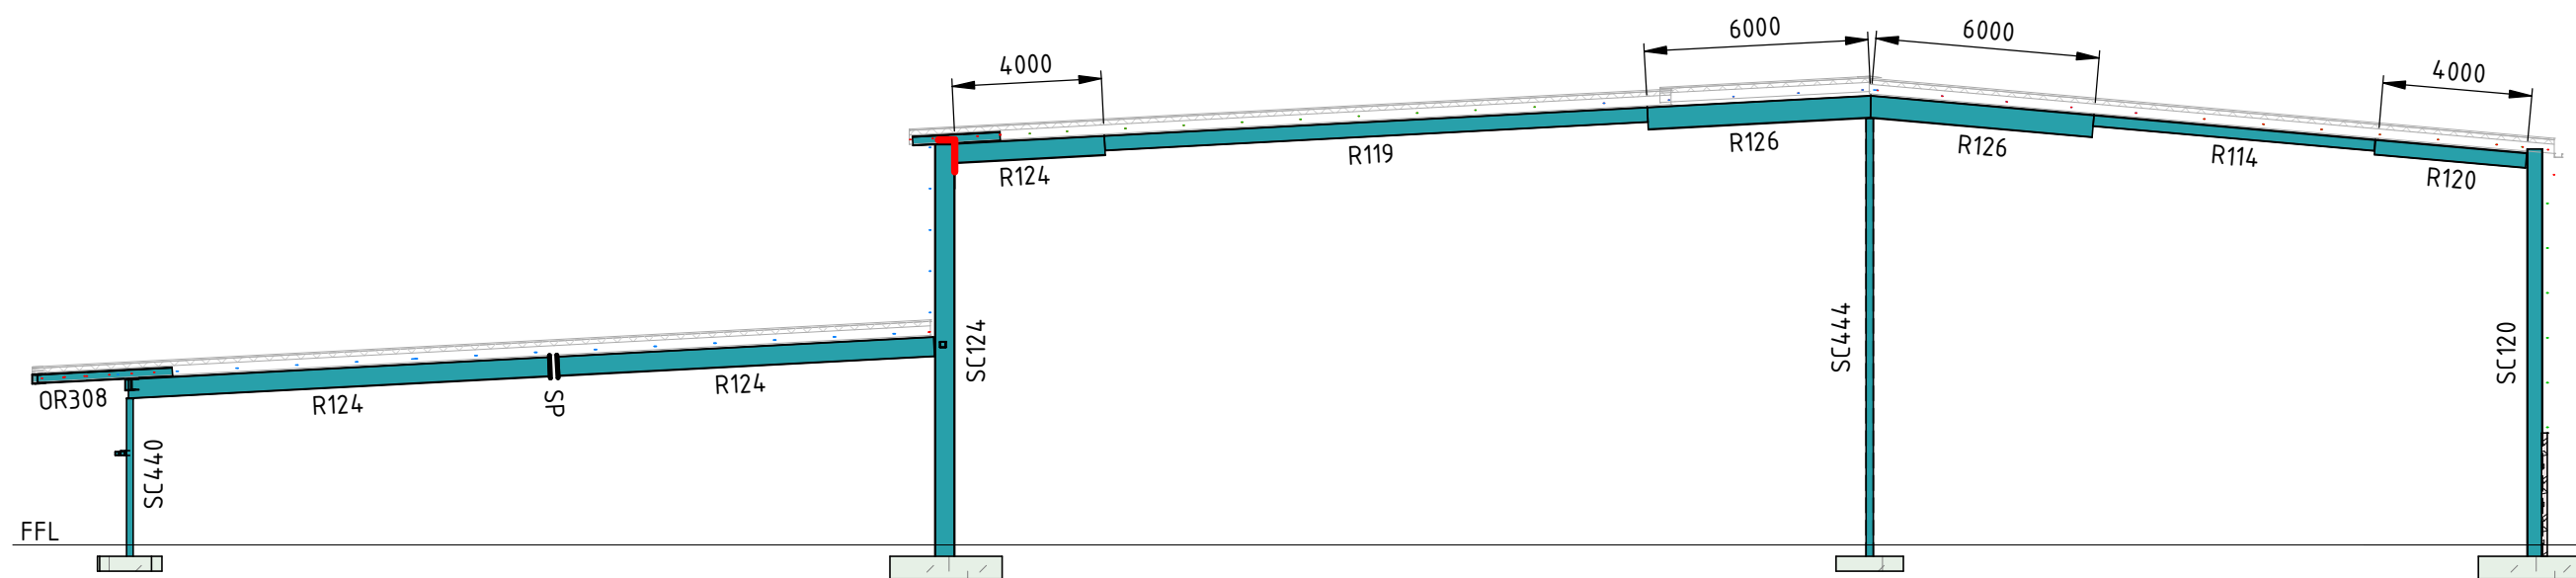


SECTION B1
SCALE 1 : 200

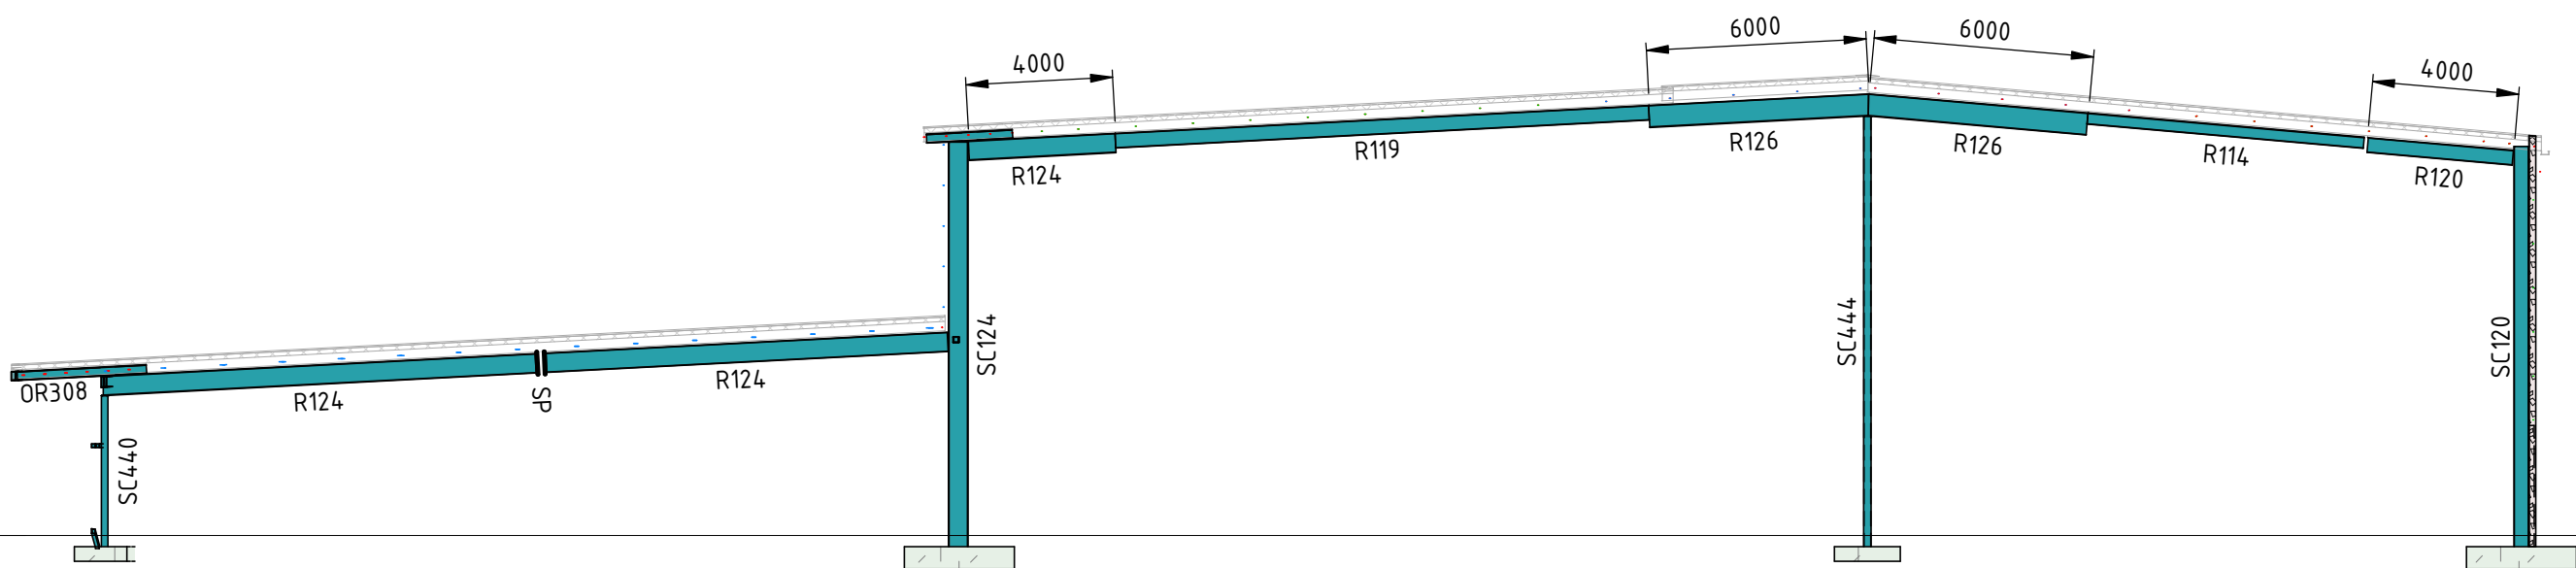

SECTION B2
SCALE 1 : 200

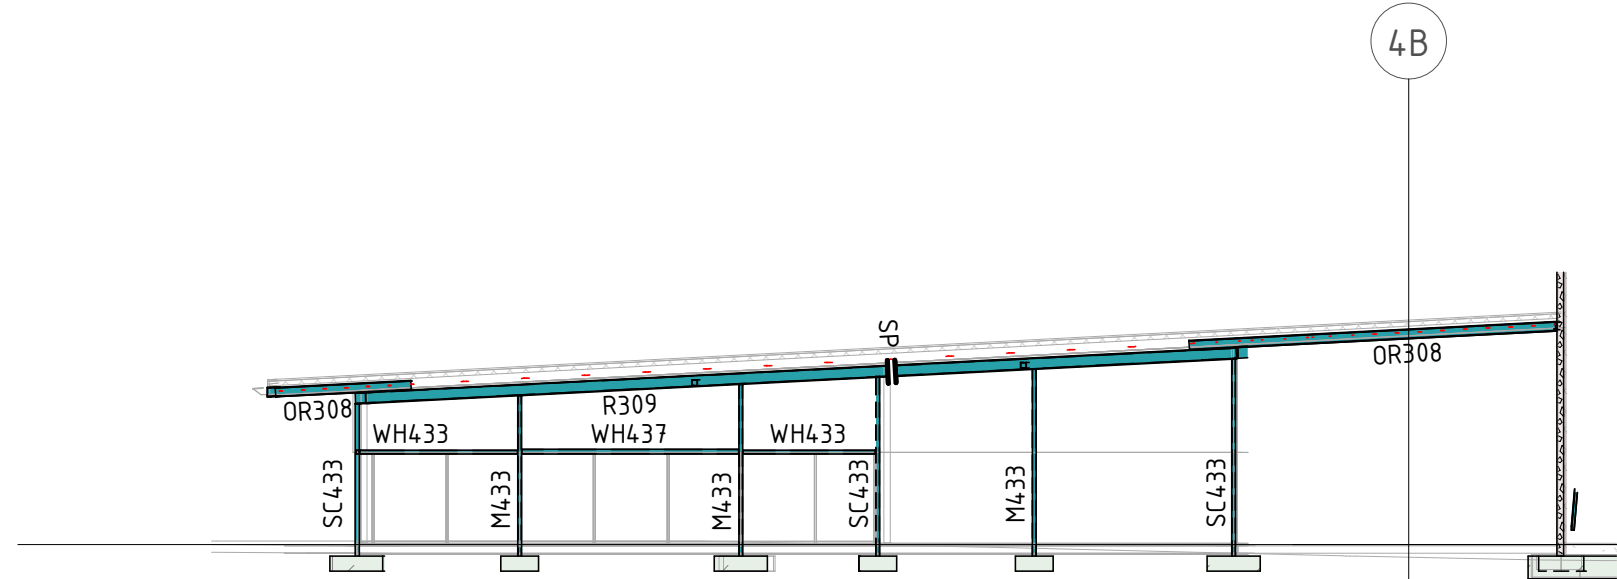

SECTION B3
SCALE 1 : 200

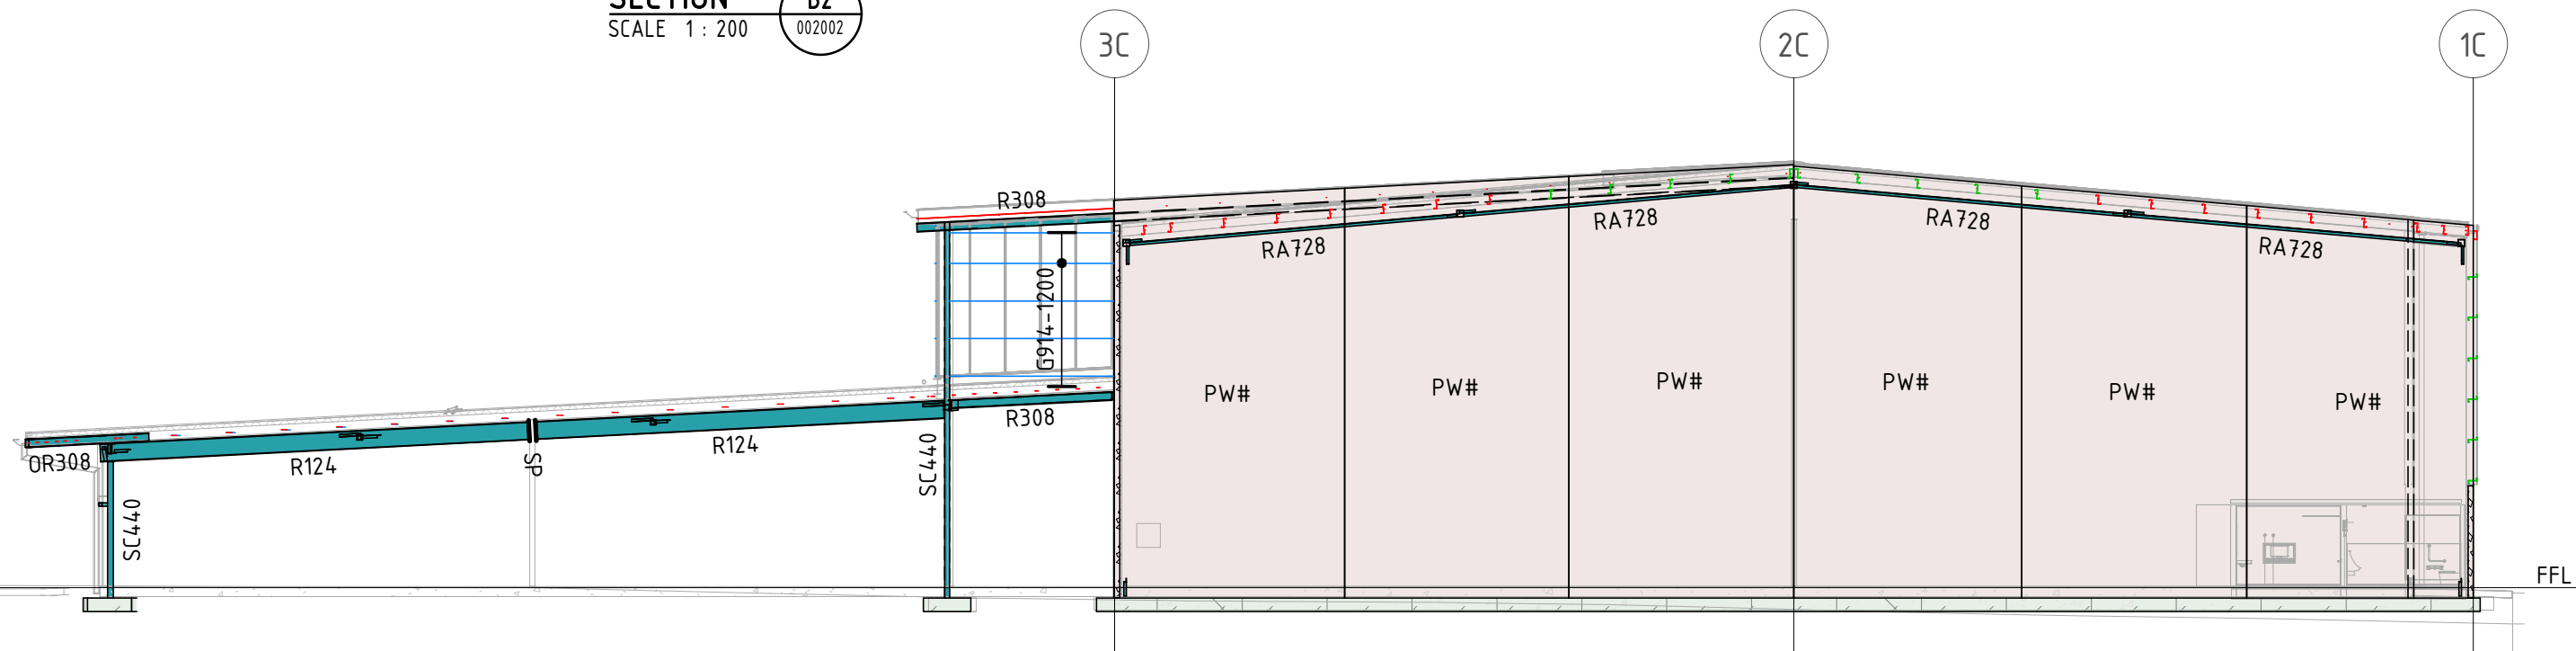


SECTION C1
SCALE 1 : 200

ELEVATIONS AND SECTIONS NOTES

- REFER S0.001-S0.003 FOR CONSTRUCTION NOTES
- ALL PURLINS AND GIRTS TO BE STRAMIT EXACTA. ANY ALTERNATIVE TO BE APPROVED BY NORTHROP CONSULTING ENGINEERS PRIOR TO FABRICATION.
- REFER ARCHITECTURAL DRAWINGS FOR ALL ROOF PENETRATION LOCATIONS.
- THE EXACT LOCATION OF PENETRATION TRIMMING PURLIN AND GIRTS ARE TO BE CONFIRMED WITH SERVICE PROVIDER PRIOR TO FABRICATION.

ELEVATIONS AND SECTIONS LEGEND

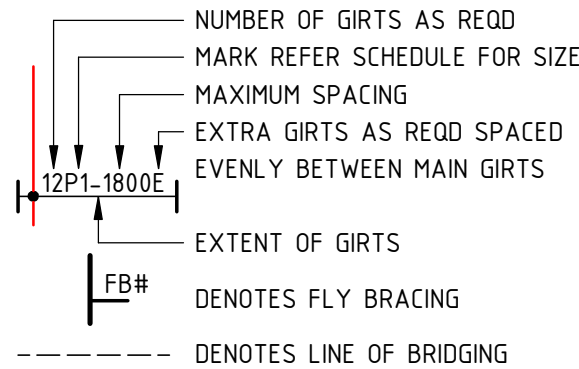

GIRT COLOURS

- REFER MEMBER SCHEDULE FOR SIZE MARKS
- 1.0mm C/Z GIRT THICKNESS
 - 1.2mm C/Z GIRT THICKNESS
 - 1.5mm C/Z GIRT THICKNESS
 - 1.9mm C/Z GIRT THICKNESS
 - 2.4mm C/Z GIRT THICKNESS
 - 3.0mm C/Z GIRT THICKNESS

GIRT LAPS

ALL GIRT LAPS TO BE 15% OF THE LARGEST ADJACENT SPAN UNLESS NOTED OTHERWISE

- 20% OF LARGEST ADJACENT SPAN
- 25% OF LARGEST ADJACENT SPAN
- 30% OF LARGEST ADJACENT SPAN
- 35% OF LARGEST ADJACENT SPAN

MEMBER SCHEDULE

MARK	SIZE
COLUMN	
SC120	410 UB 59.7
SC121	460 UB 67.1
SC124	530 UB 82.0
SC433	100 x 100 x 5.0 SHS
SC440	150 x 150 x 5.0 SHS
SC444	200 x 200 x 6.0 SHS
HANGING COLUMN	
HC444	200 x 200 x 6.0 SHS
MULLION	
M308	250 PFC
M433	100 x 100 x 5.0 SHS
BEAM	
B306	200 PFC
B308	250 PFC
B309	300 PFC
OUTRIGGER	
OR308	250 PFC
RAFTER	
R114	310 UB 40.4
R119	410 UB 53.7
R120	410 UB 59.7
R121	460 UB 67.1
R124	530 UB 82.0
R125	530 UB 92.4
R126	610 UB 101
R308	250 PFC
R309	300 PFC
RAKING ANGLE	
RA728	90 x 90 x 8 EA
ROOF BRACING	
RB725	75 x 75 x 8 EA
STRUT	
S433	100x100x5.0SHS
S440	150x150x5.0SHS
S444	200x200x6.0SHS
WALL BRACING	
WB725	75 x 75 x 8 EA
WALL HEAD	
WH433	100x100x5.0SHS
WH437	125x125x5.0SHS
GIRT	
G914	EZ250-15
G915	EZ250-19
G946	EC250-24
PURLIN	
P914	EZ250-15
P915	EZ250-19
P916	EZ250-24
P946	EC250-24

COPYRIGHT :
REPRODUCTION OF WHOLE OR PART OF THIS
DOCUMENT CONSTITUTES AN INFRINGEMENT
OF COPYRIGHT. THE INFORMATION, IDEAS,
AND CONCEPTS CONTAINED IN THIS
DOCUMENT ARE CONFIDENTIAL. THE
RECIPIENT(S) OF THIS DOCUMENT IS
PROHIBITED FROM DISCLOSING SUCH
INFORMATION IDEAS AND CONCEPTS TO ANY
PERSON WITHOUT THE PRIOR WRITTEN
CONSENT OF THE BRISBANE AIRPORT
CORPORATION PTY. LTD.

NS	STEEL DETAILS ISSUE	04.06.26	B
NS	PRELIM STEEL ISSUE	29.05.26	A
DRN	AMENDMENTS	DATE	REV

NORTHROP
PROJECT NUMBER: 250946

Drawn: HP	Checked:
Design Coordinated: HP	Compliance Checked: --
Authorised For Issue: NS	Construction Checked: --

SKYGATE PLAY
BUILDING SECTIONS - SHEET 4

 Brisbane Airport		BRISBANE AIRPORT CORPORATION PTY LTD 11 THE CIRCUIT, BRISBANE AIRPORT, QLD 4008, AUSTRALIA PO BOX 61, HAMILTON CENTRAL, QLD 4007, AUSTRALIA T: +61 7 3406 3000 E: INFO@BNE.COM.AU W: BNE.COM.AU				Scale: As indicated Size: A1 Revision: B	
Drawing Number	Project No.	Originator	Volume	Level	Type	Discipline	Number
	25021	NOR	XX	01	DR	ST	006504