




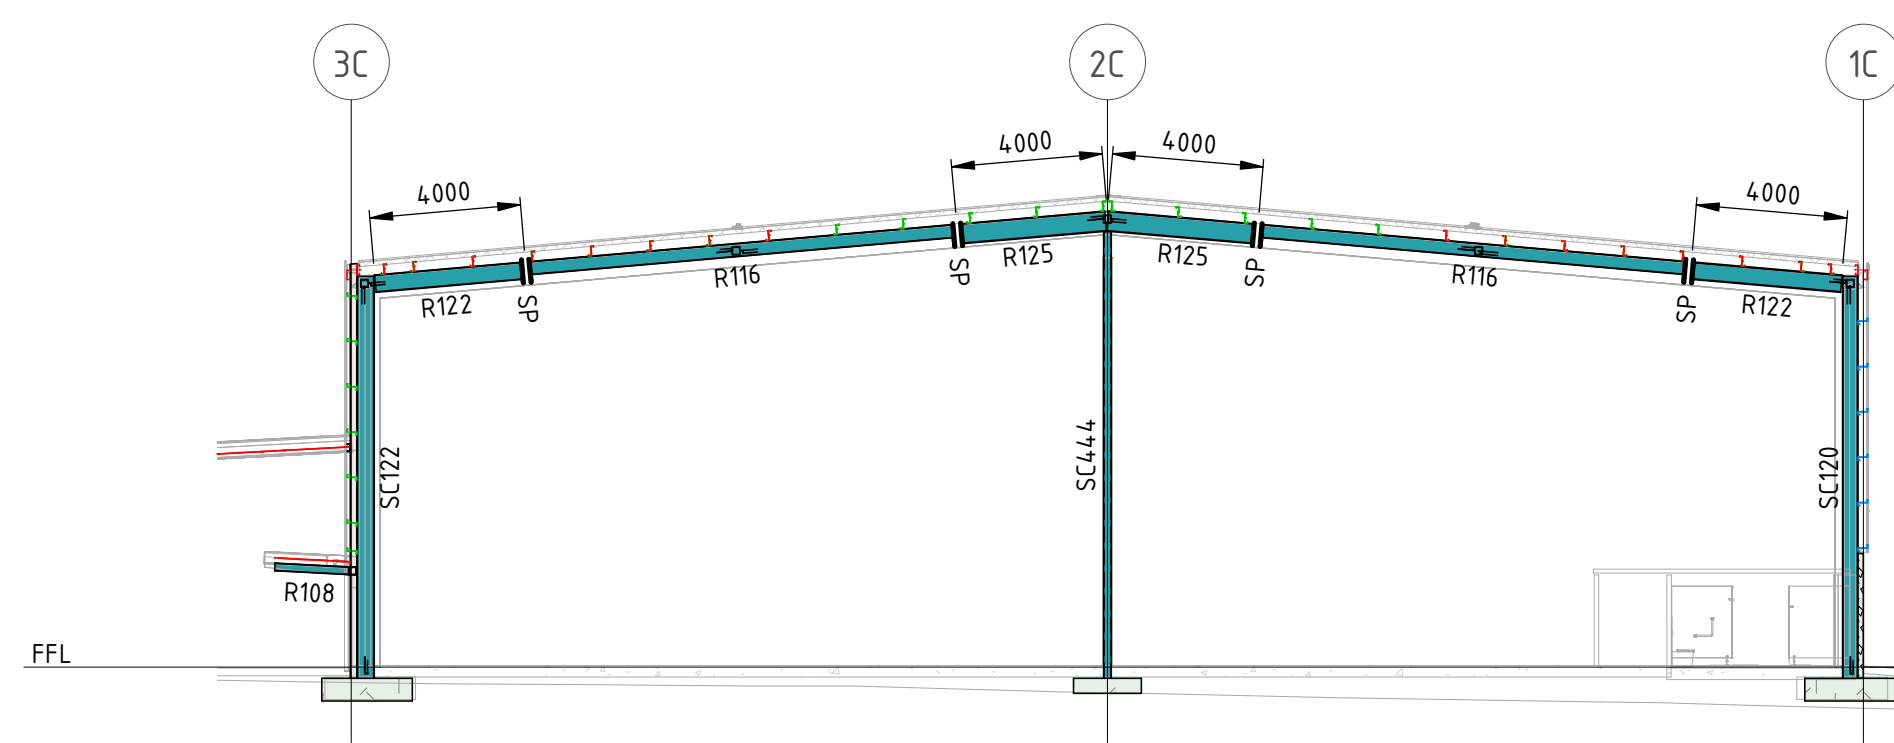


SECTION C2
SCALE 1 : 200
006002

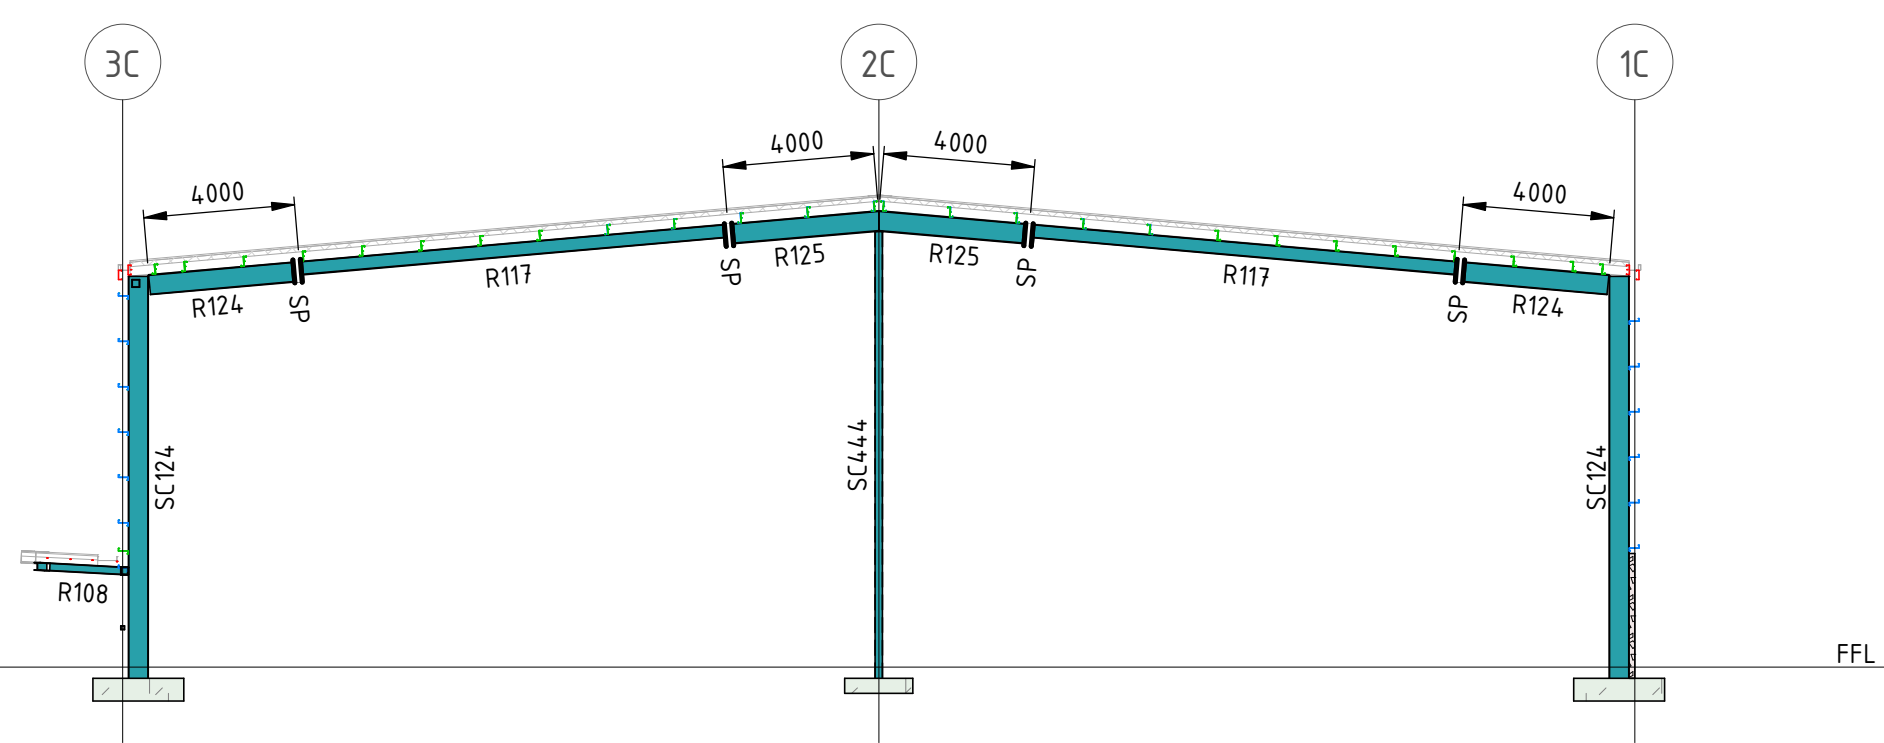


SECTION C3
SCALE 1 : 200
002002

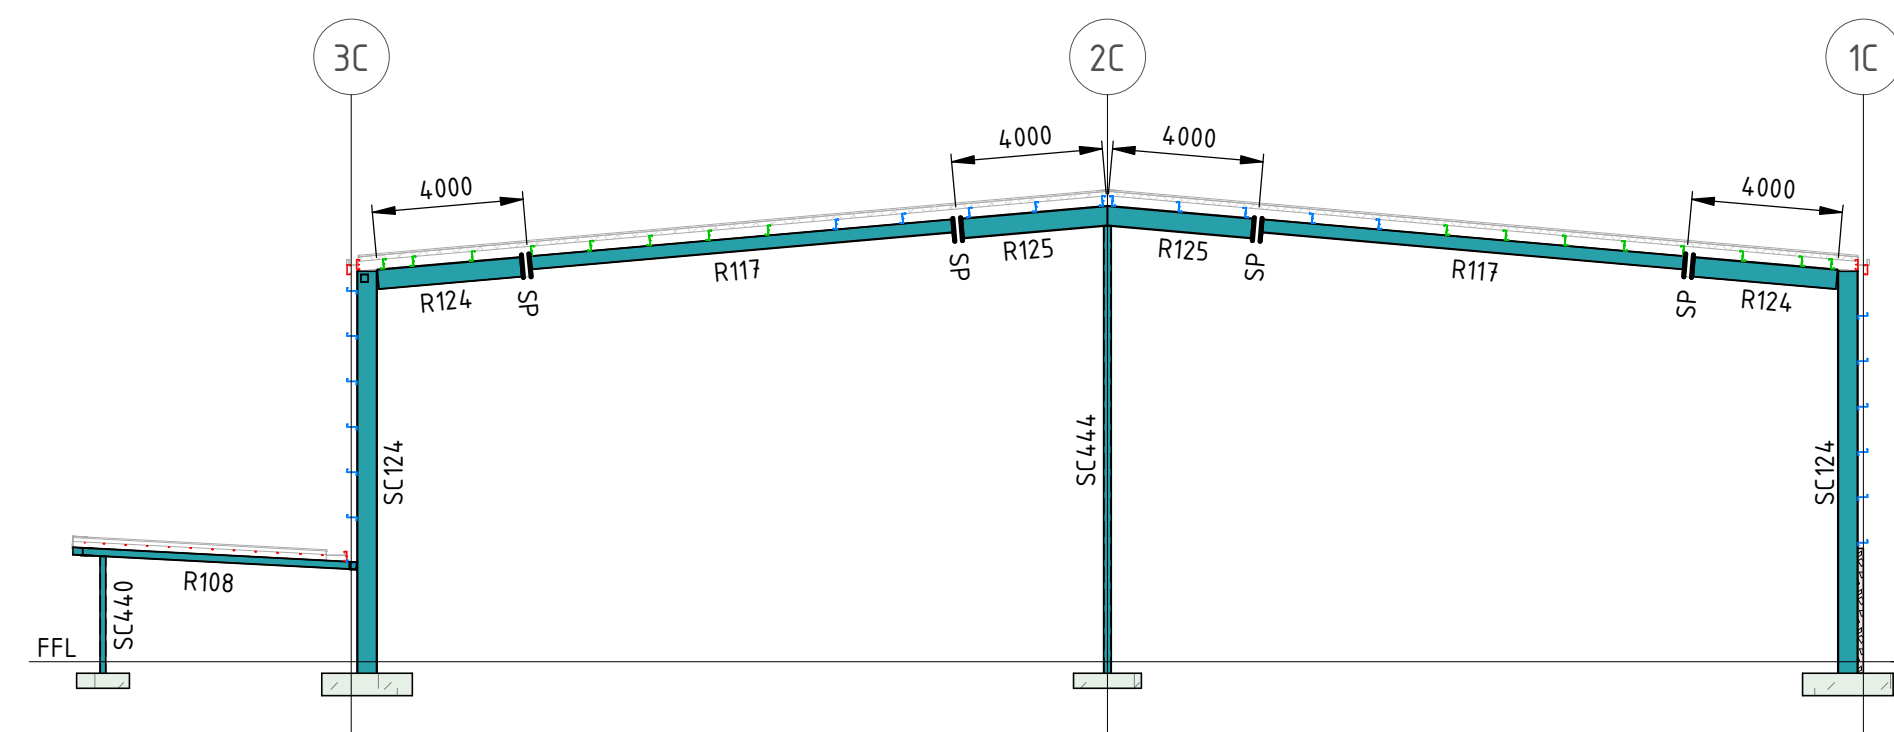


SECTION C4
SCALE 1 : 200
006502

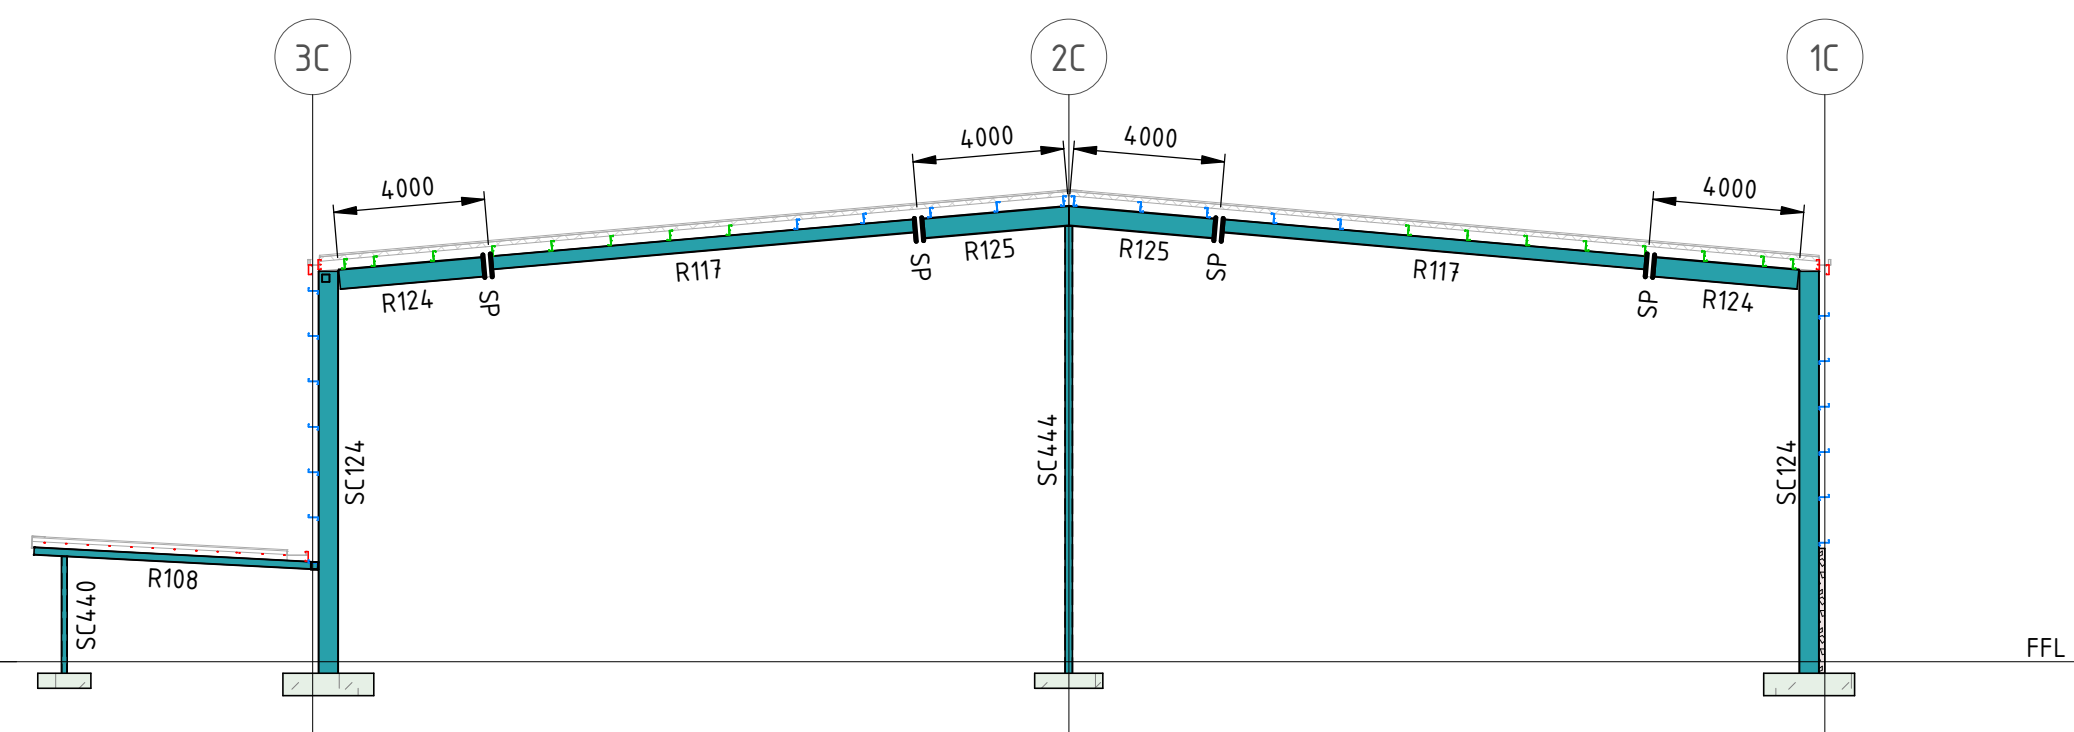


SECTION C5
SCALE 1 : 200
006502

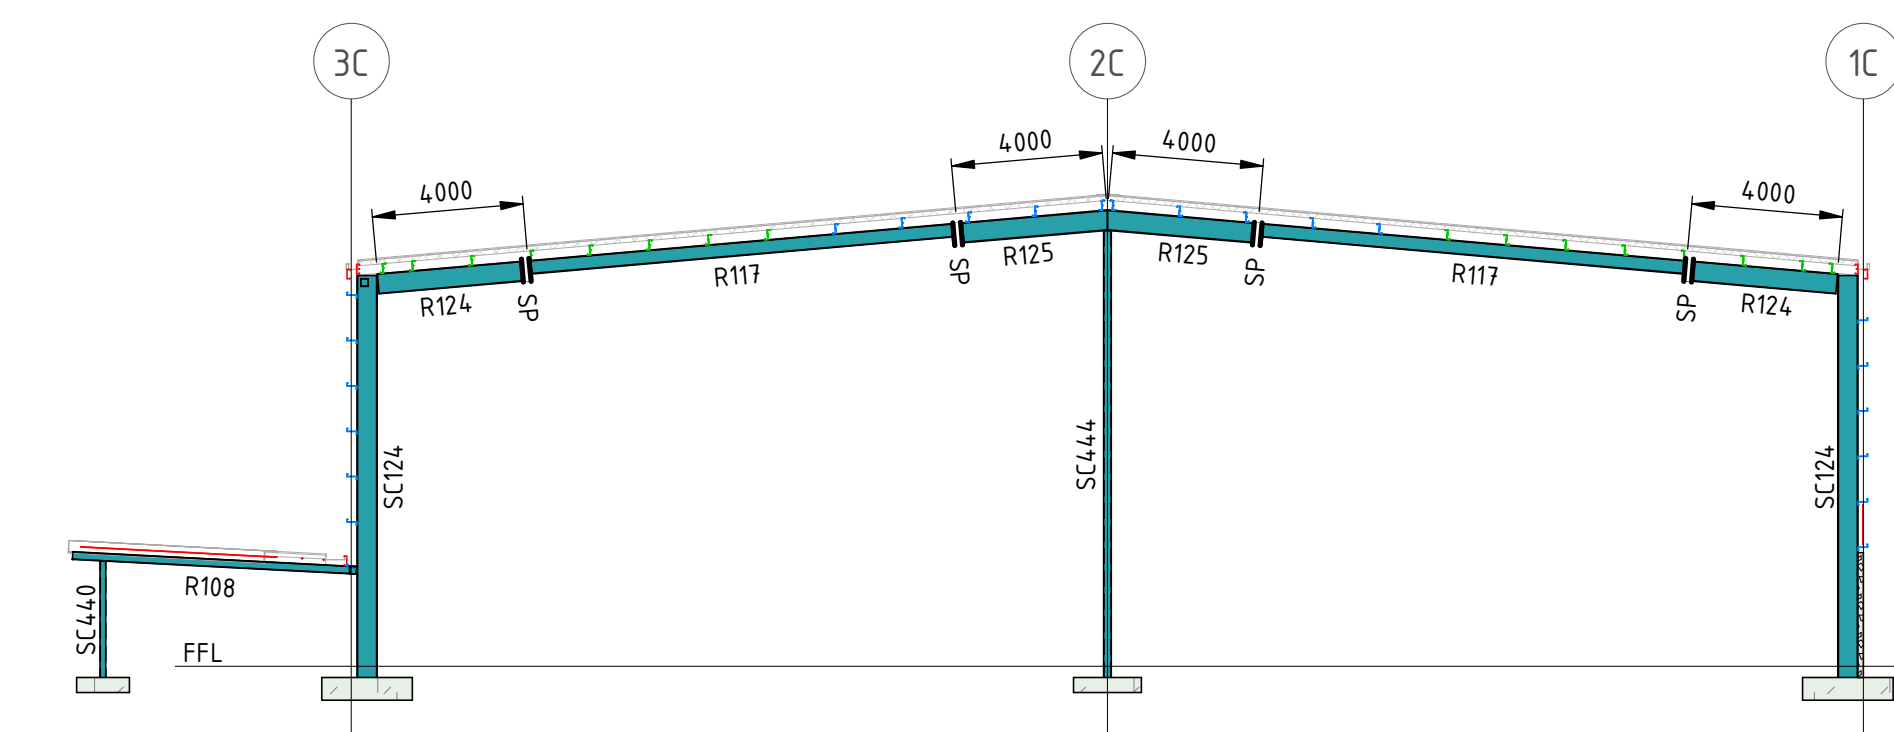


SECTION C6
SCALE 1 : 200
001003

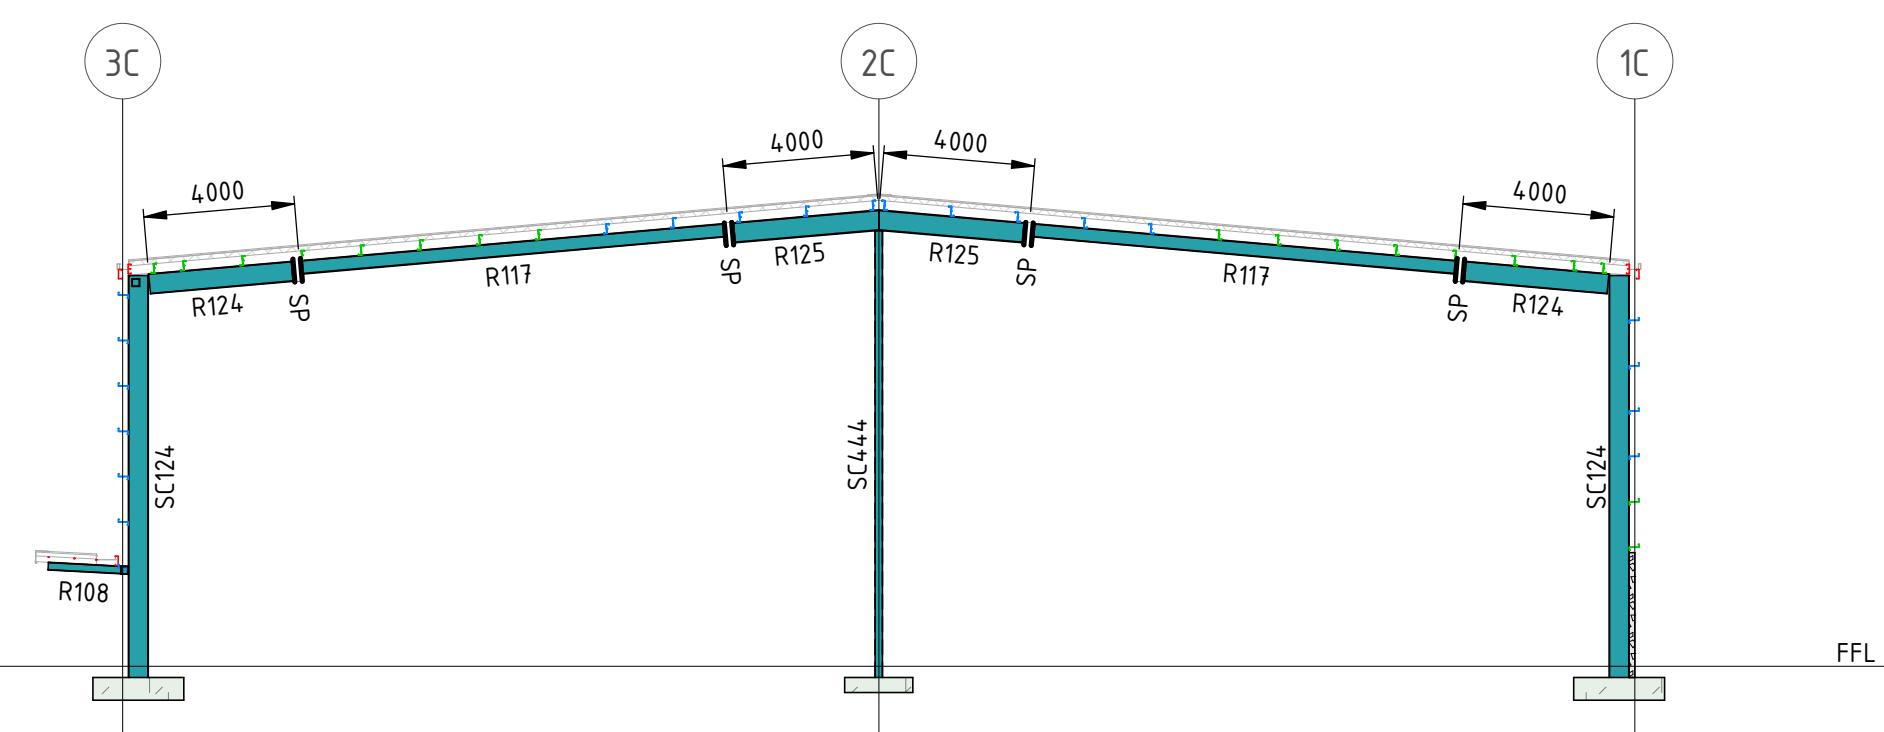


SECTION C7
SCALE 1 : 200
006502

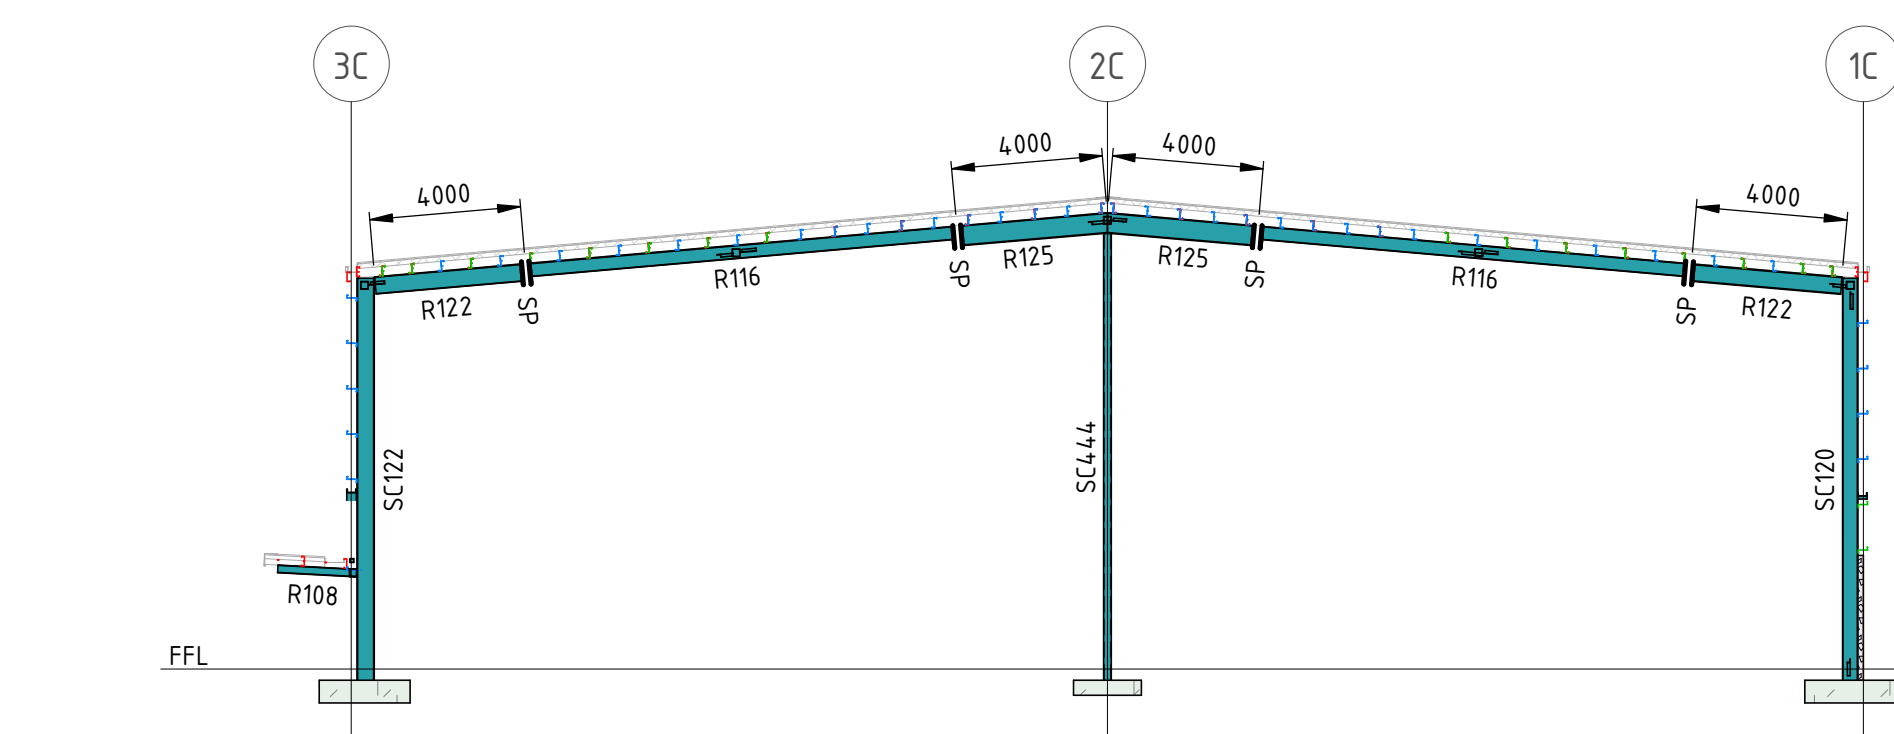

SECTION C8
SCALE 1 : 200 006502

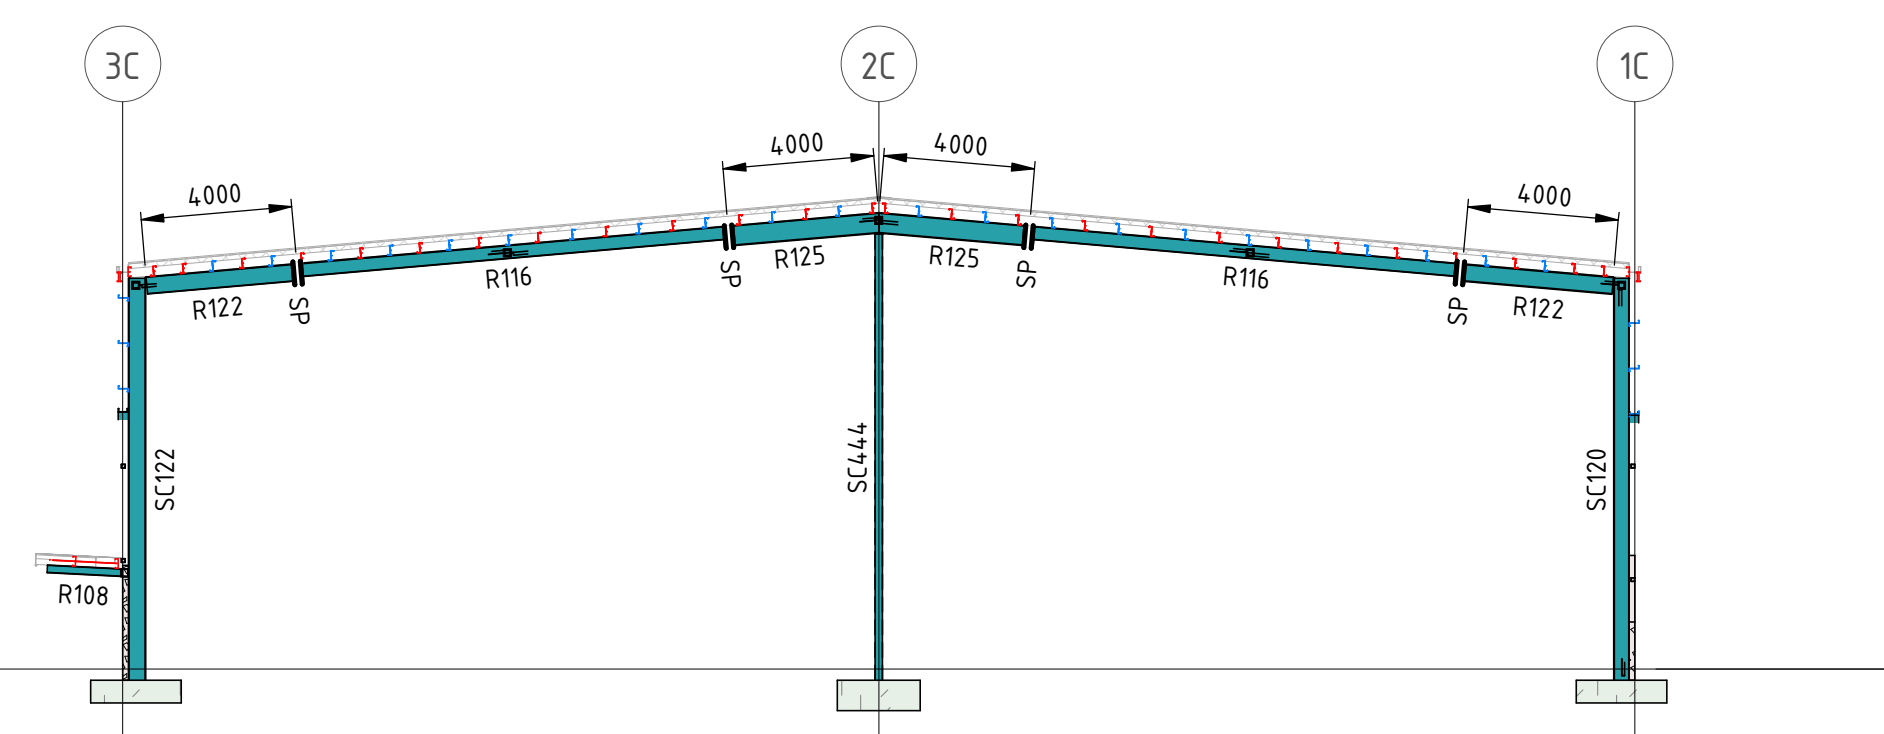

SECTION C9
SCALE 1 : 200 006502

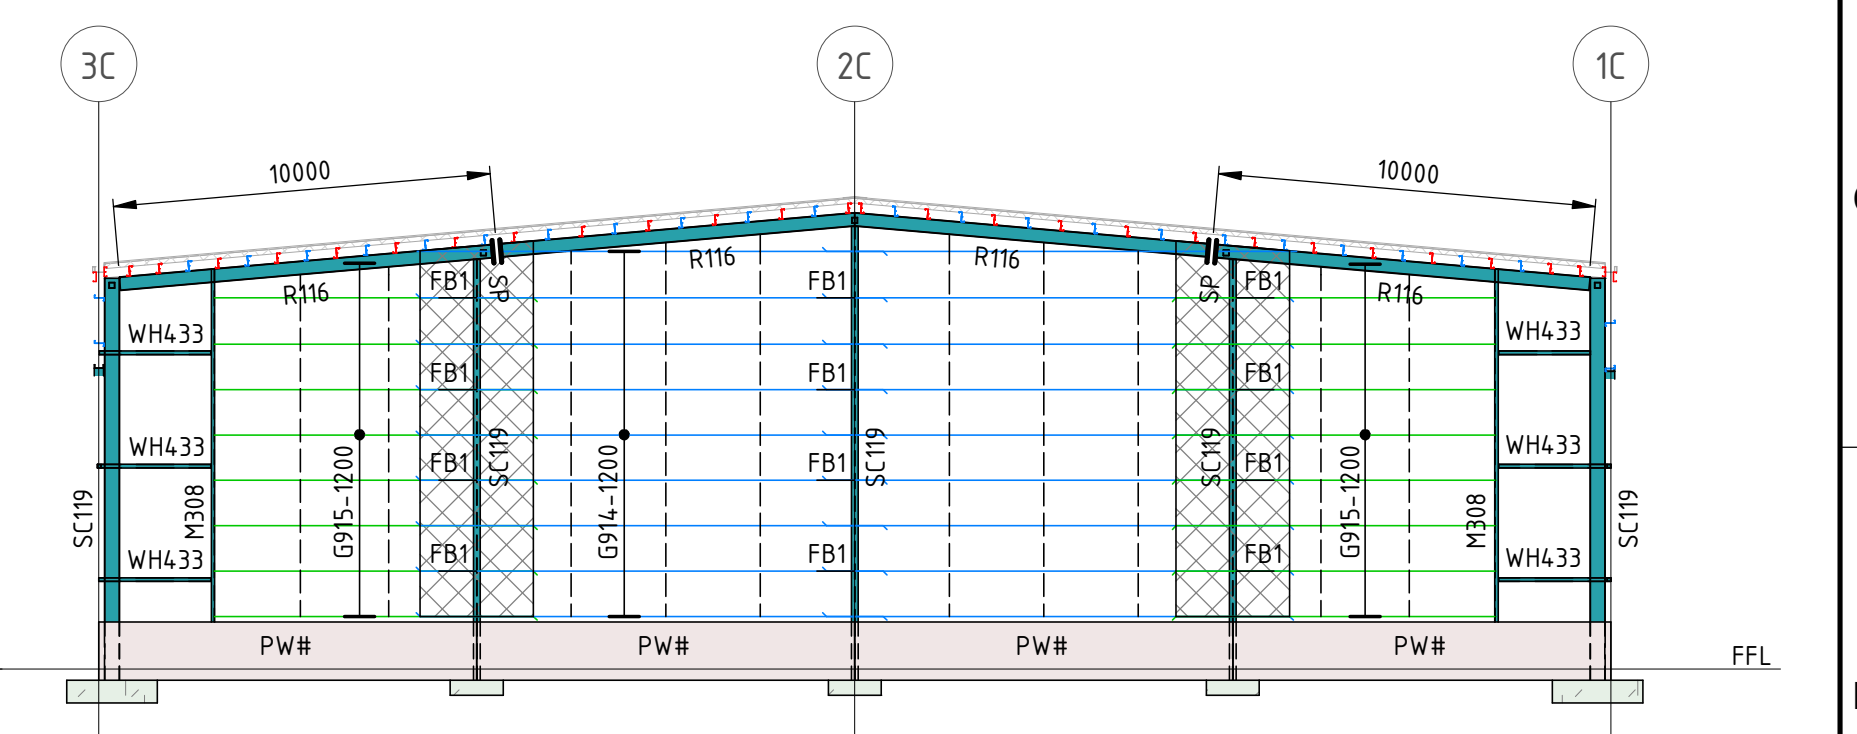


SECTION C10
SCALE 1 : 200 006502

MARK		SIZE
COLUMN		
SC119	410 UB 53.7	
SC120	410 UB 59.7	
SC122	460 UB 74.6	
SC124	530 UB 82.0	
SC440	150 x 150 x 5.0 SHS	
SC444	200 x 200 x 6.0 SHS	
MULLION		
M308	250 PFC	
BEAM		
B306	200 PFC	
B308	250 PFC	
OUTRIGGER		
OR308	250 PFC	
RAFTER		
R108	200 UB 25.4	
R116	360 UB 44.7	
R117	360 UB 50.7	
R122	460 UB 74.6	
R124	530 UB 82.0	
R125	530 UB 92.4	
ROOF BRACING		
RB725	75 x 75 x 8 EA	
STRUT		
S440	150x150x5.0SHS	
S444	200x200x6.0SHS	
WALL BRACING		
WB725	75 x 75 x 8 EA	
WALL HEAD		
WH433	100x100x5.0SHS	
GIRT		
G914	EZ250-15	
G915	EZ250-19	
G946	EC250-24	
PURLIN		
P914	EZ250-15	
P915	EZ250-19	
P916	EZ250-24	
P946	EC250-24	

ELEVATIONS AND SECTIONS NOTES

1. REFER S0.001-S0.003 FOR CONSTRUCTION NOTES
2. ALL PURLINS AND GIRTS TO BE STRAMIT EXACTA.
ANY ALTERNATIVE TO BE APPROVED BY NORTHPROP
CONSULTING ENGINEERS PRIOR TO FABRICATION.
3. REFER ARCHITECTURAL DRAWINGS FOR ALL ROOF
PENETRATION LOCATIONS.
4. THE EXACT LOCATION OF PENETRATION TRIMMING
PURLIN AND GIRTS ARE TO BE CONFIRMED WITH
SERVICE PROVIDER PRIOR TO FABRICATION.

ELEVATIONS AND SECTIONS LEGEND

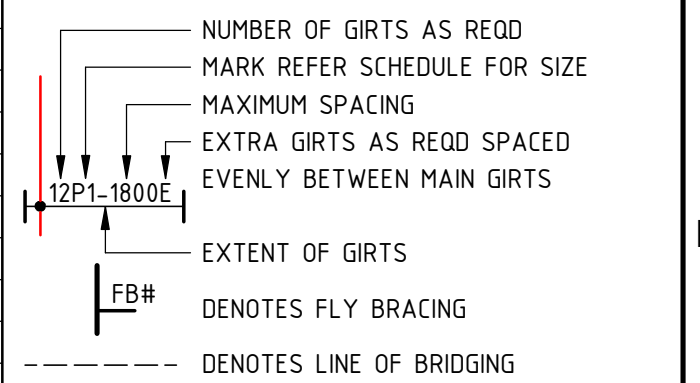

GIRT COLOURS

REFER MEMBER SCHEDULE FOR SIZE MARKS

- 1.0mm C/Z GIRT THICKNESS
- 1.2mm C/Z GIRT THICKNESS
- 1.5mm C/Z GIRT THICKNESS
- 1.9mm C/Z GIRT THICKNESS
- 2.4mm C/Z GIRT THICKNESS
- 3.0mm C/Z GIRT THICKNESS

GIRT LAPS

ALL GIRT LAPS TO BE 15% OF THE LARGEST
ADJACENT SPAN UNLESS NOTED OTHERWISE

