




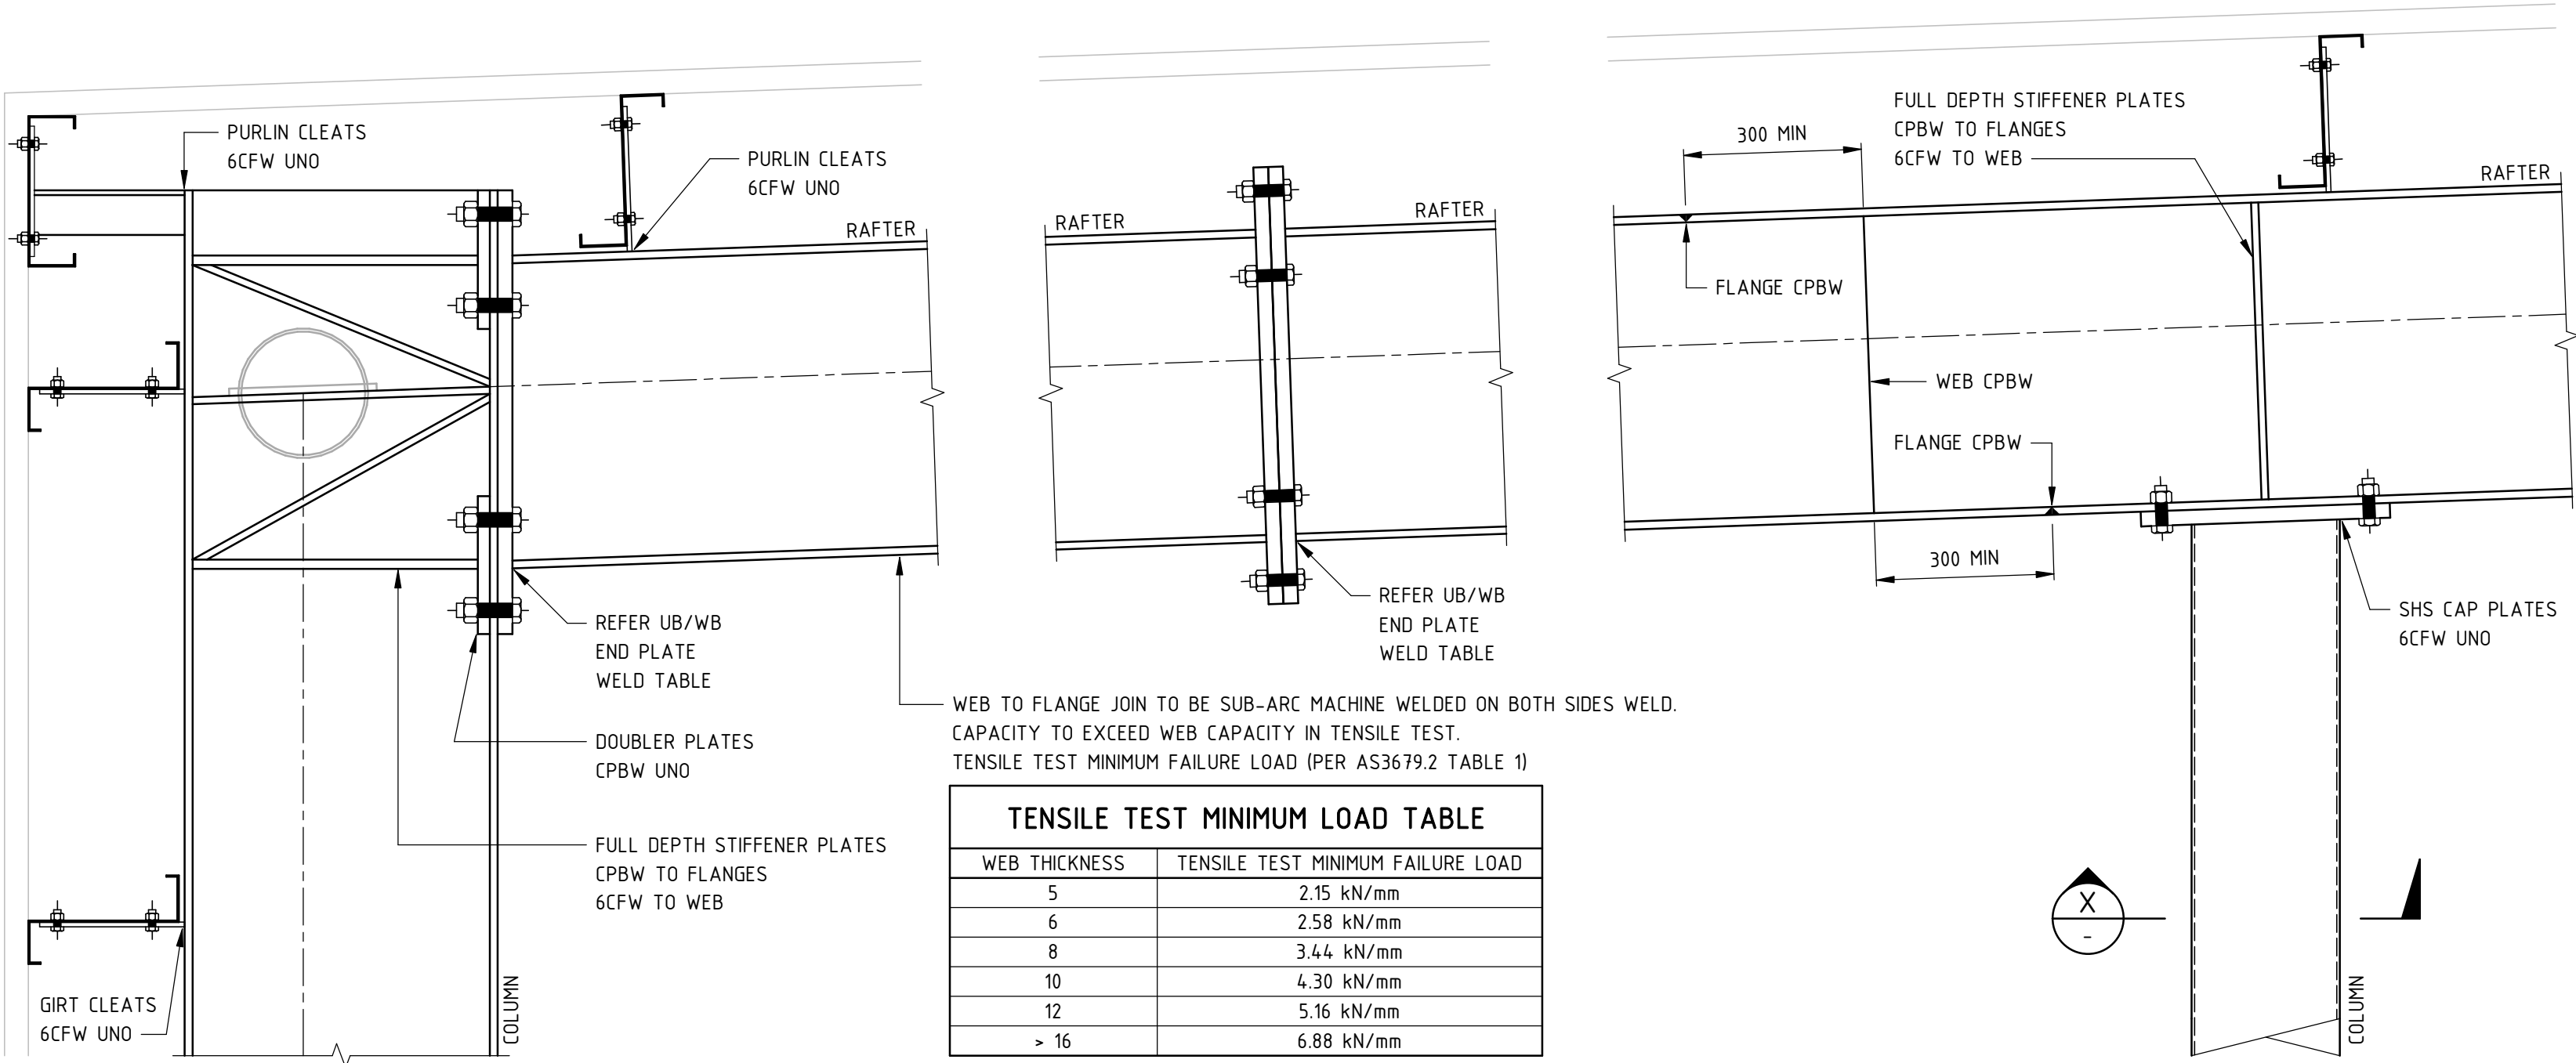

TENSILE TEST MINIMUM LOAD TABLE	
WEB THICKNESS	TENSILE TEST MINIMUM FAILURE LOAD
5	2.15 kN/mm
6	2.58 kN/mm
8	3.44 kN/mm
10	4.30 kN/mm
12	5.16 kN/mm
> 16	6.88 kN/mm

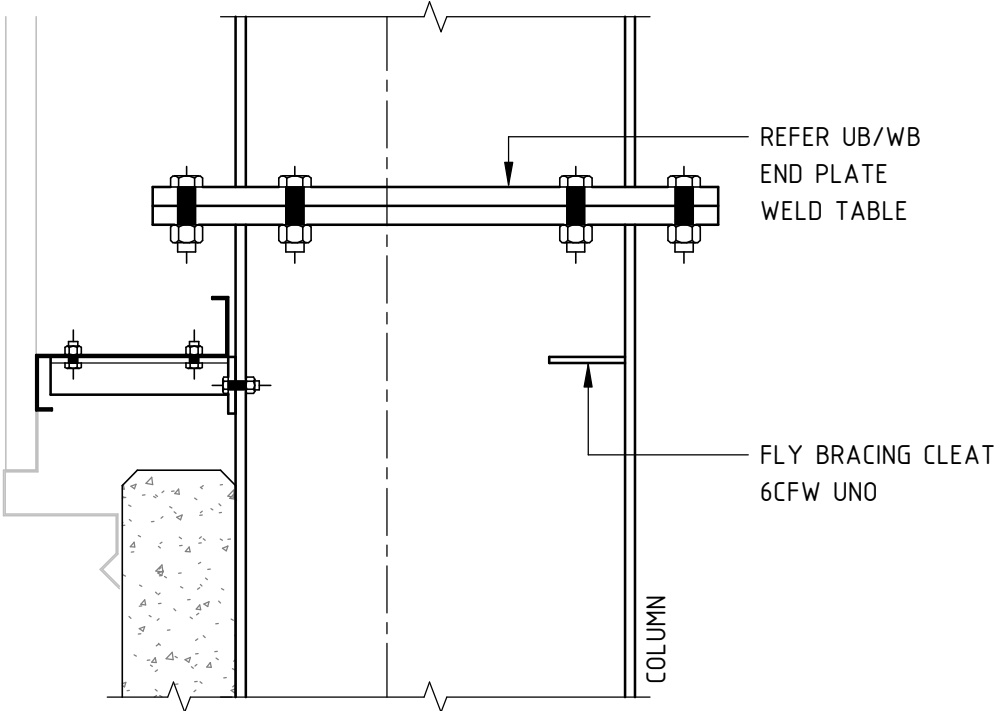


'T' PLATE OR CLEAT WELD TABLE	
'T' PLATE OR CLEAT THICKNESS	WEB WELD
≤ 12	6
≥ 16	8

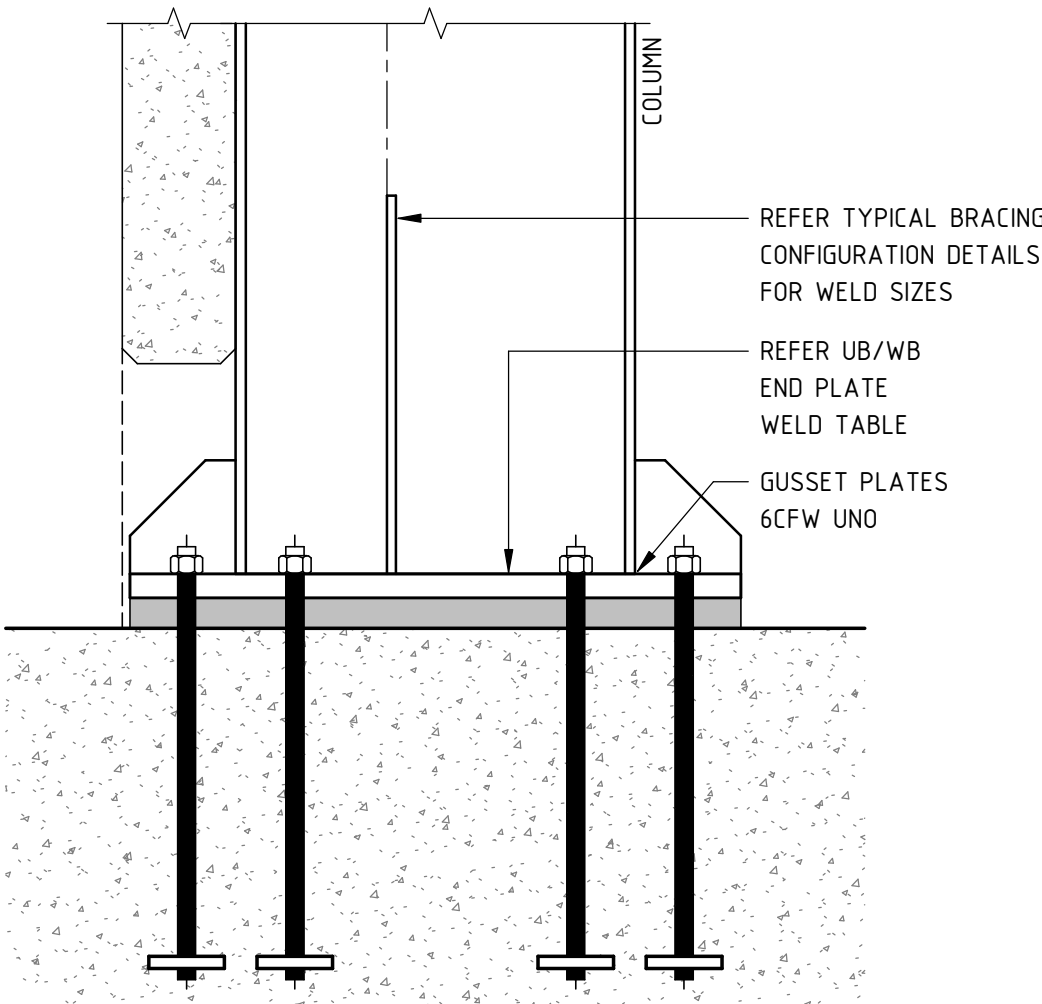

TYPICAL FRAMING ARRANGEMENTS WELD MAP DETAIL

NOTE:
ALL WELD SIZES TO BE EQUAL TO THICKNESS OF STEEL SECTION UNLESS NOTED OTHERWISE.
WELD MAP TO BE USED FOR STEEL FRAMING CONNECTION DETAILING.
REFER TO TYPICAL BRACING DETAILS FOR WELDS OF BRACING MEMBER CONNECTIONS.

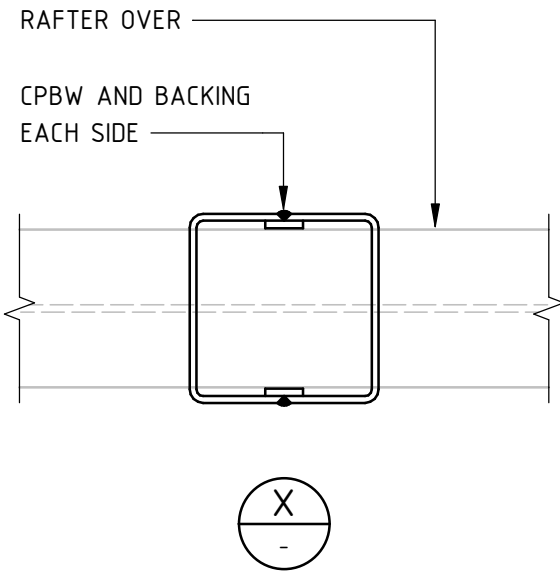

MATERIAL SUBSTITUTION LIST (NORTHROP APPROVED)			
MARK	SIZE	SUBSTITUTED SECTION	SUBSTITUTED GRADE
COLUMN			
SC119	410 UB 53.7		
SC120	410 UB 59.7		
SC121	460 UB 67.1		
SC122	460 UB 74.6		
SC124	530 UB 82.0		
SC433	100 x 100 x 5.0 SHS		
SC440	150 x 150 x 5.0 SHS		
SC444	200 x 200 x 6.0 SHS		
HANGING COLUMN			
HC444	200 x 200 x 6.0 SHS		
MULLION			
M308	250 PFC		
M433	100 x 100 x 5.0 SHS		
BEAM			
B306	200 PFC		
B308	250 PFC		
B309	300 PFC		
OUTRIGGER			
OR308	250 PFC		
RAFTER			
R108	200 UB 25.4		
R114	310 UB 40.4		
R116	360 UB 44.7		
R117	360 UB 50.7		
R119	410 UB 53.7		
R120	410 UB 59.7		
R121	460 UB 67.1		
R122	460 UB 74.6		
R124	530 UB 82.0		
R125	530 UB 92.4		
R126	610 UB 101		
R308	250 PFC		
R309	300 PFC		
RAKING ANGLE			
RA728	90 x 90 x 8 EA		
ROOF BRACING			
RB725	75 x 75 x 8 EA		
STRUT			
S433	100x100x5.0SHS		
S440	150x150x5.0SHS		
S444	200x200x6.0SHS		
WALL BRACING			
WB430	89x89x6.0SHS		
WB725	75 x 75 x 8 EA		
WALL HEAD			
WH433	100x100x5.0SHS		
WH437	125x125x5.0SHS		

COPYRIGHT : REPRODUCTION OF WHOLE OR PART OF THIS DOCUMENT CONSTITUTES AN INFRINGEMENT OF COPYRIGHT. THE INFORMATION, IDEAS, AND CONCEPTS CONTAINED IN THIS DOCUMENT ARE CONFIDENTIAL. THE RECIPIENT(S) OF THIS DOCUMENT IS PROHIBITED FROM DISCLOSING SUCH INFORMATION IDEAS AND CONCEPTS TO ANY PERSON WITHOUT THE PRIOR WRITTEN CONSENT OF THE BRISBANE AIRPORT CORPORATION PTY. LTD.	NS	STEEL DETAILS ISSUE	04.06.26	A
DRN		AMENDMENTS	DATE	REV

NORTHROP
PROJECT NUMBER: 250946

Drawn: HP	Checked:
Design Coordinated: HP	Compliance Checked: --
Authorised For Issue: NS	Construction Checked: --

SKYGATE PLAY

TYPICAL STEEL DETAILS - SHEET 1

 Brisbane Airport	BRISBANE AIRPORT CORPORATION PTY LTD						Scale:	1 : 10
	11 THE CIRCUIT, BRISBANE AIRPORT, QLD, 4008, AUSTRALIA						Size:	A1
	PO BOX 61, HAMILTON CENTRAL, QLD, 4507, AUSTRALIA T: +61 7 3408 3000 E: INFO@BNE.COM.AU W: BNE.COM.AU						Revision:	A
Drawing Number	Project No.	Originator	Volume	Level	Type	Discipline	Number	
	25021	NOR	XX	01	DR	ST	006901	