




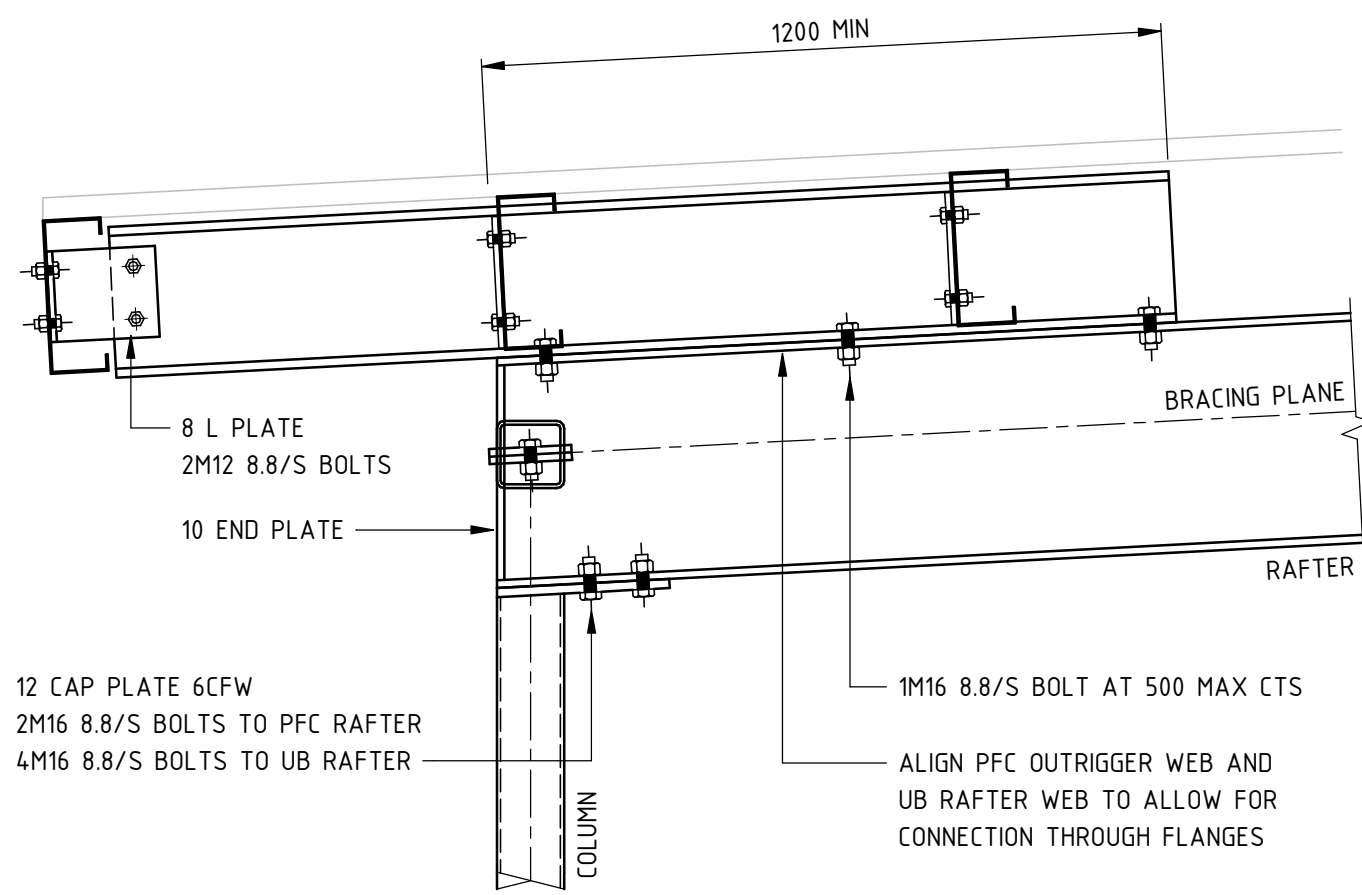


TYPICAL OFFICE COLUMN
TO RAFTER DETAIL

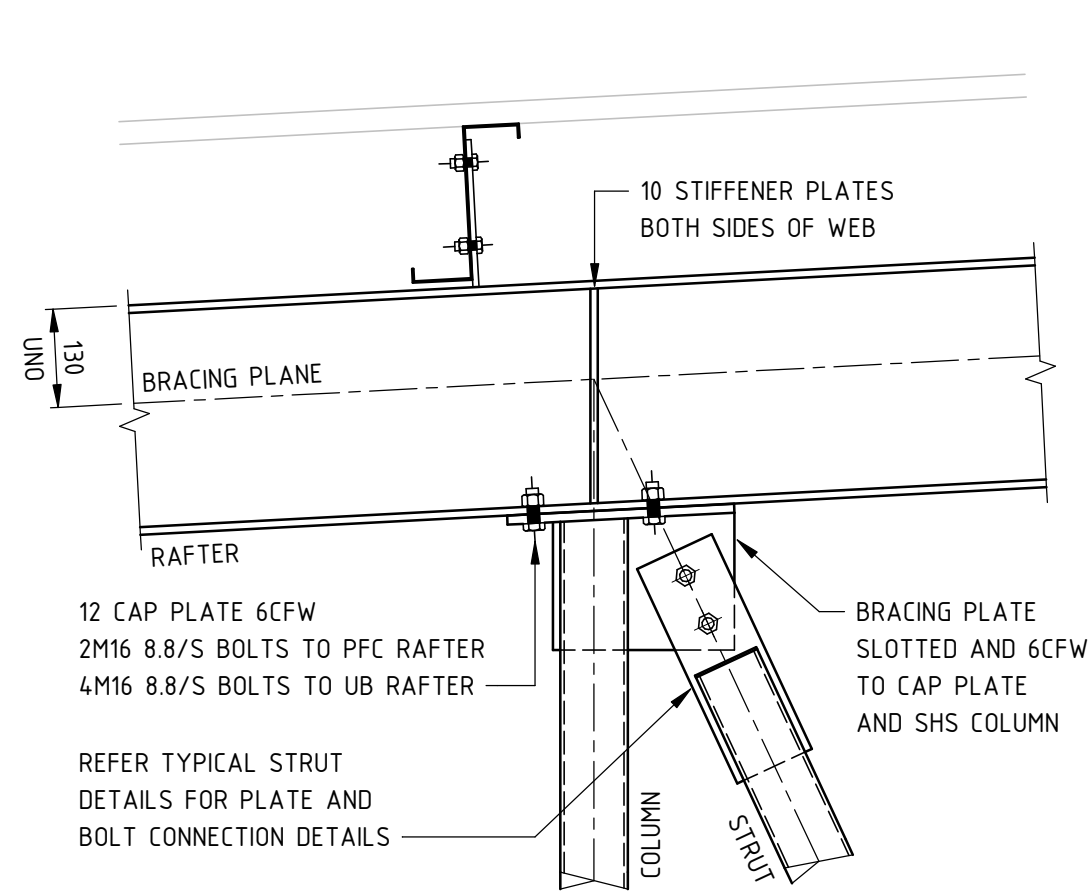


TYPICAL OFFICE COLUMN
TO RAFTER DETAIL

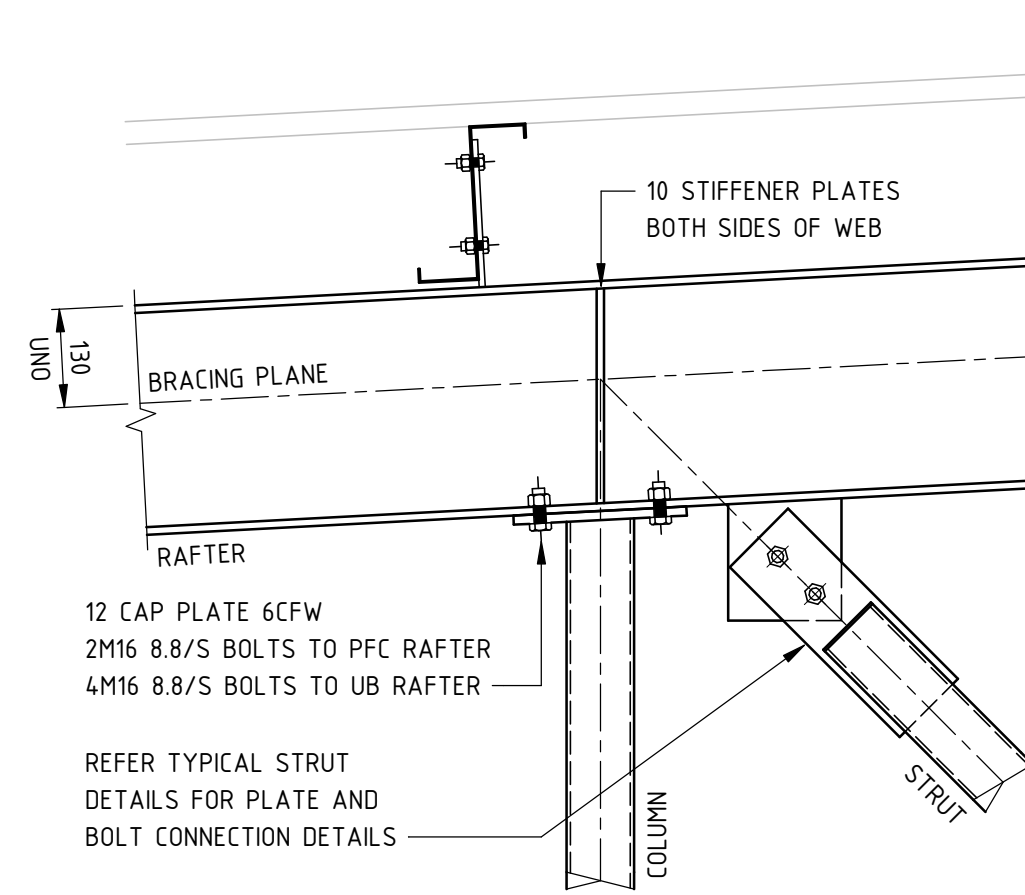


TYPICAL OFFICE COLUMN
TO RAFTER DETAIL

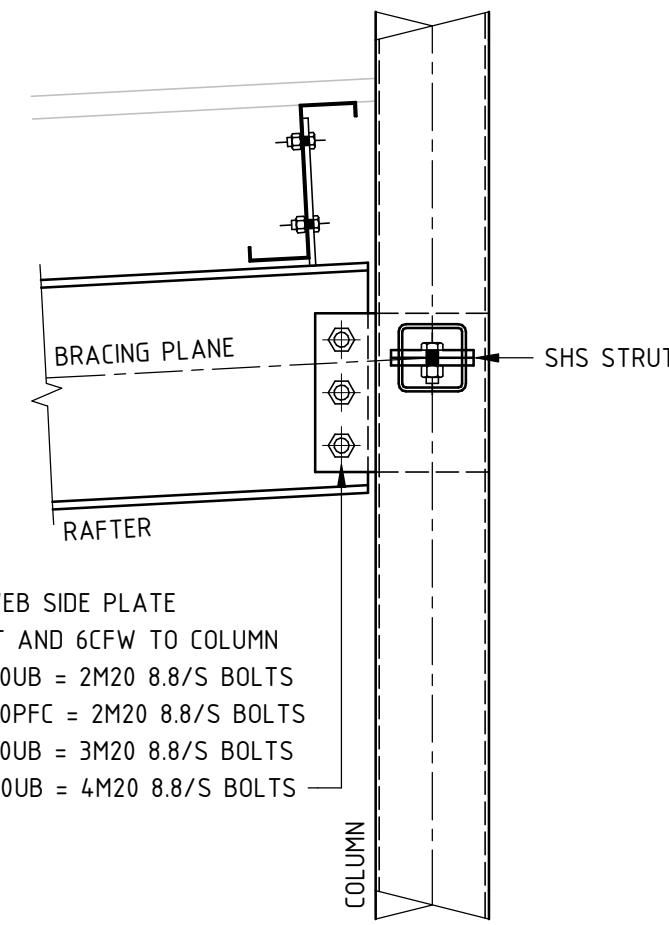


TYPICAL OFFICE COLUMN
TO RAFTER DETAIL

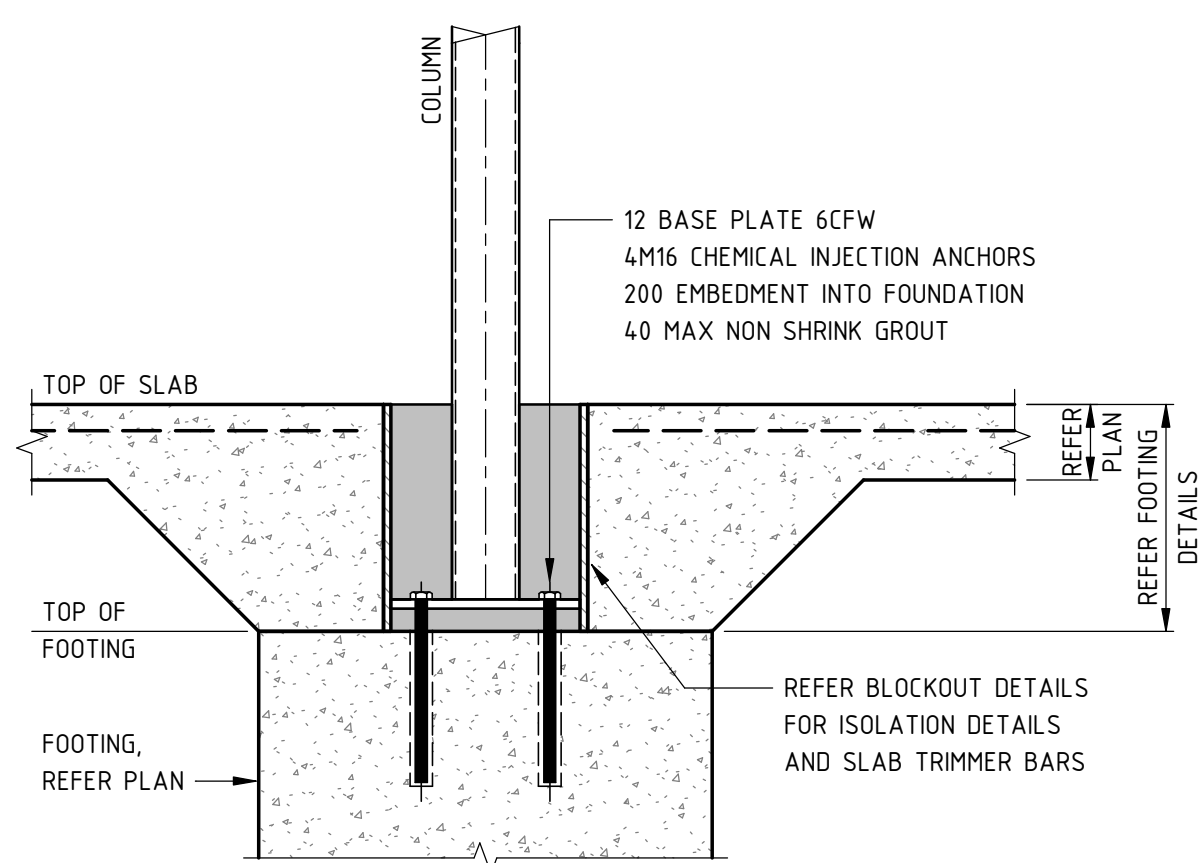


TYPICAL OFFICE COLUMN BASE PLATE DETAIL

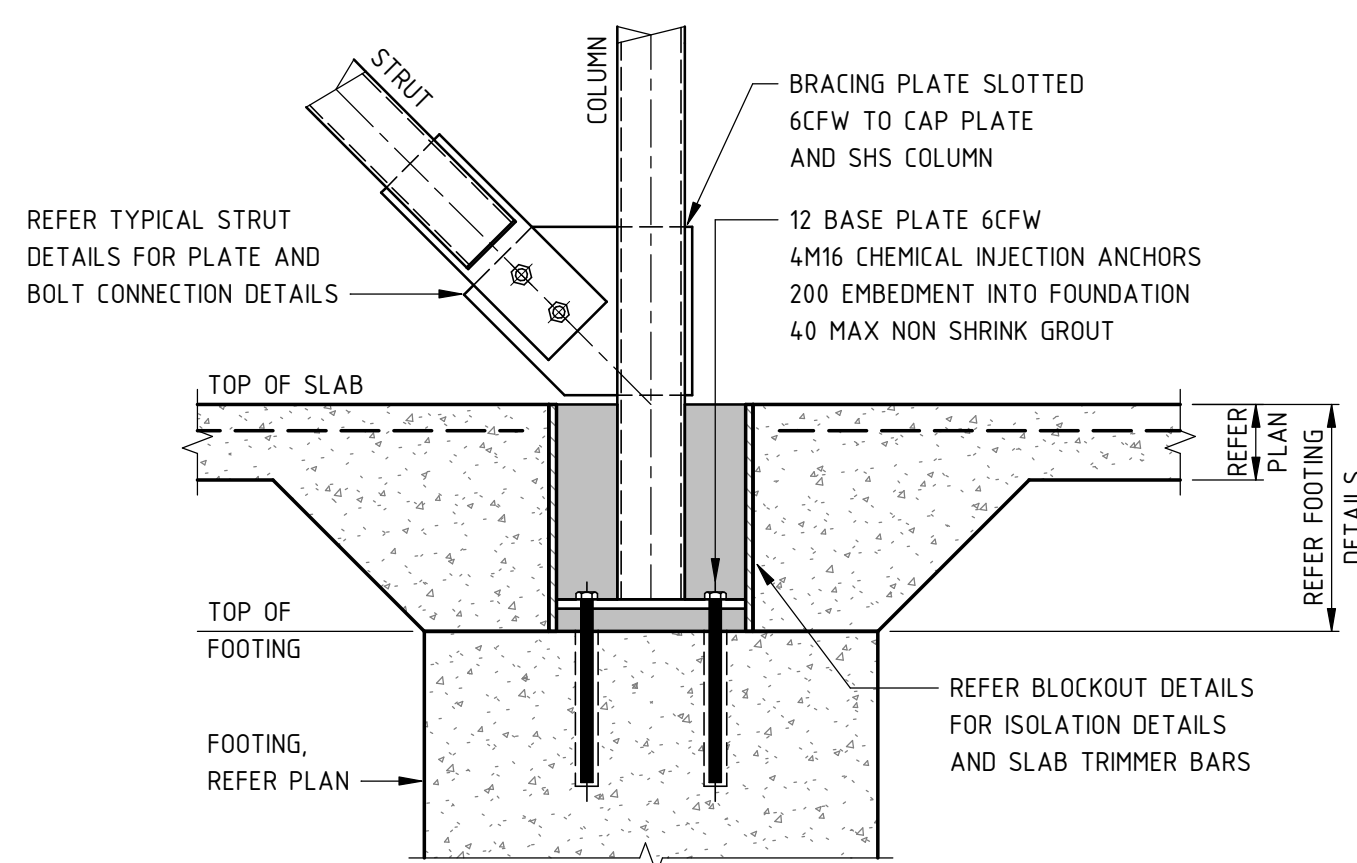


TYPICAL OFFICE COLUMN BASE PLATE DETAIL
AT WALL BRACING

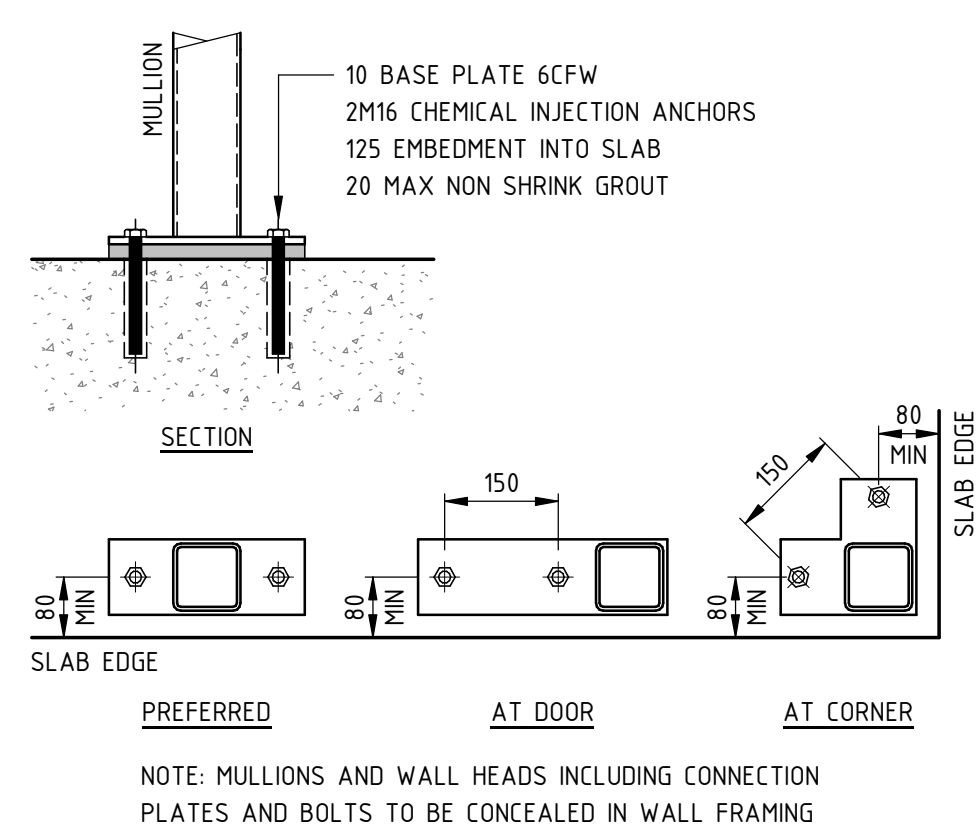

TYPICAL OFFICE MULLION BASE PLATE
TO SLAB DETAILS

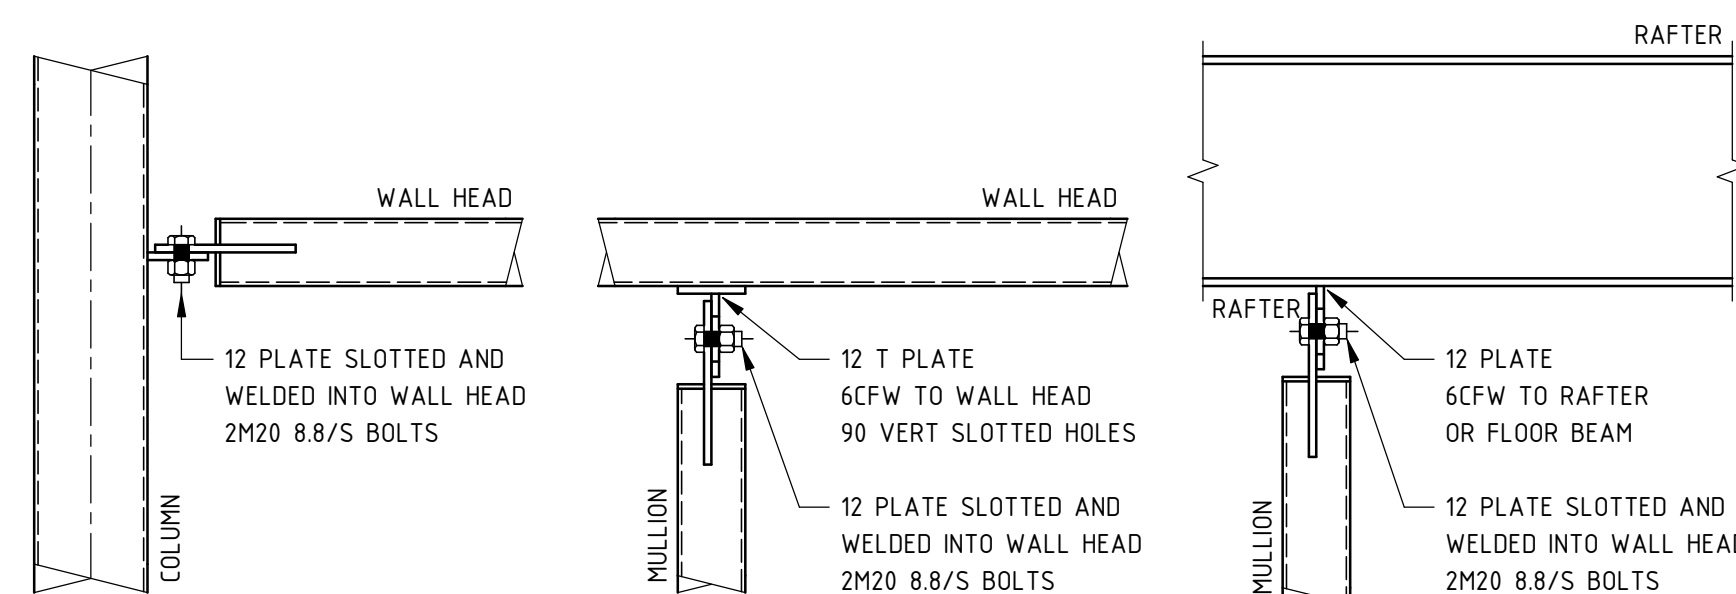

TYPICAL WALL HEAD AND MULLION CONNECTION DETAILS

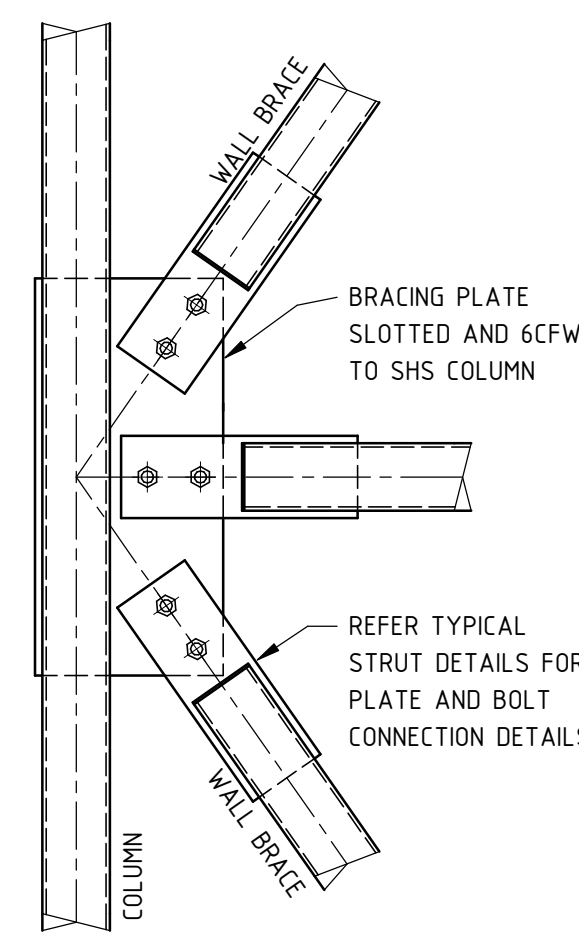

TYPICAL OFFICE WALL BRACE DETAIL

COPYRIGHT :
REPRODUCTION OF WHOLE OR PART OF THIS
DOCUMENT CONSTITUTES AN INFRINGEMENT
OF COPYRIGHT. THE INFORMATION, IDEAS,
AND CONCEPTS CONTAINED IN THIS
DOCUMENT ARE CONFIDENTIAL. THE
RECIPIENT(S) OF THIS DOCUMENT IS
PROHIBITED FROM DISCLOSING SUCH
INFORMATION IDEAS AND CONCEPTS TO ANY
PERSON WITHOUT THE PRIOR WRITTEN
CONSENT OF THE BRISBANE AIRPORT
CORPORATION PTY. LTD.

NS	STEEL DETAILS ISSUE	04.06.26	A
DRN	AMENDMENTS	DATE	REV

NORTHROP
PROJECT NUMBER: 250946

Drawn: HP	Checked:
Design Coordinated: HP	Compliance Checked: --
Authorised For Issue: NS	Construction Checked: --

SKYGATE PLAY
TYPICAL STEEL DETAILS SHEET 4

BRISBANE AIRPORT CORPORATION PTY LTD 11 THE CIRCUIT, BRISBANE AIRPORT, QLD 4008, AUSTRALIA PO BOX 61, HAMILTON CENTRAL, QLD 4507, AUSTRALIA T: +61 7 3406 3000 E: INFO@BNE.COM.AU W: BNE.COM.AU	Scale: 1 : 10 Size: A1 Revision: A
Project No. Originator Volume Level Type Discipline Number 25021 - NOR - XX - 01 - DR - ST - 006904	