


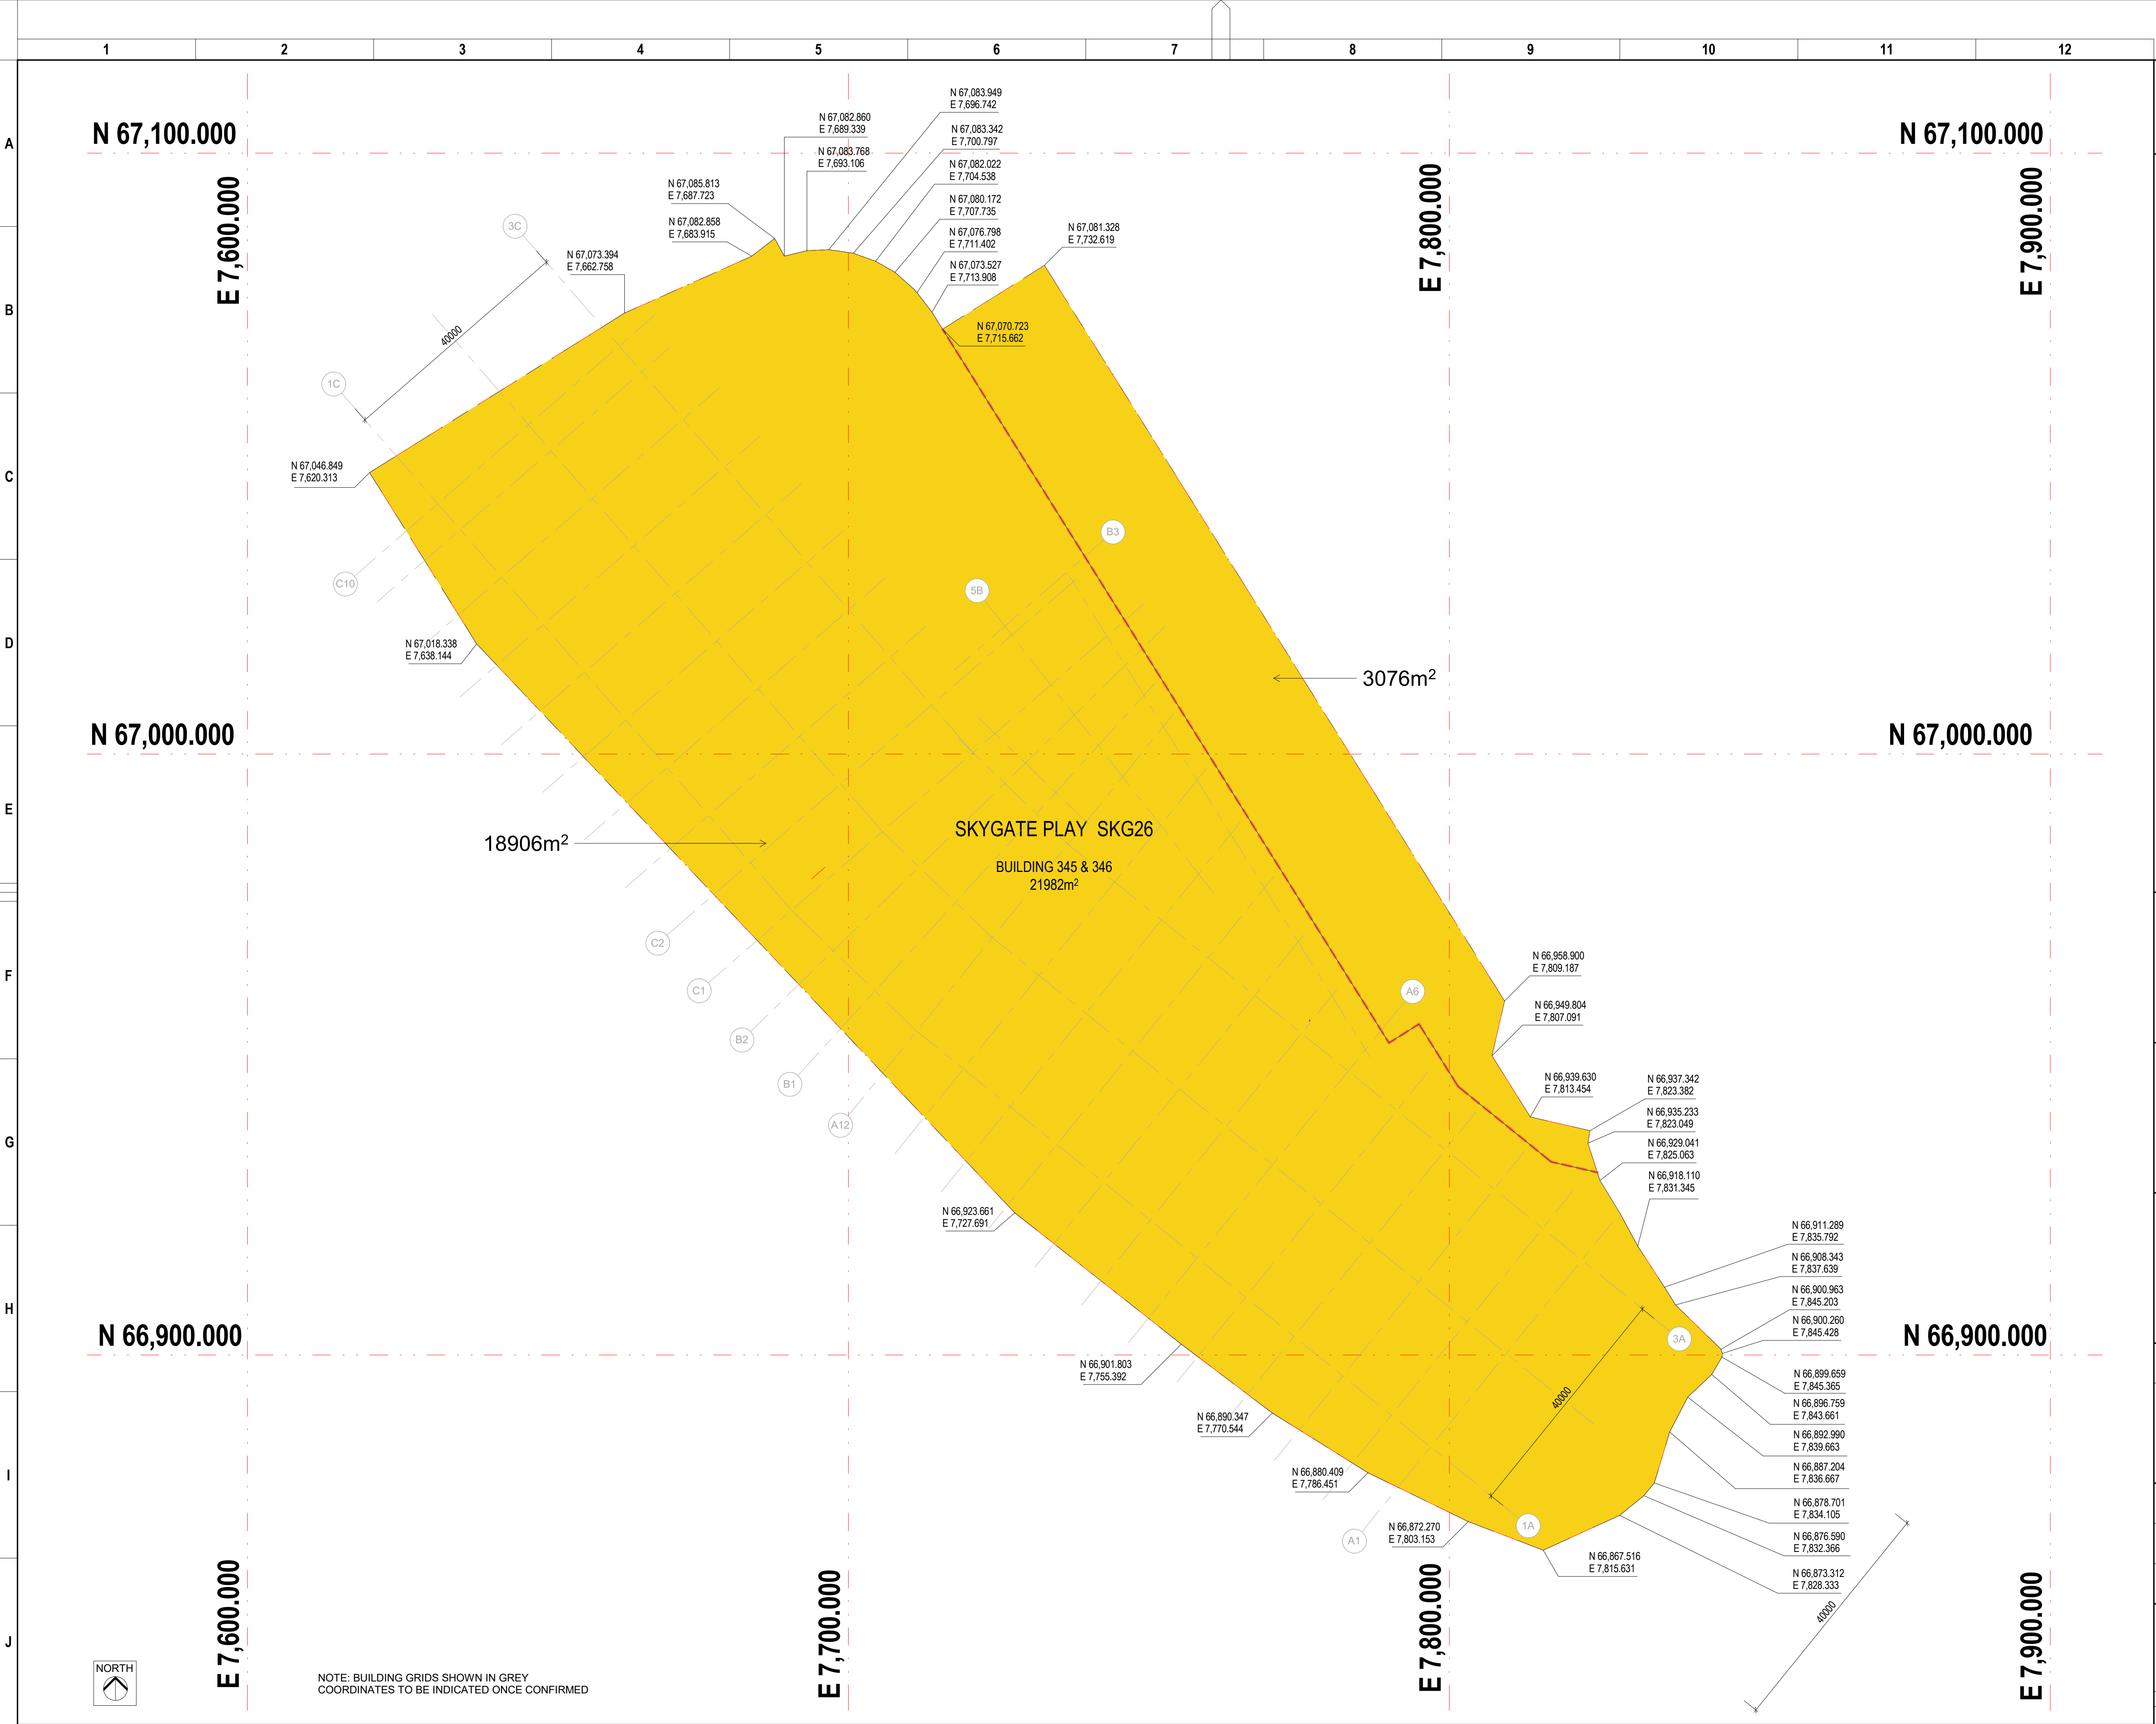

COPYRIGHT: REPRODUCTION OF WHOLE OR PART OF THIS DOCUMENT CONSTITUTES AN INFRINGEMENT OF COPYRIGHT. THE INFORMATION, IDEAS AND CONCEPTS CONTAINED IN THIS DOCUMENT ARE CONFIDENTIAL. THE RECIPIENT(S) OF THIS DOCUMENT IS PROHIBITED FROM DISCLOSING SUCH INFORMATION IDEAS AND CONCEPTS TO ANY PERSON WITHOUT THE PRIOR WRITTEN CONSENT OF THE BRISBANE AIRPORT CORPORATION PTY. LTD.

DRN	AMENDMENTS	DATE	REV
JB	30% DD ISSUE	12.09.2025	1
JB	AREA REQUESTS	23.09.2025	2
JB	FOR COORDINATION	12.11.2025	3
JB	60% DD ISSUE 1	18.12.2025	4
JB	60% DD ISSUE 2	05.02.2026	5

Archipelago

Archipelago
Level 3, 109 George Street, Brisbane QLD 4000
T +617 3238 4800 www.archipelago.com.au
© ARCHIPELAGO ARCHITECTS PTY. LTD. All Rights Reserved
This work is copyright and cannot be reproduced or copied by any means without written permission of Archipelago Architects Pty Ltd. Any
license, express or implied, to use this document for any purpose
whatsoever is restricted to the terms of the agreement between Archipelago Architects P
y Ltd and the instructing party.

SKYGATE PLAY	
BAC GRID SETOUT PLAN	
Drawn JB	Checked DC
Design Coordinated N/A	Compliance Checked N/A
Authorised For Issue DC	Construction Checked N/A

 Brisbane Airport Corporation Pty Ltd 11 The Circuit Brisbane Airport QLD 4008 Telephone : 61 7 3406 3000 Facsimile : 61 7 3406 3111 Email : info@bne.com.au www.brisbaneairport.com.au ABN 54 076 870 650		Scale 1 : 500
Project No. 25021 - ARC - XX - 01 - DR - AR - 000010		Size A1
Drawing No. 25021 - ARC - XX - 01 - DR - AR - 000010		Revision 5
Project No. 25021 - ARC - XX - 01 - DR - AR - 000010		Number