


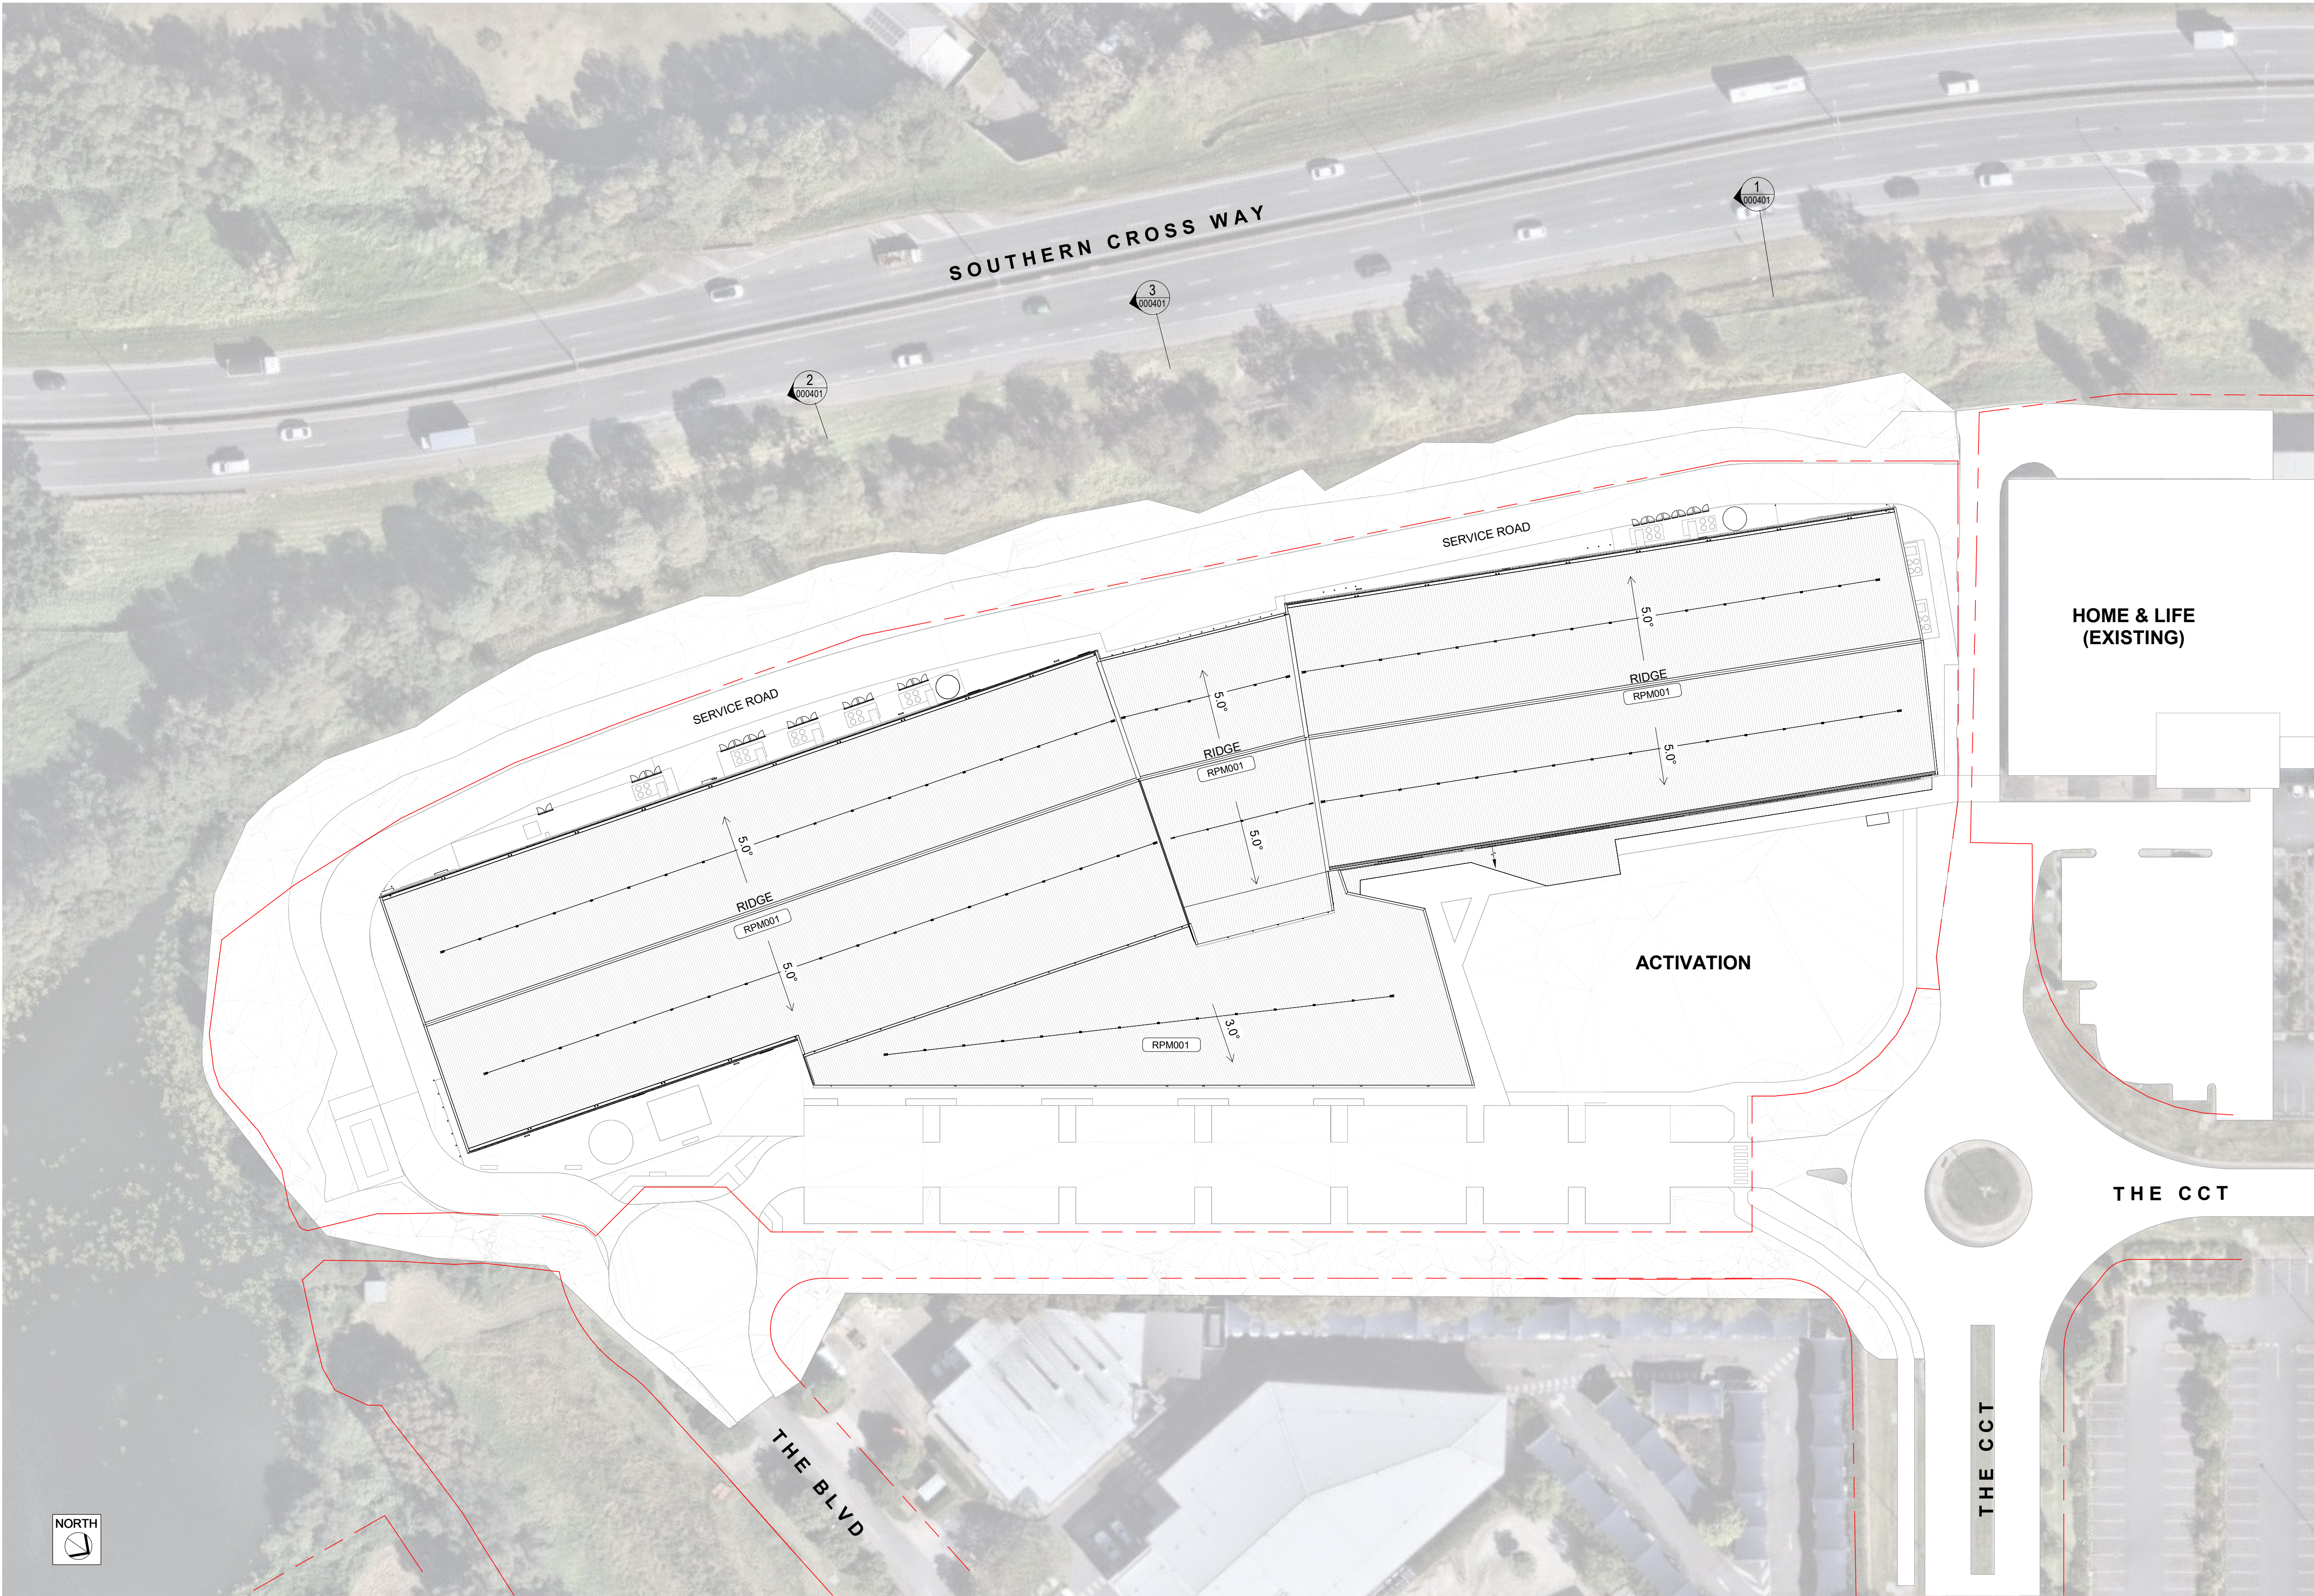

1 SITE PLAN
1 : 500

COPYRIGHT :
REPRODUCTION OF WHOLE OR PART OF THIS DOCUMENT
CONSTITUTES AN INFRINGEMENT OF COPYRIGHT. THE
INFORMATION, IDEAS AND CONCEPTS CONTAINED IN THIS
DOCUMENT ARE CONFIDENTIAL. THE RECIPIENT(S) OF
THIS DOCUMENT IS PROHIBITED FROM DISCLOSING SUCH
INFORMATION IDEAS AND CONCEPTS TO ANY PERSON
WITHOUT THE PRIOR WRITTEN CONSENT OF THE
BRISBANE AIRPORT CORPORATION PTY. LTD.

DRN	AMENDMENTS	DATE	REV
JB	PRELIMINARY WIP ISSUE	25.07.2025	1
JB	WIP TENANCY PLAN	21.08.2025	2
JB	WIP CONCEPT	22.08.2025	3
JB	QUANTITY SURVEYOR ISSUE	29.08.2025	4
JB	30% DD ISSUE	12.09.2025	5
JB	FOR COORDINATION	12.11.2025	6
JB	FOR COORDINATION	04.12.2025	7
JB	60% DD ISSUE 1	18.12.2025	8
DC	FOR COORDINATION	21.01.2026	9
JB	FOR COORDINATION	29.01.2026	10
JB	60% DD ISSUE 2	05.02.2026	11

TAG LEGEND	
BCT1	Baby Change Tables
BIN1	WASTE BIN - RECESSED
BIN2	NAPPY BIN - IN CUPBOARD
BOL001	BOLLARD - FIXED
BOL002	BOLLARD - REMOVABLE
CFL01	CEILING - PLASTERBOARD
CFL03	CEILING - FIRE RATED
CLD004	INSULATED PANEL CLADDING - KINGSPAN KS1000RW WALL PANEL OR SIMILAR - REFER TO SECTION J REPORT
CLD005	DANPALON SINGLE GLAZED TRANSLUCENT CLADDING
CLD006	PRECAST CONCRETE
COL	STRUCTURAL COLUMN - REFER STRUCTURAL ENGINEER
CON001	CONCRETE SLAB
CON002	CONCRETE SLAB - EXTERNAL HARDSTAND
CT1	CURTAIN TRACK
DP	DOWNPIPE
FH	DOUBLE PILLAR FIRE HYDRANT REFER HYD. ENG.
FHR	FIRE HOSE REEL REFER HYD. ENG.
FLW003	FLOOR DRAIN
GPO1	GPO SINGLE
GPOC	GPO SINGLE - CLEANERS
GT01	COLORBOND FOLDED STEEL GUTTER
GT02	KINGSPAN MEMBRANE LINED INSULATED GUTTER
M-FLT-1	WET AREA TILES - FLOOR
M-FTL2	WET AREA TILES - FLOOR
M-TIL2	WET AREA - WALL TILE
M-VNL1	SHEET VINYL - FLOOR
MCT1	PRIVACY CURTAIN
MEC001	MECHANICAL DUCT - REFER MECHANICAL ENGINEER
MLV001	MECHANICAL EXHAUST LOUVRE
MR2	MIRROR 2
MR3	MIRROR 3
RPM001	INSULATED ROOF PANEL
RSS001	ROOF SAFETY SYSTEM
SCR001	POWDERCOATED ALUMINIUM SCREENING
SD3	SOAP DISPENSER
SNK2	SINK - CLEANERS
STR001	STRUCTURAL COLUMN - REFER STRUCTURAL ENGINEER
T1	WC - STANDARD
T2	WC - AMBULANT
T4	WC - UNIVERSAL
THR1	TOILET ROLL HOLDER
TMV	THERMOSTATIC MIXING VALVE
TP1	TAP - WALL MOUNTED SENSOR
TRH2	TOILET ROLL HOLDER
UR1	URINAL - WALL HUNG
UR4	URINAL - TROUGH
W.01	POWDERCOATED ALUMINIUM FRAMED COMMERCIAL GLAZING

Archipelago

Archipelago
Level 3, 109 George Street, Brisbane QLD 4000
T +617 3238 4800 www.archipelago.com.au
© ARCHIPELAGO ARCHITECTS PTY. LTD. All Rights Reserved
This work is copyright and cannot be reproduced or copied by any means without written
permission of Archipelago Architects Pty Ltd. Any
license, express or implied, to use this document for any purpose
whatsoever is restricted to the terms of the agreement between Archipelago Architects Pt
y Ltd and the instructing party.

SKYGATE PLAY	
SITE PLAN	

Drawn JB	Checked DC
Design Coordinated N/A	Compliance Checked N/A
Authorised For Issue DC	Construction Checked N/A

 Brisbane Airport	Brisbane Airport Corporation Pty Ltd 11 The Circuit Brisbane Airport QLD 4008 PO Box 61 Hamilton QLD 4007 Australia						Scale 1 : 500
	Telephone : 61 7 3406 3000 Facsimile : 61 7 3406 3111 Email : info@bne.com.au www.brisbaneairport.com.au ABN 54 076 870 650						Size A1
							Revision 11
Drawing No.	Project No.	Originator	Volume	Level	Type	Discipline	Number
	25021	- ARC	- XX	- 01	- DR	- AR	- 000101