


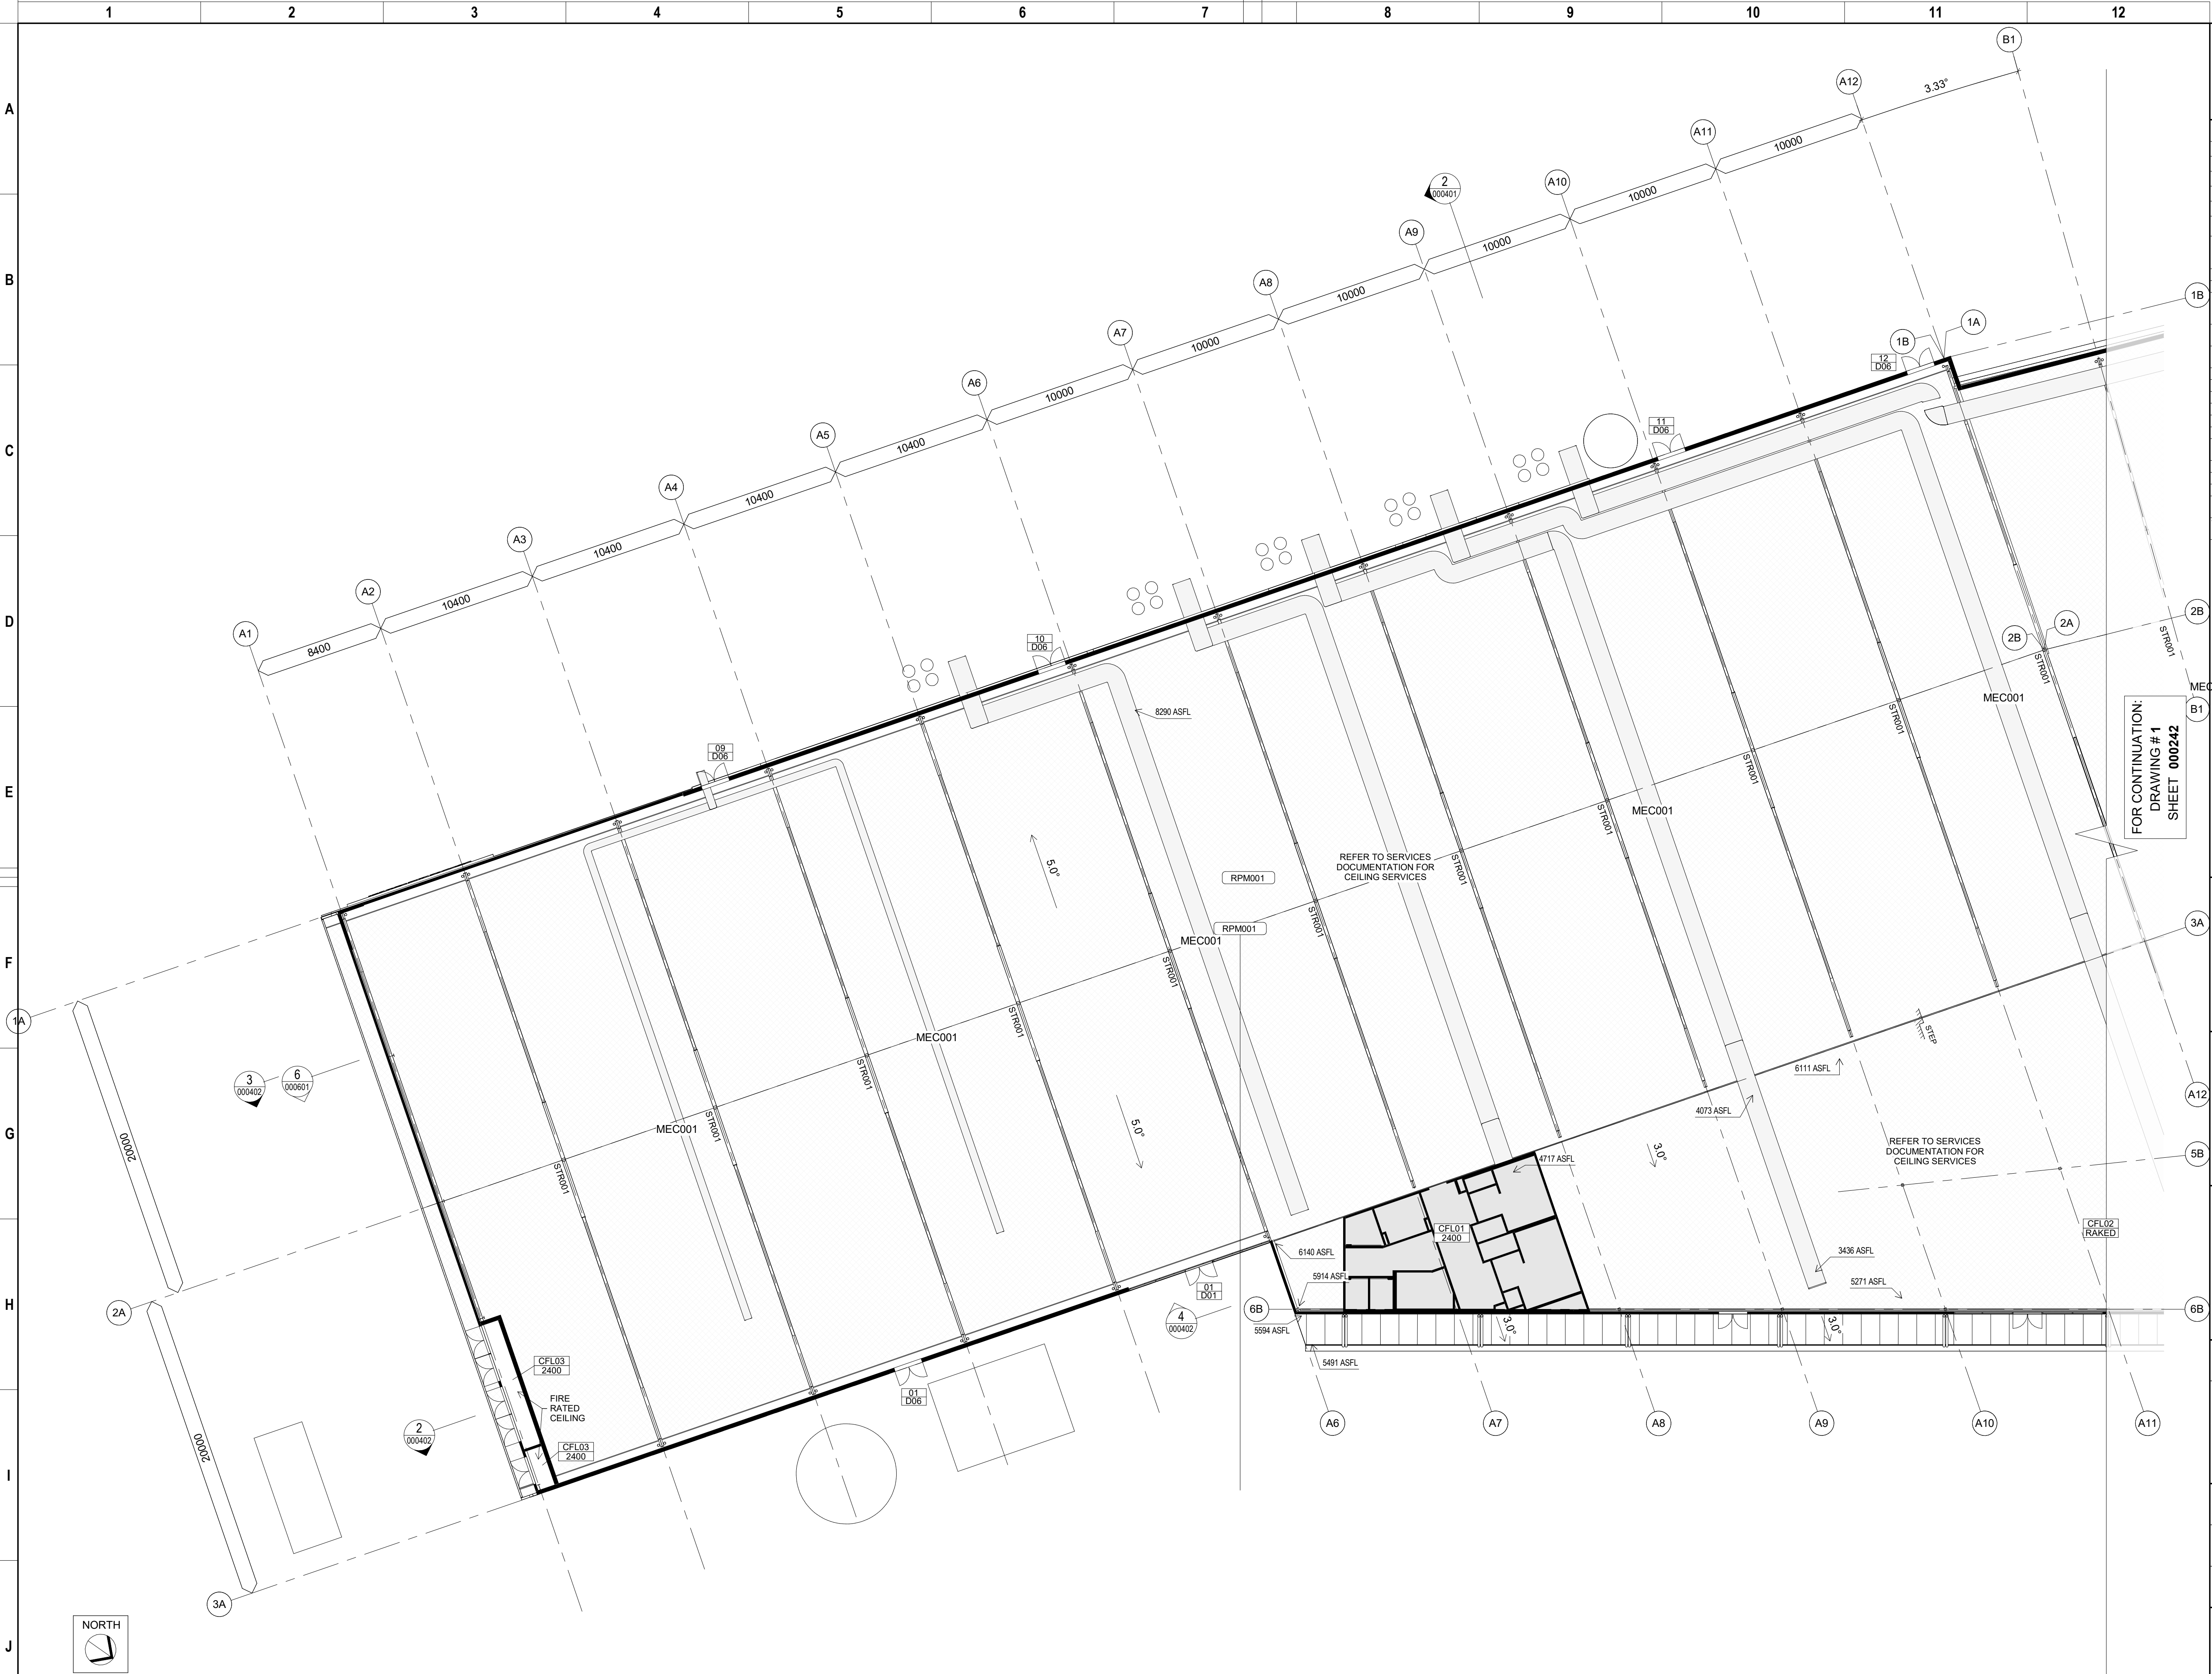

COPYRIGHT :
REPRODUCTION OF WHOLE OR PART OF THIS DOCUMENT
CONSTITUTES AN INFRINGEMENT OF COPYRIGHT. THE
INFORMATION, IDEAS AND CONCEPTS CONTAINED IN THIS
DOCUMENT ARE CONFIDENTIAL. THE RECIPIENT(S) OF
THIS DOCUMENT IS PROHIBITED FROM DISCLOSING SUCH
INFORMATION IDEAS AND CONCEPTS TO ANY PERSON
WITHOUT THE PRIOR WRITTEN CONSENT OF THE
BRISBANE AIRPORT CORPORATION PTY. LTD.

DRN	AMENDMENTS	DATE	REV
JB	FOR COORDINATION	04.12.2025	1
JB	60% DD ISSUE 1	18.12.2025	2
DC	FOR COORDINATION	21.01.2026	3
JB	FOR COORDINATION	29.01.2026	4
JB	60% DD ISSUE 2	05.02.2026	5

TAG LEGEND	
CFL01	CEILING - PLASTERBOARD
CFL03	CEILING - FIRE RATED
CLD004	INSULATED PANEL CLADDING - KINGSPAN KS1000RW WALL PANEL OR SIMILAR - REFER TO SECTION J REPORT
CLD005	DANPALON SINGLE GLAZED TRANSLUCENT CLADDING
COL	STRUCTURAL COLUMN - REFER STRUCTURAL ENGINEER
CT1	CURTAIN TRACK
DP	DOWNPIPE
GT01	COLORBOND FOLDED STEEL GUTTER
GT02	KINGSPAN MEMBRANE LINED INSULATED GUTTER
M-TIL2	WET AREA - WALL TILE
MCT1	PRIVACY CURTAIN
MEC001	MECHANICAL DUCT - REFER MECHANICAL ENGINEER
MLV001	MECHANICAL EXHAUST LOUVRE
RPM001	INSULATED ROOF PANEL
RSS001	ROOF SAFETY SYSTEM
STR001	STRUCTURAL COLUMN - REFER STRUCTURAL ENGINEER
W.01	POWDERCOATED ALUMINIUM FRAMED COMMERCIAL GLAZING

Archipelago

Archipelago
Level 3, 109 George Street, Brisbane QLD 4000
T +617 3238 4800 www.archipelago.com.au
© ARCHIPELAGO ARCHITECTS PTY LTD. All Rights Reserved
This work is copyright and cannot be reproduced or copied by any means without written
permission of Archipelago Architects Pty Ltd. Any
license, express or implied, to use this document for any purpose
whatsoever is restricted to the terms of the agreement between Archipelago Architects Pt
y Ltd and the instructing party.

SKYGATE PLAY

REFLECTED CEILING PLAN - PART A

Drawn JB	Checked DC
Design Coordinated	Compliance Checked
Authorised For Issue	Construction Checked

Brisbane Airport Corporation Pty Ltd
11 The Circuit Brisbane Airport QLD 4008
PO Box 61 Hamilton QLD 4007 Australia
Telephone : 61 7 3406 3000
Facsimile : 61 7 3406 3111
Email : info@bne.com.au
www.brisbaneairport.com.au
ABN 54 076 870 650

Scale
1 : 200
Size
A1
Revision
5

Project No.	Originator	Volume	Level	Type	Discipline	Number
25021	ARC	XX	01	DR	AR	000241

Plot Date & Time: 5/02/2026 10:13:35 AM