

A

B

C

D

E


F

G


H

I


J

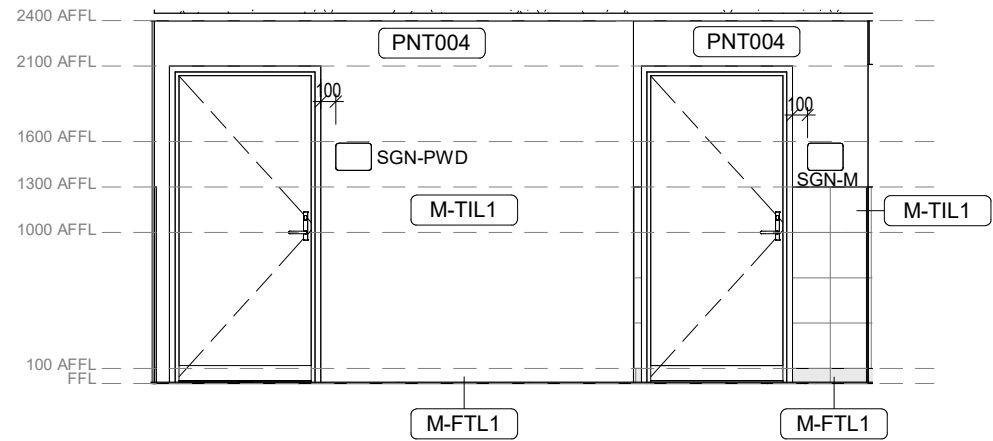


1 Game Over - Amenities - Corridor - Elevation 1
1:50

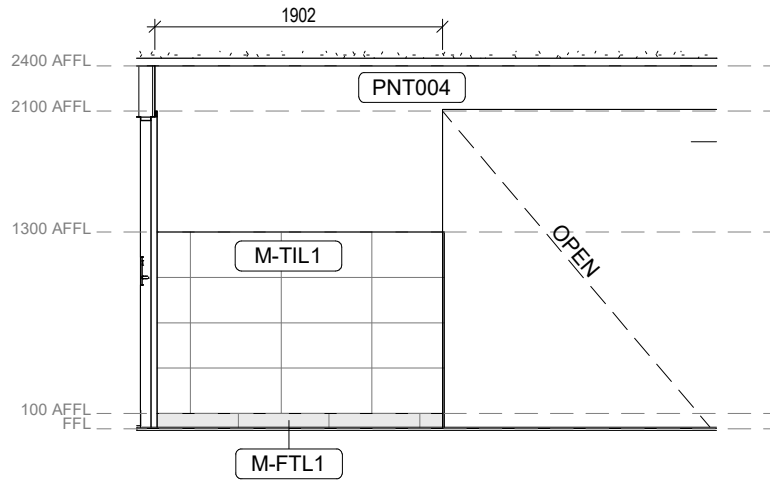


2 Game Over - Amenities - Corridor - Elevation 2
1:50

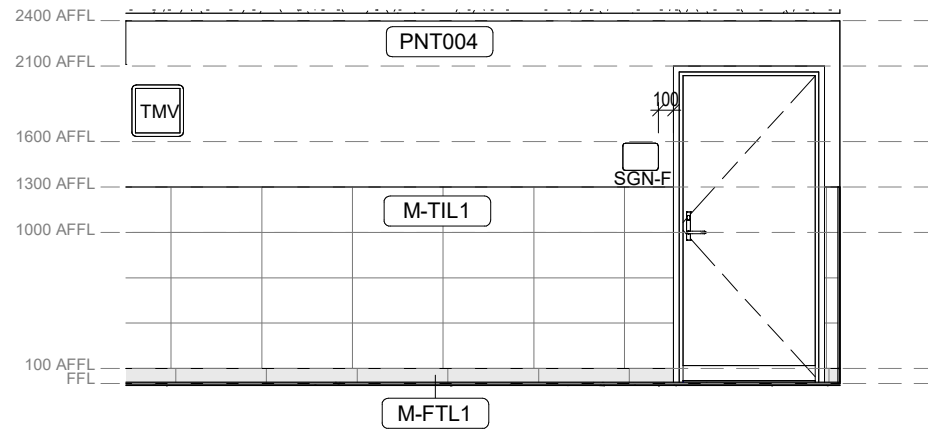


3 Game Over - Amenities - Corridor - Elevation 3
1:50

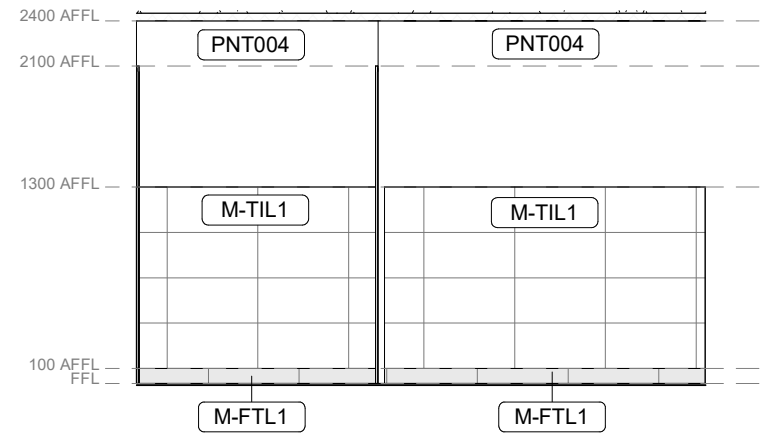


4 Game Over - Amenities - Corridor - Elevation 4
1:50

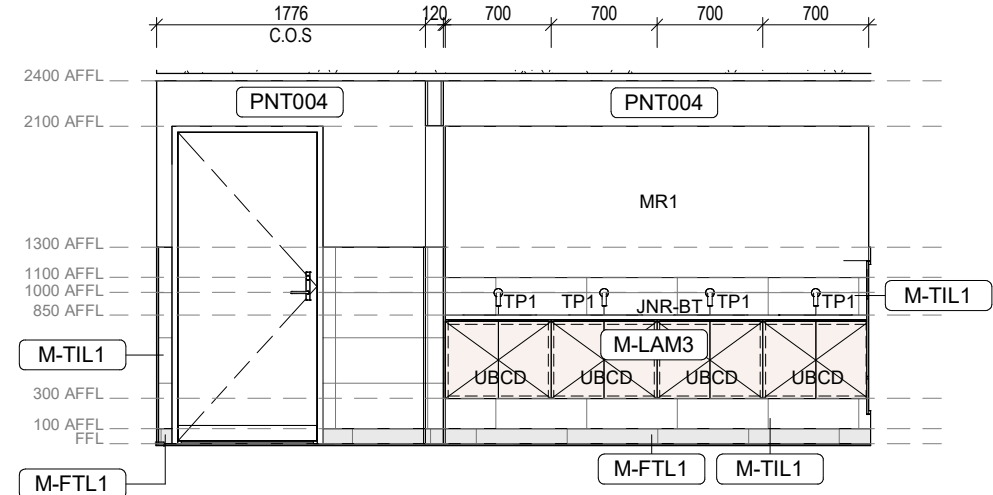


5 Game Over - Amenities - Female - Elevation 1
1:50

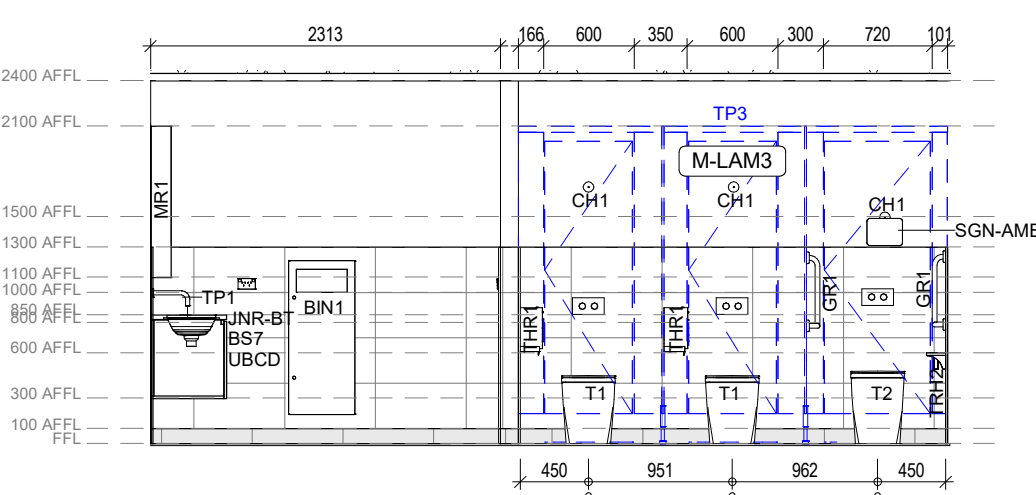


6 Game Over - Amenities - Female - Elevation 2
1:50

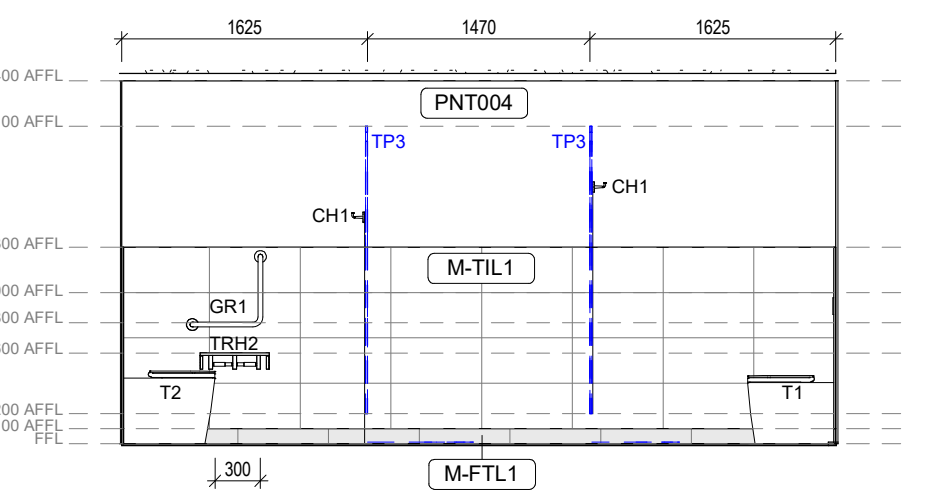


7 Game Over - Amenities - Female - Elevation 3
1:50

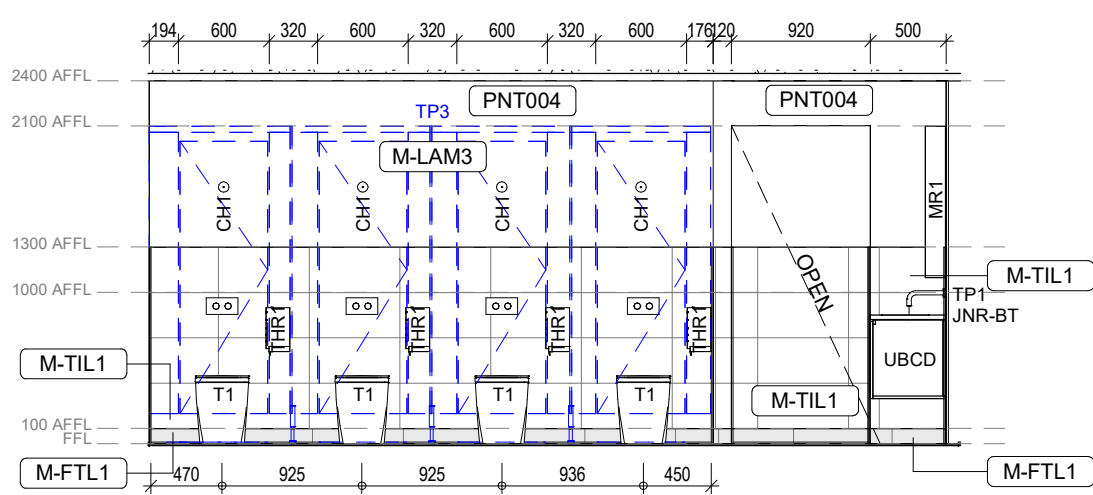


8 Game Over - Amenities - Female - Elevation 4
1:50

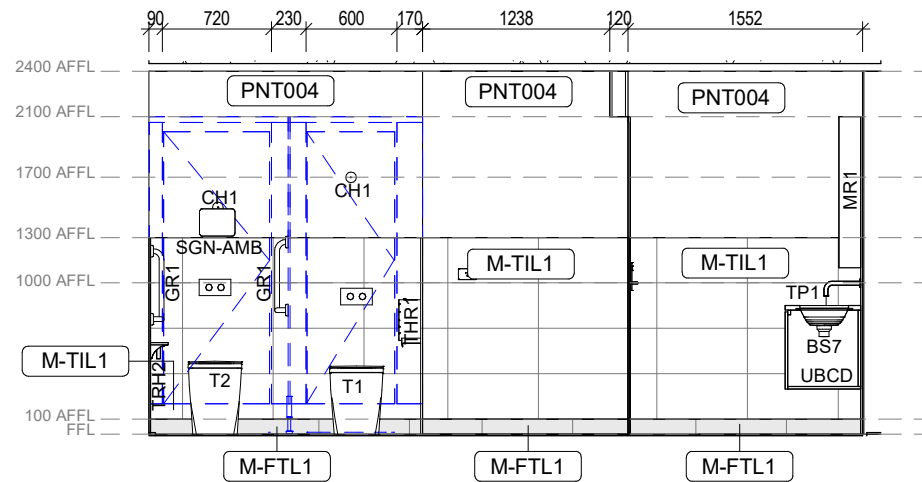


9 Game Over - Amenities - Male - Elevation 1
1:50

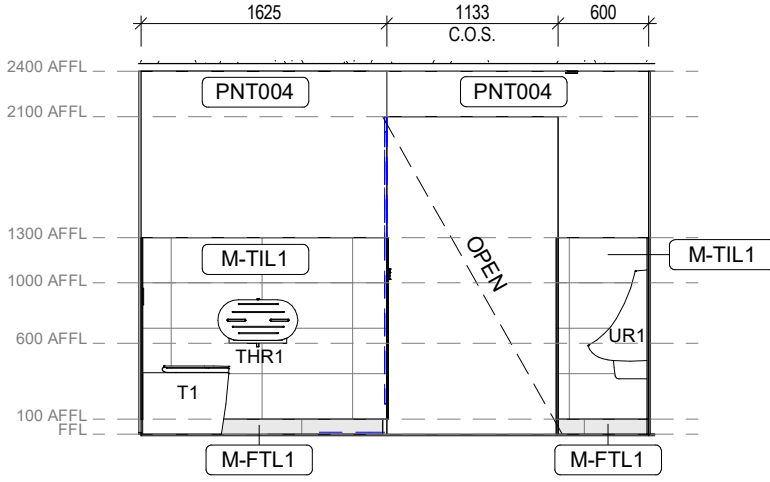


10 Game Over - Amenities - Male - Elevation 2
1:50

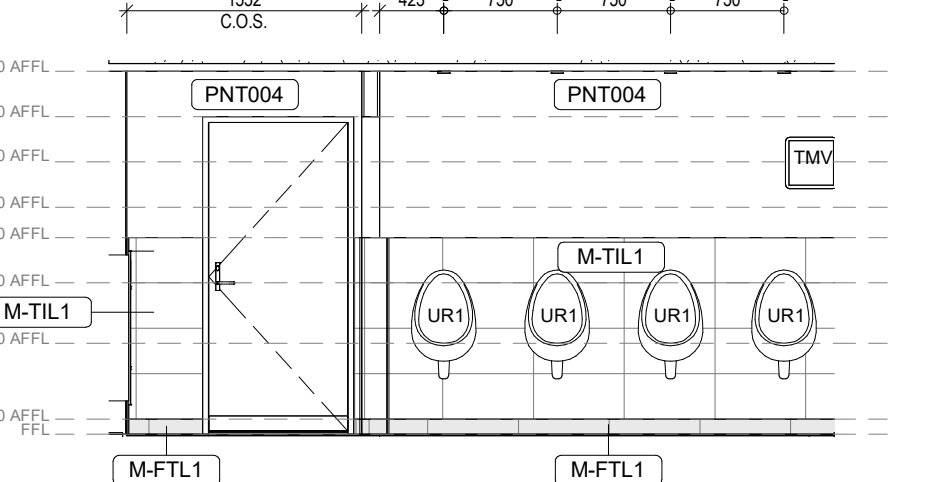


11 Game Over - Amenities - Male - Elevation 3
1:50

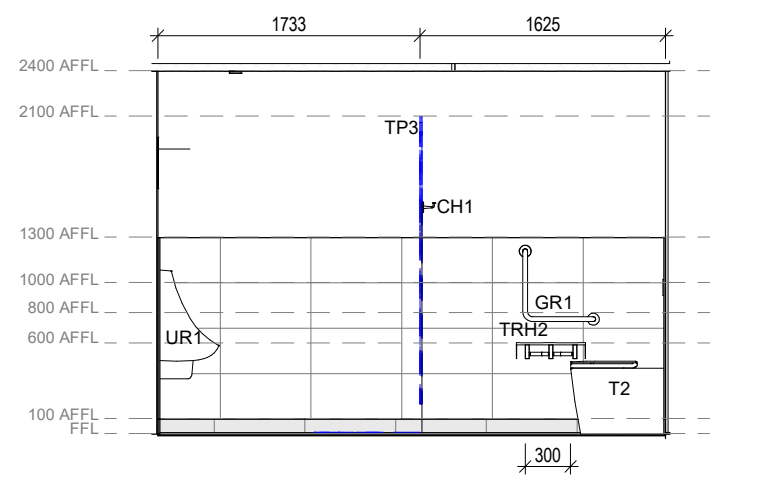


12 Game Over - Amenities - Male - Elevation 4
1:50

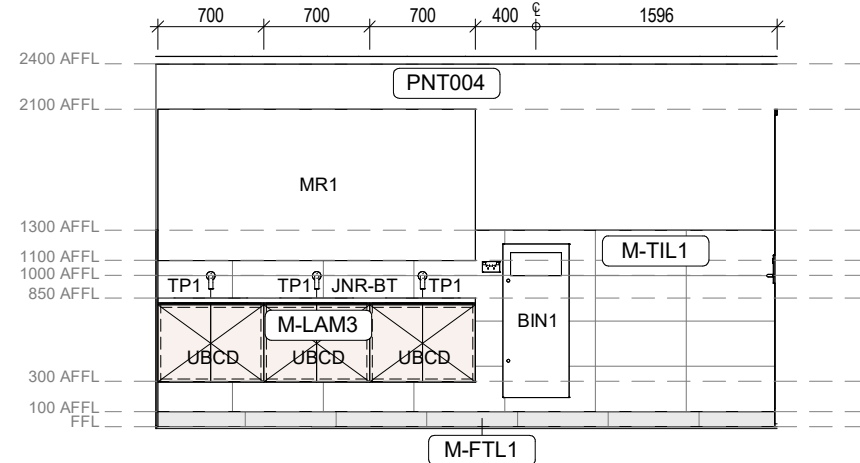


13 Game Over - Amenities - Male - Elevation 5
1:50

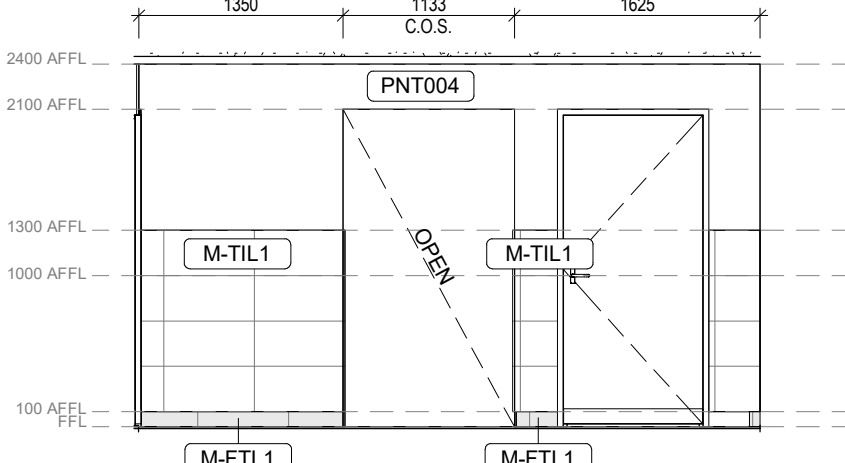


14 Game Over - Amenities - Male - Elevation 6
1:50

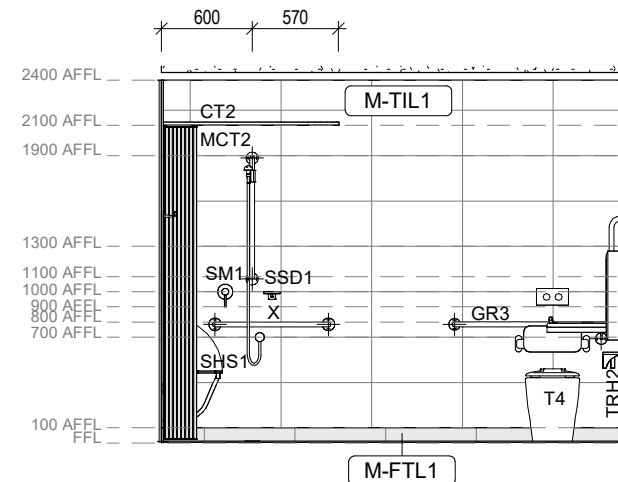


15 Game Over - Amenities - PWD - Elevation 1
1:50

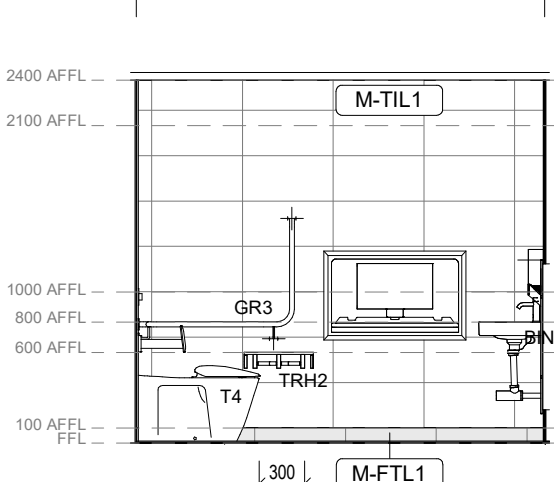

16 Game Over - Amenities - PWD - Elevation 2
1:50

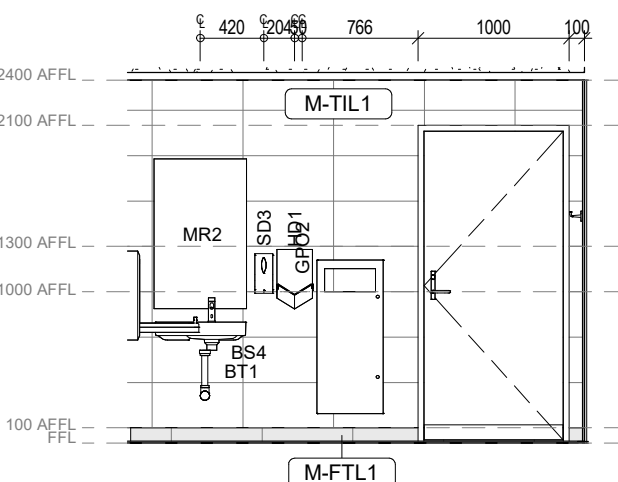

17 Game Over - Amenities - PWD - Elevation 3
1:50

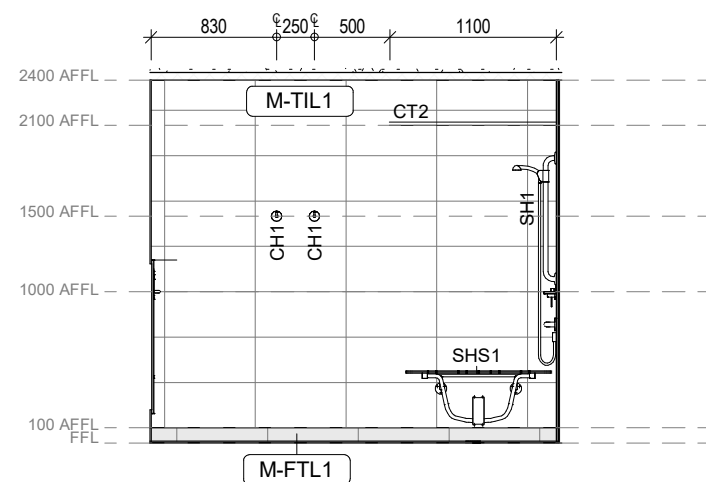

18 Game Over - Amenities - PWD - Elevation 4
1:50

COPYRIGHT :
REPRODUCTION OF WHOLE OR PART OF THIS DOCUMENT
CONSTITUTES AN INFRINGEMENT OF COPYRIGHT. THE
INFORMATION, IDEAS AND CONCEPTS CONTAINED IN THIS
DOCUMENT ARE CONFIDENTIAL. THE RECIPIENT(S) OF
THIS DOCUMENT IS PROHIBITED FROM DISCLOSING SUCH
INFORMATION IDEAS AND CONCEPTS TO ANY PERSON
WITHOUT THE PRIOR WRITTEN CONSENT OF THE
BRISBANE AIRPORT CORPORATION PTY. LTD.

DRN	AMENDMENTS	DATE	REV
JB	60% DD ISSUE 2	05.02.2026	1

Archipelago

Archipelago
Level 3, 109 George Street, Brisbane QLD 4000
T +617 3236 4806 www.archipelago.com.au
© ARCHIPELAGO ARCHITECTS PTY. LTD. All Rights Reserved
This work is copyright and cannot be reproduced or copied by any means without written
permission of Archipelago Architects Pty Ltd. Any
license, express or implied, to use this document for any purpose
whatsoever is restricted to the terms of the agreement between Archipelago Architects Pt
y Ltd and the instructing party.

SKYGATE PLAY

WET AREA INTERNAL ELEVATIONS - GAME
OVER

Drawn Author	Checked Checker
Design Coordinated	Compliance Checked
Authorised For Issue	Construction Checked

Brisbane Airport	Brisbane Airport Corporation Pty Ltd 11 The Circuit Brisbane Airport QLD 4008 PO Box 61 Hamilton QLD 4007 Australia Telephone : 61 7 3406 3000 Facsimile : 61 7 3406 3111 Email : info@bne.com.au www.brisbaneairport.com.au ABN 54 076 870 650	Scale 1 : 50 Size A1 Revision 1
	Project No. Originator Volume Level Type Discipline Number	25021 - - - - - 000811