


D01 - DOUBLE GLAZED DOOR


| TYPE     | NUMBER | ROOM NAME | LEAF THICKNESS | LEAF A WIDTH | LEAF B WIDTH | LEAF HEIGHT | PANEL TYPE                   | PANEL FINISH | JAMB TYPE | JAMB FINISH | AUTOMATIC DOOR | VISION PANEL | HINGES | LOCK TYPE                  | CARD READER | DOOR CLOSER | KICK PLATE | DOOR SEALS | SIGNAGE   | THRESHOLD |
|----------|--------|-----------|----------------|--------------|--------------|-------------|------------------------------|--------------|-----------|-------------|----------------|--------------|--------|----------------------------|-------------|-------------|------------|------------|-----------|-----------|
| D01      | 01     | AREA 51   | 40             | 920          | 920          | 2340        | EXTERNAL - GLAZED SWING DOOR | GLZ001       | ALUMINIUM | PDC         | NO             | Yes          |        | FREE HANDLE EGRESS/KEYLOCK | NO          | YES         | No         | WEATHER    | STATUTORY | KILARGO   |
| D01      | 02     | AREA 51   | 40             | 920          | 920          | 2340        | EXTERNAL - GLAZED SWING DOOR | GLZ001       | ALUMINIUM | PDC         | NO             | Yes          |        | FREE HANDLE EGRESS/KEYLOCK | NO          | YES         | No         | WEATHER    | STATUTORY | KILARGO   |
| D01      | 03     |           | 40             | 920          | 920          | 2340        | EXTERNAL - GLAZED SWING DOOR | GLZ001       | ALUMINIUM | PDC         | NO             | Yes          |        | FREE HANDLE EGRESS/KEYLOCK | NO          | YES         | No         | WEATHER    | STATUTORY | KILARGO   |
| D01      | 04     |           | 40             | 920          | 920          | 2340        | EXTERNAL - GLAZED SWING DOOR | GLZ001       | ALUMINIUM | PDC         | NO             | Yes          |        | FREE HANDLE EGRESS/KEYLOCK | NO          | YES         | No         | WEATHER    | STATUTORY | KILARGO   |
| D01      | 05     |           | 40             | 920          | 920          | 2340        | EXTERNAL - GLAZED SWING DOOR | GLZ001       | ALUMINIUM | PDC         | NO             | Yes          |        | FREE HANDLE EGRESS/KEYLOCK | NO          | YES         | No         | WEATHER    | STATUTORY | KILARGO   |
| D01      | 06     |           | 40             | 920          | 920          | 2340        | EXTERNAL - GLAZED SWING DOOR | GLZ001       | ALUMINIUM | PDC         | NO             | Yes          |        | FREE HANDLE EGRESS/KEYLOCK | NO          | YES         | No         | WEATHER    | STATUTORY | KILARGO   |
| TOTAL: 6 |        |           

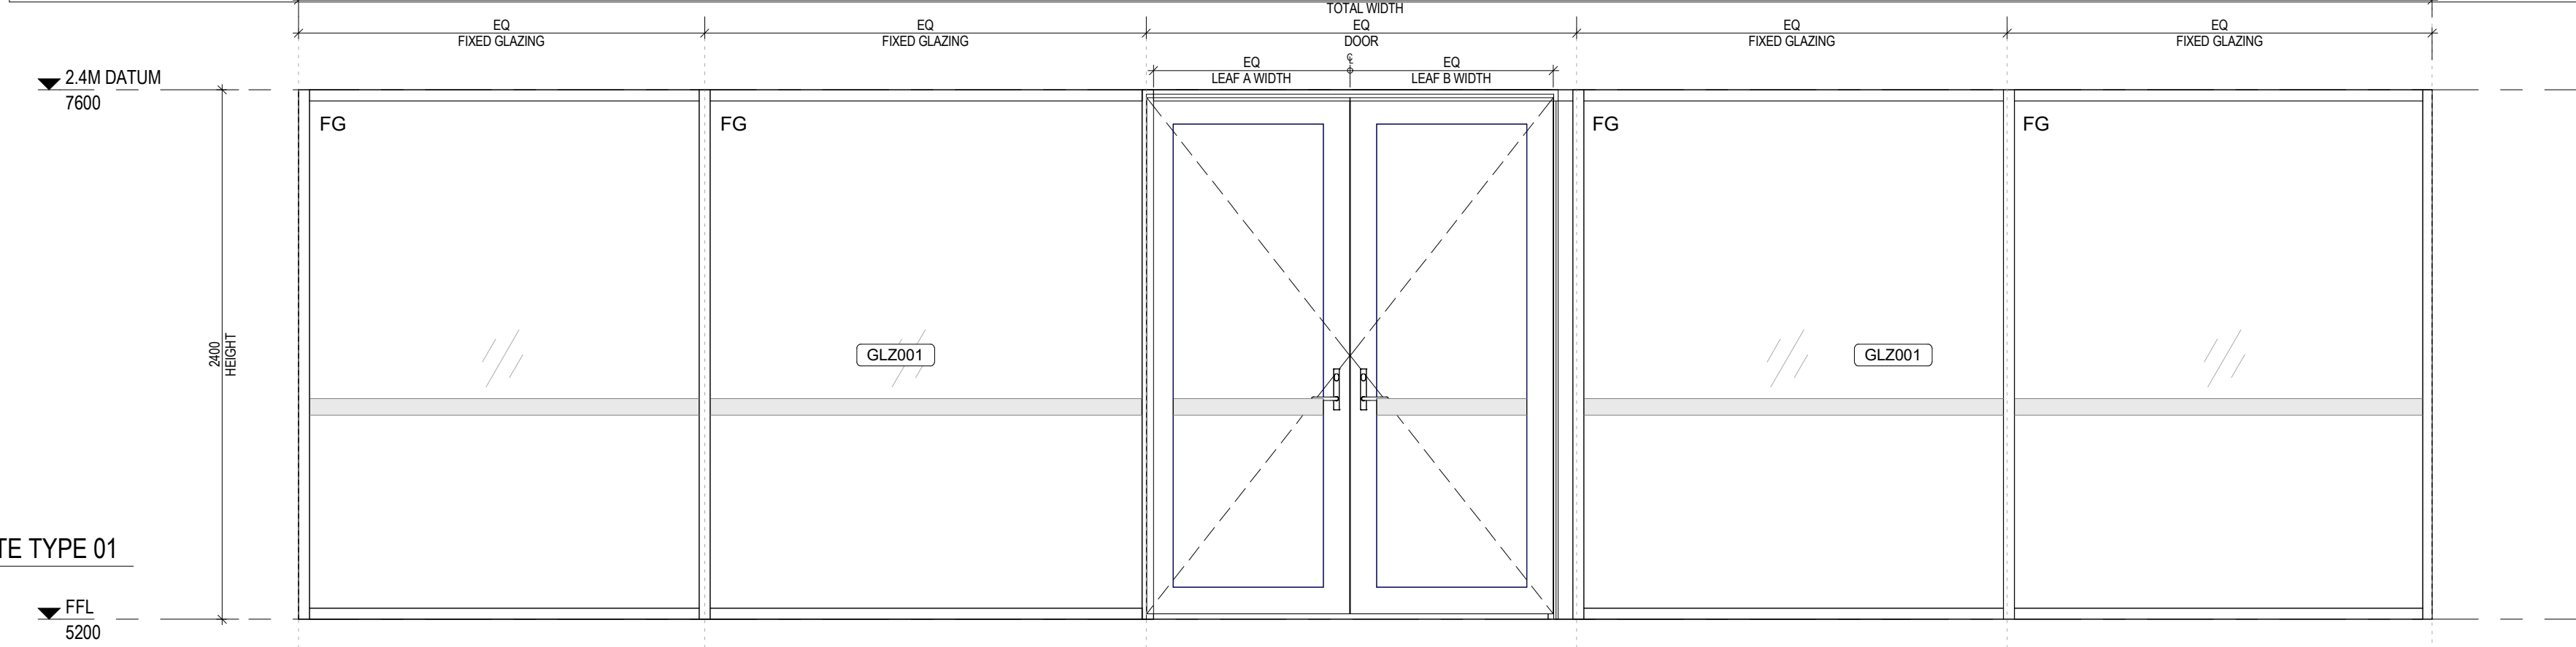

D01 - GLAZING SUITE TYPE 01  
1:25

D02 - DOUBLE GLAZED DOOR


| TYPE     | NUMBER | ROOM NAME | LEAF THICKNESS | LEAF A WIDTH | LEAF B WIDTH | LEAF HEIGHT | PANEL TYPE                   | PANEL FINISH | JAMB TYPE | JAMB FINISH | AUTOMATIC DOOR | VISION PANEL | HINGES | LOCK TYPE                  | CARD READER | DOOR CLOSER | KICK PLATE | DOOR SEALS | SIGNAGE   | THRESHOLD |
|----------|--------|-----------|----------------|--------------|--------------|-------------|------------------------------|--------------|-----------|-------------|----------------|--------------|--------|----------------------------|-------------|-------------|------------|------------|-----------|-----------|
| D02      | 01     | AREA 51   | 40             | 920          | 920          | 2340        | EXTERNAL - GLAZED SWING DOOR | GLZ001       | ALUMINIUM | PDC         | NO             | Yes          |        | FREE HANDLE EGRESS/KEYLOCK | NO          | YES         | No         | WEATHER    | STATUTORY | KILARGO   |
| D02      | 02     | AREA 51   | 40             | 920          | 920          | 2340        | EXTERNAL - GLAZED SWING DOOR | GLZ001       | ALUMINIUM | PDC         | NO             | Yes          |        | FREE HANDLE EGRESS/KEYLOCK | NO          | YES         | No         | WEATHER    | STATUTORY | KILARGO   |
| TOTAL: 2 |        |           

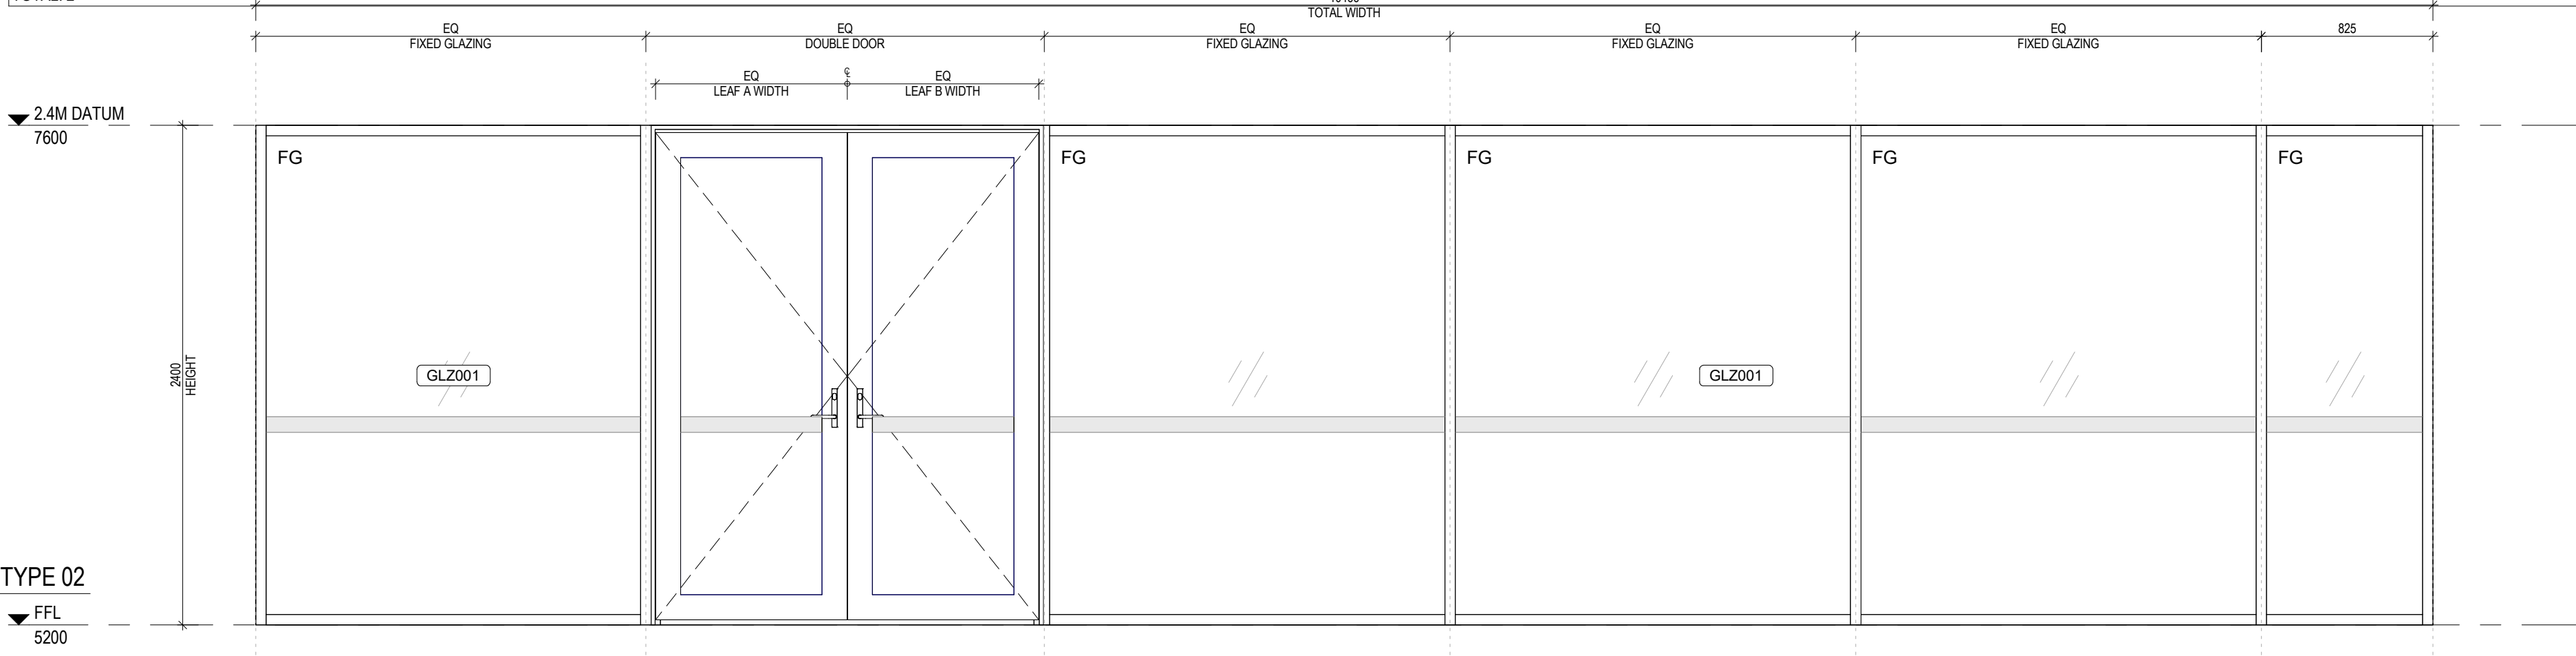

D02 - GLAZING SUITE TYPE 02  
1:25

D03 - SLIDING GLAZED DOOR


| TYPE     | NUMBER | ROOM NAME | TOTAL WIDTH | TOTAL HEIGHT | LEAF THICKNESS | PANEL TYPE                     | PANEL FINISH | JAMB TYPE | JAMB FINISH | AUTOMATIC DOOR | LOCK TYPE | CARD READER | DOOR CLOSER | KICK PLATE | DOOR SEALS | SIGNAGE | THRESHOLD |
|----------|--------|-----------|-------------|--------------|----------------|--------------------------------|--------------|-----------|-------------|----------------|-----------|-------------|-------------|------------|------------|---------|-----------|
| D03      | 01     |           | 4800        | 2400         |                | EXTERNAL - SLIDING GLAZED DOOR | GLZ001       | ALUMINIUM | PDC         | YES            | AUTO DOOR | NO          | AUTO        |            | WEATHER    |         | FLW003    |
| D03      | 02     |           | 4800        | 2400         |                | EXTERNAL - SLIDING GLAZED DOOR | GLZ001       | ALUMINIUM | PDC         | YES            | AUTO DOOR | NO          | AUTO        |            | WEATHER    |         | FLW003    |
| TOTAL: 2 |        |           |             |              |                |                                |              |           |             |                |           |             |             |            |            |         |           |

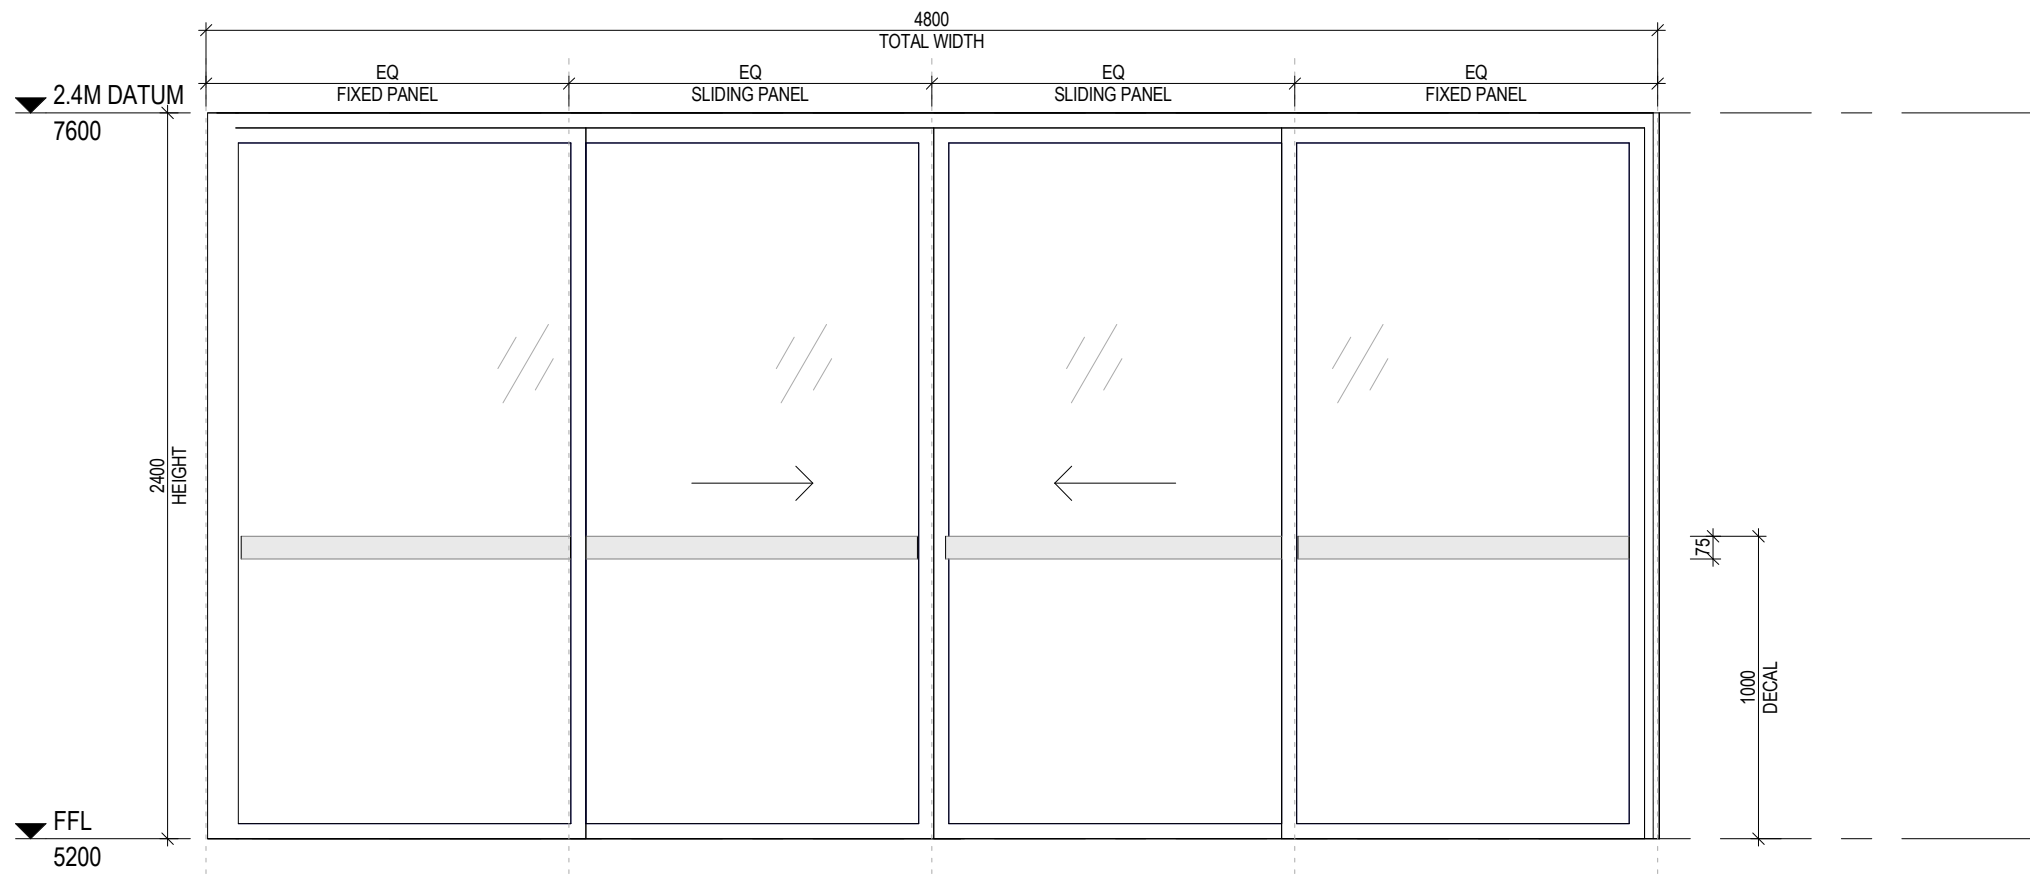

D03 - SLIDING GLAZED AUTO DOOR  
1:25

D09 - BIFOLD DOOR

| TYPE     | NUMBER | ROOM NAME | OVERALL WIDTH | LEAF THICKNESS | PANEL TYPE | PANEL FINISH | JAMB TYPE | JAMB FINISH | HINGES | LOCK TYPE | DOOR SEALS | SIGNAGE | THRESHOLD |
|----------|--------|-----------|---------------|----------------|------------|--------------|-----------|-------------|--------|-----------|------------|---------|-----------|
| D09      | 01     |           | 4575          |                |            |              |           |             |        |           |            |         |           |
| D09      | 02     |           | 4600          |                |            |              |           |             |        |           |            |         |           |
| TOTAL: 2 |        |           |               |                |            |              |           |             |        |           |            |         |           |

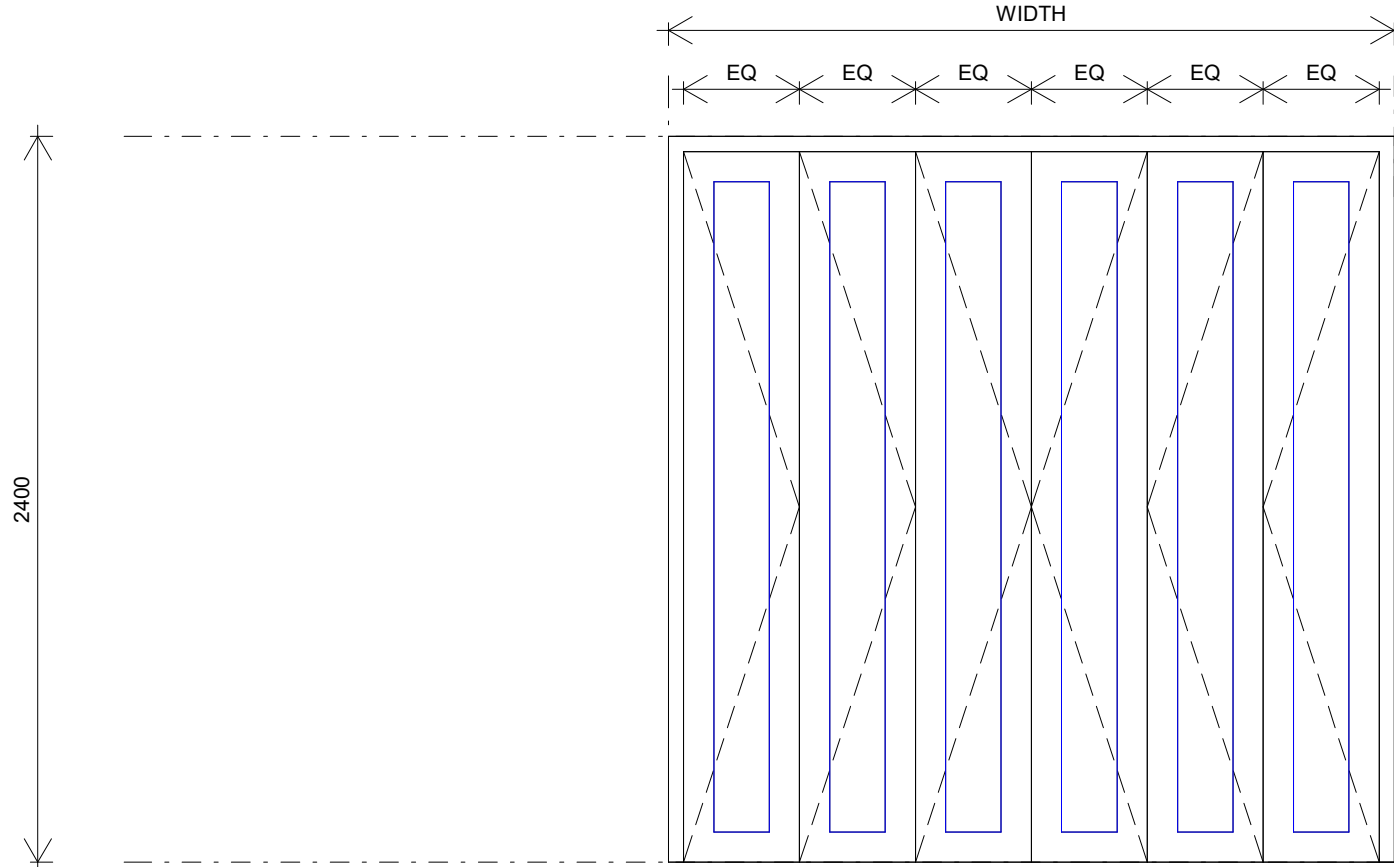

D09 - GLAZED BIFOLD DOOR  
1:25

NOTE: DOOR AND WINDOW  
SCHEDULE STILL UNDER  
DEVELOPMENT

COPYRIGHT :  
REPRODUCTION OF WHOLE OR PART OF THIS DOCUMENT  
CONSTITUTES AN INFRINGEMENT OF COPYRIGHT. THE  
INFORMATION, IDEAS AND CONCEPTS CONTAINED IN THIS  
DOCUMENT ARE CONFIDENTIAL. THE RECIPIENT(S) OF  
THIS DOCUMENT IS PROHIBITED FROM DISCLOSING SUCH  
INFORMATION IDEAS AND CONCEPTS TO ANY PERSON  
WITHOUT THE PRIOR WRITTEN CONSENT OF THE  
BRISBANE AIRPORT CORPORATION PTY. LTD.

| DRN | AMENDMENTS     | DATE       | REV |
|-----|----------------|------------|-----|
| JB  | 60% DD ISSUE 1 | 18.12.2025 | 1   |
| JB  | 60% DD ISSUE 2 | 05.02.2026 | 2   |

LEGEND

Archipelago

Archipelago  
Level 3, 109 George Street, Brisbane QLD 4000  
T +617 3236 4606 www.archipelago.com.au  
© ARCHIPELAGO ARCHITECTS PTY. LTD. All Rights Reserved  
This work is copyright and cannot be reproduced or copied by any means without written  
permission of Archipelago Architects Pty Ltd. Any  
license, express or implied, to use this document for any purpose  
whatsoever is restricted to the terms of the agreement between Archipelago Architects Pt  
y Ltd and the instructing party.

SKYGATE PLAY

DOOR SCHEDULE - GLAZING

|                      |                      |
|----------------------|----------------------|
| Drawn<br>JB          | Checked<br>DC        |
| Design Coordinated   | Compliance Checked   |
| Authorised For Issue | Construction Checked |

|   |   |            |        |       |      |            |        |
|---|---|------------|--------|-------|------|------------|--------|
| <br><b>Brisbane<br/>Airport</b> | Brisbane Airport Corporation Pty Ltd<br>11 The Circuit Brisbane Airport QLD 4008<br>PO Box 61 Hamilton QLD 4007 Australia               |            |        |       |      |            | Scale  |
|   | Telephone : 61 7 3406 3000<br>Facsimile : 61 7 3406 3111<br>Email : info@bne.com.au<br>www.brisbaneairport.com.au<br>ABN 54 076 870 650 |            |        |       |      |            | 1 : 25 |
|   |   |            |        |       |      |            | Size   |
|   |   |            |        |       |      |            | A1     |
|   |   |            |        |       |      | Revision   | 2      |
|   | Project No   | Originator | Volume | Level | Type | Discipline | Number |
| Drawing No.   | 25021   | ARC        | XX     | 01    | DR   | AR         | 000950 |