


Sheet size: A1
Drawing to be printed in colour
Drawing © Northrop Consulting Engineers Pty Ltd.

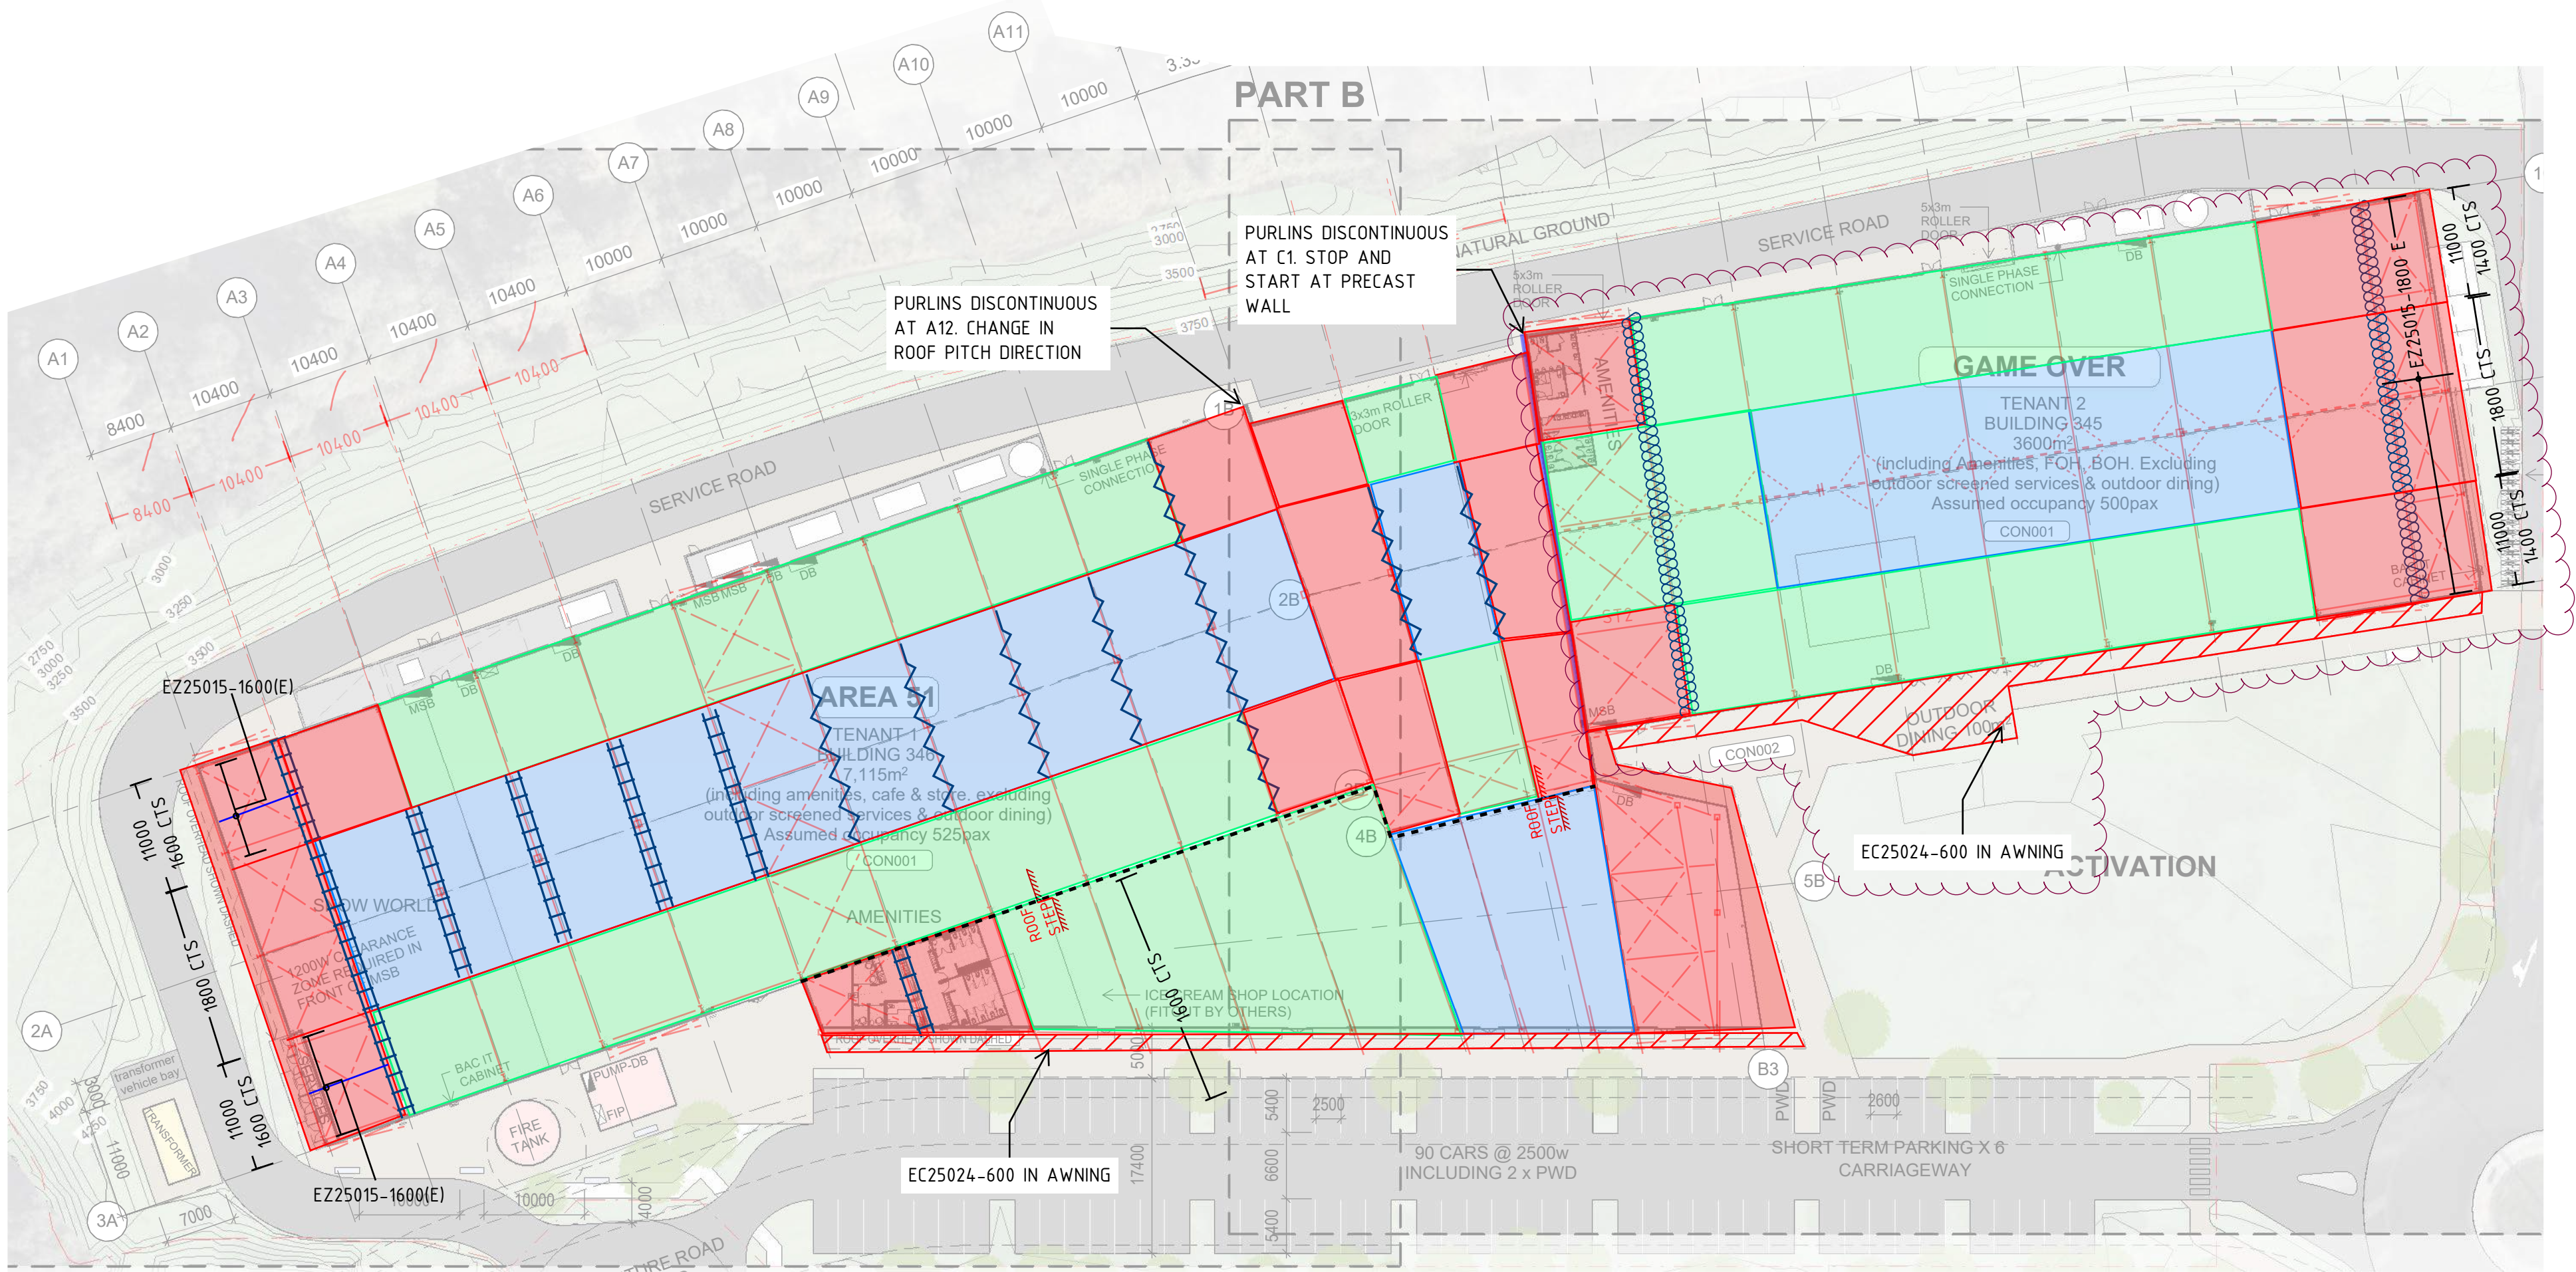

PURLIN PLAN

EZ25015

EZ25019

EZ25024

20% LAP

25% LAP

30% LAP

ALLOW 15% LAPS UNO

ALLOW FOR 3 ROWS OF BRIDGING TYP.

PURLINS TO BE STRAMMIT EXACTA

Legend to denote extra purlin required between regular centres

EZ250XX (E) IN GAPS

size of extras

NOT FOR CONSTRUCTION

NORTHROP

BRISBANE
Level 25, 12 Creek Street
Brisbane City, QLD 4000
brisbane@northrop.com.au
(07) 3365 0400

PARTNERS



Brisbane Airport Corporation Pty Ltd
11 The Circuit Brisbane Airport QLD 4008
PO Box 61 Hamilton QLD 4207 Australia
Telephone : 61 7 3406 3000
Facsimile : 61 7 3406 3111
Email : info@bae.com.au
www.brisbaneairport.com.au
ABN 54 076 870 650

Archipelago

DRAWN

Author

DESIGNED

Designer

1:100

0

0

1:100

Scale at A1

Refer to architect's drawings for setout

JOB MANAGER

Checker

VERIFIER

Approver

REV. DESCRIPTION

A FOR INFORMATION

B FOR INFORMATION

C FOR INFORMATION

D FOR TENDER

ISSUED

NS

JS

NS

NS

04/02/26

DATE

29/08/25

21/11/25

19/12/25

PROJECT

BAC BNE SKYGATE PLAY

ADDRESS

DRAWING TITLE

**PORTAL FRAME ELEVATIONS
SHEET 3**

25021-NRP-XX-01-DR-ST-000009

JOB No.

250946

DRAWING No.

REV.

D