



BARRIER KERB - TYPE B2

EXPANSION JOINTS @ MAX 12m CTRS / TOOL JOINTS @ MAX 3m CTRS
ALL RADII TO BE 20mm U.N.O.

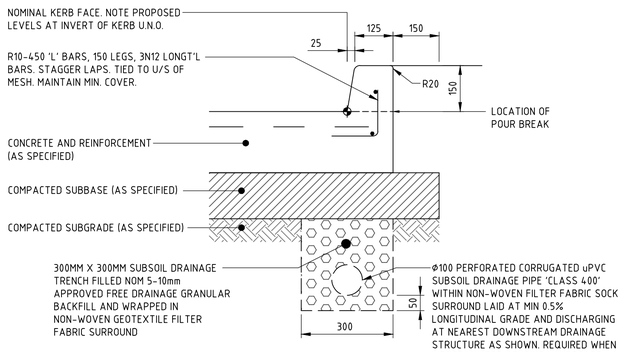


INTEGRAL KERB 'IK'

PROVIDE TOOL JOINTS @ MAX 3m CENTRES AND TO MATCH SAWN AND DOWELED JOINTS. DISCONTINUE LONGT'L REINF'T AT ALL JOINTS. ALL RADIUS' TO BE 20mm UNLESS NOTED OTHERWISE

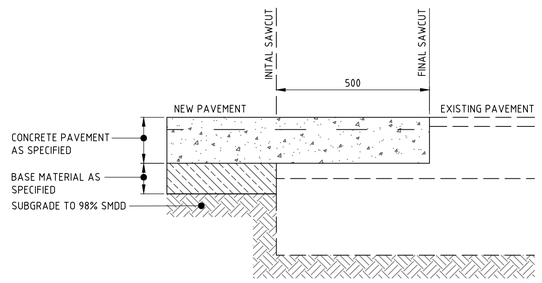


NEW CONCRETE TO NEW ASPHALT PAVEMENT JUNCTION DETAIL 'INT'

NOTES:
- MATCH ASPHALT SMOOTHLY WITH EXISTING
- FINAL SAWCUT TO BE UNDERTAKEN AT A TIME TO ENSURE MINIMAL DAMAGE / CHIPPING OCCURS TO EDGE OF EXISTING

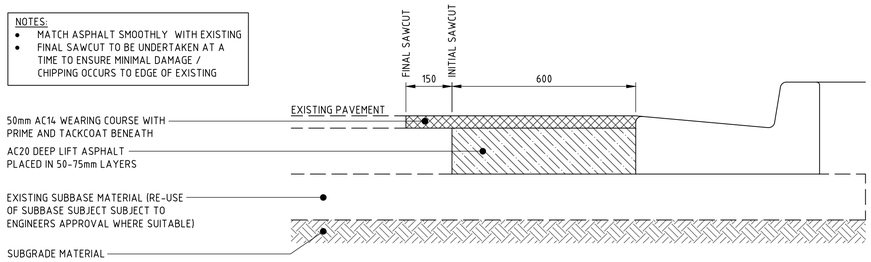


PAVEMENT INTERFACE 'INT1'

MIN CBR ___% (CONTRACTOR TO CONFIRM ONSITE)

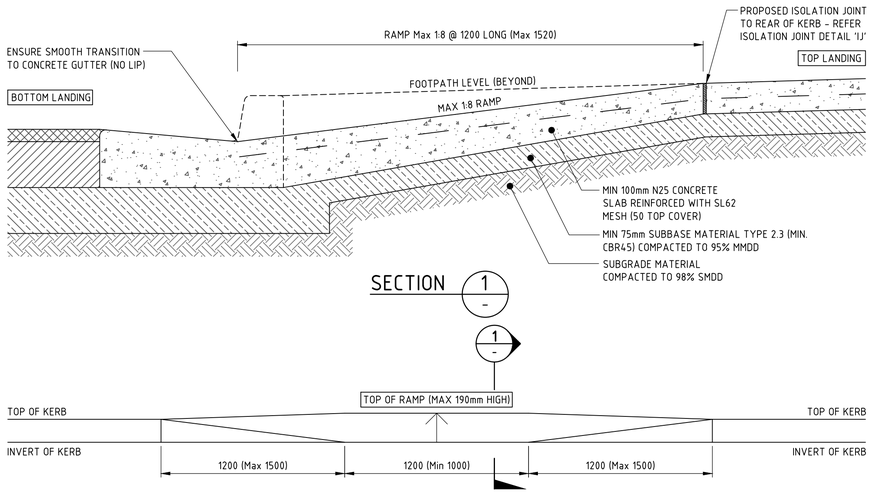


ELEVATION

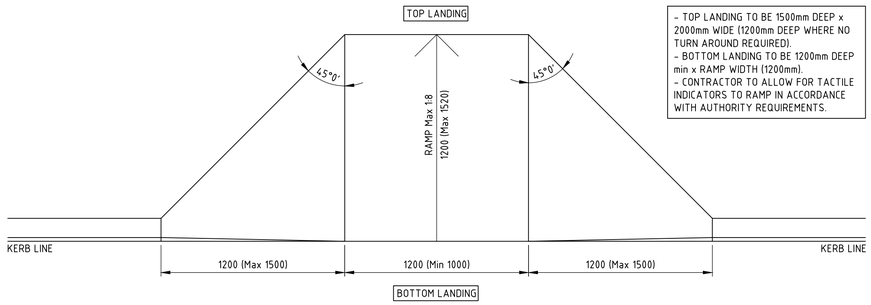

- TOP LANDING TO BE 1500mm DEEP x 2000mm WIDE (1200mm DEEP WHERE NO TURN AROUND REQUIRED).
- BOTTOM LANDING TO BE 1200mm DEEP min x RAMP WIDTH (1200mm).
- CONTRACTOR TO ALLOW FOR TACTILE INDICATORS TO RAMP IN ACCORDANCE WITH AUTHORITY REQUIREMENTS.


PLAN
KERB RAMP 'KR'

'KR' DENOTES 1.2m WIDE KERB RAMP AT PEDESTRIAN CROSSING AND SIGNALS
'KR1' DENOTES 2.0m WIDE KERB RAMP AT PEDESTRIAN CROSSING AND SIGNALS
'KR2' DENOTES 3.2m WIDE KERB RAMP AT PEDESTRIAN CROSSING AND SIGNALS

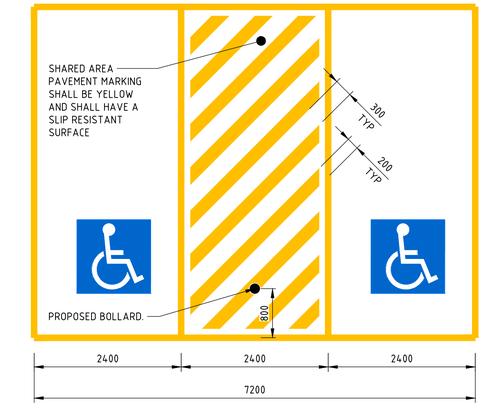


DISABLED SHARED AREA

SCALE 1:50

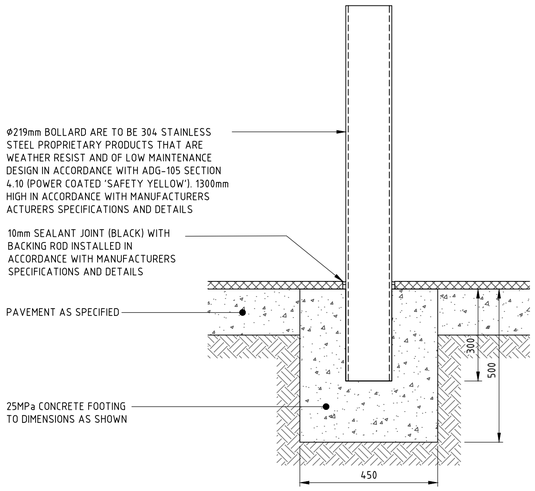

BOLLARD 'B'

PROVIDE 600mm CLEARANCE TO FACE OF KERB / TRAVEL LANE

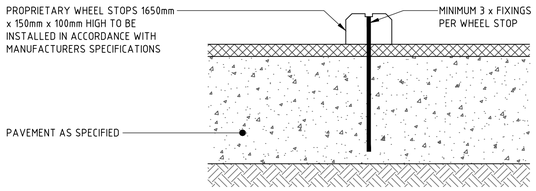

WHEEL STOP 'WS'

WHEEL STOPS TO BE INSTALLED IN ACCORDANCE WITH AUSTRALIAN STANDARDS AS2890.1

NOT FOR CONSTRUCTION

SCALE 1:50@ A1 0.0 0.5 1.0 1.5 2.0 2.5m

COPYRIGHT :
REPRODUCTION OF WHOLE OR PART OF THIS DOCUMENT CONSTITUTES AN INFRINGEMENT OF COPYRIGHT. THE INFORMATION, IDEAS AND CONCEPTS CONTAINED IN THIS DOCUMENT ARE CONFIDENTIAL. THE RECIPIENT(S) OF THIS DOCUMENT IS PROHIBITED FROM DISCLOSING SUCH INFORMATION IDEAS AND CONCEPTS TO ANY PERSON WITHOUT THE PRIOR WRITTEN CONSENT OF THE BRISBANE AIRPORT CORPORATION PTY. LTD.

JD	PRELIMINARY DESIGN 30%	01.09.25	A
JD	ISSUED FOR TENDER	23.12.25	B
JD	ISSUED FOR TENDER	28.01.26	C
LQ	ISSUED FOR TENDER	30.01.26	D
MM	ISSUED FOR APPROVAL	11.06.26	E
DRN	AMENDMENTS	DATE	REV

XENIA

NORTHROP
Brisbane
The Annex, Level 8, 12 Creek Street, Brisbane QLD 4000
GPO BOX 423 Brisbane QLD 4001
(07) 3365 0400 brisbane@northrop.com.au
ABN 81 094 433 100

Drawn M.MANLAPIT 11.06.26	Checked A.TATHAM 11.06.26
Design Coordinated R.MITCHELL 11.06.26	Compliance Checked S.KILLORAN 11.06.26
Authorised For Issue S.KILLORAN 11.06.26	Construction Checked N/A

SKYGATE PLAY
BRISBANE AIRPORT

TYPICAL SECTION AND DETAILS

Brisbane Airport
BRISBANE AIRPORT CORPORATION PTY LTD
11 THE CIRCUIT, BRISBANE AIRPORT QLD 4008
PO BOX 61, HAMILTON CENTRAL QLD 4007 AUSTRALIA
T +61734063200
E INFO@BNE.COM.AU
W BNE.COM.AU

Scale	Size	Revision
AS ABOVE	A1	E

Drawing Number	Project No.	Originator	Volume	Level	Type	Discipline	Number
	25021	NRP	XX	XX	DR	CI	000220

File: 250946-C-000220-Typical Xsec & Details.dwg
C:\12dS\data\NorthropSYN\250946 - BNE PLAY Skygate_572\CAD\4-DD
Pentable: ----
Printer: AUTOCAD PDF (GENERAL DOCUMENTATION)
User: Mark Manlapit
Plot Date & Time: 6/11/2026 8:38:40 AM