


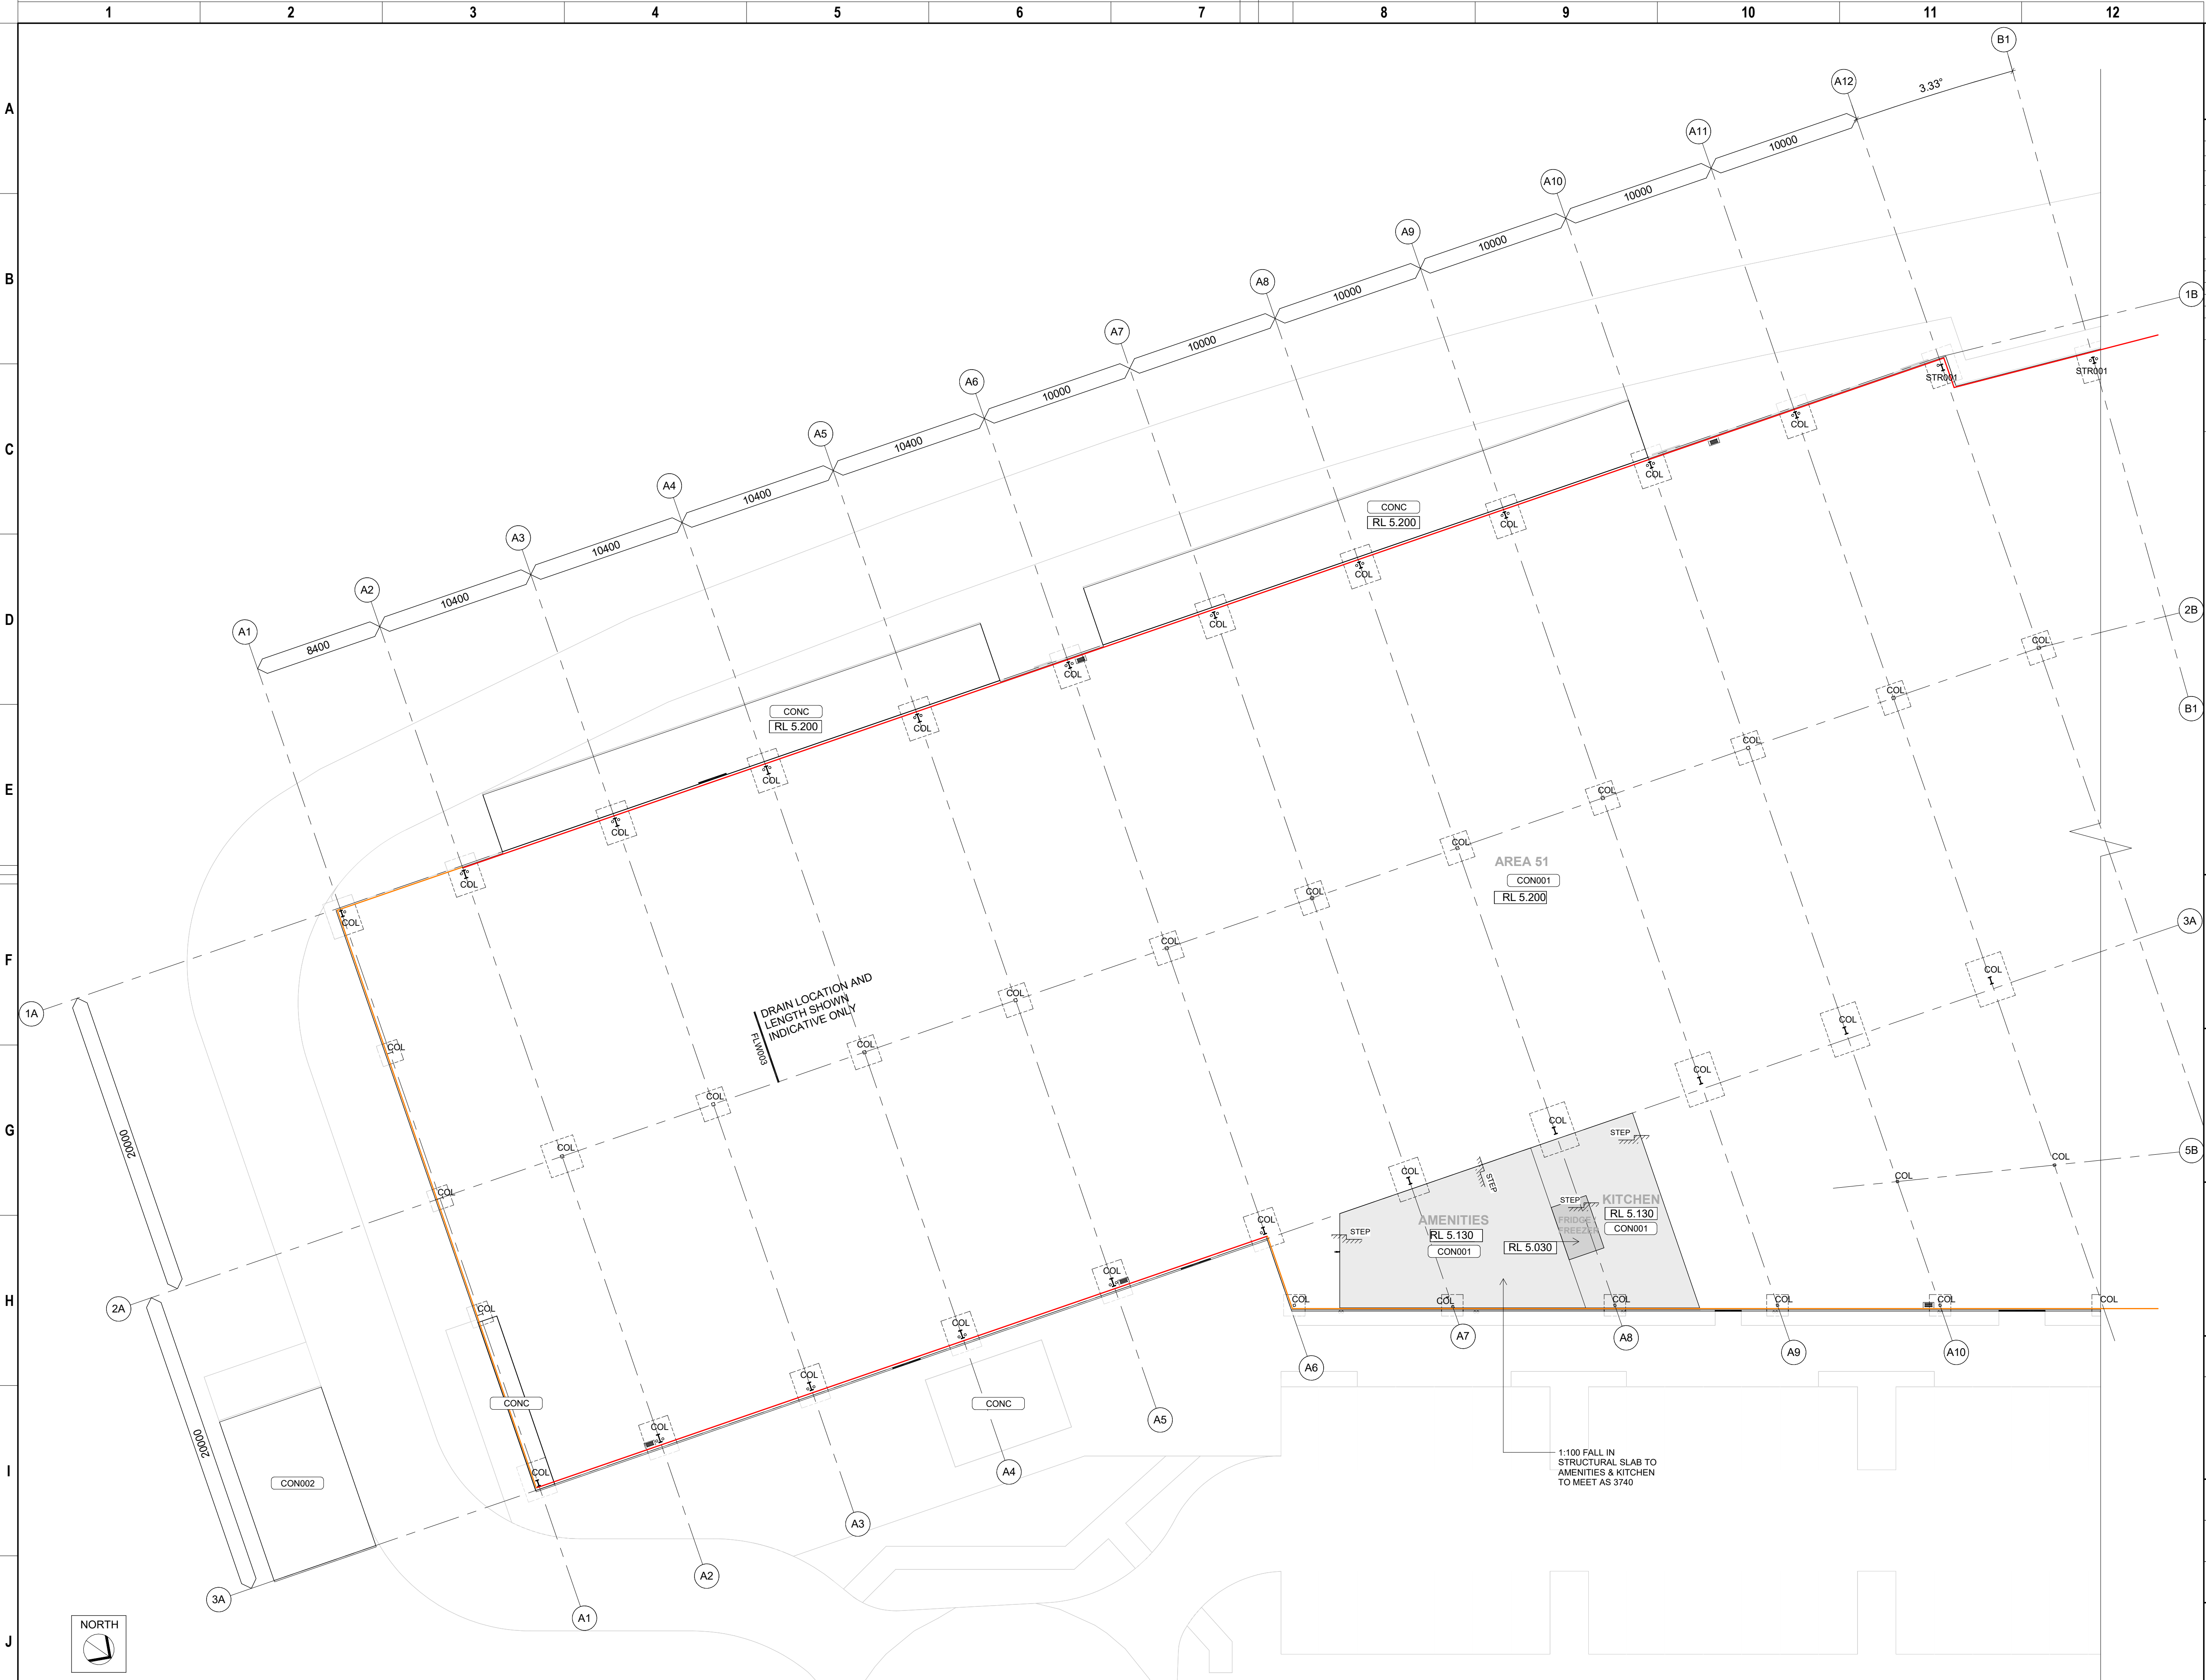

COPYRIGHT :
REPRODUCTION OF WHOLE OR PART OF THIS DOCUMENT
CONSTITUTES AN INFRINGEMENT OF COPYRIGHT. THE
INFORMATION, IDEAS AND CONCEPTS CONTAINED IN THIS
DOCUMENT ARE CONFIDENTIAL. THE RECIPIENT(S) OF
THIS DOCUMENT IS PROHIBITED FROM DISCLOSING SUCH
INFORMATION IDEAS AND CONCEPTS TO ANY PERSON
WITHOUT THE PRIOR WRITTEN CONSENT OF THE
BRISBANE AIRPORT CORPORATION PTY. LTD.

DRN	AMENDMENTS	DATE	REV
JB	60% DD ISSUE 1	18.12.2025	1
JB	FOR COORDINATION	29.01.2026	2
JB	60% DD ISSUE 2	05.02.2026	3

TAG LEGEND	
COL	STRUCTURAL COLUMN - REFER STRUCTURAL ENGINEER
CON001	CONCRETE SLAB
CON002	CONCRETE SLAB - EXTERNAL HARDSTAND
DP	DOWNPIPE
FHR	FIRE HOSE REEL REFER HYD. ENG.
FLW003	FLOOR DRAIN
STR001	STRUCTURAL COLUMN - REFER STRUCTURAL ENGINEER

SLAB SETOUT LEGEND	
	PENETRATION REFER HYDRAULICS DRAWINGS
	100mm HOB UNO
	70mm WET AREA SETDOWN UNO
	170mm FRIDE / FREEZER SETDOWN UNO
	STRUCTURAL FOOTING BELOW
	90mm WIDE & 25mm DEEP SETDOWN
	150mm WIDE & 25mm DEEP SETDOWN
	STEP
	STEP IN SLAB
	TOW 00.000 TOP OF WALL
	TOH 00.000 TOP OF HOB
	FALL TO SLAB
NOTE:	
FOR STRUCTURAL SLABS AND COLUMNS PLEASE REFER TO STRUCTURAL DRAWINGS	
ALL HYDRAULIC PENETRATION LOCATIONS TO BE SET OUT FROM FIGURED DIMENSIONS. FROM ARCHITECTURAL PLANS	

Archipelago
Archipelago
Level 3, 109 George Street, Brisbane QLD 4000
T +61 7 3238 4800 www.archipelago.com.au
© ARCHIPELAGO ARCHITECTS PTY LTD. All Rights Reserved
This work is copyright and cannot be reproduced or copied by any means without written permission of Archipelago Architects Pty Ltd. Any license, express or implied, to use this document for any purpose whatsoever is restricted to the terms of the agreement between Archipelago Architects Pty Ltd and the instructing party.

SKYGATE PLAY

STRUCTURAL SETOUT PLAN - PART A

Drawn JB	Checked DC
Design Coordinated	Compliance Checked
Authorised For Issue	Construction Checked

		Brisbane Airport Corporation Pty Ltd 11 The Circuit Brisbane Airport QLD 4008 PO Box 61 Hamilton QLD 4007 Australia Telephone : 61 7 3406 3000 Facsimile : 61 7 3406 3111 Email : info@bne.com.au www.brisbaneairport.com.au ABN 54 076 870 650	Scale As indicated
Project No.		Volume	Level
Discipline		Type	Number
Drawing No.		25021 - ARC - XX - 01 - DR - AR - 000221	Revision 3