

A

B

C

D

E


F

G


H

I


J

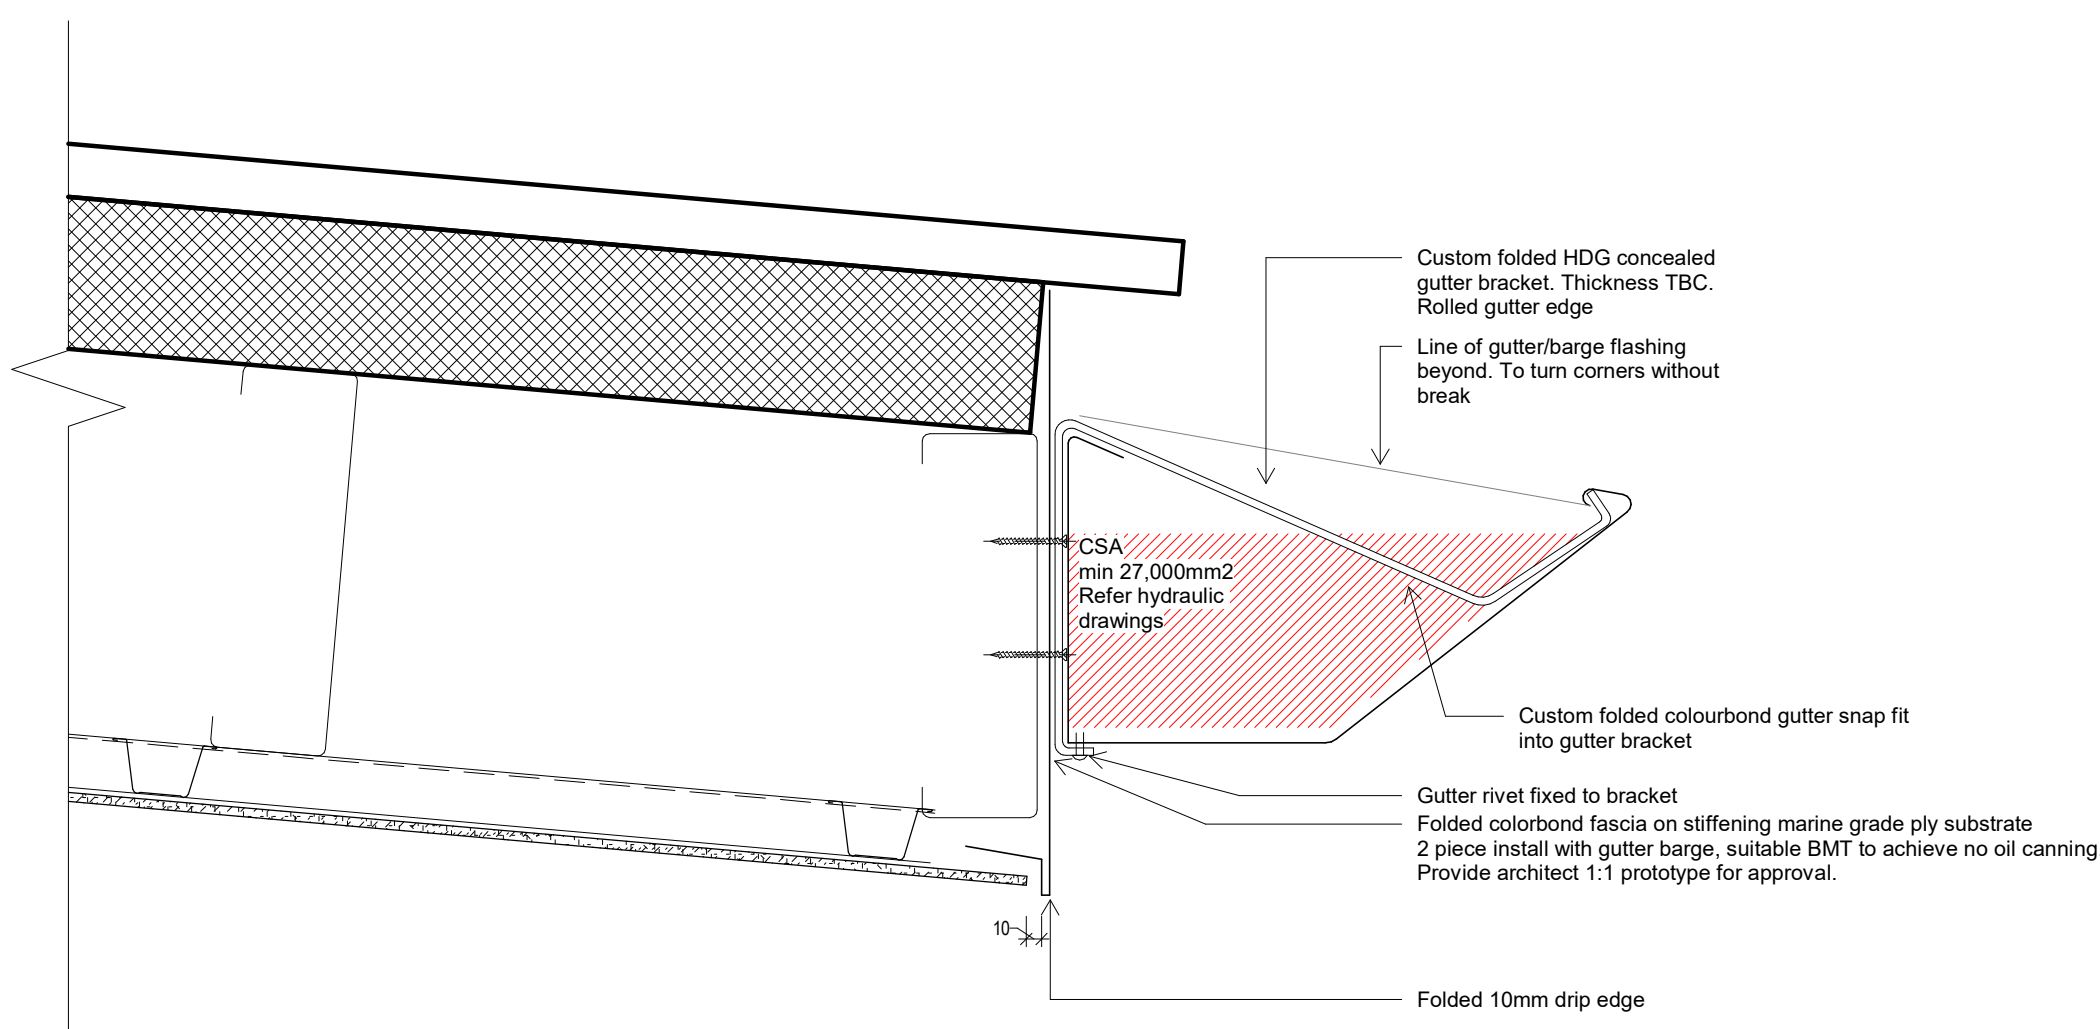


TYPICAL MITRED CORNER

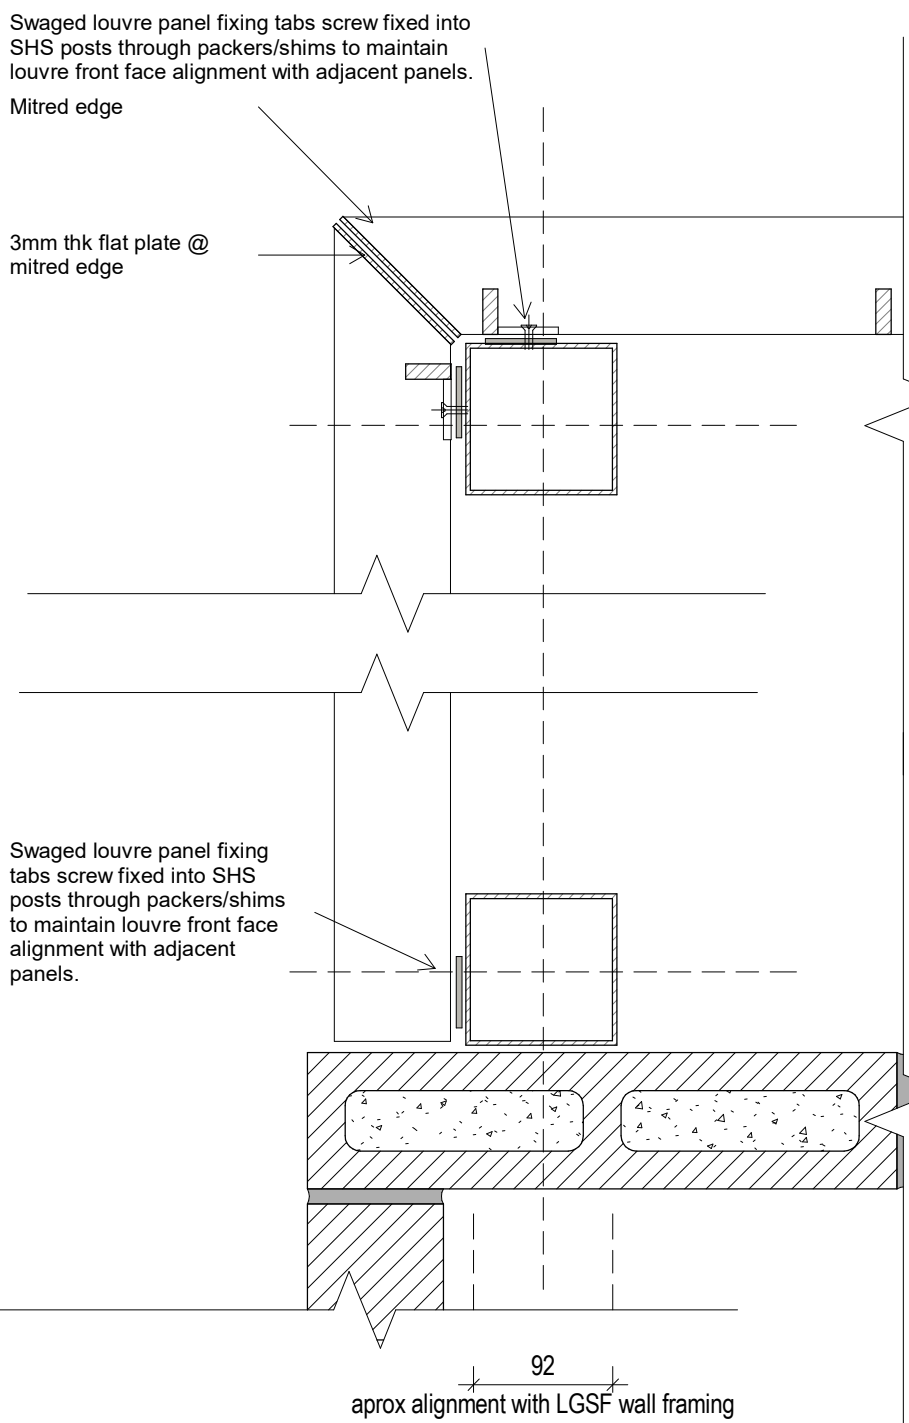

TYPICAL LOUVRED DOOR (HINGE SIDE)

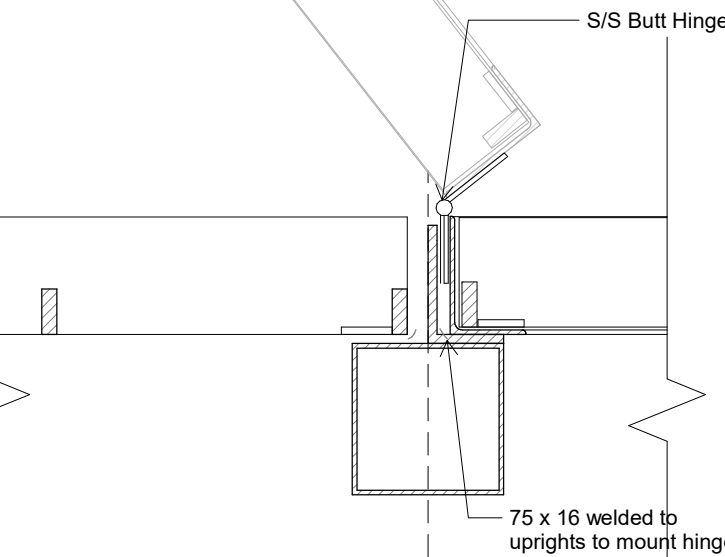


TYPICAL LOUVRED DOOR ('LATCH' SIDE)

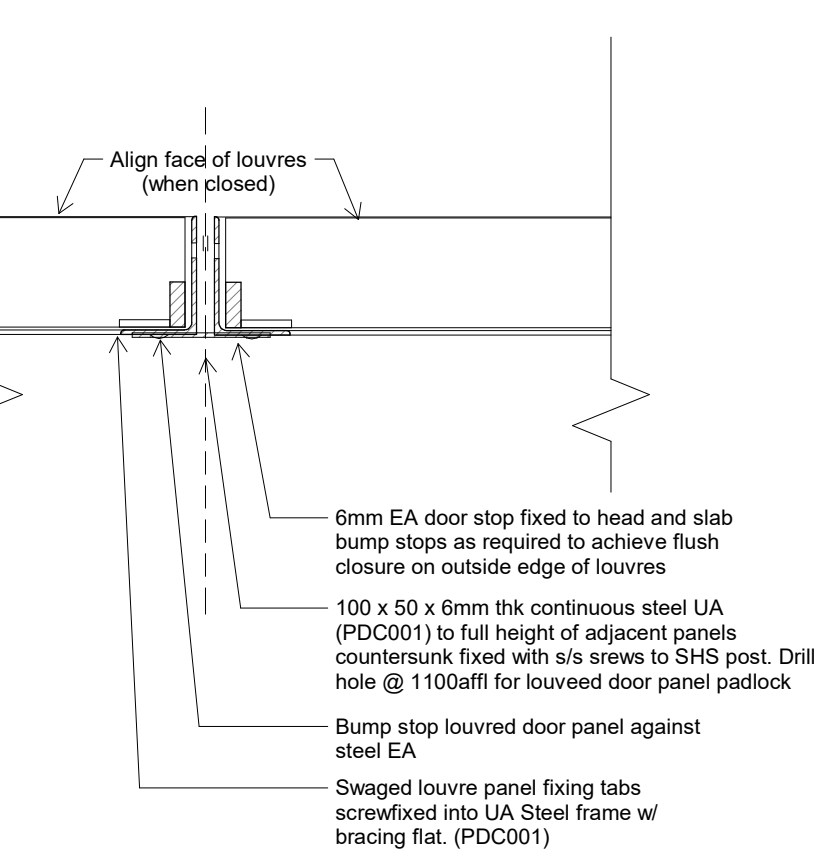

TYPICAL WALL JUNCTION

SCR001 - TYPICAL PLAN DETAILS


1:5

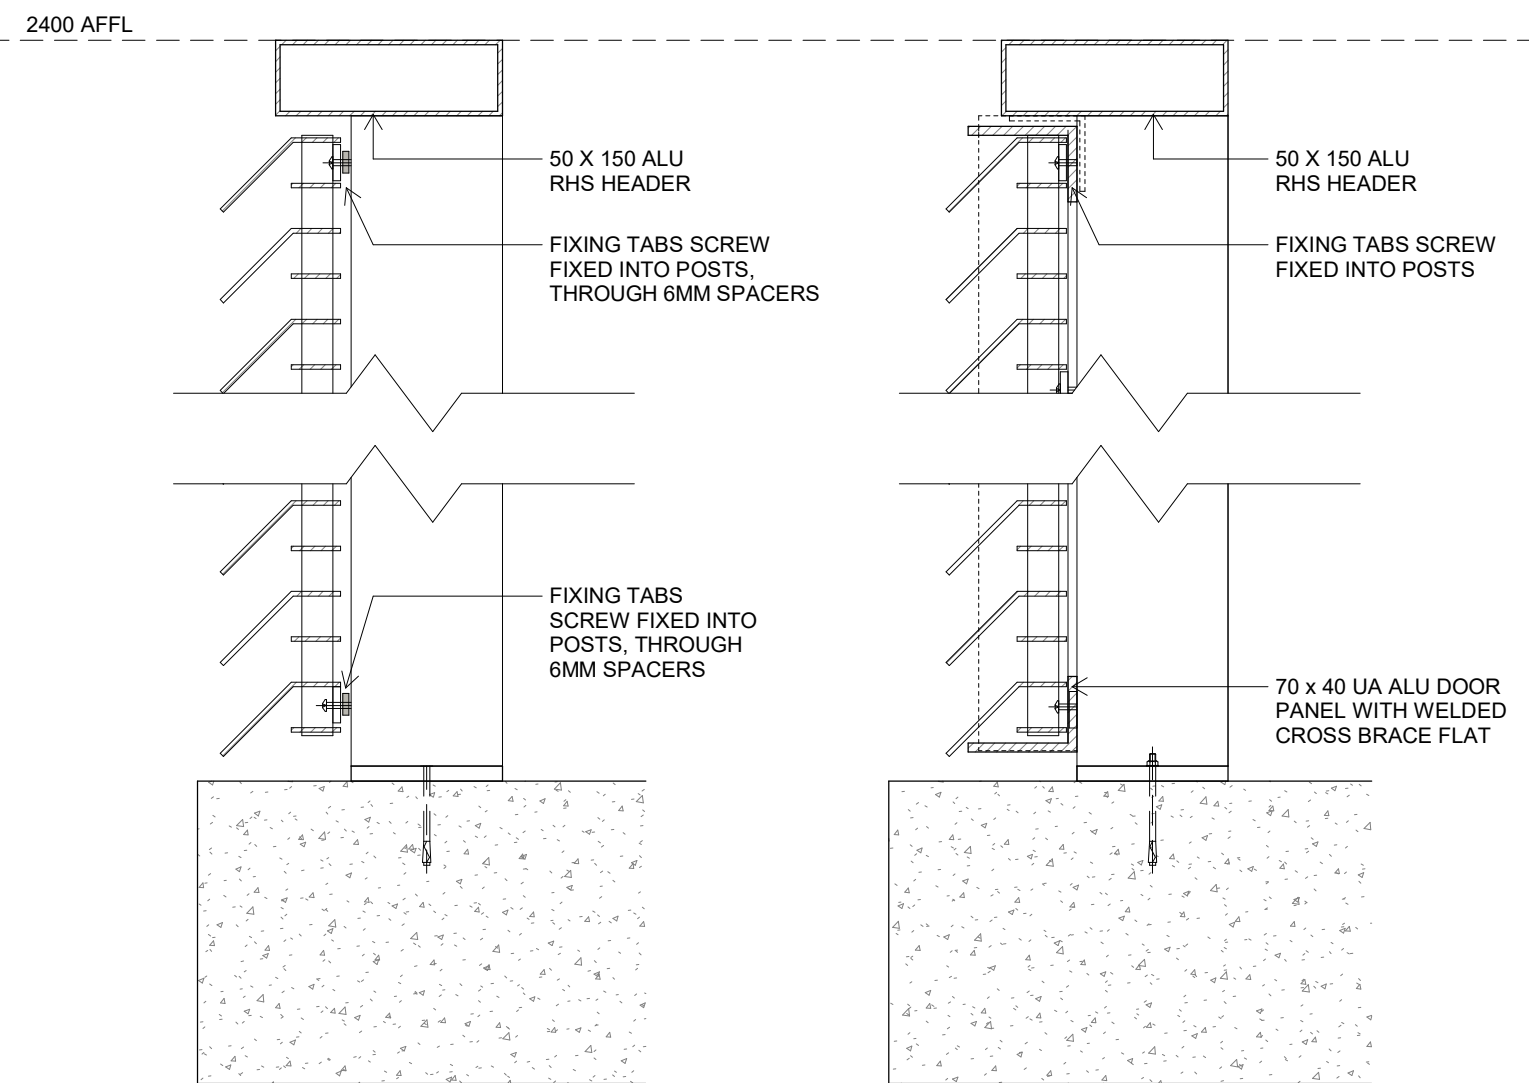

ALL POSTS, FRAMING AND LOUVRES TO BE PDC003 FINISH

SCR001 - TYPICAL SECTION DETAILS

1:5

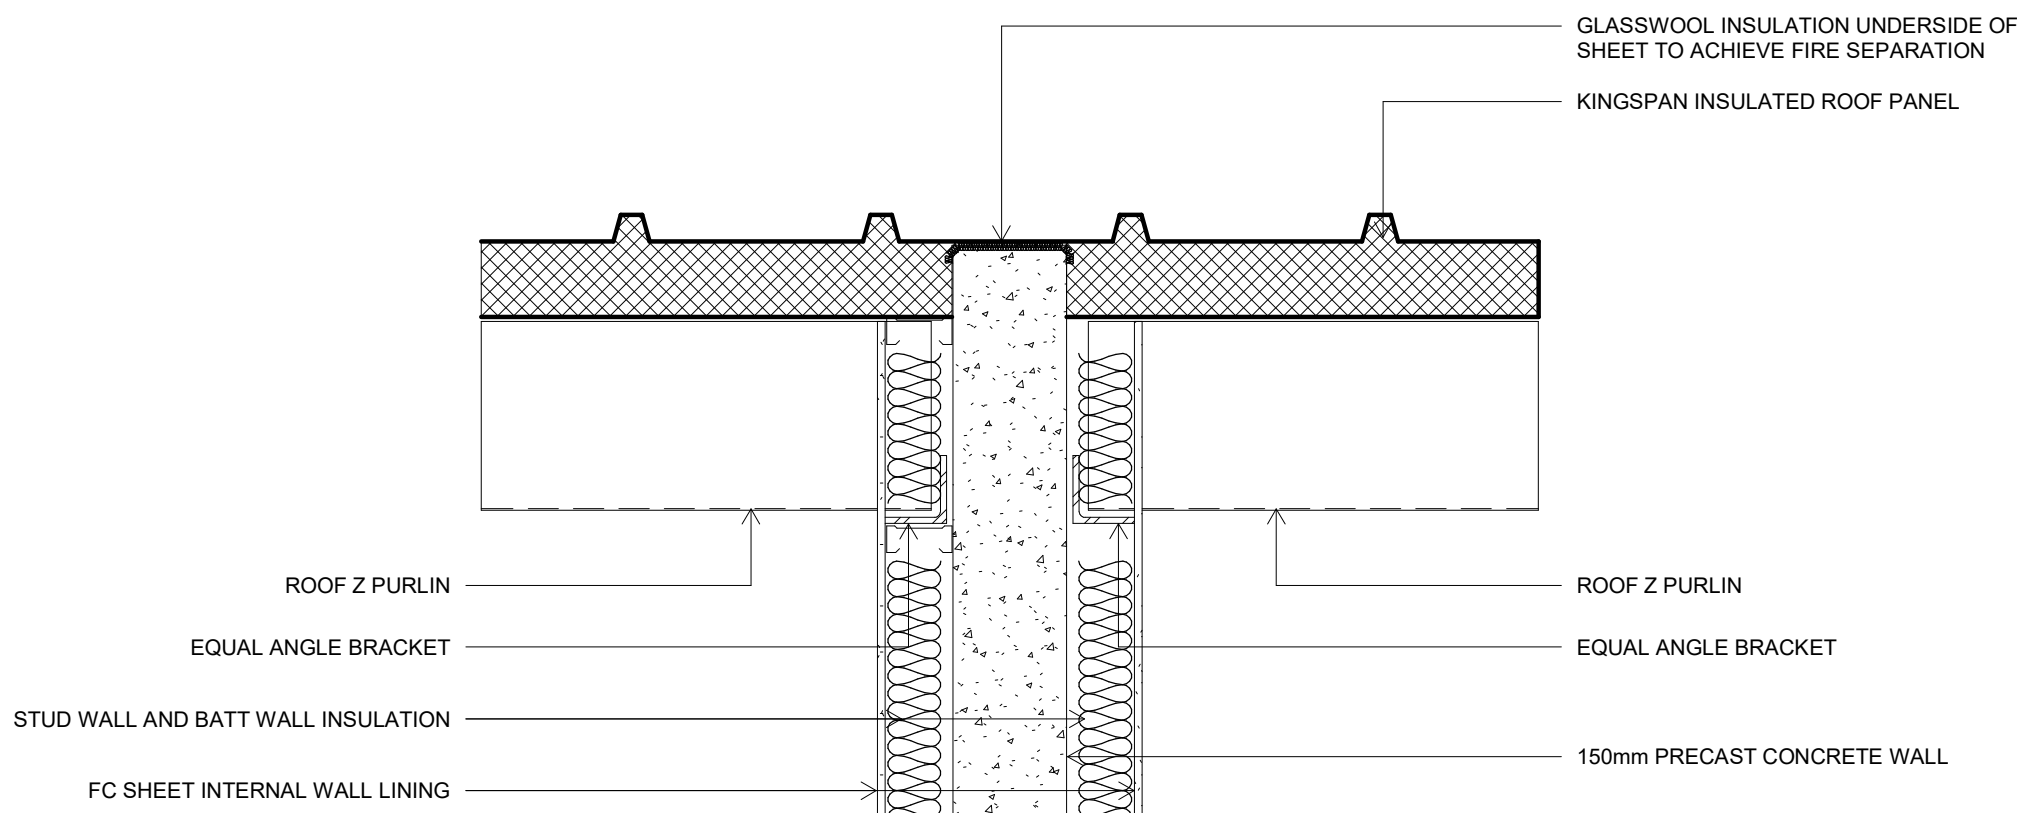

2 TENANCY FIRE WALL - DETAIL SECTION

1:10

COPYRIGHT :  
REPRODUCTION OF WHOLE OR PART OF THIS DOCUMENT  
CONSTITUTES AN INFRINGEMENT OF COPYRIGHT. THE  
INFORMATION, IDEAS AND CONCEPTS CONTAINED IN THIS  
DOCUMENT ARE CONFIDENTIAL. THE RECIPIENT(S) OF  
THIS DOCUMENT IS PROHIBITED FROM DISCLOSING SUCH  
INFORMATION IDEAS AND CONCEPTS TO ANY PERSON  
WITHOUT THE PRIOR WRITTEN CONSENT OF THE  
BRISBANE AIRPORT CORPORATION PTY. LTD.

| DRN | AMENDMENTS     | DATE       | REV |
|-----|----------------|------------|-----|
| JB  | 60% DD ISSUE 1 | 18.12.2025 | 1   |
| JB  | 60% DD ISSUE 2 | 05.02.2026 | 2   |

Archipelago

Archipelago  
Level 3, 109 George Street, Brisbane QLD 4000  
T +617 3238 4806 www.archipelago.com.au  
© ARCHIPELAGO ARCHITECTS PTY. LTD. All Rights Reserved  
This work is copyright and cannot be reproduced or copied by any means without written  
permission of Archipelago Architects Pty Ltd. Any  
license, express or implied, to use this document for any purpose  
whatsoever is restricted to the terms of the agreement between Archipelago Architects Pt  
y Ltd and the instructing party.

SKYGATE PLAY

DETAILS 01

|                      |                      |
|----------------------|----------------------|
| Drawn<br>JB          | Checked<br>DC        |
| Design Coordinated   | Compliance Checked   |
| Authorised For Issue | Construction Checked |



Brisbane Airport Corporation Pty Ltd  
 11 The Circuit Brisbane Airport QLD 4008  
 PO Box 61 Hamilton QLD 4007 Australia

Telephone: 61 7 3406 3000  
 Facsimile: 61 7 3406 3111  
 Email: [info@one.com.au](mailto:info@one.com.au)  
[www.brisbaneairport.com.au](http://www.brisbaneairport.com.au)  
 ABN 54 076 870 650

Scale  
As indicated

Size  
A1

Revision  
2

|             | Project No. | Originator | Volume | Level | Type | Discipline | Number |
|-------------|-------------|------------|--------|-------|------|------------|--------|
| Drawing No. | 25021       | - ARC      | - XX   | - 01  | - DR | - AR       | 000650 |