



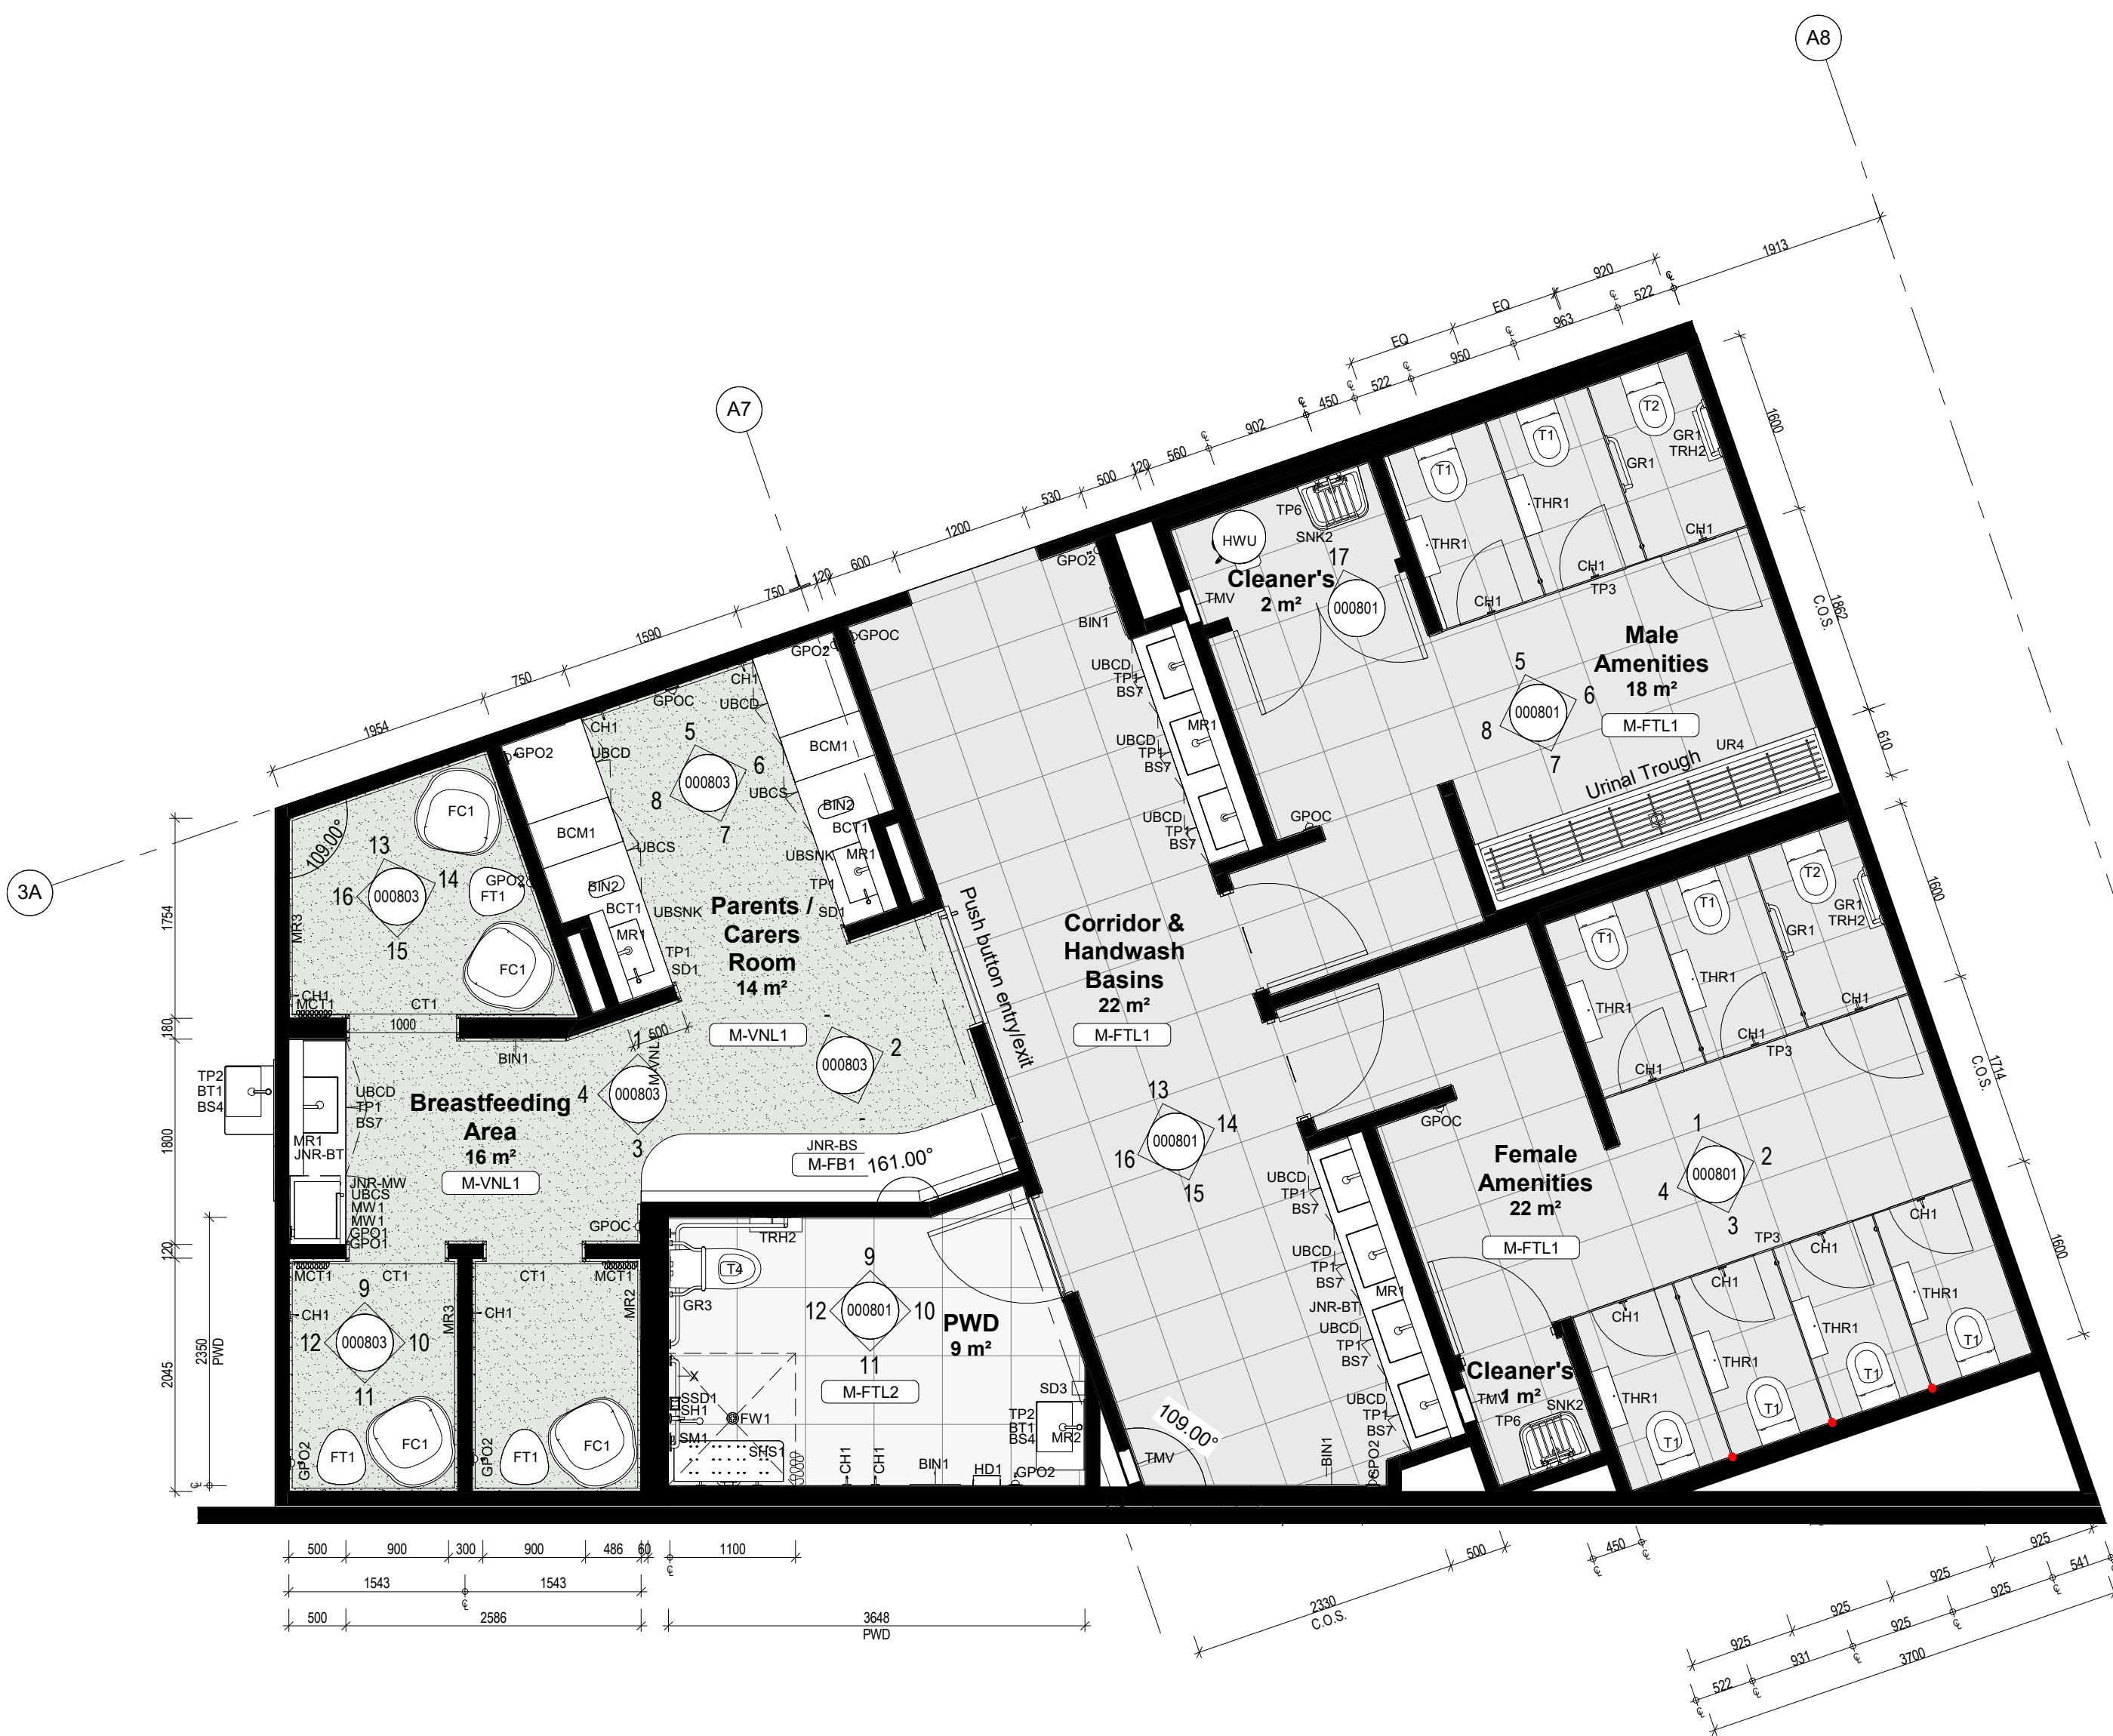

1 WET AREA PLAN - Area 51
1 : 50

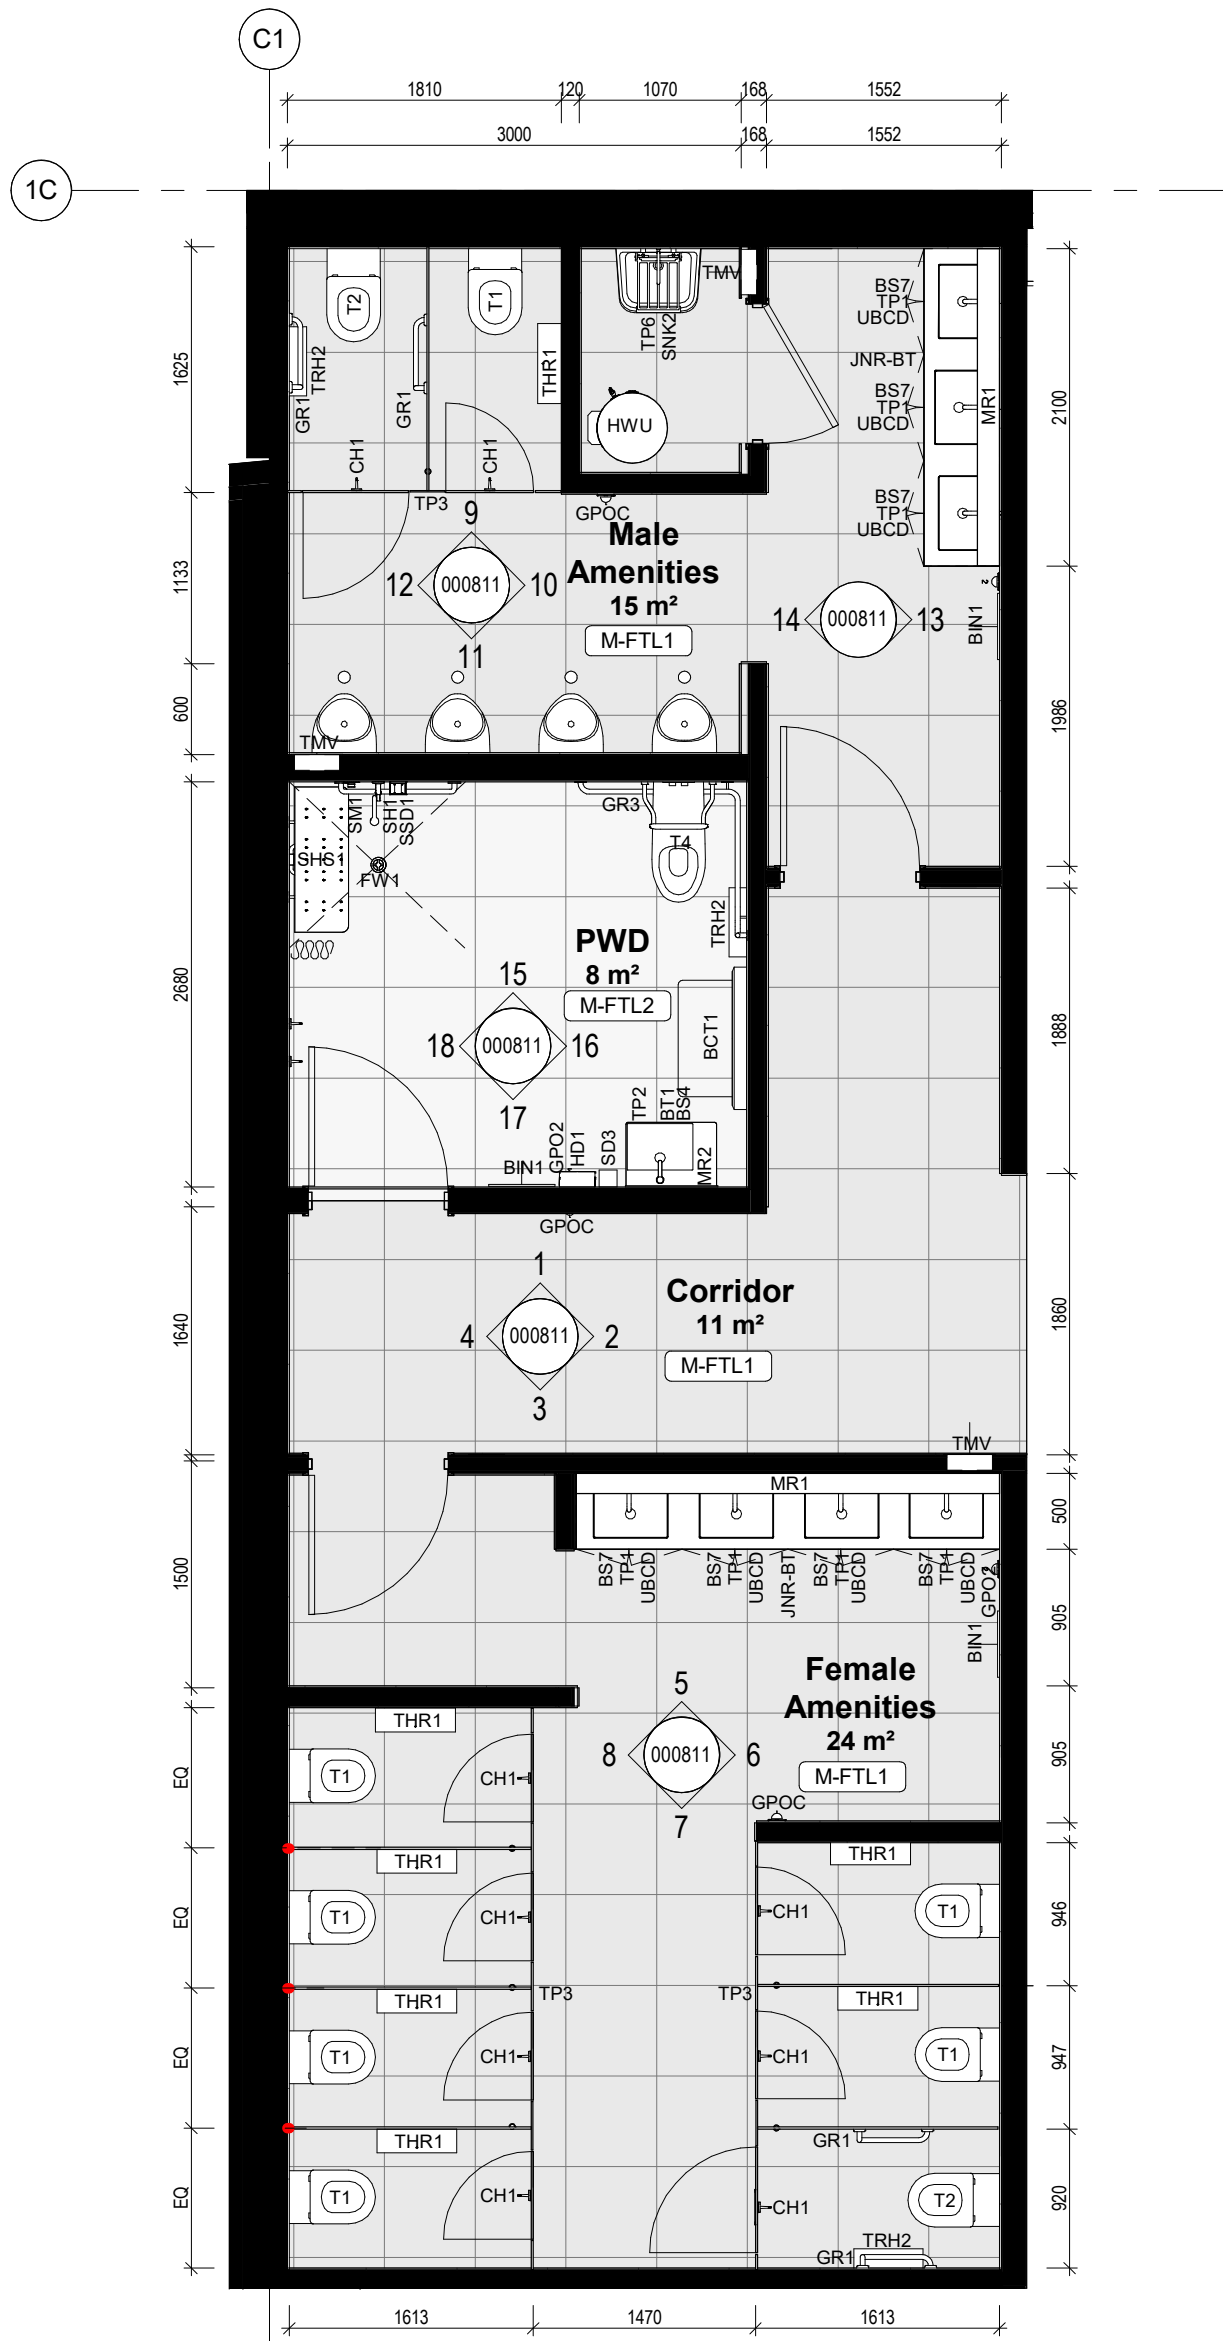

2 WET AREA PLAN - GAME OVER
1 : 50

Furniture, Fixtures & Fittings		
Type Mark	Description	Count
Casework		
BCT1	JOINERY: Custom Joinery Unit with Scalloped Change Table embedded in design	2
JNR-BS	JOINERY: benchseat, upholstered	1
JNR-BT	JOINERY: bench top	5
JNR-MW	JOINERY: microwave shelf	1
MR1	All-in-one mirror unit - Dolphin Avero - custom design	7
TP3	Compact laminate Floor Mounted Partition System	6
UBCD	JOINERY: underbench cupboard, double	17
UBCS	JOINERY: underbench cupboard, single	3
UBSNK	JOINERY: underbench sink shroud DDA COMPLIANT	2

Electrical Equipment		
HD1	Wall Mounted Hand Dryer	2
MW1	Microwave	2

Furniture, Fixtures & Fittings		
Type Mark	Description	Count
Electrical Fixtures		
GPO1	GPO: SINGLE	2
GPO2	GPO: DOUBLE	11
GPOC	GPO: single, wall mounted, cleaner	7
HWU	HOT WATER SYSTEM: Rheem Stainless Steel Heavy Duty Electric 50L 3x3.6kW	1
Furniture		
FC1	FURNITURE: chair, single armchair	4
FT1	FURNITURE: table, occasional	3

Furniture, Fixtures & Fittings		
Type Mark	Description	Count
Plumbing Fixtures		
BS4	BASIN: wall mounted	2
BS7	BASIN: under counter	17
BT1	Bottle Trap	2
SH1	Shower Set + Grab rail	2
SM1	Shower Mixer	2
SNK2	SINK: cleaners	2
T1	WC: standard	15
T2	WC: ambulant	4
T4	WC: universal	2
TMV	Thermostatic Mixing Valve in Recessed Lockable Box	5
TP1	TAP: wall mounted sensor tap	17
TP2	TAP: hob mounted sensor tap	2
TP6	TAP: wall mounted cleaners sink set	2
UR1	URINAL: wall hung urinal with ceiling mounted smart flush sensor	4
UR4	URINAL: trough	1

Furniture, Fixtures & Fittings		
Type Mark	Description	Count
Signage		
SGN-AMB	SIGNAGE: ambulant toilet	4
SGN-BC	SIGNAGE: parents room / baby change	1
SGN-F	SIGNAGE: female toilet	2
SGN-M	SIGNAGE: male toilet	2
SGN-PB	SIGNAGE: push to open button	1
SGN-PWD	SIGNAGE: all gender accessible toilet & shower	2

Furniture, Fixtures & Fittings		
Type Mark	Description	Count
Specialty Equipment		
BCM1	Baby Change Mat & SFB1 Safety Belt	2
BCT1	Baby Change Table - Fold Down	1
BIN1	Waste Bin - Recessed	7
BIN2	Nappy Bin - In cupboard	2
CH1	Coat Robe Hook and Door Stop	28
CT1	Curtain track - privacy screen (straight)	3
CT2	Curtain track - shower (L)	2
GR1	Grab Rail - Ambulant	8
GR3	Grab Rail - PWD	2
MCT1	Privacy Curtain	2
MCT2	Shower Curtain	2
MR2	Mirror (610 x 990)	3
MR3	Mirror (610 x 1800)	2
SD1	Soap Dispenser, sensor, hob mounted	2
SD3	Soap Dispenser, sensor, wall mounted	2
SHS1	Folding Shower Seat	2
SSD1	Soap Dish	2
THR1	Toilet Roll Holder	15
TRH2	Toilet Roll Holder	6

COPYRIGHT: REPRODUCTION OF WHOLE OR PART OF THIS DOCUMENT CONSTITUTES AN INFRINGEMENT OF COPYRIGHT. THE INFORMATION, IDEAS AND CONCEPTS CONTAINED IN THIS DOCUMENT ARE CONFIDENTIAL. THE RECIPIENT(S) OF THIS DOCUMENT IS PROHIBITED FROM DISCLOSING SUCH INFORMATION IDEAS AND CONCEPTS TO ANY PERSON WITHOUT THE PRIOR WRITTEN CONSENT OF THE BRISBANE AIRPORT CORPORATION PTY. LTD.

DRN	AMENDMENTS	DATE	REV
JB	60% DD ISSUE 1	18.12.2025	1
JB	FOR COORDINATION	29.01.2026	2
JB	60% DD ISSUE 2	05.02.2026	3

TAG LEGEND	
BCT1	Baby Change Tables
BIN1	WASTE BIN - RECESSED
BIN2	NAPPY BIN - IN CUPBOARD
CLD006	PRECAST CONCRETE
COL	STRUCTURAL COLUMN - REFER STRUCTURAL ENGINEER
CON001	CONCRETE SLAB
CON002	CONCRETE SLAB - EXTERNAL HARDSTAND
CT1	CURTAIN TRACK
DP	DOWNPIPE
FH	DOUBLE PILLAR FIRE HYDRANT REFER HYD. ENG.
FLW003	FLOOR DRAIN
GPO1	GPO SINGLE
GPOC	GPO SINGLE - CLEANERS
M-FTL-1	WET AREA TILES - FLOOR
M-FTL-2	WET AREA TILES - FLOOR
M-TIL-2	WET AREA - WALL TILE
M-VNL1	SHEET VINYL - FLOOR
MCT1	PRIVACY CURTAIN
MEC001	MECHANICAL DUCT - REFER MECHANICAL ENGINEER
MR2	MIRROR 2
MR3	MIRROR 3
SD3	SOAP DISPENSER
SNK2	SINK - CLEANERS
T1	WC STANDARD
T2	WC - AMBULANT
T4	WC - UNIVERSAL
THR1	TOILET ROLL HOLDER
TMV	THERMOSTATIC MIXING VALVE
TP1	TAP - WALL MOUNTED SENSOR
TRH2	TOILET ROLL HOLDER
UR1	URINAL - WALL HUNG
UR4	URINAL - TROUGH

Archipelago

Archipelago
Level 3, 109 George Street, Brisbane QLD 4000
T +61 7 3236 4000 www.archipelago.com.au
© ARCHIPELAGO ARCHITECTS PTY LTD. All Rights Reserved
This work is copyright and cannot be reproduced or copied by any means without written permission of Archipelago Architects Pty Ltd. Any license, express or implied, to use this document for any purpose whatsoever is restricted to the terms of the agreement between Archipelago Architects Pty Ltd and the instructing party.

SKYGATE PLAY

WET AREA PLANS

Drawn JB	Checked DC
Design Coordinated	Compliance Checked
Authorised For Issue	Construction Checked

 Brisbane Airport	Brisbane Airport Corporation Pty Ltd 11 The Circuit Brisbane Airport QLD 4008 PO Box 61 Hamilton QLD 4007 Australia	Scale 1 : 50
	Telephone : 61 7 3406 3000 Facsimile : 61 7 3406 3111 Email : info@bne.com.au	Size A1
	www.brisbaneairport.com.au ABN 54 076 870 650	Revision 3

Drawing No.	25021 - ARC - XX - 01 - DR - AR - 000800
-------------	--