


Typical Wet Area Fittings and Fixture Setout:


Typical Fittings and Fixture Setout

Typical fixture mounting heights unless otherwise noted.

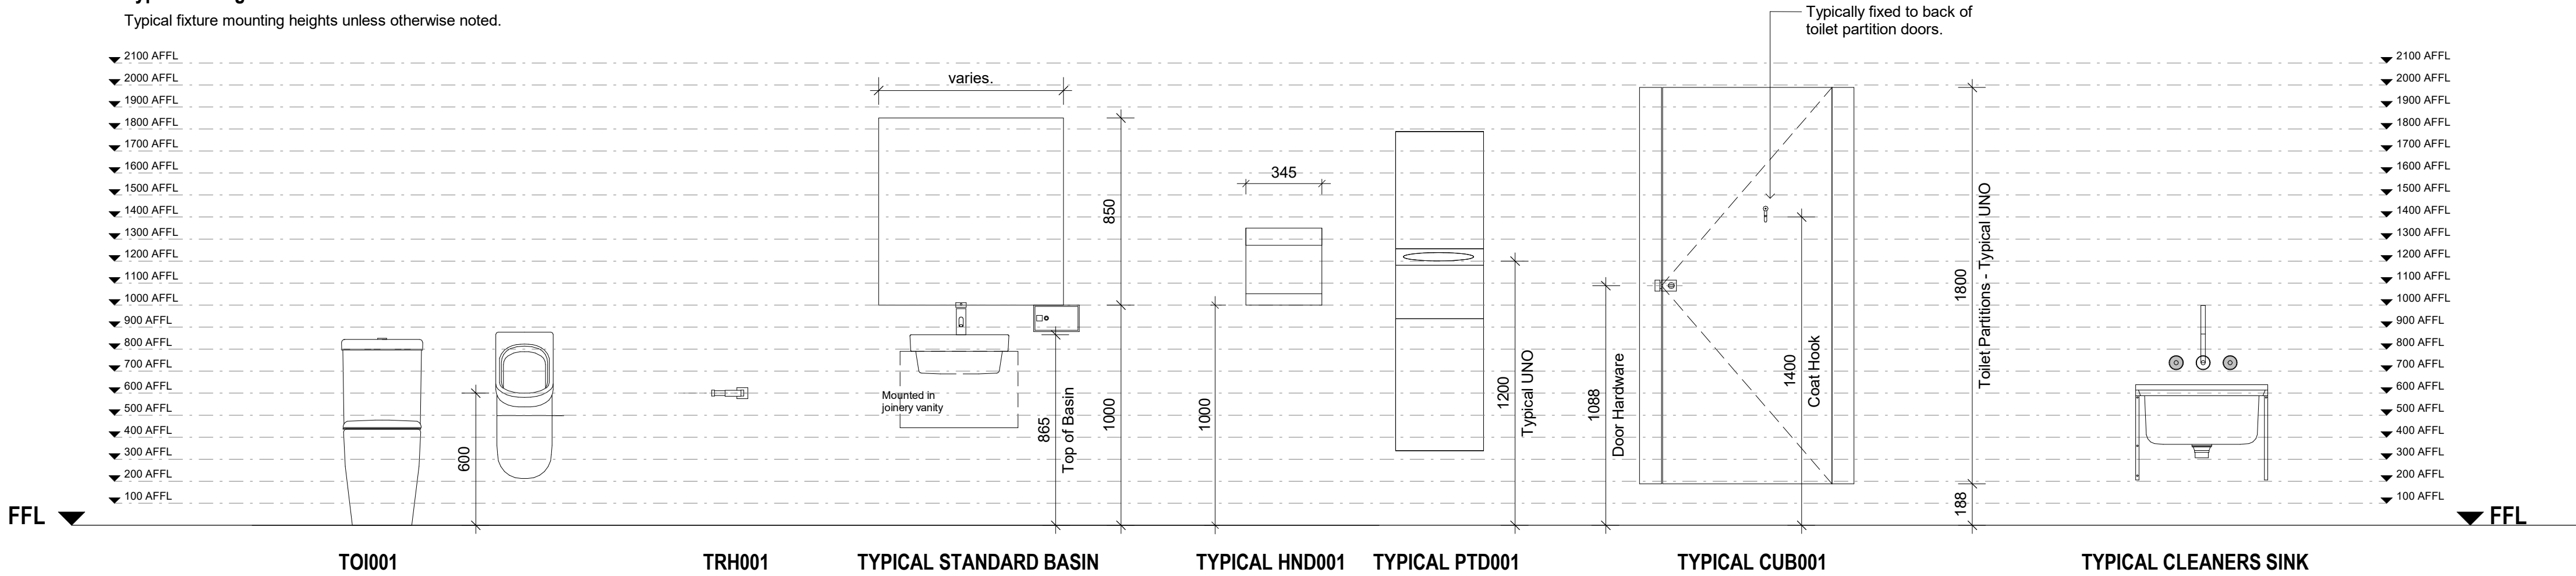


Typical PWD Fittings and Fixture Setout

NOTE: All fittings and fixtures to comply with AS1428.1 2009 standards

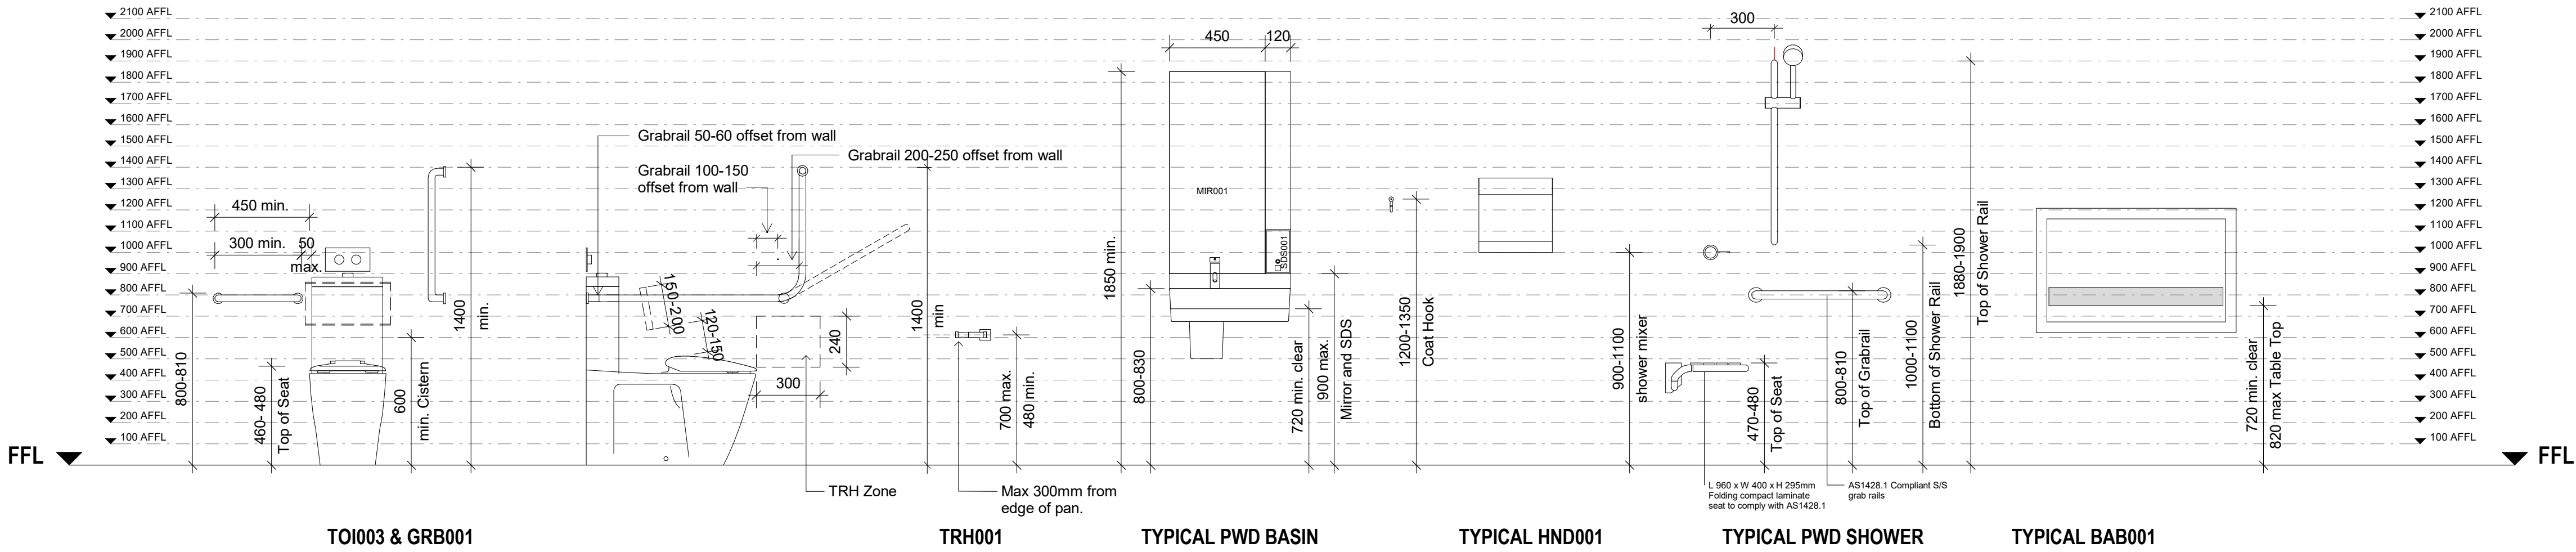

Typical Ambulant Fittings and Fixture Setout

NOTE: All fittings and fixtures to comply with AS1428.1 2009 standards

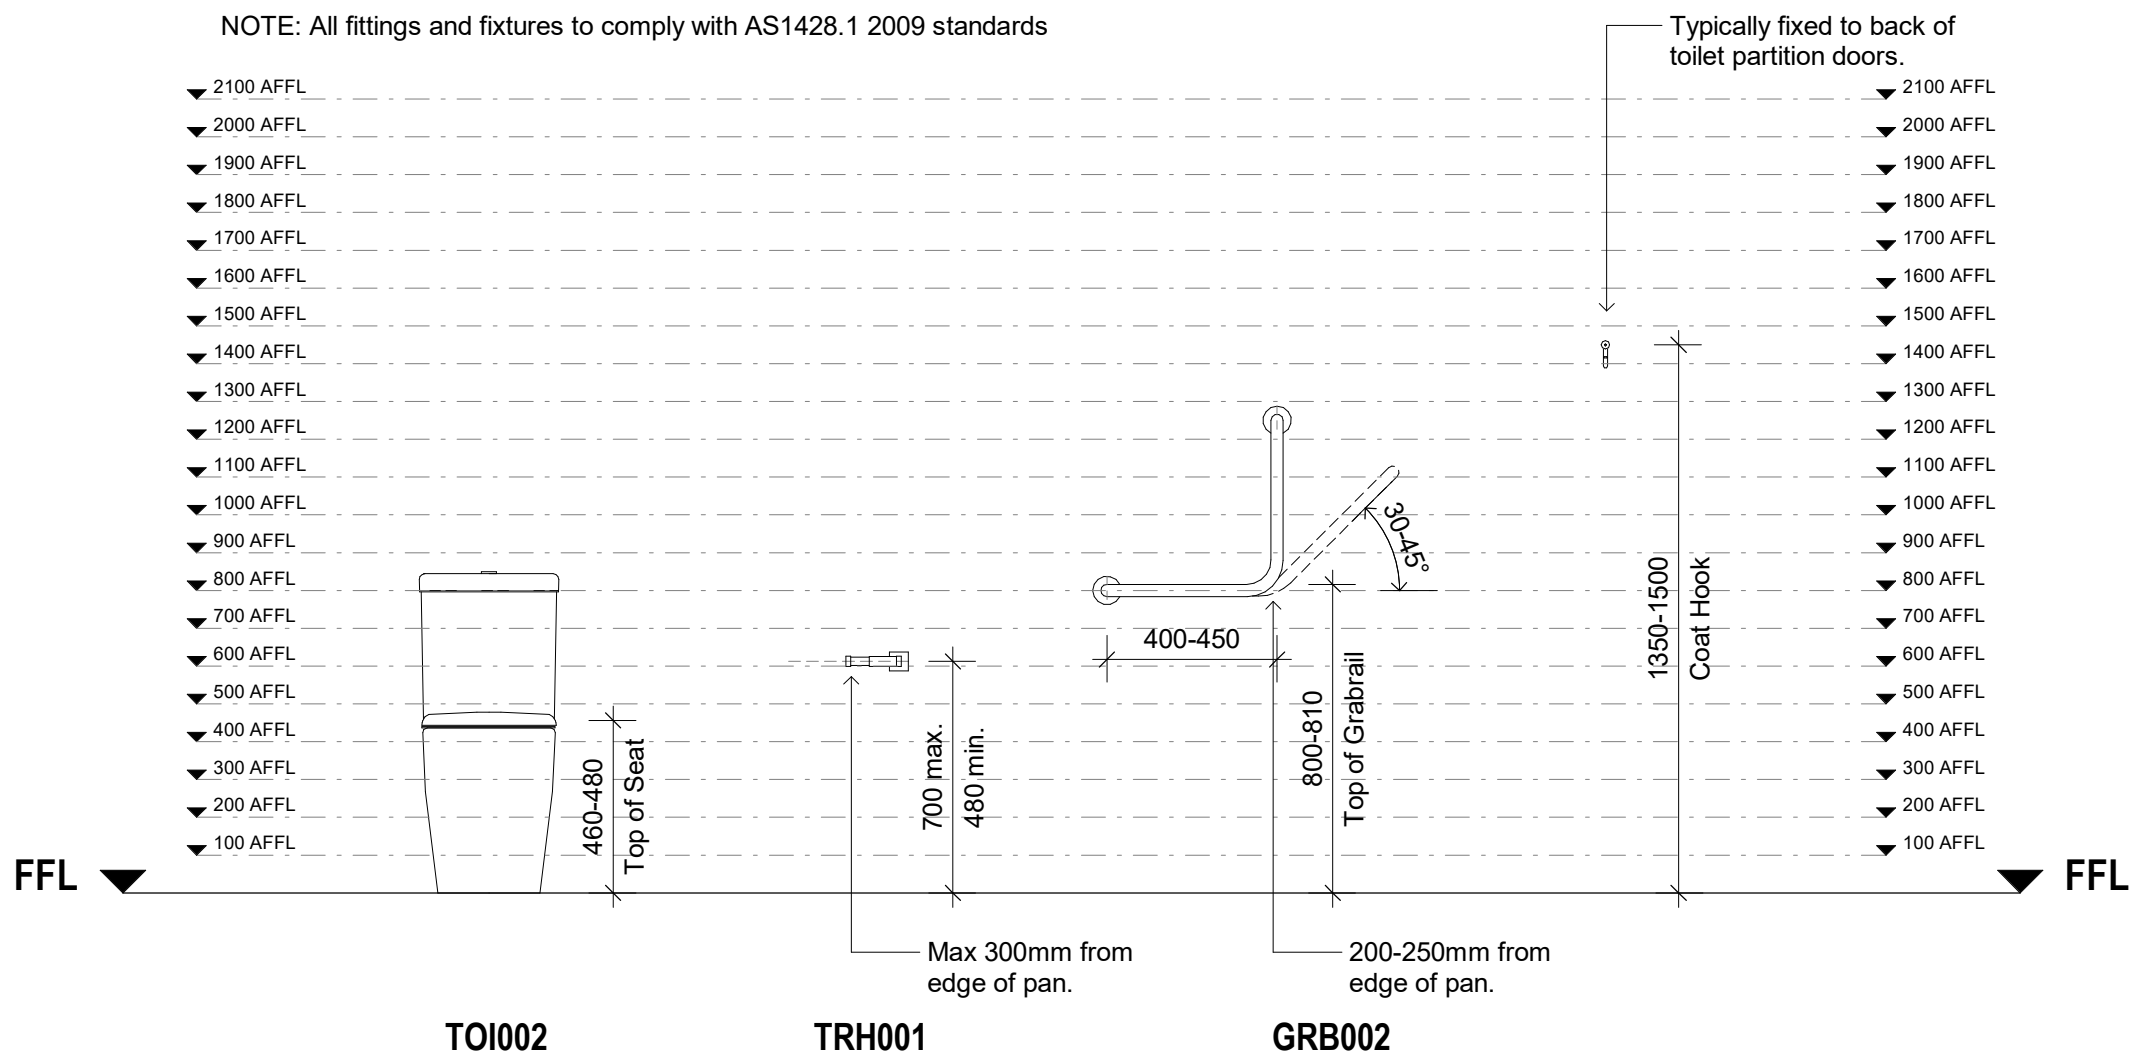

LEGEND:

General Notes:

- All fixtures and fittings are shown indicatively only, refer to Fixtures and Fittings Schedule for fixtures and fitting specifications and details.
- All fixtures, fittings and dimensions within the PWD and ambulant areas to comply with AS1428.1 2009.
- Partition structure to support 1100N when grab rails are supported from wall.
- Location of all Floor Wastes and Hydraulic services to be confirmed with Hydraulic Engineer's drawings.
- Elevation setout of fittings and fixtures is typical unless noted otherwise.
- Refer to manufacturer's guides for all fittings and fixtures in for installation requirements.
- All fixture dimensions are measured from the Finished Floor Level (FFL).
- Fixture setouts from adjoining walls typically from finished surface.
- Typically all walls within wet areas to have full height tiles. Refer to elevations for tile codes and extents.
- Provide aluminium square profile BAT trims to all exposed tile junctions.

COPYRIGHT:
REPRODUCTION OF WHOLE OR PART OF THIS DOCUMENT
CONSTITUTES AN INFRINGEMENT OF COPYRIGHT. THE
INFORMATION, IDEAS AND CONCEPTS CONTAINED IN THIS
DOCUMENT ARE CONFIDENTIAL. THE RECIPIENT(S) OF
THIS DOCUMENT IS PROHIBITED FROM DISCLOSING SUCH
INFORMATION IDEAS AND CONCEPTS TO ANY PERSON
WITHOUT THE PRIOR WRITTEN CONSENT OF THE
BRISBANE AIRPORT CORPORATION PTY. LTD.

DRN	AMENDMENTS	DATE	REV
JB	60% DD ISSUE 1	18.12.2025	1
JB	60% DD ISSUE 2	05.02.2026	2

Archipelago

Archipelago
Level 3, 109 George Street, Brisbane QLD 4000
T +617 3238 4500 www.archipelago.com.au
© ARCHIPELAGO ARCHITECTS PTY. LTD. All Rights Reserved
This work is copyright and cannot be reproduced or copied by any means without written
permission of Archipelago Architects Pty Ltd. Any
license, express or implied, to use this document for any purpose
whatsoever is restricted to the terms of the agreement between Archipelago Architects Pt
y Ltd and the instructing party.

SKYGATE PLAY

WET AREA DETAILS - TYPICAL SETOUTS

Drawn JB	Checked DC
Design Coordinated	Compliance Checked
Authorised For Issue	Construction Checked

	Brisbane Airport Corporation Pty Ltd 11 The Circuit Brisbane Airport QLD 4008 PO Box 61 Hamilton QLD 4007 Australia Telephone : 61 7 3406 3000 Facsimile : 61 7 3406 3111 Email : info@bne.com.au www.brisbaneairport.com.au ABN 54 076 870 650	Scale 1 : 20 Size A1 Revision 2
	Project No. Originator Volume Level Type Discipline Number	

Drawing No.	25021 - ARC - XX - 01 - DR - AR - 000820
-------------	--