

LEGEND

- FINISHED SURFACE

EXISTING SURFACE


BULK EARTHWORKS SURFACE

EARTHWORKS AREA OF CUT


EARTHWORKS AREA OF FILL
-

NOTES


FOR EARTHWORKS LAYOUT PLAN & REFERENCE NOTES
REFER DWG No C-101

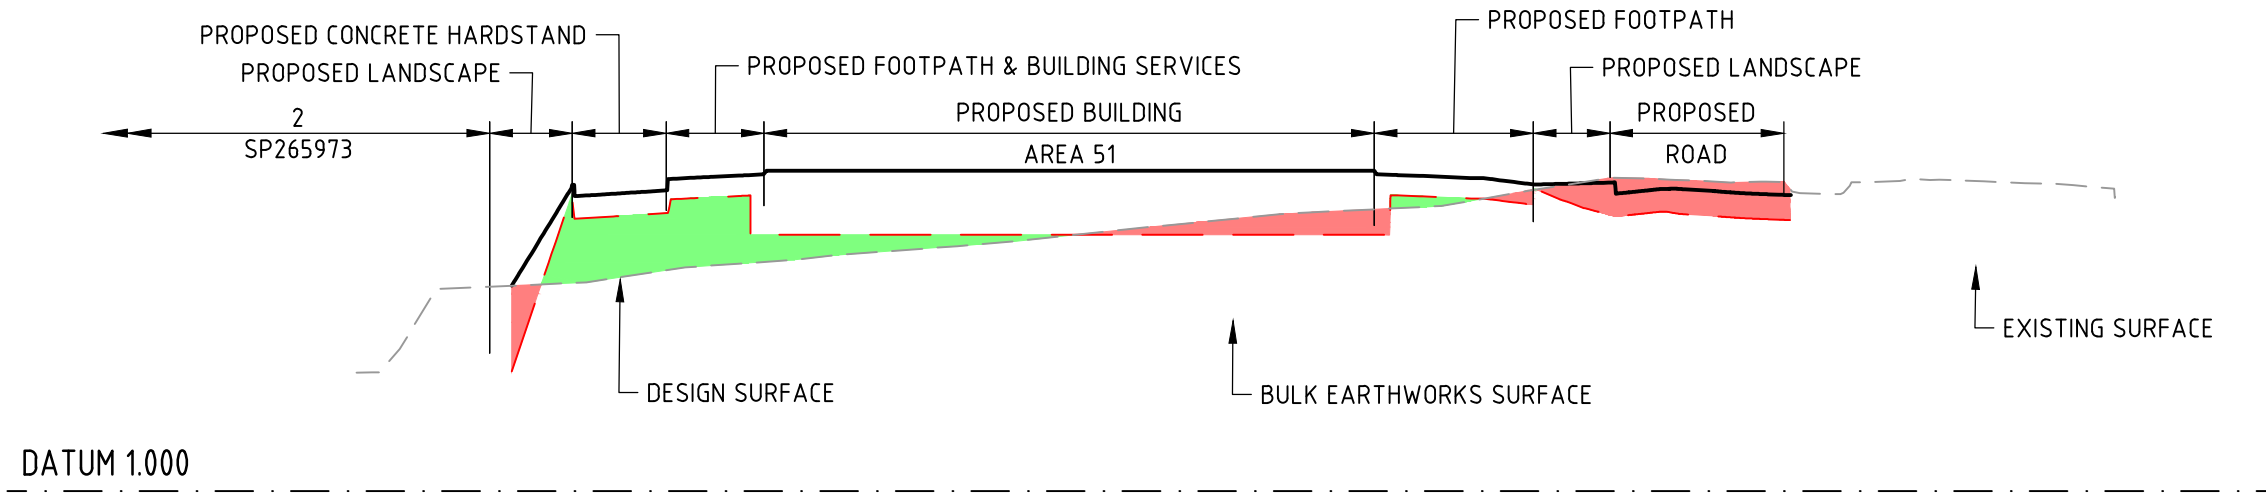


SECTION D
H 1500 V 1:100

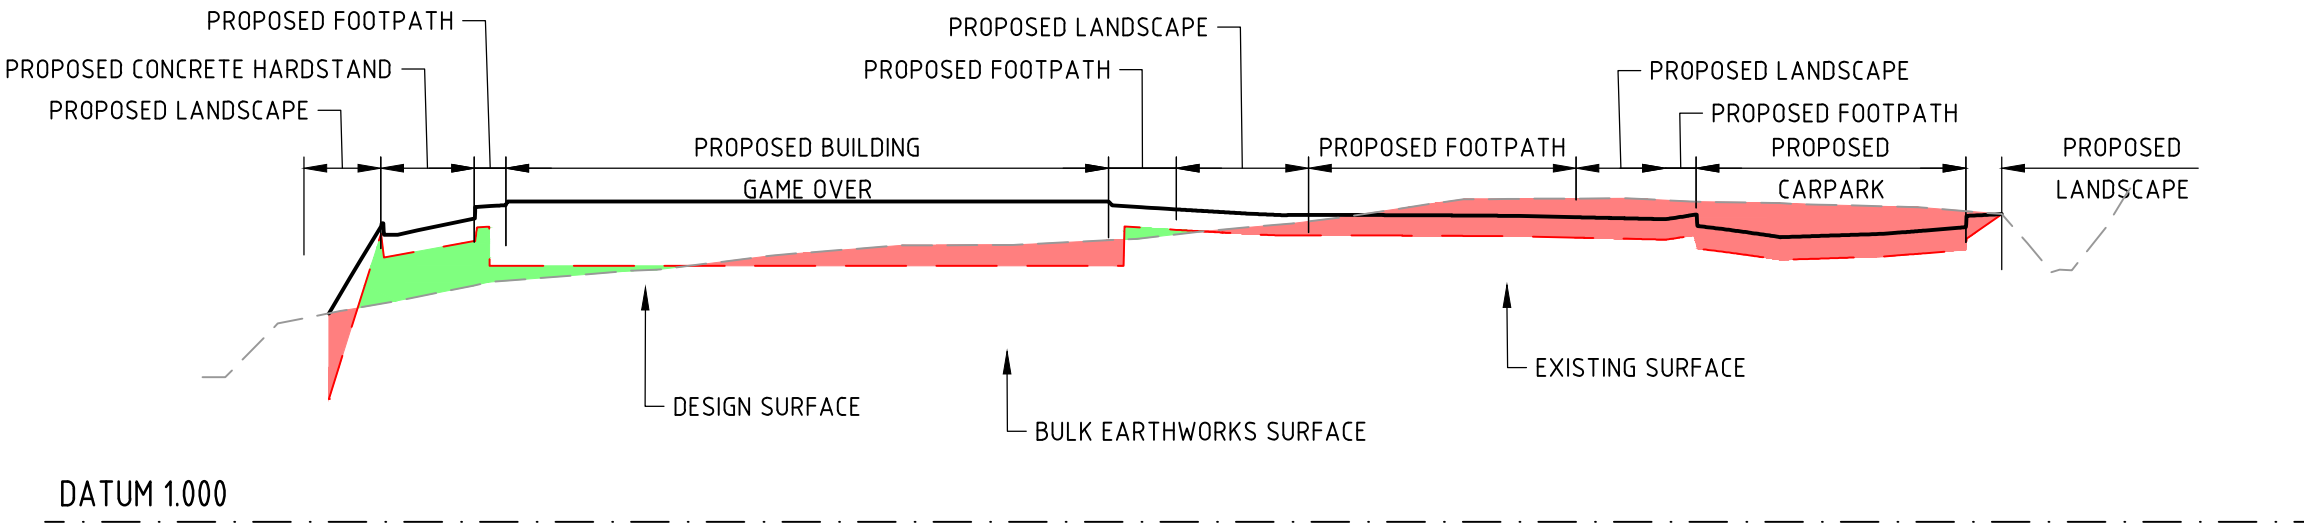

SECTION C
H 1500 V 1:100

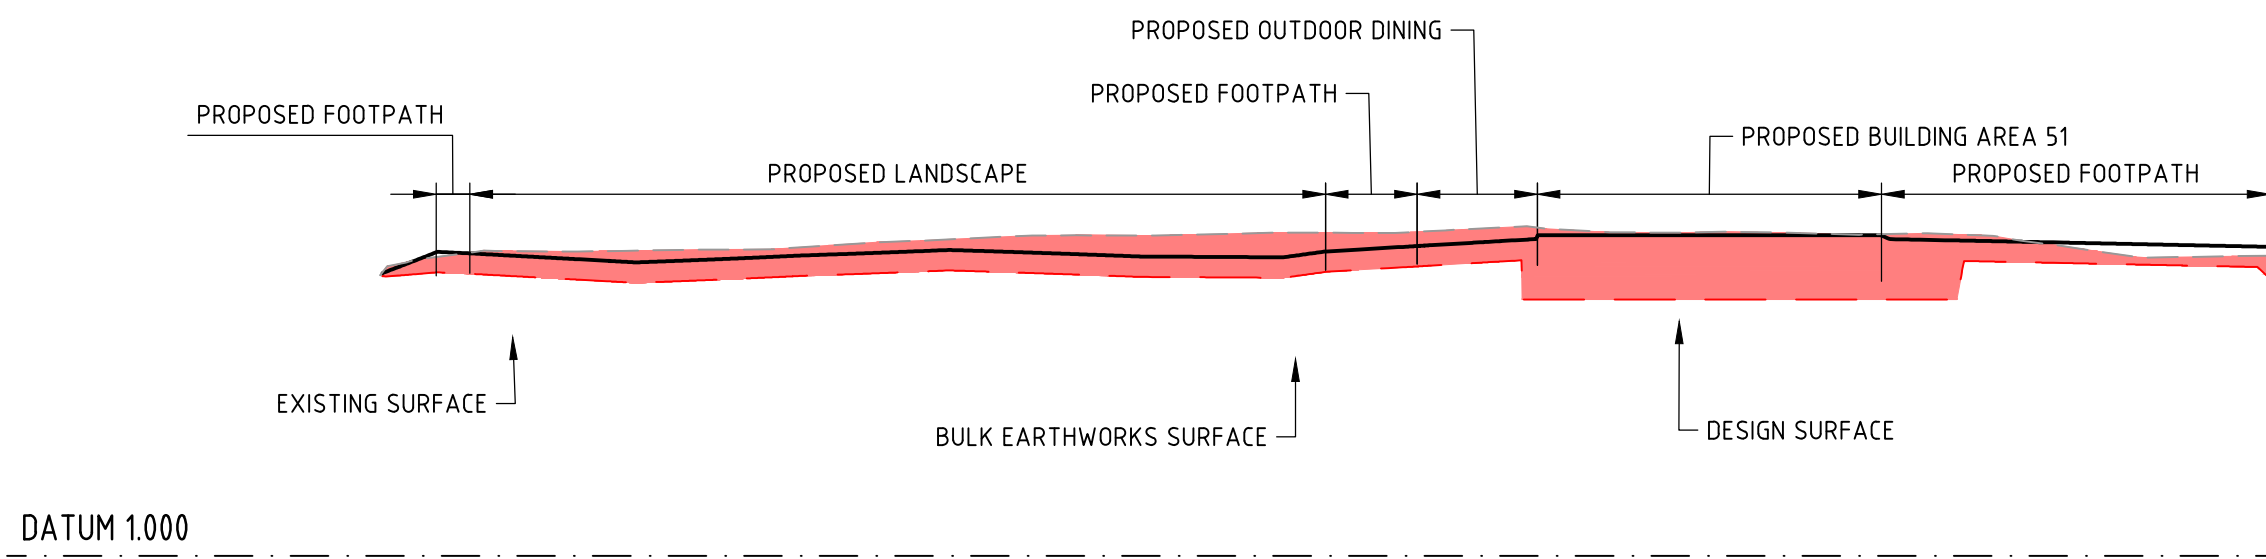


SECTION B
H 1500 V 1:100

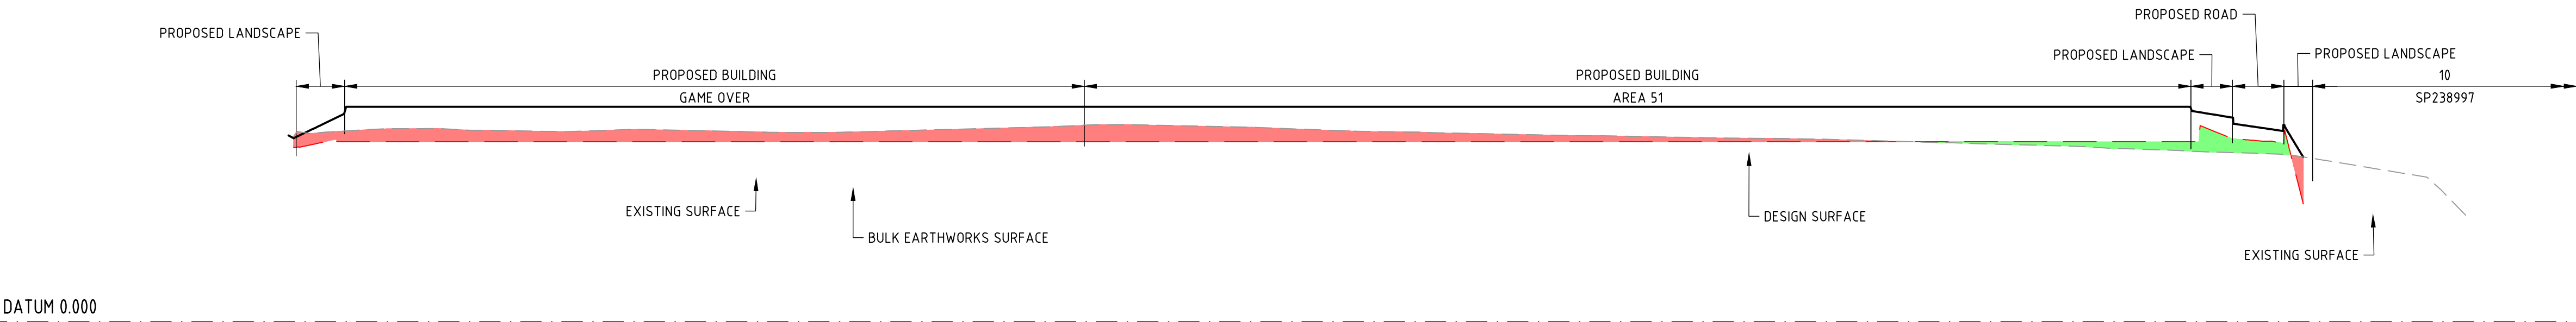

SECTION A
H 1500 V 1:100

NOT FOR CONSTRUCTION

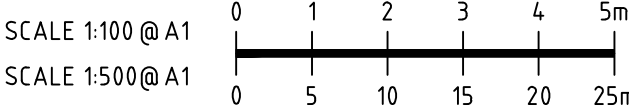

revision notes				Brisbane Airport				NORTHROP				Drawn J. DENG				Checked A. DE ANDRADE				SKYGATE PLAY BRISBANE AIRPORT				Brisbane Airport				Scale AS ABOVE			
COPYRIGHT : REPRODUCTION OF WHOLE OR PART OF THIS DOCUMENT CONSTITUTES AN INFRINGEMENT OF COPYRIGHT. THE INFORMATION, IDEAS AND CONCEPTS CONTAINED IN THIS DOCUMENT ARE CONFIDENTIAL. THE RECIPIENT(S) OF THIS DOCUMENT IS PROHIBITED FROM DISCLOSING SUCH INFORMATION IDEAS AND CONCEPTS TO ANY PERSON WITHOUT THE PRIOR WRITTEN CONSENT OF THE BRISBANE AIRPORT CORPORATION PTY. LTD.				Brisbane Level 25, 12 Creek Street, Brisbane QLD 4000 GPO BOX 423 Brisbane QLD 4001 (07) 3365 0400 brisbane@northrop.com.au ABN 81 094 433 100				Design Coordinated R. MITCHELL				Compliance Checked S.KILLORAN				BULK EARTHWORKS SECTIONS				Size A1				Revision C				Drawing Number			
AMENDMENTS				DATE				Rev				Authorised For Issue S.KILLORAN				Construction Checked N/A				Project No. 25021 - NRP - XX - XX - DR- CI -000111				Originator Volume Level Type Discipline Number				Plot Date & Time: 9/02/2026 2:16:08 PM			
DRN				Printer: AUTOCAD PDF (GENERAL DOCUMENTATION)				User: Lionel Quijano				File: 250946-C-000111-EarthworkSections.dwg				Pentable: ---				C:\12d\stdata\NorthropSYN\250946 - BAC SKYGATE_572\CAD\3-DD											