




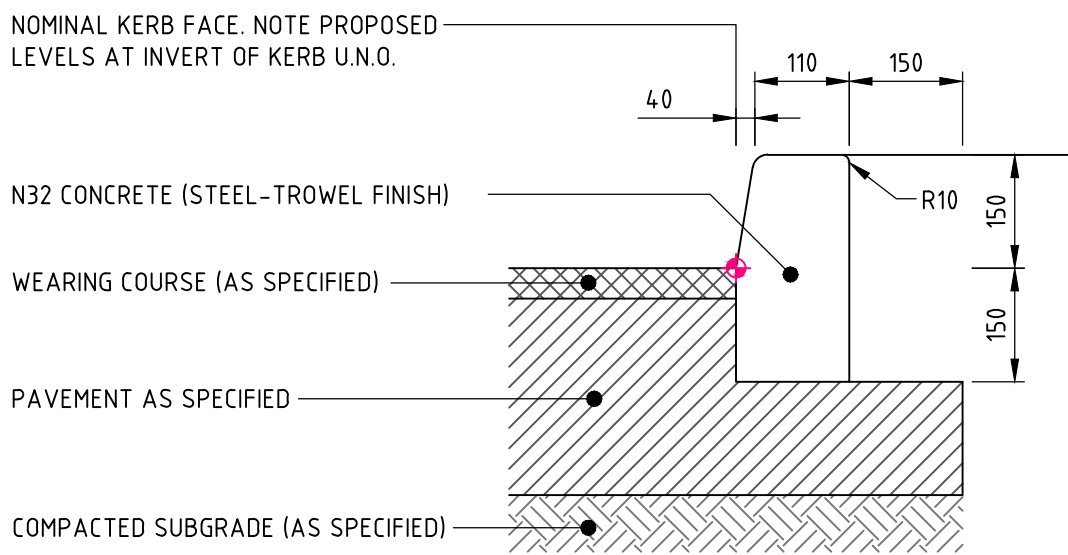

BARRIER KERB - TYPE B2
EXPANSION JOINTS @ MAX 12m CTRS / TOOL JOINTS @ MAX 3m CTRS
ALL RADII TO BE 20mm U.N.O.

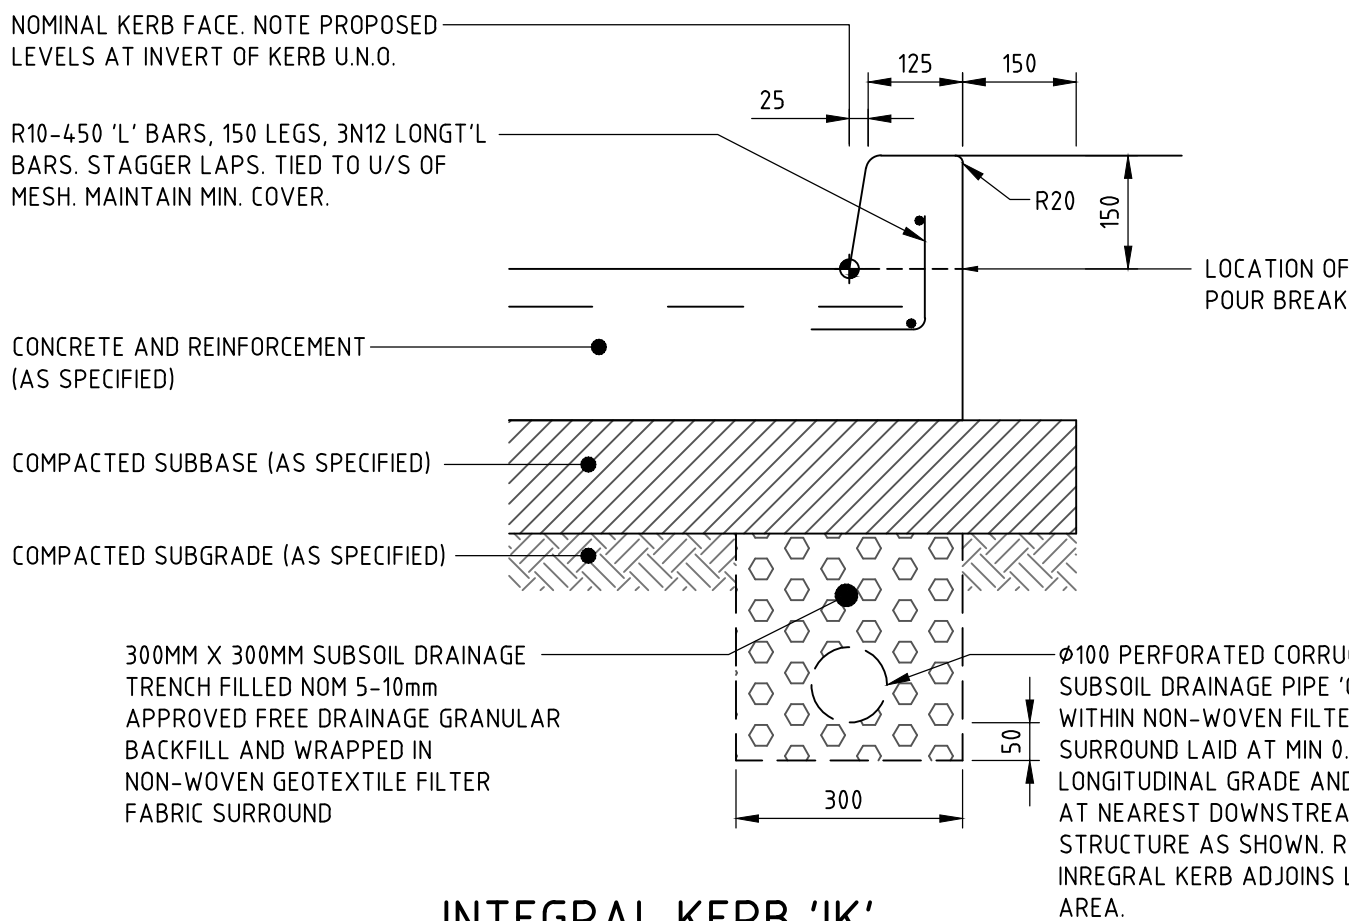


INTEGRAL KERB 'IK'
PROVIDE TOOL JOINTS @ MAX 3m CENTRES AND TO MATCH SAWN AND DOWELED JOINTS. DISCONTINUE LONG'L REINF'T AT ALL JOINTS. ALL RADII'S TO BE 20mm UNLESS NOTED OTHERWISE

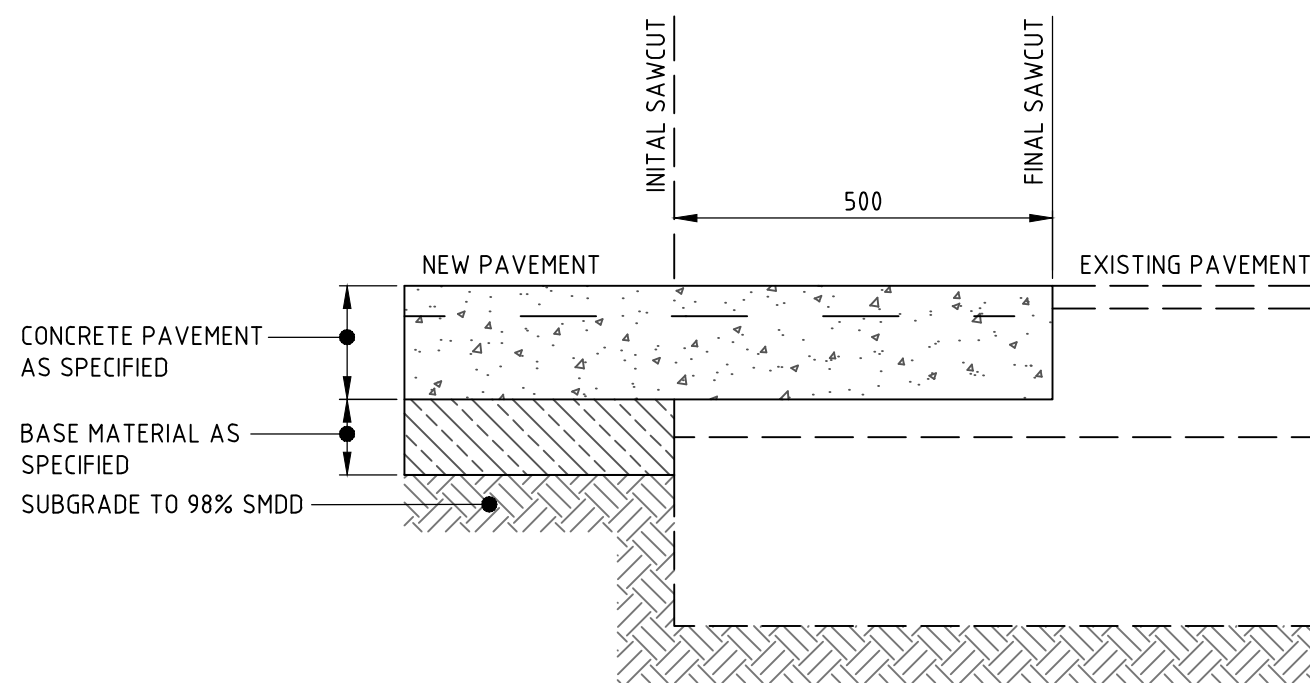


**NEW CONCRETE TO NEW ASPHALT
PAVEMENT JUNCTION DETAIL 'INT'**


- NOTES:**
- MATCH ASPHALT SMOOTHLY WITH EXISTING
 - FINAL SAWCUT TO BE UNDERTAKEN AT A TIME TO ENSURE MINIMAL DAMAGE / CHIPPING OCCURS TO EDGE OF EXISTING

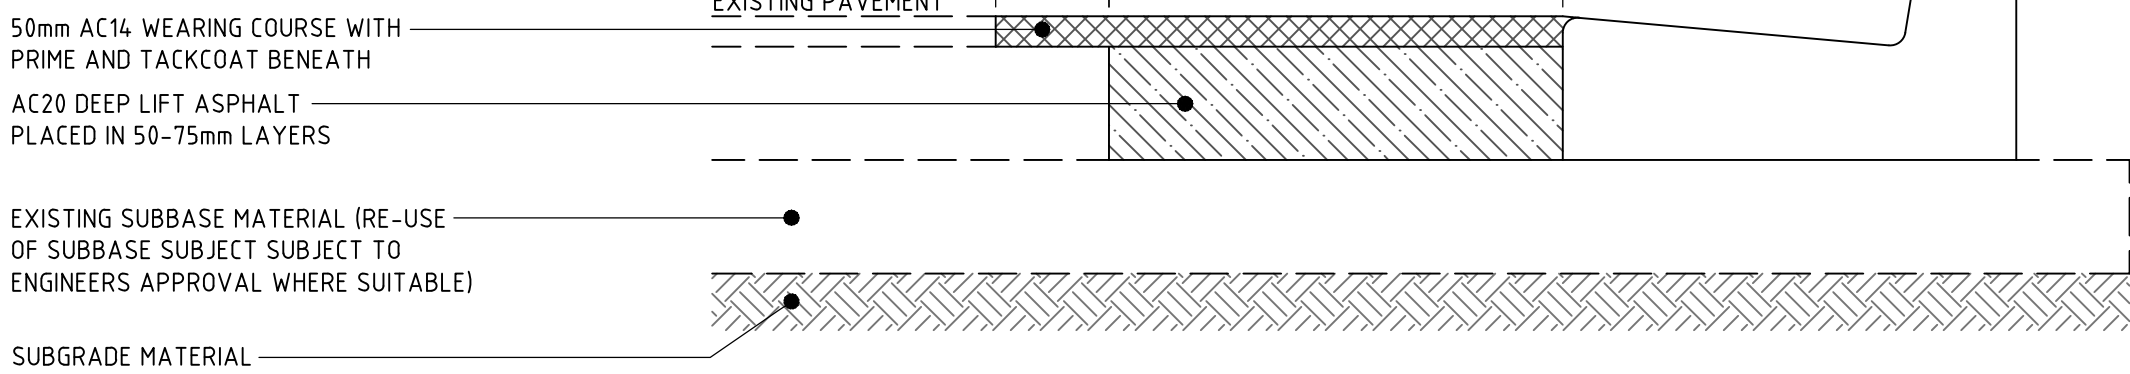


PAVEMENT INTERFACE 'INT1'
MIN CBR ____% (CONTRACTOR TO CONFIRM ONSITE)

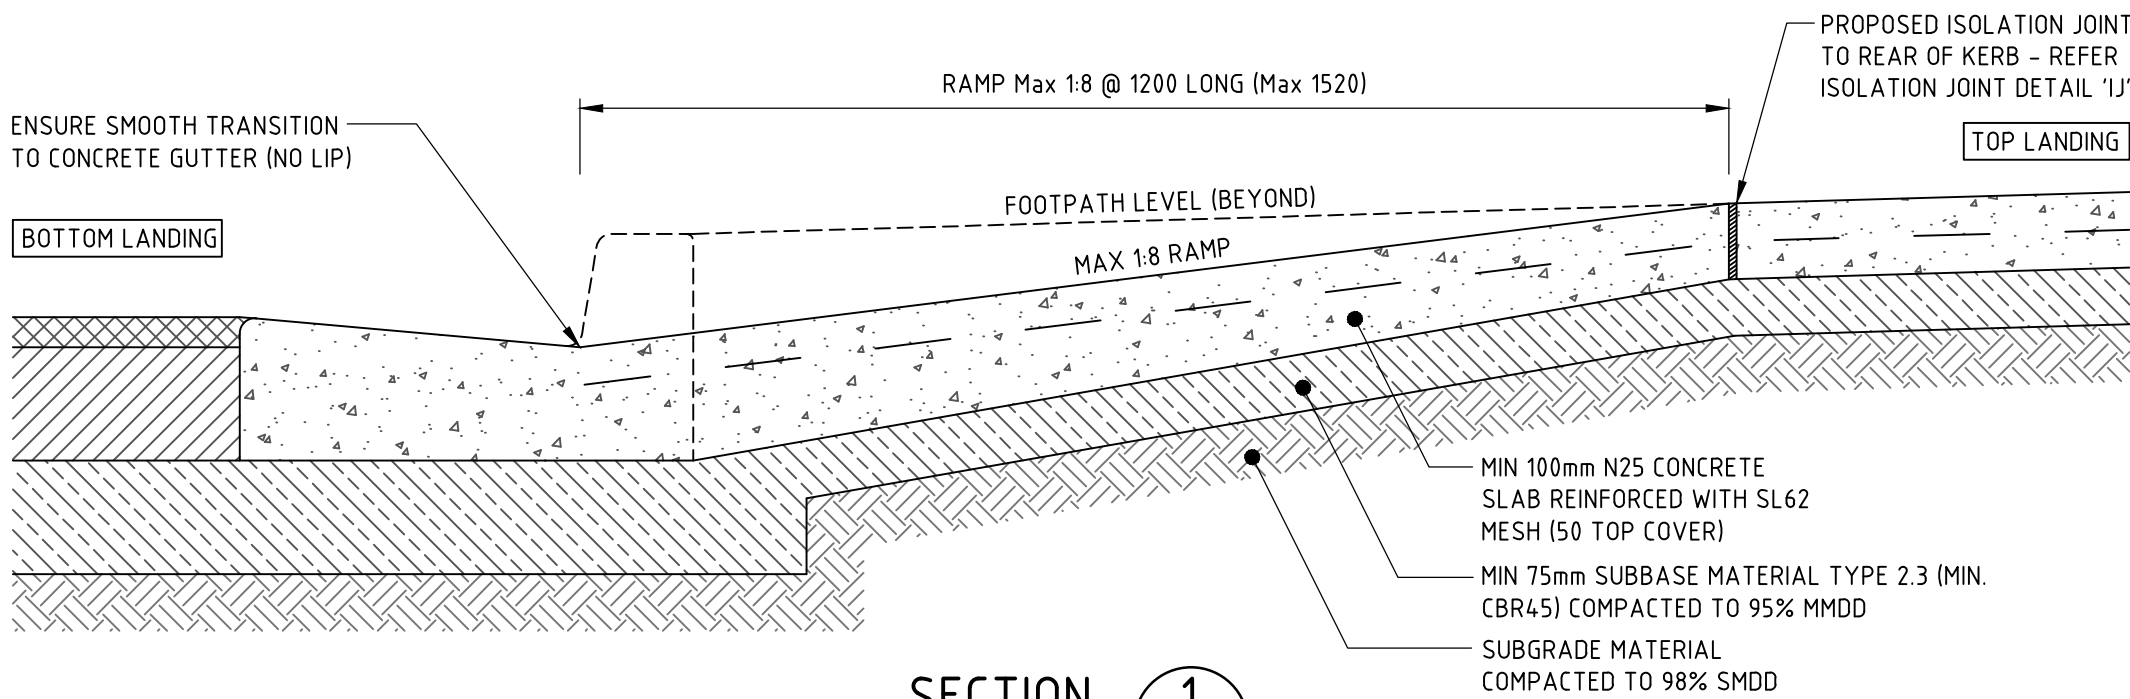

SECTION 1

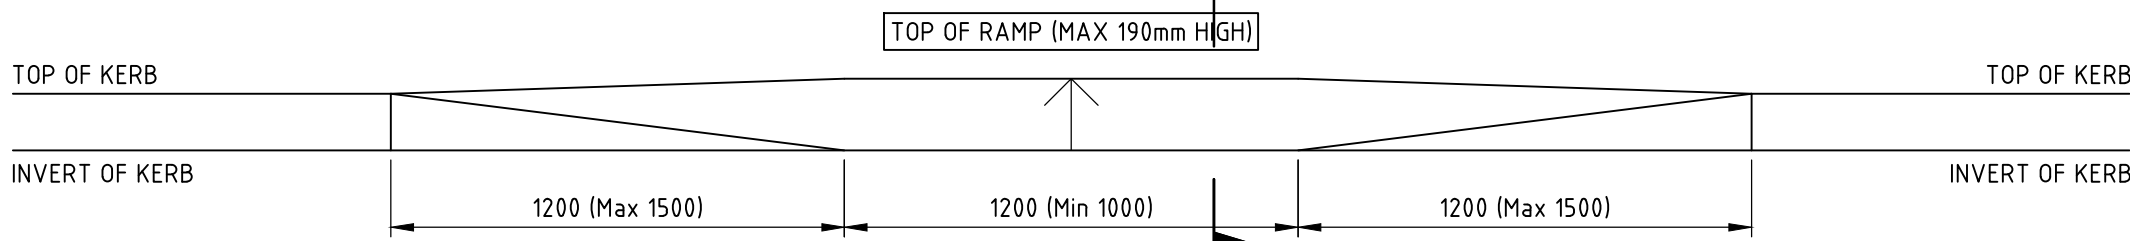


ELEVATION

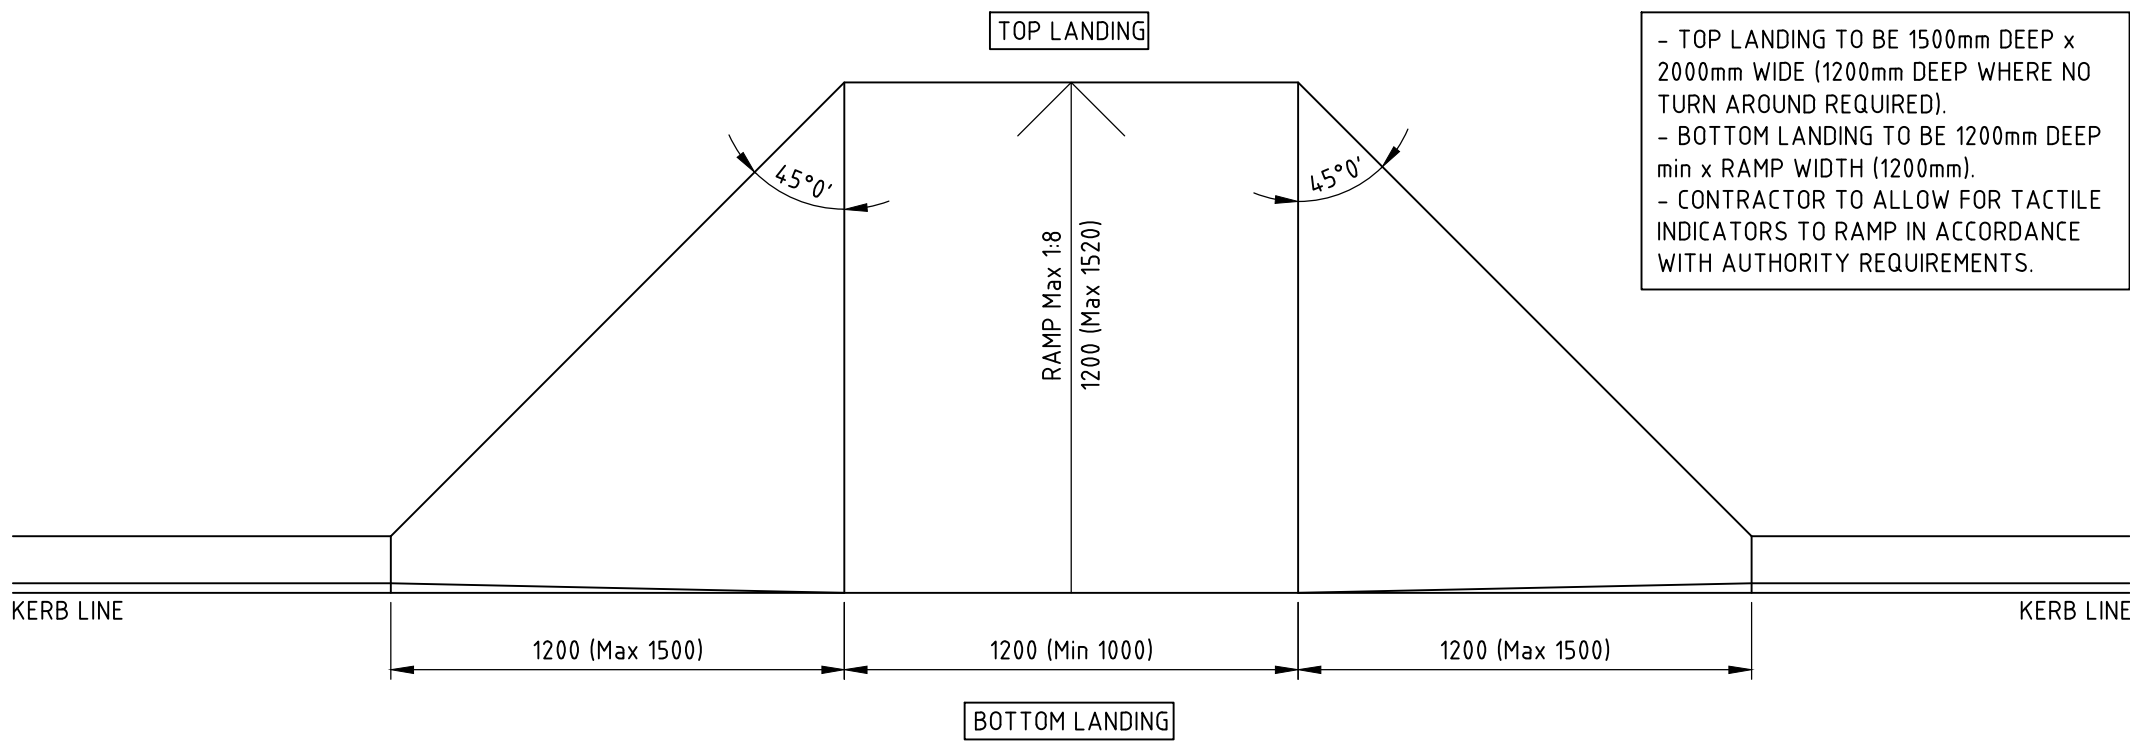


**PLAN
KERB RAMP 'KR'**

'KR' DENOTES 1.2m WIDE KERB RAMP AT PEDESTRIAN CROSSING AND SIGNALS
'KR1' DENOTES 2.0m WIDE KERB RAMP AT PEDESTRIAN CROSSING AND SIGNALS
'KR2' DENOTES 3.2m WIDE KERB RAMP AT PEDESTRIAN CROSSING AND SIGNALS

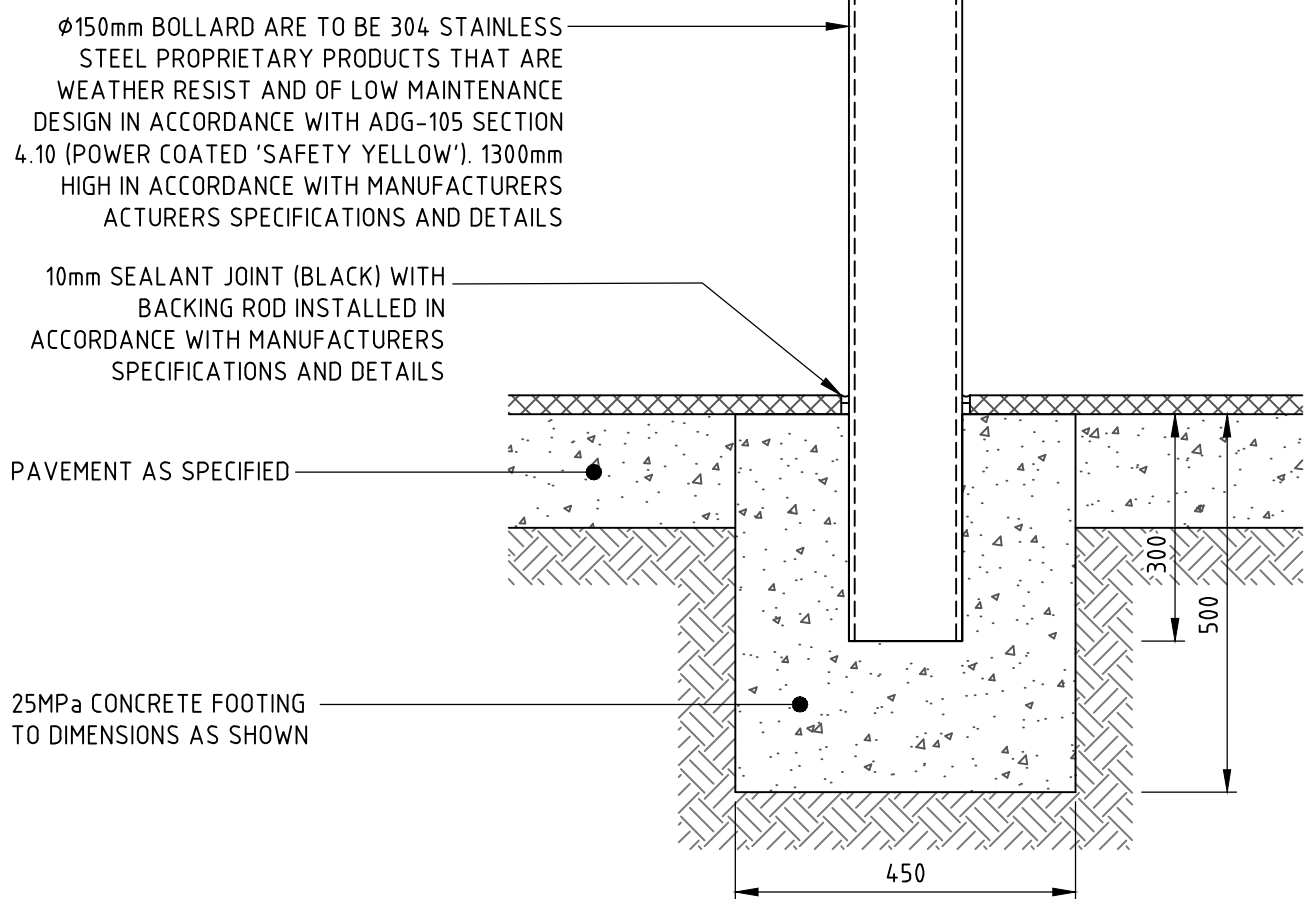

BOLLARD 'B'
PROVIDE 600mm CLEARANCE TO FACE OF KERB / TRAVEL LANE

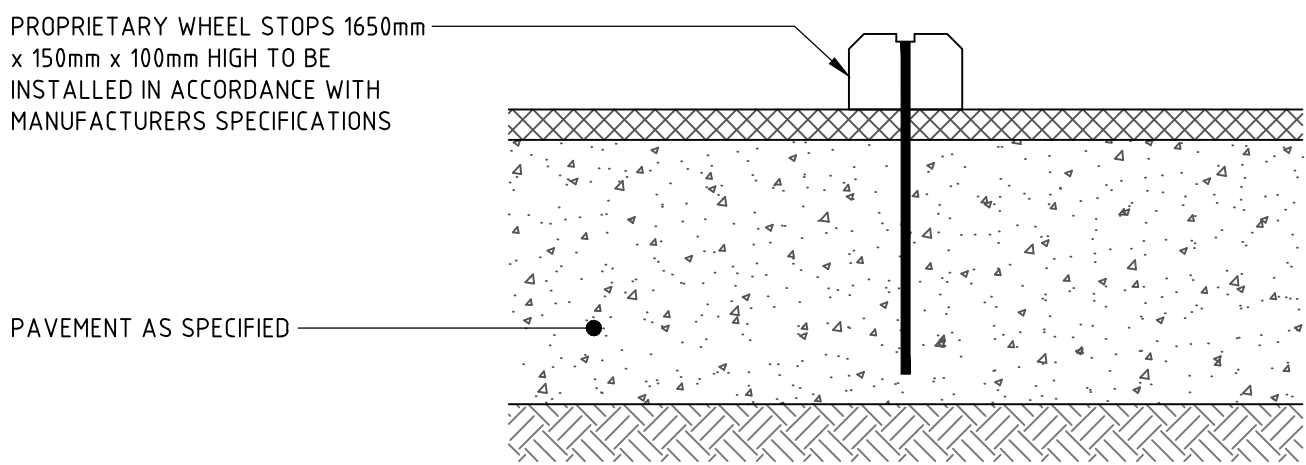

WHEEL STOP 'WS'
WHEEL STOPS TO BE INSTALLED IN ACCORDANCE WITH AUSTRALIAN STANDARDS AS2890.1

NOT FOR CONSTRUCTION